**АГЕНТСТВО ПО МЕЛИОРАЦИИ И ИРРИГАЦИИ**
**ПРИ ПРАВИТЕЛЬСТВЕ РЕСПУБЛИКИ ТАДЖИКИСТАН**

**ГУП "ПРОЕКТНЫЙ ИНСТИТУТ**
**"ТАДЖИКГИПРОВОДХОЗ"**

# РАБОЧИЙ ПРОЕКТ

## "Баркарорсозии пойгоххои обкашии Лохур-0,Лохур-1,Лохур-2 ва Лохур-3 дар нохияи Рудаки"

**АЛЬБОМ-1**

## Аванкамера насосной станции Лохур-0.
## Гидротехническое решения.

**ДУШАНБЕ-2026**

**АГЕНТСТВО ПО МЕЛИОРАЦИИ И ИРРИГАЦИИ**
**ПРИ ПРАВИТЕЛЬСТВЕ РЕСПУБЛИКИ ТАДЖИКИСТАН**

**ГУП "ПРОЕКТНЫЙ ИНСТИТУТ**
**"ТАДЖИКГИПРОВОДХОЗ"**

# РАБОЧИЙ ПРОЕКТ

## "Баркарорсозии пойгоххои обкашии Лохур-0,Лохур-1,Лохур-2 ва Лохур-3 дар нохияи Рудаки"

**АЛЬБОМ-1**

## Аванкамера насосной станции Лохур-0.
## Гидротехническое решения.

ГЛ. ИНЖЕНЕР ИНСТИТУТА: ХАЙБАРОВ С.

ГЛ. ИНЖЕНЕР ПРОЕКТА: ШОМИЛИ У.

**ДУШАНБЕ-2026**

Таб. 1

| Ведомость основных комплектов рабочих чертежей | | |
|---|---|---|
| **Обозначение** | **Наименование** | **Примечание** |
| 1 | 2 | 3 |
| .ПЗ | Пояснительная записка | Книга-1 |
| ТГИ | Инженерно-топогеодезический изысканий | Книга-2 |
| ИГИ | Инженерно-геологический и гидрогеологичекий изысканий | Книга-3 |
| ТХ | **Насосной станции Лохур-0.** Технологическая часть | Альбом-1 |
| ГР | **Насосной станции Лохур-0.** Гидротехническое решение | Альбом-2 |
| АС | **Насосной станции Лохур-0. Архитектурно-строительная часть** | Альбом-3 |
| АС | **Насосной станции Лохур-0. Дежурное помещение Архитектурно-строительная часть** | Альбом-4 |
| АС | **Насосной станции Лохур-0. Уборная на 1-го очко Архитектурно-строительная часть** | Альбом-5 |
| ЭО | Электротехническая часть | Альбом-6 |
| СМ | Сметная документация | Книга-4 |

Таб.3

| Ведомость ссылочных и прилагаемых документов | | |
|---|---|---|
| Обозначение | Наименование | Примечание |
| | **Ссылочные документы** | |
| ГОСТ 10704-91 | Трубы металлические | |
| ГОСТ 9466-75 | Электроды для дуговой сварки сталей и наплавки | |
| | классификация и общие технические условия | |
| ГОСТ 19903-74 | Лист стальная | |
| 30ч906бр | Задвижки с электроприводом | |
| ГОСТ 8509-93 | Уголки стальные горячекатаные равнопрочные | |
| | **Прилагаемые документы** | |
| ТХ.СО-1 | Спецификация основного оборудования насосной станции | 2-листов |

Таб. 2

| Ведомость рабочих чертежей основного комплекта **ТХ** | | |
|---|---|---|
| **Лист** | **Наименование** | **Примечание** |
| 1 | 2 | 3 |
| 1 | Общие данные | |
| 2 | План площадка насосной станции М1:500. Экспликация и ведомость объёмов работ. | |
| 3 | Разрез в осях 1 -2. М1:100. Ведомость объёмов демонтажных работ. | |
| 4 | Сороудерживающая решетка. Спецификация. | |
| 5 | Ограждение ОГ-1. Спецификация. | |
| 6 | Поперечный профиль на сбросно канал Lобщ.=103,0пм. Ведомость объемов строительно монтажных работ | |

Настоящий проект выполнен в соответствии с дествующими нормами и правилами, в том числе по взрыво - пожарной безопасности.

Гл. инженер проекта Шомили У.

Согласовано

Взамен инв.

Подпись и дата

Инв. подл


| Изм. | Кол.уч. | Лист | № док. | Подп. | Дата | "Баркарорсозии пойгоххои обкашии Лохур-0,Лохур-1,Лохур-2 ва Лохур-3 дар нохияи Рудаки" | | |
|---|---|---|---|---|---|---|---|---|
| Разработ. | | Фрайдунпоев О. | | | | Аванкамера насосной станции Лохур-0. Гидротехническое решения. | Стадия | Лист | Листов |
| ГИП | | Шомили У. | | | | | РП | 1 | 5 |
| Нач. отдел | | Шомили У. | | | | Общие данные. | ГУП "Проектный Институт "Точикгипроводхоз" Душанбе - 2026 | | |
| Норм. контр. | | Хайбаров С. | | | | | | | |

S

N

## Экспликация


| № п/п | Наименование | Ед. измер. | Кол-во | Примечание |
|---|---|---|---|---|
| 1 | Всасывающий трубопровод Ø=1200мм, (4-нитки) | пм | 52,0 | Существующий сохраняется |
| 2 | **Служебная площадка раз:1,0х5,0м** | шт | 4,0 | Существующий подлежит восстановление |
| 3 | **Аванкамера раз: 7,0х58,0м** | шт | 1,0 | Существующий подлежит восстановление |
| 4 | Сбросной затвор ГС2,0х2,5м | шт | 2,0 | Существующий подлежит восстановление |
| 5 | **Подающая канал к аванкамера раз: Вср=2,50м** | пм | 129,0 | Существующий подлежит восстановление |

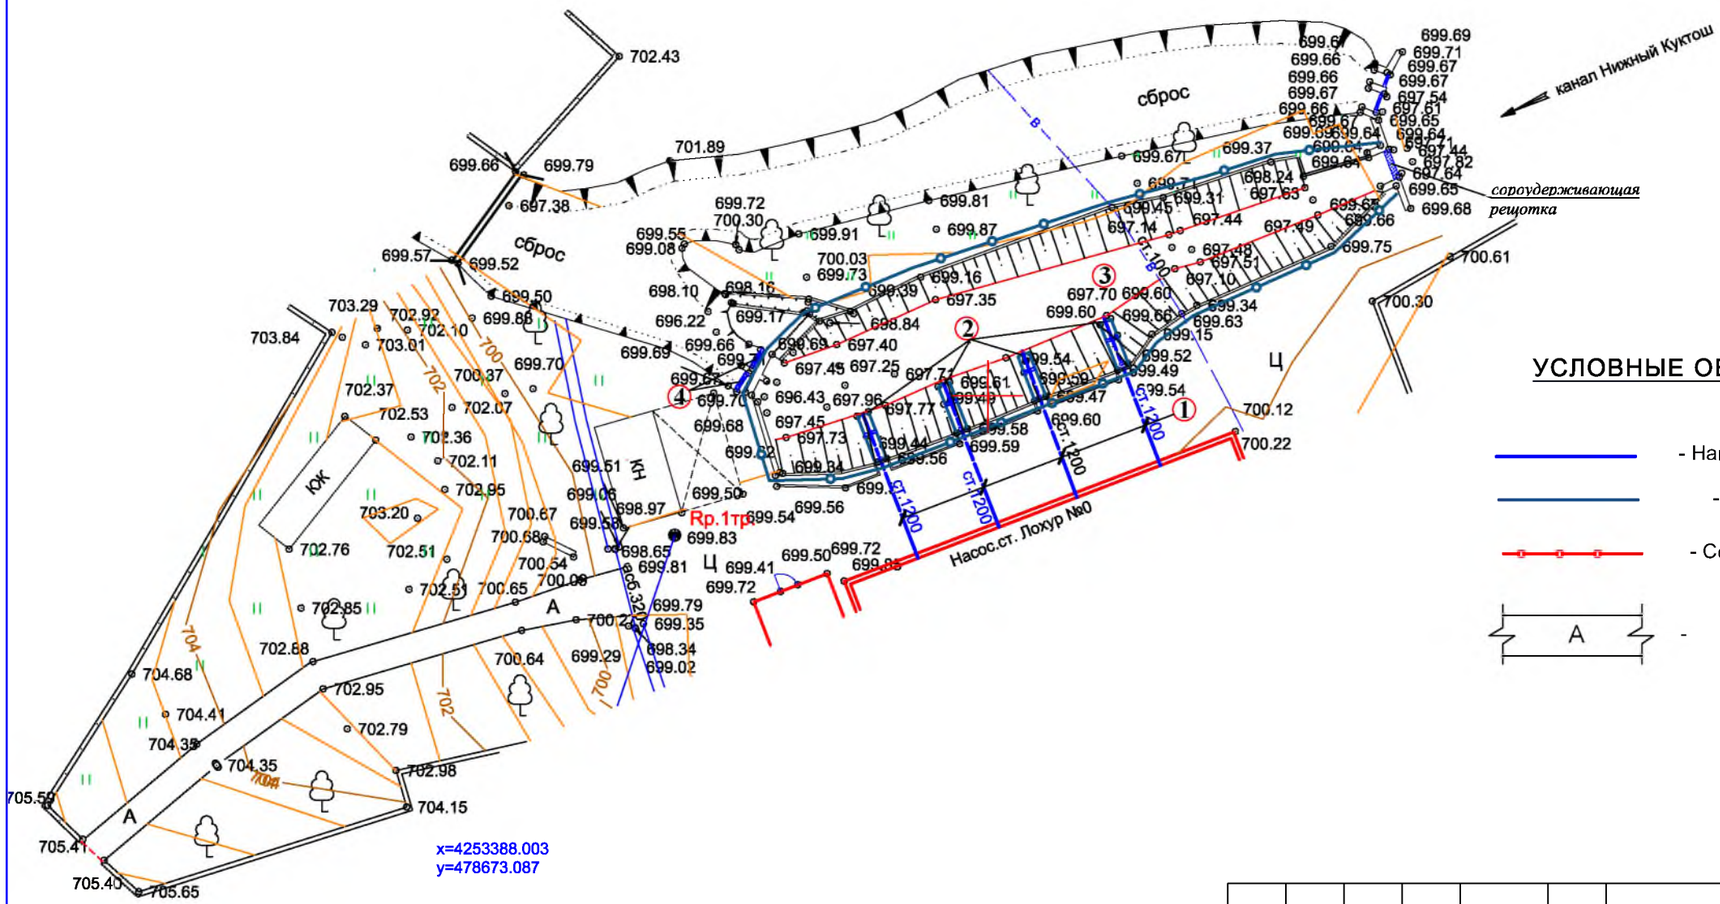


## УСЛОВНЫЕ ОБОЗНАЧЕНИЯ

- Напорный и всасывающий трубопровод
- Сбросной труба
- Сетчатое ограждение
- А - Внутри площадочная подъездная асфальтная дорога

| Изм. | Кол.уч. | Лист | № док. | Поди. | Дата | "Баркарорсозии пойгоххои обкашии Лохур-0,Лохур-1,Лохур-2 ва Лохур-3 дар нохияи Рудаки" | | | |
|---|---|---|---|---|---|---|---|---|---|
| Разработ. | | Фрайдунпоев О. | | | | Аванкамера насосной станции Лохур-0. Гидротехническое решения. | Стадия | Лист | Листов |
| ГИП | | Шомили У. | | | | | РП | 2 | 5 |
| Нач. отдел | | Шомили У. | | | | План площадка насосной станции М1:500. Экспликация и ведомость объёмов работ. | ГУП "Проектный Институт "Точикгипроводхоз" Душанбе - 2026 | | |
| Норм. контр. | | Хайбаров С. | | | | | | | |

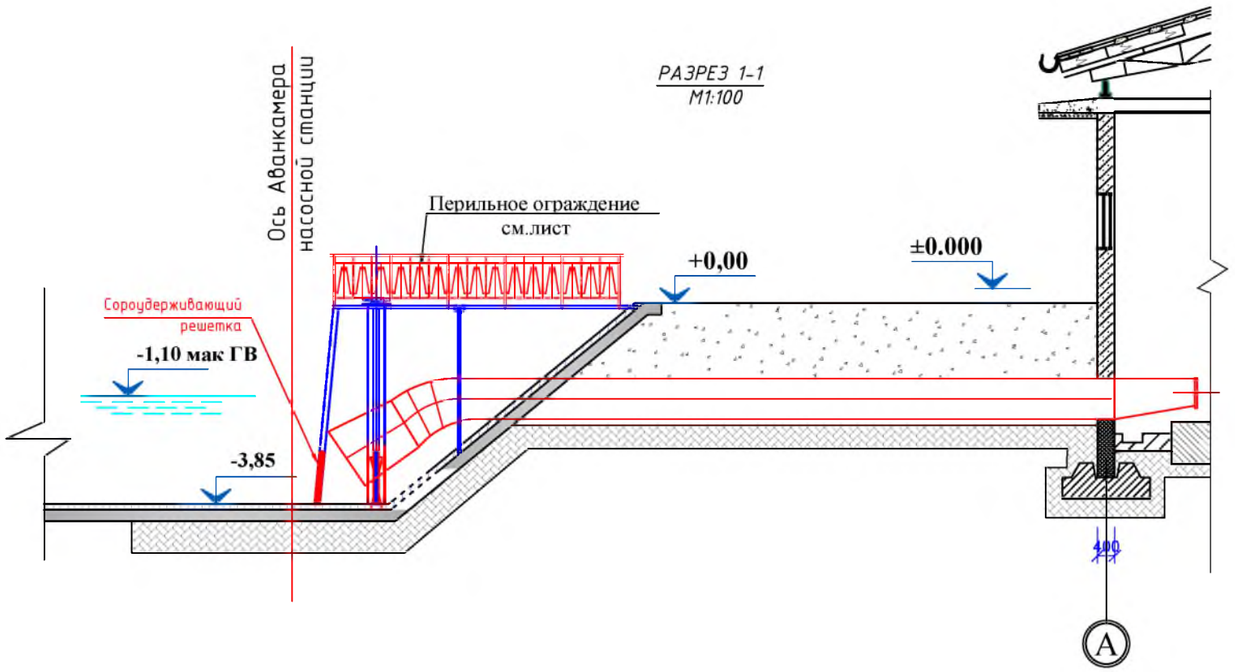


## Ведомость объёмов

| № п /п | Наименование | Ед. изм | Масса оборудования, кг | Примечание |
|---|---|---|---|---|
| 1 | Демонтаж существующие ограждение | пм | 64,0 | |
| 2 | Установка перильное ограждение | пм | 131, | |
| 3 | Установка новый шит затвора ГС 100х100см | шт | 4,0 | |
| 4 | Изготовление и установка сороудерживающие рещетки раз :1,25х1,5м | шт | 4,0 | |
| 5 | Очистка от заиление дно аванкамера насосной стации в ручную t=20см | м³ | 80,0 | |
| 6 | Устройство бетонная облицовка дно по всей площади аванкамера t=10см из бетона В20 | м³ | 16,0 | |
| 7 | Устройство сетки 5Вр-1 шаг150мм | м² | 156,0 | |
| 8 | Анкер из арматуры AIII Ø10мм, шаг 800мм,L=200мм -244шт | кг | 30,2 | |

## Примечание


1. Данный лист рассматривать совместно с листом- 2,3,6 и ТХ.СО
2. Нумерация позиции см.ТХ.СО.

| Изм. | Кол.уч. | Лист | № док. | Подп. | Дата | "Баркарорсозии пойгоххои обкашии Лохур-0,Лохур-1,Лохур-2 ва Лохур-3 дар нохияи Рудаки" | | |
|---|---|---|---|---|---|---|---|---|
| Разработ. | | Фрайдунпосв О. | | | | Аванкамера насосной станции Лохур-0. Гидротехническое решения. | Стадия | Лист | Листов |
| | | | | | | | РП | 3 | 5 |
| ГИП | | Шомили У. | | | | | | | |
| Нач. отдел | | Шомили У. | | | | Разрез в осях 1 -2. М1:100. Ведомость объёмов демонтажных работ. | ГУП "Проектный Институт "Точикгипроводхоз" Душанбе - 2026 | | |
| Норм. контр. | | Хайбаров С. | | | | | | | |

Согласовано

Инв. подл | Подпись и дата | Взамен инв.


Сороудерживающая решетка

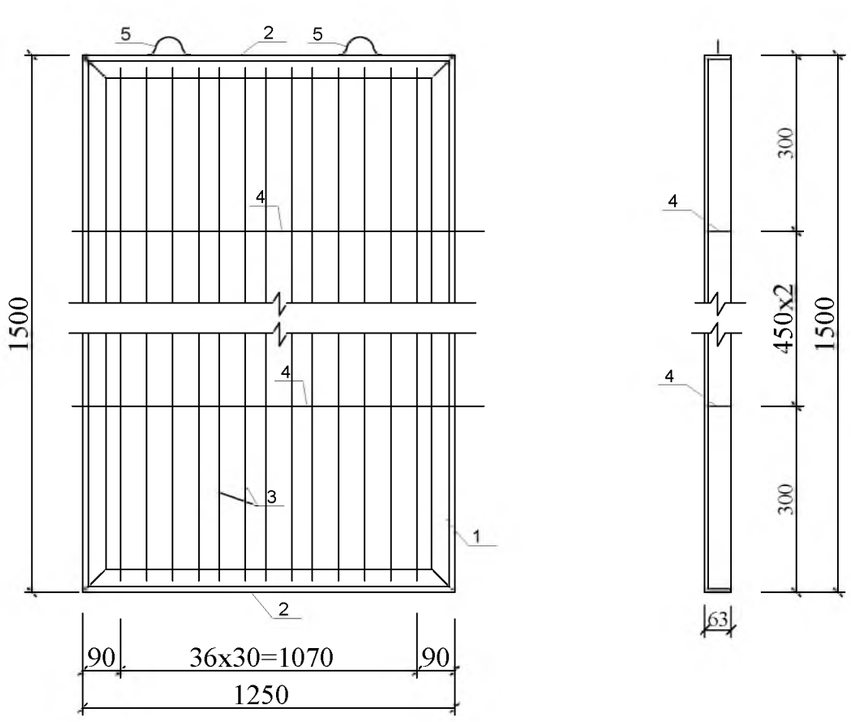







Деталь 3

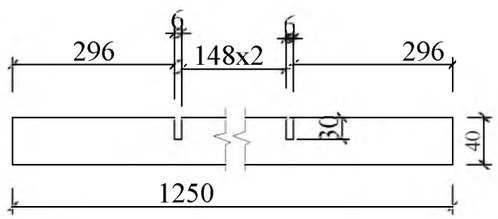


Деталь 5

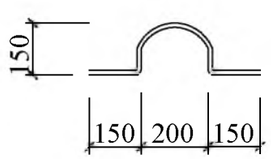


Деталь 4

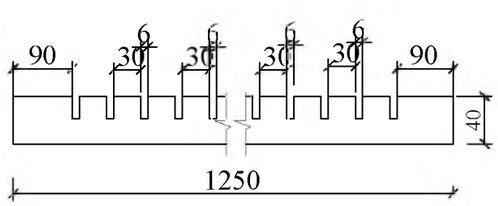


## Спецификация на одну сороудерживающую решетку

| Марка. поз. | Обозначение | Наименование | Кол. | Масса ед. кг. | Приме-чание |
|---|---|---|---|---|---|
| 1 | ГОСТ 8509-72 | Уголок 63х5 L=3,0м | 2 | 14,43 | 28,86кг |
| 2 | ГОСТ 8509-72 | Уголок 63х5 L=2,5м | 2 | 12,02 | 24,04кг |
| 3 | ГОСТ 103-76 | Полоса 5х40 L=1,50м | 36 | 2,35 | 84,78кг |
| 4 | ГОСТ 103-76 | Полоса 5х40 L=1,25м | 2 | 1,96 | 3,93кг |
| 5 | ГОСТ 5781-91 | Арматура Ø AIII 16 L=650мм | 2 | 1,027 | 2,054кг |
| | | Электроды | | | 2,0кг |

**Изготовить сороудерживающие решетки -4шт**

Согласовано

Взам. инв. №

Подпись. и дата


Инв. № подл.

| | | | | | | |
|---|---|---|---|---|---|---|
| | | | | | | "Баркарорсозии пойгоххои обкашии Лохур-0,Лохур-1,Лохур-2 ва Лохур-3 дар нохияи Рудаки" |
| Изм. | Кол.уч. | Лист | № док. | Подп. | Дата | |
| Разработ. | | Фрайдунпосев О. | | | | Аванкамера насосной станции Лохур-0. Гидротехническое решения. |
| ГИП | | Шомили У. | | | | |
| Нач. отдел | | Шомили У. | | | | Сороудерживающая решетка. Спецификация. |
| Норм. контр. | | Хайбаров С. | | | | |


| Стадия | Лист | Листов |
|---|---|---|
| РП | 4 | 5 |

**ГУП "Проектный Институт "Точикгипроводхоз" Душанбе - 2026**


## Секция перильного ограждения

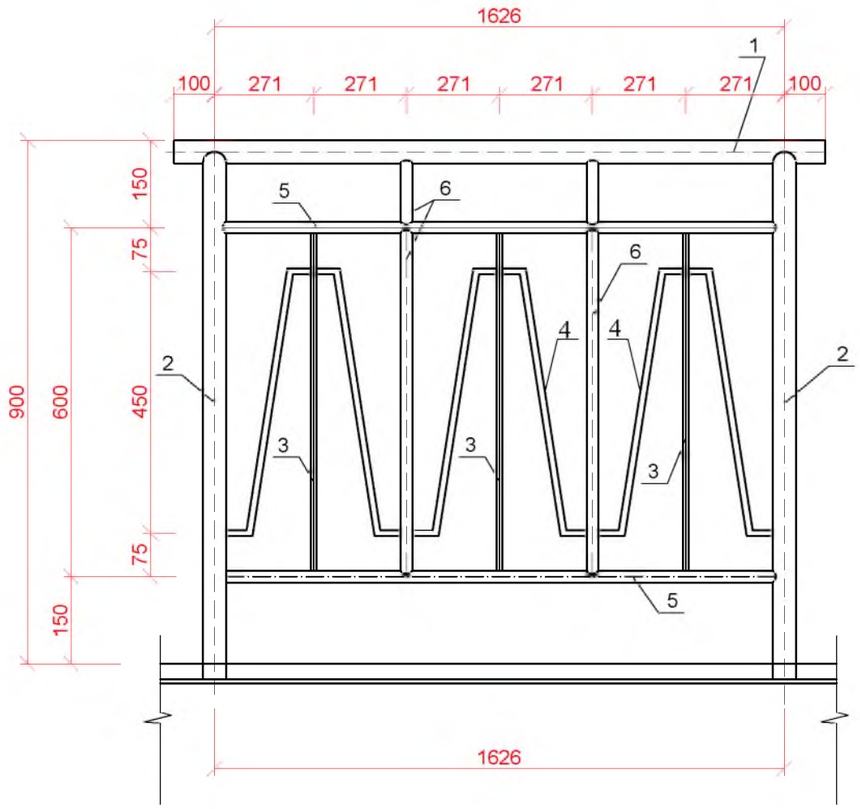


## Деталь, поз. 2

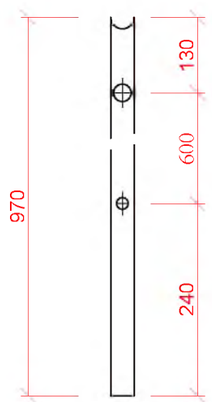


## Деталь, поз. 4

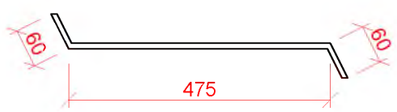


## Спецификация на 1 секцию перильного ограждения

| Марка Поз. | Обозначение | Наименование | ОГ 1 | | Примеч. |
|---|---|---|---|---|---|
| | | | Кол | Масса ед. кг | |
| | | **Детали** | | | |
| 1 | | Труба $\frac{32x2,0\ ГОСТ10704\text{-}91}{Вст3сп\ ГОСТ380\text{-}88}$ l=1826 | 1 | 2,69 | |
| 2 | | Труба $\frac{40x2,5\ ГОСТ10704\text{-}91}{Вст3сп\ ГОСТ380\text{-}88}$ l=970 | 2 | 2,24 | 4,48кг |
| 3 | | Труба $\frac{15x1,4\ ГОСТ10704\text{-}91}{ГОСТ380\text{-}88\ Вст3сп}$ l=600 | 3 | 0,282 | 0,85 кг |
| 4 | | Ø12 AI ГОСТ 5781-82, ℓ=595 | 6 | 0,49 | 3,17кг |
| 5 | | Труба $\frac{25x2,0\ ГОСТ10704\text{-}91}{Вст3сп\ ГОСТ380\text{-}88}$ l=1620 | 2 | 1,83 | 3,67кг |
| 6 | | Труба $\frac{25x2,0\ ГОСТ10704\text{-}91}{Вст3сп\ ГОСТ380\text{-}88}$ l=720 | 2 | 0,81 | 1,63 кг |
| 7 | | Окраска перильного ограждения | 1 | - | 16,49кг |
| 8 | ГОСТ 9467-75 | Электроды Э-42, 2 % | | 0,40 | |
| | | | | | |

**Примечание:**

1. ØГ 1 - ограждение предназначено по контуру сооружение вес - 16,49 кг
2. Сварные швы выполнять ручной дуговой сваркой по ГОСТ 5264-80 по всему контуру соприкасания деталей.
3. Все размеры даны в мм
4. Изготовит **67**шт ограждение ОГ-1

Согласовано


Взам. инв. №

Подпись. и дата

Инв. № подл.

| Изм. | Кол.уч. | Лист | № док. | Подп. | Дата | "Баркарорсозии пойгоххои обкашии Лохур-0,Лохур-1,Лохур-2 ва Лохур-3 дар нохияи Рудаки" | | | |
|---|---|---|---|---|---|---|---|---|---|
| Разработ. | | Фрайдунпосев О. | | | | Аванкамера насосной станции Лохур-0. Гидротехническое решения. | Стадия | Лист | Листов |
| ГИП | | Шомили У. | | | | | РП | 5 | 5 |
| Нач. отдел | | Шомили У. | | | | Ограждение ОГ-1. Спецификация. | ГУП "Проектный Институт "Точикгипроводхоз" Душанбе - 2026 | | |
| Норм. контр. | | Хайбаров С. | | | | | | | |

## Поперечный профиль на сбросно канал Lобщ.=103,0пм

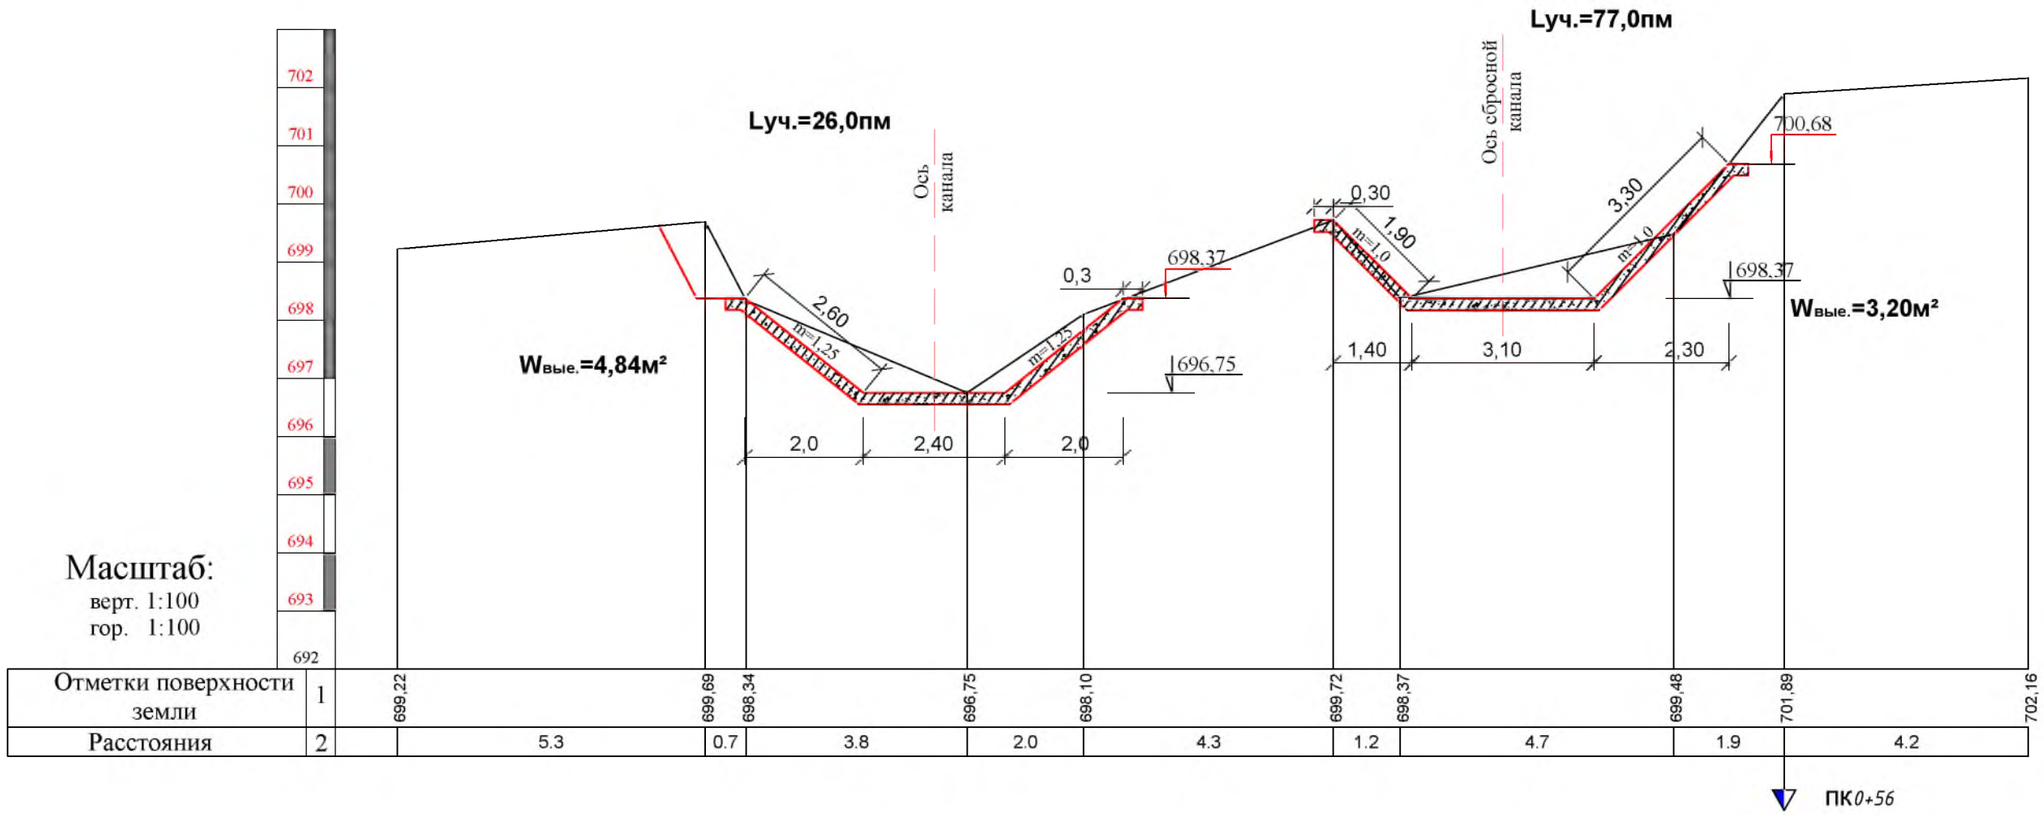


| | | | | | | | | | | | |
|---|---|---|---|---|---|---|---|---|---|---|---|
| Отметки поверхности земли | 1 | 699,22 | 699,69 | 698,34 | 696,75 | 698,10 | 699,72 | 698,37 | 699,48 | 701,89 | 702,16 |
| Расстояния | 2 | | 5.3 | 0.7 | 3.8 | 2.0 | 4.3 | 1.2 | 4.7 | 1.9 | 4.2 |

ПК0+56

Масштаб:
верт. 1:100
гор. 1:100

Согласовано

Взамен инв

Подпись и дата

Инв. подл

### Ведомость объемов строительно монтажных работ

| № п/п | Наименование работ | Ед. изм | Кол- во | Примечание |
|---|---|---|---|---|
| 1 | Разработка грунта II-кат. под сечение канала .L общ.=103,0м на участке гидропоста t=20см | м³ | 372,24 | 10% вручную |
| 2 | Планировка в ручную под сечение (дно и откосы) канала на участке бетонный и каменный крепление L общ.=103,0м | м² | 898,50 | |
| 3 | Гравийно-песчанная подготовка t=10см (дно и откосы) канала на участке бетонный крепление L общ.=103,0м | м³ | 90,0 | |
| 4 | Облицовка сбросного канала из монолитного ж/бетона B20 F150 W6 t=20см<br>- дно<br>- откосы<br>- сетка из арматуры AIII Ø12мм шаг: 20/20см (8,88кг на 1м²) | м³<br>м³<br>кг | 60,22<br>119,50<br>7978,68 | |
| | **2. Прочие работы.** | | | |
| 5 | Устройство деформационного швов на поперечное сечение канала шаг через 6м канала раз: h=200мм, t=40мм, Lуч-1.=8,90м и Lуч.2=8,20м | шт | 17.0 | |
| 6 | Антисептированный брус 40х100мм | м³ | 0,60 | |
| 7 | Битумно-полимерная мастика | м² | 8,564 | |
| 8 | Прокладка из гидроизола ГИ-Г В=0.4м | м² | 59,40 | |
| 9 | Пароизол Ø40мм | пм | 18,70 | |
| 10 | Геомембрана из полиэтилена ПВД (HDPE) толщиной 1,0мм. | м² | 898,50 | |

| Изм. | Кол.уч. | Лист | № док. | Подп. | Дата | ГР |
|---|---|---|---|---|---|---|
| | | | | | | "Баркарорсозии пойгоххои обкашии Лохур-0,Лохур-1,Лохур-2 ва Лохур-3 дар нохияи Рудаки" |
| Разработ. | | Фойдушоев О. | | | | Аванкамера насосной станции Лохур-0. Гидротехническое решения. |
| ГИП | | Шомили У. | | | | |
| Нач. отдел | | Шомили У. | | | | Поперечный профиль на сбросно канал Lобщ.=103,0пм. Ведомость объемов строительно монтажных работ |
| Норм. контр. | | Хайбаров С. | | | | |

| Стадия | Лист | Листов |
|---|---|---|
| РП | 6 | 5 |

**ГУП "Проектный Институт "Точикгипроводхоз" Душанбе - 2026**

Таб. 1

| Ведомость основных комплектов рабочих чертежей | | |
|---|---|---|
| **Обозначение** | **Наименование** | **Примечание** |
| 1 | 2 | 3 |
| .ПЗ | Пояснительная записка | Книга-1 |
| ТГИ | Инженерно-топогеодезический изысканий | Книга-2 |
| ИГИ | Инженерно-геологический и гидрогеологичекий изысканий | Книга-3 |
| ТХ | **Насосной станции Лохур-0.** Технологическая часть | Альбом-1 |
| ГР | **Насосной станции Лохур-0.** Гидротехническое решение | Альбом-2 |
| АС | **Насосной станции Лохур-0. Архитектурно-строительная часть** | Альбом-3 |
| АС | **Насосной станции Лохур-0. Дежурное помещение Архитектурно-строительная часть** | Альбом-4 |
| АС | **Насосной станции Лохур-0. Уборная на 1-го очко Архитектурно-строительная часть** | Альбом-5 |
| ЭО | Электротехническая часть | Альбом-6 |
| СМ | Сметная документация | Книга-4 |

Таб. 2

| Ведомость рабочих чертежей основного комплекта **ТХ** | | |
|---|---|---|
| **Лист** | **Наименование** | **Примечание** |
| 1 | 2 | 3 |
| 1 | Общие данные | |
| 2 | План здание трансформаторное помещение. Ведомость объёмов работ | |
| 3 | Фасад по А-Б и Б-А. | |
| 4 | План кровли.Спецификация | |
| 5 | Схема расположения деревянных элементов кровли.Спецификация | |
| 6 | Разрез 1-1;2-2. Узел "В" Спецификация | |
| 7 | Окна из металло-пластиковых профилей О-1,2,3 и 4. Спецификация. | |
| 8 | Вороты ВМ-1 и ВМ-2. Спецификация. | |

Таб.3

| Ведомость ссылочных и прилагаемых документов | | |
|---|---|---|
| Обозначение | Наименование | Примечание |
| | **Ссылочные документы** | |
| ГОСТ 10704-91 | Трубы металлические | |
| ГОСТ 9466-75 | Электроды для дуговой сварки сталей и наплавки | |
| | классификация и общие технические условия | |
| ГОСТ 19903-74 | Лист стальная | |
| 30ч906бр | Задвижки с электроприводом | |
| ГОСТ 8509-93 | Уголки стальные горячекатаные равнопрочные | |
| | **Прилагаемые документы** | |
| ТХ.СО-1 | Спецификация основного оборудования насосной станции | 2-листов |

Настоящий проект выполнен в соответствии с дествующими нормами и правилами, в том числе по взрыво - пожарной безопасности.

Гл. инженер проекта Шомили У.

Согласовано

Взамен инв.

Подпись и дата

Инв. подл


| | | | | | | |
|---|---|---|---|---|---|---|
| | | | | | | **АС** |
| | | | | | | **"Баркарорсозии пойгоххои обкашии Лохур-0,Лохур-1,Лохур-2 ва Лохур-3 дар нохияи Рудаки"** |
| Изм. | Кол.уч. | Лист | № док. | Подп. | Дата | |
| Разработ. | | Фрайдунпоев О. | | | | Насосной станции Лохур-0. Архитектурно-строительная часть. |
| ГИП | | Шомили У. | | | | |
| Нач. отдел | | Шомили У. | | | | |
| Норм. контр. | | Хайбаров С. | | | | Общие данные. |

| Стадия | Лист | Листов |
|---|---|---|
| РП | 1 | 8 |

**ГУП "Проектный Институт "Точикгипроводхоз" Душанбе - 2026**

**План здание трансформаторное помещение**

М1:100

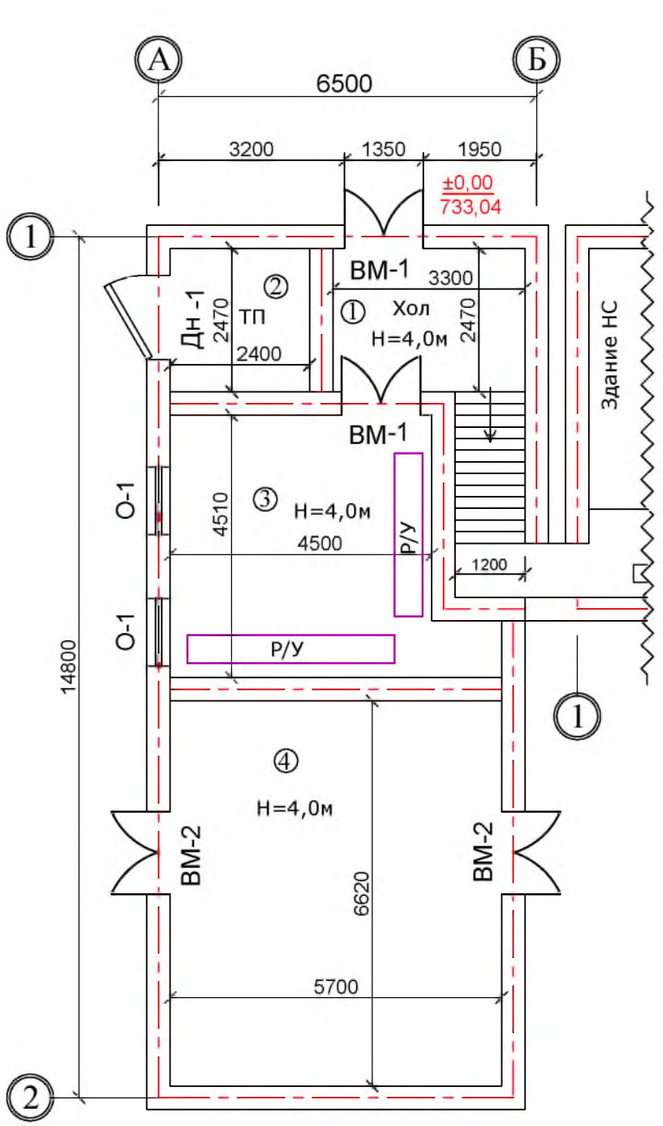


## Ведомость объёмов работ

| № п /п | Наименование | Ед. изм | Кол-во | Примечание |
|---|---|---|---|---|
| 1 | Демонтаж существующие деревянные оконные блоки раз:1200х1900мм (n=2,0шт) | м² | 4,56 | |
| 2 | Демонтаж существующие деревянные дверные блоки раз:1350х2350мм (n=2,0шт) | м² | 6,345 | |
| 3 | Демонтаж существующие деревянные дверные блоки раз:1420х2350мм (n=2,0шт) | м² | 6,674 | |
| 4 | Демонтаж существующие деревянные дверные блоки раз:1450х2100мм (n=1,0шт) | м² | 3,045 | |
| 5 | Очистка внутренных стены | м² | 235,14 | |
| 6 | Шпатлёвка, грунтовка и водоэмульционая краска внутренних стены и балки | м² | 235,14 | |
| 7 | Очистка потолка в ручную | м² | 72,11 | |
| 8 | Шпатлёвка, грунтовка и водоэмульционая окраска потолка за два раза | м² | 72,11 | |
| 9 | Очистка старый существующий штукатурка наружных стены | м² | 238,16 | |
| 10 | Устройства декоративной фасадной штукатурки наружных стены (дождик) - AMY TERAZIT Код: 223и 230 | м² | 238,16 | |
| 11 | Устройство отмостка вокруг здания раз:100см t=10см из бетона В12,5 | м³ | 4.50 | |
| 12 | Окраска существующая лестница за два раза | м² | 5,0 | |
| 13 | Установка серанит на цокольный част наружных стен высотой h=60см | м² | 30,0 | |
| | **Устройство пола** | | | |
| 14 | Устройство пола из бетона В15 t=10см | м³ | 7,21 | |

## Экспликация здании и сооружении

| № п/п | Наименование | Ед. измер. | Кол-во | Примечание |
|---|---|---|---|---|
| 1 | **Хол** раз:2,47х3,3х4,0м | шт | 1,0 | Существующий подлежит восстановление |
| 2 | **Помещение ТП** раз:2,4х2,47х4,0м | пм | 1,0 | Существующий подлежит восстановление |
| 3 | **Помещение Р/У** раз:4,5х4,51х4,0м | шт | 1,0 | Существующий подлежит восстановление |
| 4 | **Помещение складное** раз:5,7х6,62х4,0м | шт | 1,0 | Существующий подлежит восстановление |

## Примечание

1. Данный лист рассматривать совместно с листом- 3,4,5 и ТХ.СО

Согласовано

Взамен инв.

Подпись и дата


Инв. подл

| | | | | | | |
|---|---|---|---|---|---|---|
| | | | | | | **АС** |
| | | | | | | **"Баркарорсозии пойгоххои обкашии Лохур-0,Лохур-1,Лохур-2 ва Лохур-3 дар нохияи Рудаки"** |
| Изм. | Кол.уч. | Лист | № док. | Подп. | Дата | |
| Разработ. | | Фрайдунпосев О. | | | | Насосной станции Лохур-0. Архитектурно-строительная часть. |
| ГИП | | Шомили У. | | | | |
| Нач. отдел | | Шомили У. | | | | План здание трансформаторное помещение. Ведомость объёмов работ |
| Норм. контр. | | Хайбаров С. | | | | |


| Стадия | Лист | Листов |
|---|---|---|
| РП | 2 | 8 |

**ГУП "Проектный Институт "Точикгипроводхоз" Душанбе - 2026**


## ФАСАД 1-3

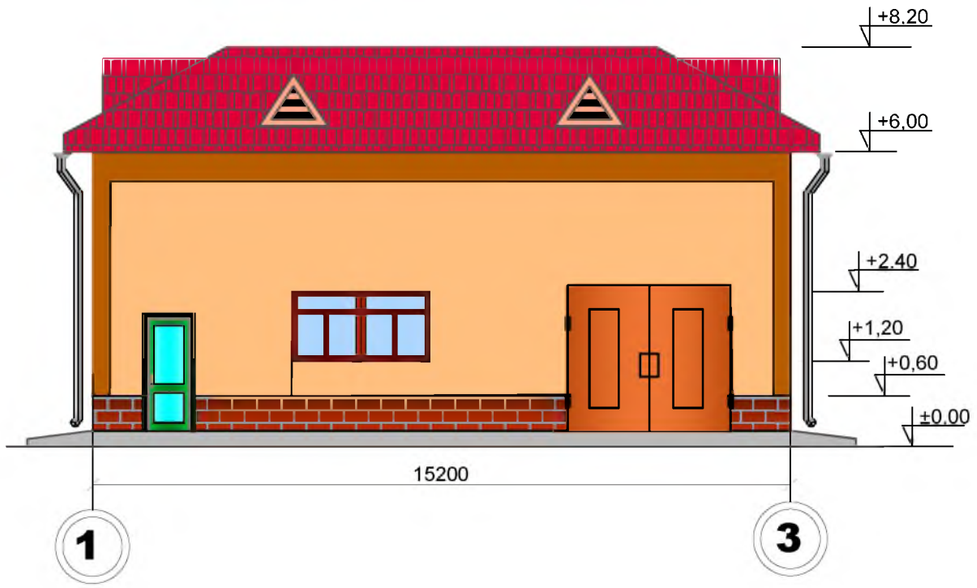


## ФАСАД А-Б

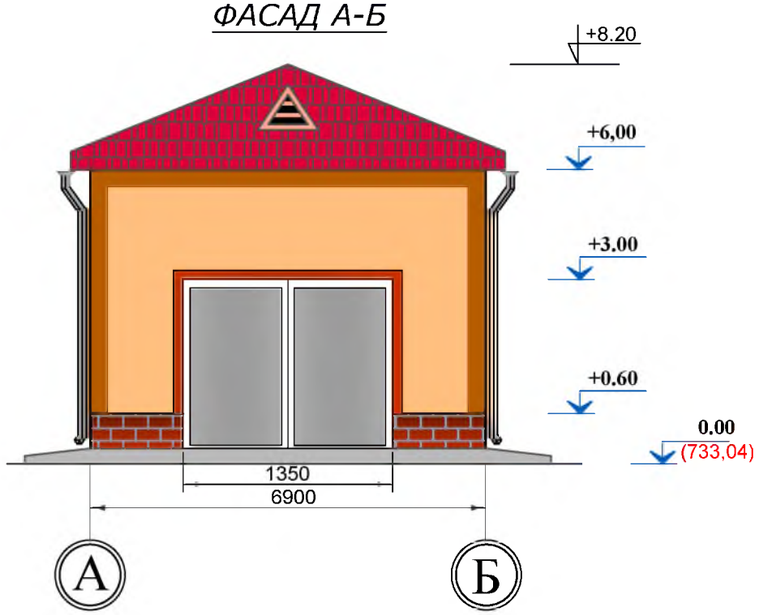


## ФАСАД Б-А

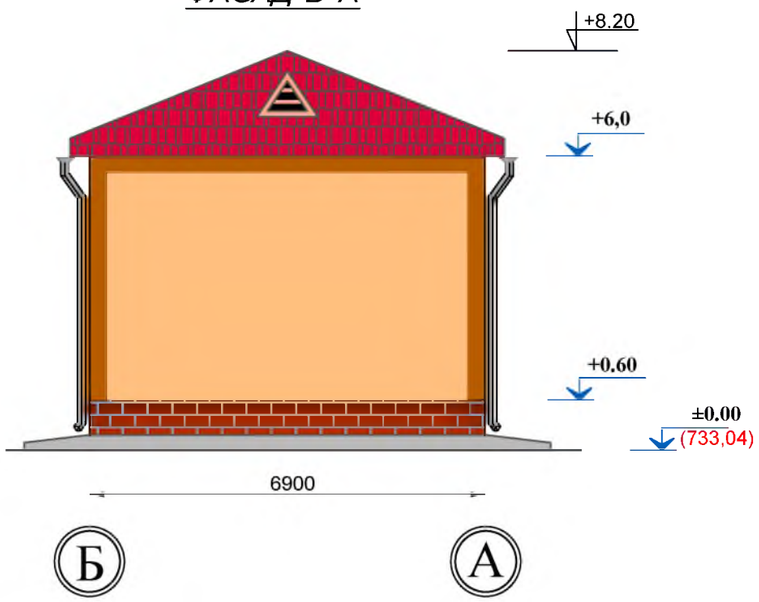


Согласовано


Взамен инв.

Подпись и дата

Инв. подл

| | | | | | | | |
|---|---|---|---|---|---|---|---|
| | | | | | | АС | |
| | | | | | | "Баркарорсозии пойгоххои обкашии Лохур-0,Лохур-1,Лохур-2 ва Лохур-3 дар нохияи Рудаки" | |
| Изм. | Кол.уч. | Лист | № док. | Подп. | Дата | | |
| | | | | | | Насосной станции Лохур-0. Архитектурно-строительная часть. | Стадия: РП; Лист: 3; Листов: 8 |
| Разработ. | | Фрайдуншоев О. | | | | | |
| ГИП | | Шомили У. | | | | | |
| Нач. отдел | | Шомили У. | | | | Фасад по А-Б и Б-А. | ГУП "Проектный Институт "Точикгипроводхоз" Душанбе - 2026 |
| Норм. контр. | | Хайбаров С. | | | | | |


# План кровли
## (на отметке +6,00)

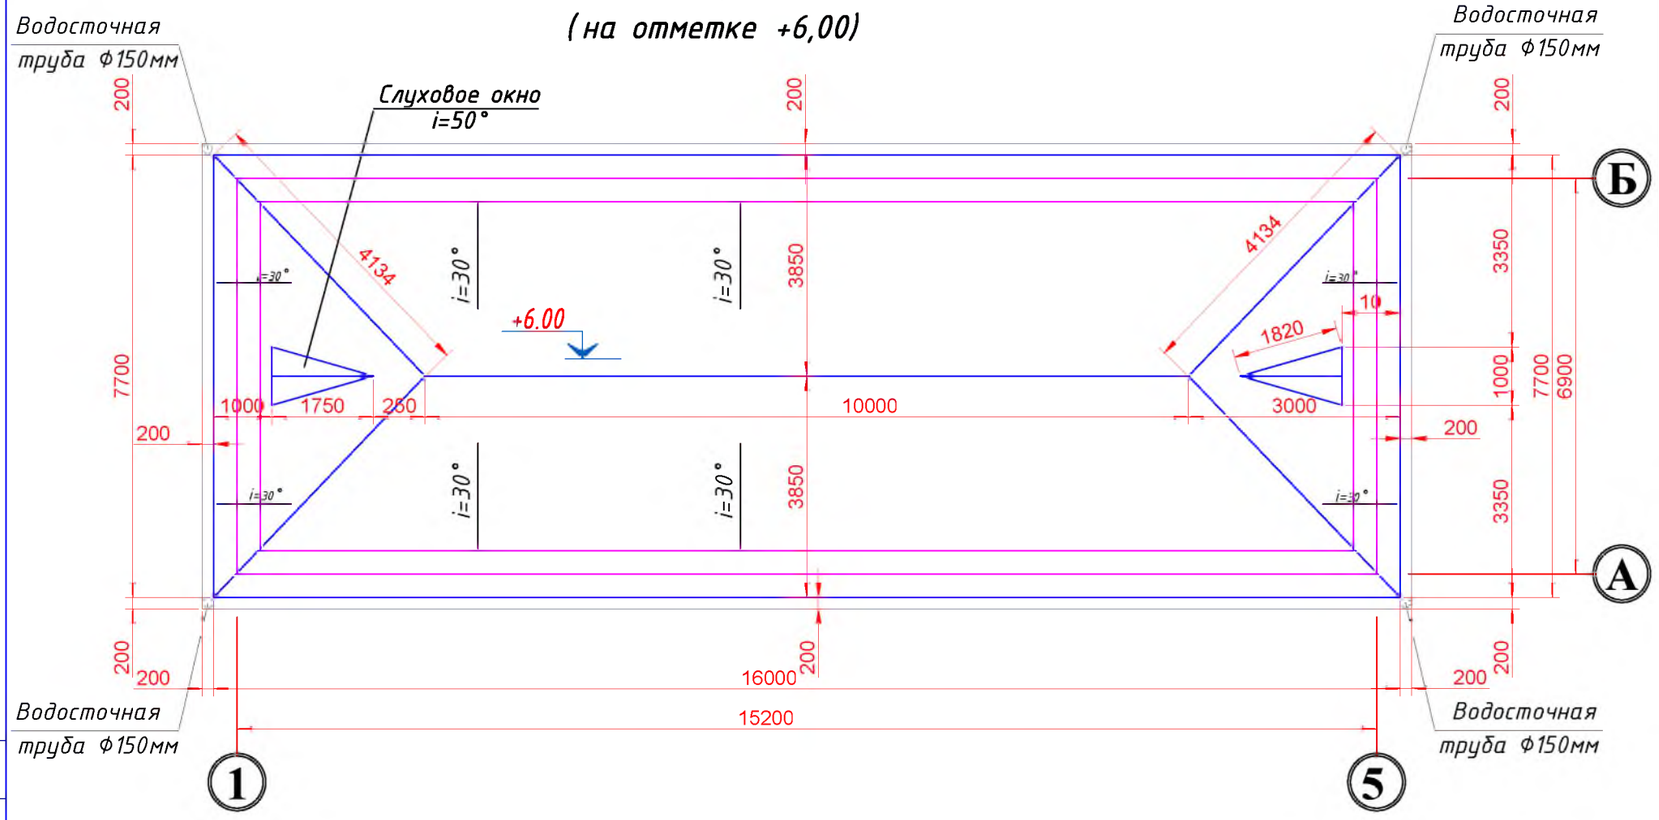



## Спецификация водосточная элементов

| | Наименование | Ед изм | Кол-во | Примечание |
|---|---|---|---|---|
| 1 | Желоб | пм | 40,0 | |
| 2 | **Водосточный труба Ø150** L=4800мм | шт | 4,0 | |
| 3 | Отвод 45° Ø150 | шт | 12,0 | |
| 4 | Воронка Ø180-150 | шт | 4,0 | |
| 5 | Коньковая деталь (фартук) | пм | 23,0 | |


## Узлы водосточных труб

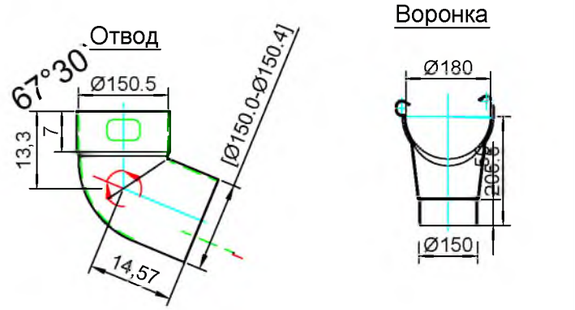



Верхнее колено 45°

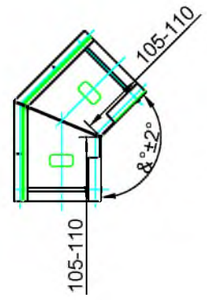


Труба

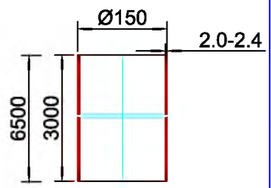

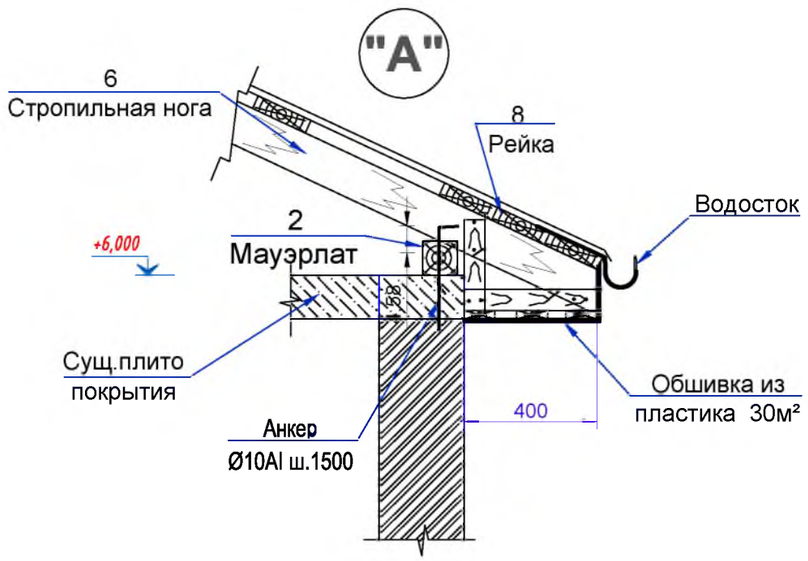
*Примечание:*

1. *Мауэрлат укладывается на слой толя и заанкеруются в перекрытию.*
2. *Кровля выполняется из металлочерепицы .*
3. *Все деревянные элементы антисептируется и покрываются специальном составом для повышения огнестойкости.*
4. *Спецификация элементов смотри на листе АС- 4; АС- 5;*
5. *Разрез 1-1, 2-2, 3-3, 4-4 смотри на листе АС-4; АС- 5; АС- 6;*
6. *Все узлы кровли выполнять по серии 2.160-6с в.1.*
7. *Все деревянные элементы антисептируются и покрываются специальным составом для повышения огнестойкости .*
8. *Деревянные элементы, соприкасающиеся с кирпичной кладкой обернуть толем .*
9. *Узлы кровли выполнены согласно по серии 2.160-6с "Узлы и детали кровля".*
10. *Кровля выполняется из металлочерепицы толщ. 0.05 мм.*
11. *Данный лист см. совместно с листом -2,3,5 И 6АС .*

Согласовано

Взамен инв.


Подпись и дата

Инв. подл


| Изм. | Кол.уч. | Лист | № док. | Подп. | Дата | АС | | |
|---|---|---|---|---|---|---|---|---|
| | | | | | | "Баркарорсозии пойгоххои обкашии Лохур-0,Лохур-1,Лохур-2 ва Лохур-3 дар нохияи Рудаки" | | |
| Разработ. | | Фрайдунпсев О. | | | | Насосной станции Лохур-0. Архитектурно-строительная часть. | Стадия | Лист | Листов |
| ГИП | | Шомили У. | | | | | РП | 4 | 8 |
| Нач. отдел | | Шомили У. | | | | План кровли.Спецификация | ГУП "Проектный Институт "Точикгипроводхоз" Душанбе - 2026 | | |
| Норм. контр. | | Хайбаров С. | | | | | | | |


## Схема расположения деревянных элементов кровли

(на отметке +8,200)

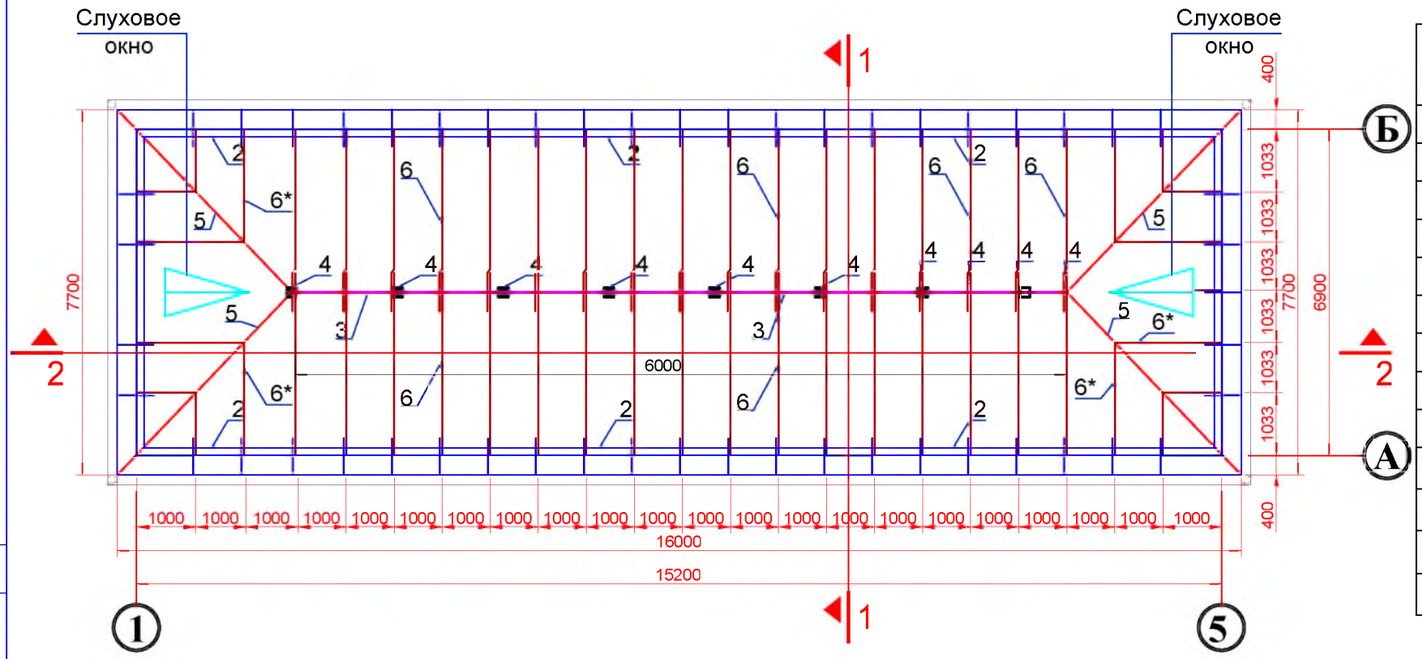


## Разрез 1-1

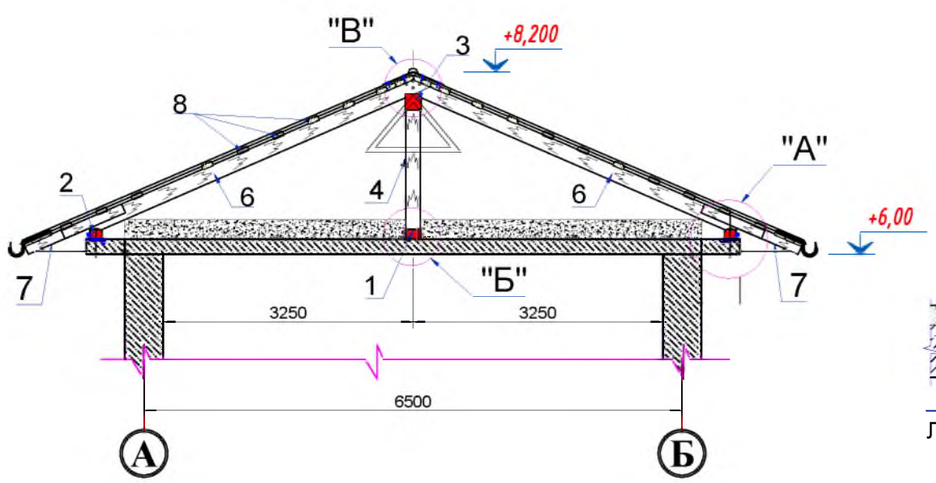


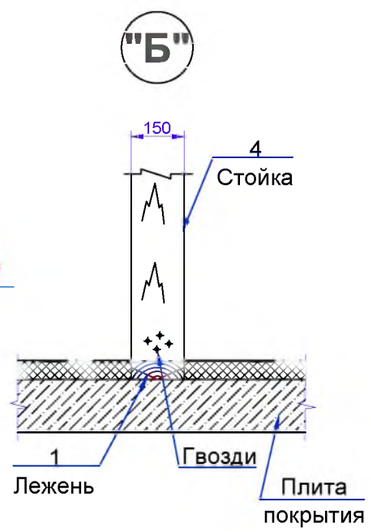
## Спецификация на один элемент

| Поз. | Обозначение | Сечение a, мм | Сечение b, мм | Сечение L, м, см | Колич. шт | Объем. м³. | Приме-чание |
|---|---|---|---|---|---|---|---|
| 1 | Лежень | 100 | 150 | 6,0 | 1 | 0.090 | |
| 2 | Мауэрлат | 80 | 100 | 36,40 | 1 | 0.291 | |
| 3 | Прогон | 150 | 150 | 6,0 | 1 | 0.135 | |
| 4 | Стойка | 150 | 150 | 2,20 | 4 | 0.198 | |
| 5 | Диагональная нога | 50 | 200 | 4,60 | 4 | 0.184 | |
| 6 | Стропильная нога | 50 | 150 | 3,80 | 18 | 0.513 | |
| 6* | Стропильная нога | 50 | 150 | 1,90 | 14 | 0.200 | Lср=1,90м |
| 7 | Кобылка | 40 | 120 | 0,8 | 36 | 0.138 | |
| 8 | Рейка шаг:400мм | 50 | 100 | 227,0 | 1 | 1.135 | |
| 9 | Профилированный настил t=0,05мм | | | | | 140м² | |
| 10 | Обшивка из пластика | | | | | 16м² | |
| 11 | Металлическая хомут для крепления мвуэрлат шаг: 1м | 50х5мм | | | 40 | 27кг | |
| 12 | Металлическая анкеры для крепления хомут | 10мм | | | 72 | | |

Металлический хомут для крепления мауэрлата на плата перекрытия

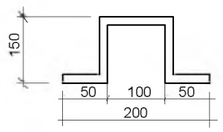


Примечание:

1. Мауэрлат укладывается на слой толя и заанкеруются в перекрытию.
2. Кровля выполняется из металлочерепицы или в олнистые стальн. листы t=0.05мм 140м².
3. Все деревянные элементы антисептируется и покрываются специальном составом для повышения огнестойкости.
4. Схема расположения элементов и спецификация элементов смотри на листе АС- 4.

| | | | | | | |
|---|---|---|---|---|---|---|
| | | | | | | АС |
| | | | | | | "Баркарорсозии пойгоххои обкашии Лохур-0,Лохур-1,Лохур-2 ва Лохур-3 дар нохияи Рудаки" |
| Изм. | Кол.уч. | Лист | № док. | Подп. | Дата | |
| Разработ. | | Фейдуллоев О. | | | | Насосной станции Лохур-0. Архитектурно-строительная часть. |
| ГИП | | Шомили У. | | | | |
| Нач. отдел | | Шомили У. | | | | Схема расположения деревянных элементов кровли.Спецификация |
| Норм. контр. | | Хайбаров С. | | | | |


| Стадия | Лист | Листов |
|---|---|---|
| РП | 5 | 8 |


ГУП "Проектный Институт "Точикгипроводхоз" Душанбе - 2026


Согласовано

Инв. подл | Подпись и дата | Взамен инв.

## Разрез 2-2

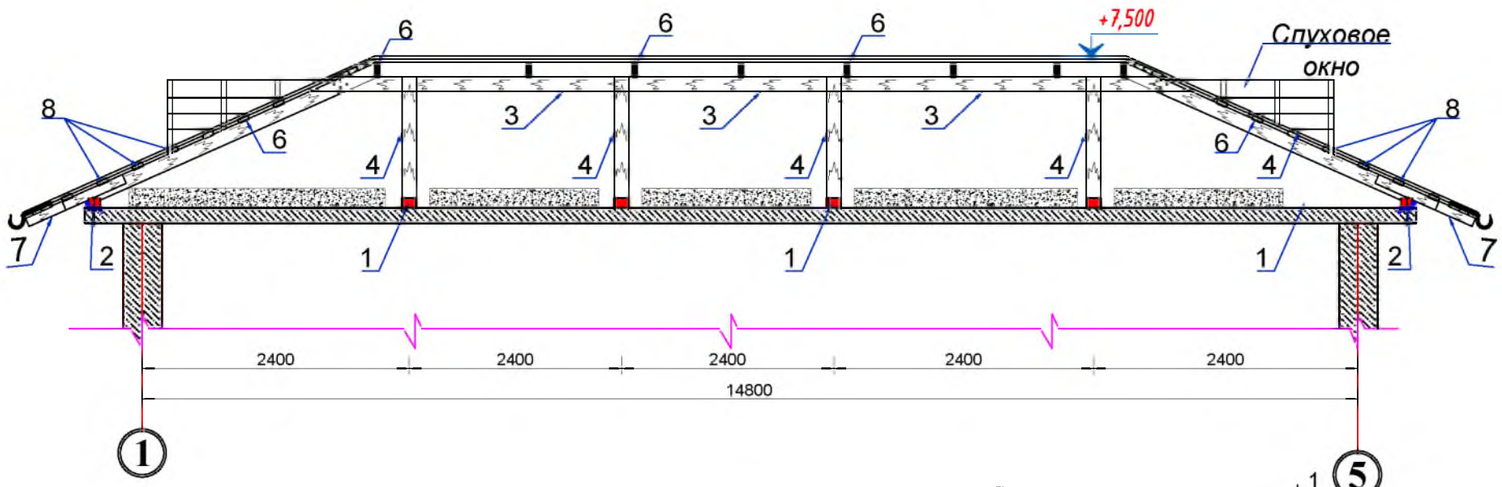

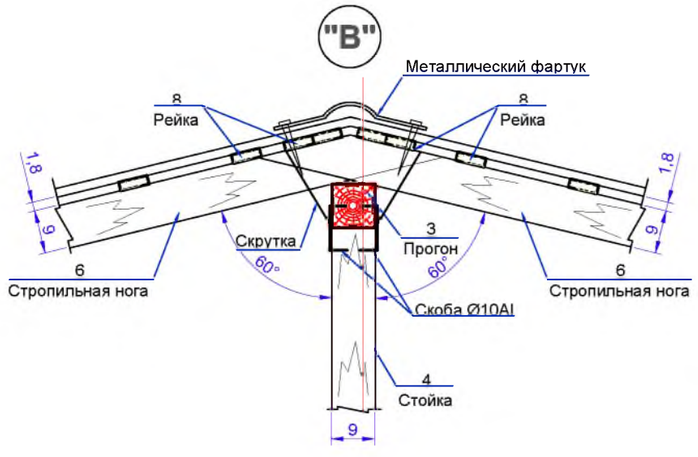
## Спецификация слуховых окон
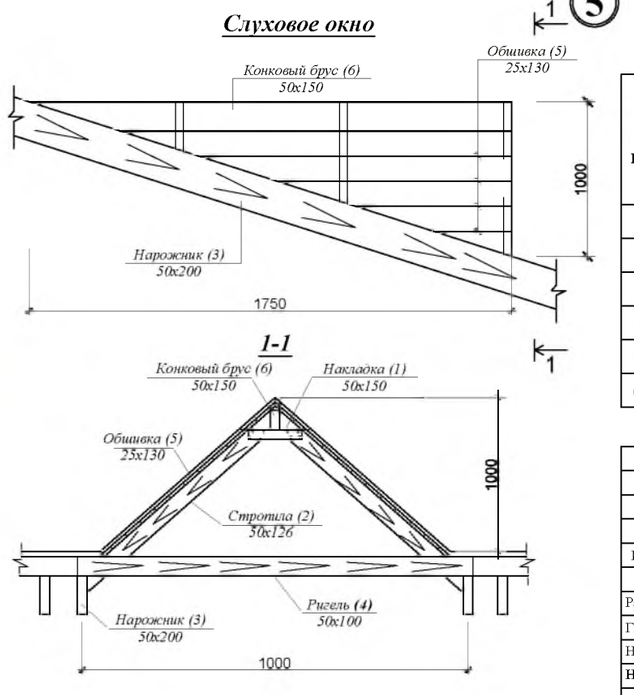
| № п/п | Наименование | Сечение мм х мм | Колич. шт. | Длина в м. | | Объём м³ | Примеч. |
|---|---|---|---|---|---|---|---|
| | | | | на один | всего | | |
| | | Расход на 1 слуховое окно | | | 2шт | | |
| 1 | Накладка | 50x150 | 1 | 0.30 | 0.30 | 0.002 | |
| 2 | Стропила | 50x126 | -- | -- | 7.0 | 0.044 | |
| 3 | Нарожник | 50x200 | 2 | 4,0 | 8 | 0,08 | |
| 4 | Ригель | 50x100 | 1 | 2.2 | 2.2 | 0,011 | |
| 5 | Обшивка | 25x130 | -- | -- | 30,6 | 0,10 | |
| 6 | Коньковый брус | 50x150 | 1 | 4,0 | 4,0 | 0,03 | |

Согласовано

Инв. подл | Подпись и дата | Взамен инв.

| Изм. | Кол.уч. | Лист | № док. | Подп. | Дата |
|---|---|---|---|---|---|
| Разработ. | | Фрайдунпоев О. | | | |
| ГИП | | Шомили У. | | | |
| Нач. отдел | | Шомили У. | | | |
| Норм. контр. | | Хайбаров С. | | | |

АС

"Баркарорсозии пойгоххои обкашии Лохур-0,Лохур-1,Лохур-2 ва Лохур-3 дар нохияи Рудаки"

Насосной станции Лохур-0.
Архитектурно-строительная часть.


| Стадия | Лист | Листов |
|---|---|---|
| РП | 6 | 8 |

Разрез 1-1;2-2. Узел "В"
Спецификация


ГУП "Проектный Институт "Точикгипроводхоз"
Душанбе - 2026

## Окна из металлопластиковых профилей

О-1

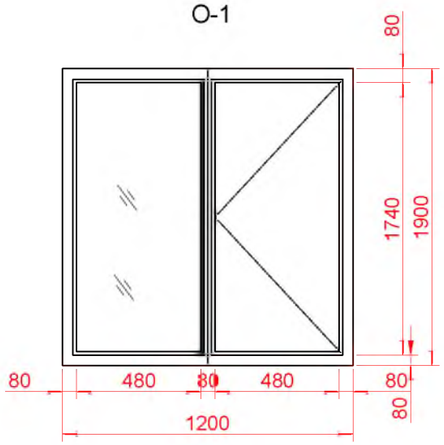



Сетка для окно. О-1

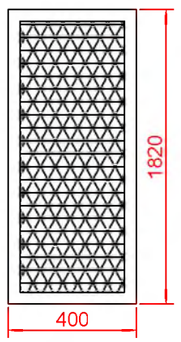


## Спецификация заполнения оконных и дверных проемов

| № поз. | Наименование | Размеры проема (ммхмм) | Количество | Всего | Примечание |
|---|---|---|---|---|---|
| 1 | О-1 | 1200 x 1900 | 2 | 2 | металлопластик |
| 2 | Сетки | 400 x 1820 | 2 | 2 | металлопластик |
| 3 | Д-1 | 1450 x 2100 | 1 | 1 | аллюминиевое |

Д - 1

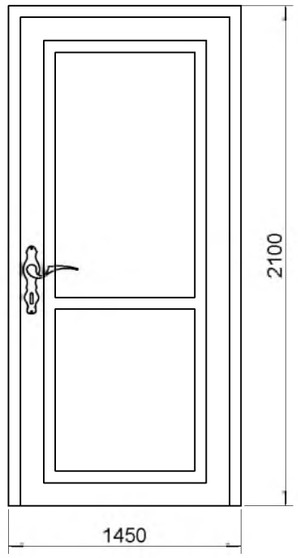


**Примечание:**

1. **Все окна и двери оборудуются навесами, ручками для открывания, замками в заводских условиях.**
2. **Размеры блоков окон и дверей даны по размеру проемов. Фирмам-изготовителям уточнить габариты блоков по месту, оставить монтажный зазор.**
3. **Размеры даны в мм**
4. **Данный лист рассматривать совместно с листами-2,3 и 5**

Согласовано


Взамен инв.

Подпись и дата


Инв. подл

| Изм. | Кол.уч. | Лист | № док. | Подп. | Дата | АС | | |
|---|---|---|---|---|---|---|---|---|
| | | | | | | "Баркарорсозии пойгоххои обкашии Лохур-0,Лохур-1,Лохур-2 ва Лохур-3 дар нохияи Рудаки" | | |
| Разработ. | | Фрайдунпосев О. | | | | Насосной станции Лохур-0. Архитектурно-строительная часть. | Стадия: РП | Лист: 7 / Листов: 8 |
| ГИП | | Шомили У. | | | | | | |
| Нач. отдел | | Шомили У. | | | | Окна из металло-пластиковых профилей О-1,2,3 и 4. Спецификация. | ГУП "Проектный Институт "Точикгипроводхоз" Душанбе - 2026 | |
| Норм. контр. | | Хайбаров С. | | | | | | |

## Ворота ВМ-1

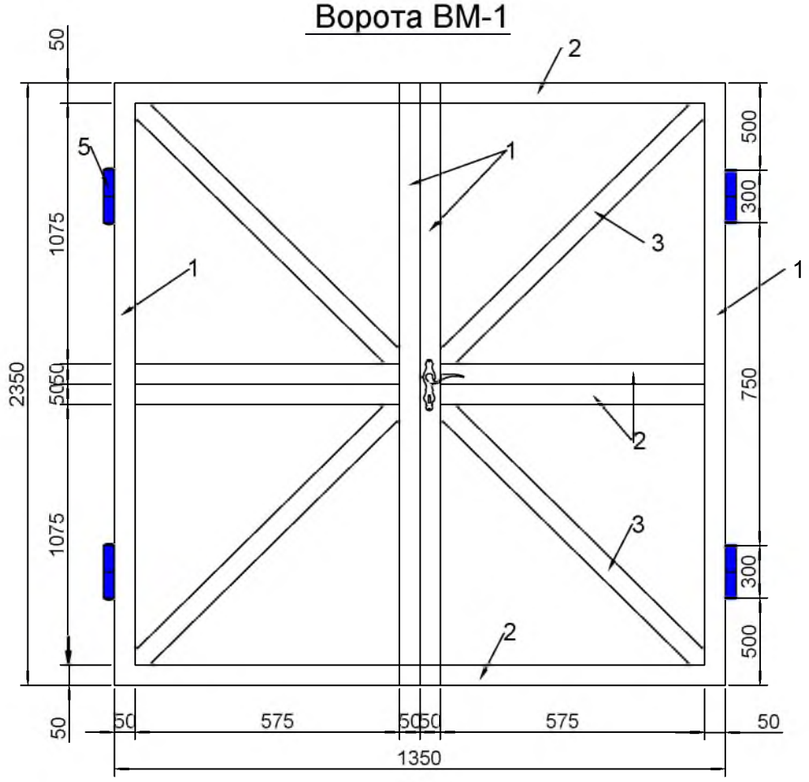


## Ворота ВМ-2

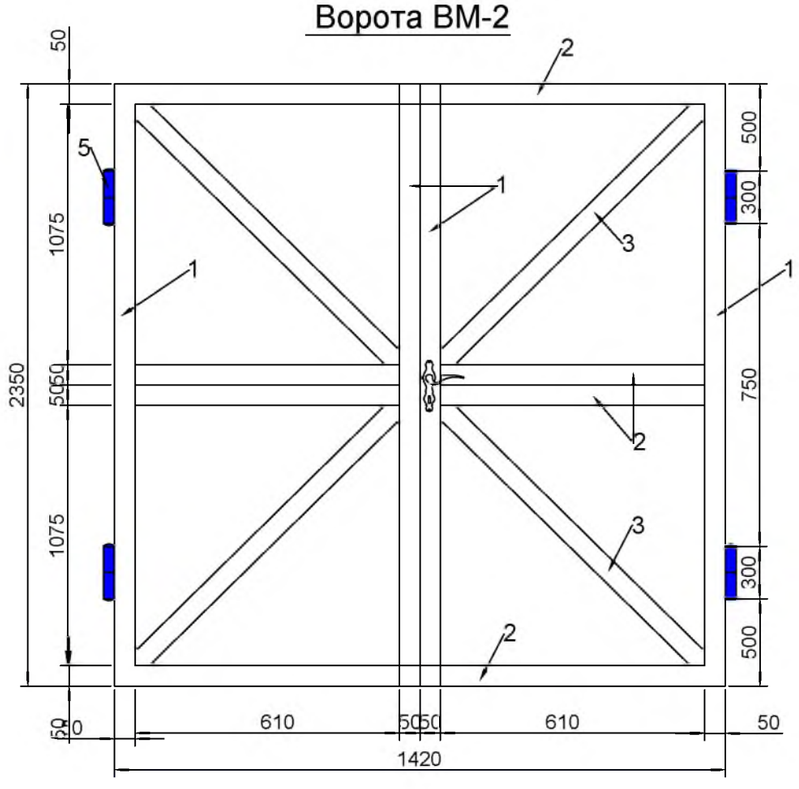


Спецификация дано на 1-го ворота

| №№ | Обозначение | Наименование | Кол-во | Масса ед.кг | Примечание |
|---|---|---|---|---|---|
| | Ворота ВМ-1 для Насосной станции | | | | |
| 1 | ГОСТ 8509-72 | Уголок L50x5 L=2850мм | 4 | 10,744 | 42,976 |
| 2 | ГОСТ 8509-72 | Уголок L50x6 L=1550мм | 4 | 5,843 | 23,372 |
| 3 | ГОСТ 8509-72 | Уголок L50x6 L=1360мм | 4 | 5,13 | 20,52 |
| 4 | ГОСТ 19903-74 | Обшивка из листовой сталь δ=1,5мм F=3,173м² | 1 | 37,36 | |
| 5 | Серия 3.017-1 вып.6 | Петля | 4 | 1,33 | 5,32 |
| 6 | Серия 3.017-1 вып.6 | Ручка | 1 | 1,93 | |
| 7 | Серия 3.017-1 вып.6 | Защелка 100 СБ | 1 | 2,0 | |
| | Ворота ВМ-2 для Насосной станции | | | | |
| 1 | ГОСТ 8509-72 | Уголок L50x5 L=2850мм | 4 | 10,744 | 42,976 |
| 2 | ГОСТ 8509-72 | Уголок L50x5 L=1620мм | 4 | 6,11 | 24,44 |
| 3 | ГОСТ 8509-72 | Уголок L50x6 L=1600мм | 4 | 6,032 | 24,128 |
| 4 | ГОСТ 19903-74 | Обшивка из листовой сталь δ=1,5мм F=3,340м² | 1 | 31,435 | |
| 5 | Серия 3.017-1 вып.6 | Петля | 4 | 1,33 | 5,32 |
| 6 | Серия 3.017-1 вып.6 | Ручка | 1 | 1,93 | |
| 7 | Серия 3.017-1 вып.6 | Защелка 100 СБ | 1 | 2,0 | |

**Примечание:**

**2.Все окна и двери оборудуются навесами, ручками для открывания, замками в заводских условиях.**

**3. Размеры блоков окон и дверей даны по размеру проемов. Фирмам-изготовителям уточнить габариты блоков по месту, оставить монтажный зазор.**

**4. Данный лист рассматривать совместно с лист-2,3,4,6,7,8 и 9**

**5. Спецификация дано на 1-го ворота всего по ВМ-1 и ВМ-2 -4шт**

Согласовано

Взамен инв.

Подпись и дата

Инв. подл

| | | | | | | |
|---|---|---|---|---|---|---|
| | | | | | | АС |
| | | | | | | "Баркарорсозии пойгоххои обкашии Лохур-0,Лохур-1,Лохур-2 ва Лохур-3 дар нохияи Рудаки" |
| Изм. | Кол.уч. | Лист | № док. | Поди. | Дата | |
| Разработ. | | Фрайдуннова О. | | | | Насосной станции Лохур-0. Архитектурно-строительная часть. |
| ГИП | | Шомили У. | | | | |
| Нач. отдел | | Шомили У. | | | | |
| Норм. контр. | | Хайбаров С. | | | | Вороты ВМ-1 и ВМ-2. Спецификация. |

| Стадия | Лист | Листов |
|---|---|---|
| РП | 8 | 8 |

**ГУП "Проектный Институт "Точикгипроводхоз" Душанбе - 2026**