АГЕНТСТВО ПО МЕЛИОРАЦИИ И ИРРИГАЦИИ
ПРИ ПРАВИТЕЛЬСТВЕ РЕСПУБЛИКИ ТАДЖИКИСТАН

ГУП "ПРОЕКТНЫЙ ИНСТИТУТ
"ТАДЖИКГИПРОВОДХОЗ"

РАБОЧИЙ ПРОЕКТ

"Баркарорсозии пойгоххои обкашии Лохур-0,Лохур-1,Лохур-2 ва Лохур-3 дар нохияи Рудаки"

АЛЬБОМ-1

Насосной станции Лохур-0.

ДЕЖУРНОЕ ПОМЕЩЕНИЕ.

ДУШАНБЕ-2026

АГЕНТСТВО ПО МЕЛИОРАЦИИ И ИРРИГАЦИИ
ПРИ ПРАВИТЕЛЬСТВЕ РЕСПУБЛИКИ ТАДЖИКИСТАН

ГУП "ПРОЕКТНЫЙ ИНСТИТУТ
"ТАДЖИКГИПРОВОДХОЗ"

РАБОЧИЙ ПРОЕКТ

"Баркарорсозии пойгоххои обкашии Лохур-0,Лохур-1,Лохур-2 ва Лохур-3 дар нохияи Рудаки"

АЛЬБОМ-1

Насосной станции Лохур-0.

ДЕЖУРНОЕ ПОМЕЩЕНИЕ.

ГЛ. ИНЖЕНЕР ИНСТИТУТА: ХАЙБАРОВ С.

ГЛ. ИНЖЕНЕР ПРОЕКТА: ШОМИЛИ У.

ДУШАНБЕ-2026

Таб. 1

Ведомость основных комплектов рабочих чертежей		
Обозначение	**Наименование**	**Примечание**
1	2	3
.ПЗ	Пояснительная записка	Книга-1
ТГИ	Инженерно-топогеодезический изысканий	Книга-2
ИГИ	Инженерно-геологический и гидрогеологичекий изысканий	Книга-3
ТХ	**Насосной станции Лохур-0.** Технологическая часть	Альбом-1
ГР	**Насосной станции Лохур-0.** Гидротехническое решение	Альбом-2
АС	**Насосной станции Лохур-0. Архитектурно-строительная часть**	Альбом-3
АС	**Насосной станции Лохур-0. Дежурное помещение Архитектурно-строительная часть**	Альбом-4
АС	**Насосной станции Лохур-0. Уборная на 1-го очко Архитектурно-строительная часть**	Альбом-5
ЭО	Электротехническая часть	Альбом-6
СМ	Сметная документация	Книга-4

Таб.3

Ведомость рабочих чертежей основного комплекта		
Лист	Наименование	Примечание
1	**Дежурное помещение**.Общие данные	
2	**Дежурное помещение**.Продолжение общие данные	
3	Дежурное помещение. Фасад А-Б и Б-А. План кровля.	
4	Дежурное помещение.Фасады 1-2 и 2-1.	
5	Дежурное помещение. Фасад А-Б. Схема расположения стропил. Спецификация.	
6	Дежурное помещение. План. План фундамента.Ведомость объемов работ.	
7	Дежурное помещение. Окн-1. Др-1 и 2. Спецификация оконных и дверных проемов.	
8	Дежурное помещение. План расположения деревянных балок. Спецификация	
9	Дежурное помещение. Фрагмент армирование перемычек. Спецификация расхода материалов	
10	Дежурное помещение. Разрезы 3-3 и 4-4. Спецификация	
11	Дежурное помещение. Перемычки ПРМ-1 и 2 .Спецификация расход материалов ОП-1	

Настоящий проект выполнен в соответствии с действующими нормами и правилами в том числе по взрыво-пожарной безопасности

Гл.инженер проекта Шомили У .

Детали полов

Наименование или номер помещения по проекту	Тип по проекту		Схема	Элементы и их толщина	м^2
	1	этаж		1. Ламинат 2. Цементная стяжка 3.подготовка из бетона В7,5 t=10 см 4.Гравийно-песчанная подготовка t=10см	11

Ведомость отделки помещений

	Наименование или номер помещения	Потолок		Стены и перегородки		Примечания
		Площадь	Вид отделки	Площадь	Вид отделки	
1	Помещение дежурная	12,0	Шпатлевка с последующей водоэмульсиенной окраской	91,0	Шпаклевка с последующей водоэмульсионной краской.	

Изм.	Кол.уч.	Лист	№ док.	Поди.	Дата	АС		
						"Баркарорсозии пойгоххои обкашии Лохур-0,Лохур-1,Лохур-2 ва Лохур-3 дар нохияи Рудаки"		
Разработ.		Фрайдунпоев О.				Насосной станции Лохур-0. Архитектурно-строительная часть.	Стадия: РП	Лист: 1 / Листов: 11
ГИП		Шомили У.						
Нач. отдел		Шомили У.				Дежурное помещение. Общие данные	ГУП "Проектный Институт "Точикгипроводхоз" Душанбе - 2026	
Норм. контр.		Хайбаров С.						

Согласовано

Взамен инв

Подпись и дата

Инв. подл

Исходные данные

Проект разработан для строительства в
IIВ климатическом районе с расчетной температурой -16°С.
Площадка строительства характеризуется следующими данными:
- вес снегового покрова для II-го района - 0,7 кПа;
- скоростное давление ветра для II-района - 0,30 кПа;
В основании фундаментов залегают грунты;
Сейсмичность стройплощадки - 7 балл
Степень огнестойкости здания - I.
Класс ответственности здания - II.

Строительные конструкции
Здание запроектировано в комплексном конструктивном решении.
Фундаменты - монолитные железобетонные из бетона класса В 15.
Сейсмопояс - монолитные железобетонные из бетона класса В 15.
Отмостка - бетонная по слою щебня толщиной 150 мм, шириной 1,50 м.
Стены из кирпичные кладки.
Перекрытие - деревянное из балок сечением 50х150 мм.
Кровля - из волнистой оцинкованной кровельной стали t=0,4-0,5мм.
Оконные блоки - индивидуального изготовления из пластика.
Дверные блоки - индивидуального изготовления из металлопластика.
Крыльца из бетона класса В15.

Антисейсмические мероприятия
Антисейсмические мероприятия предусмотрены в соответствии с требованиями главы МКС ЧТ 22-07-2007 "Строительство в сейсмических районах. Нормы проектирования". Несущие элементы железобетонного каркаса рассчитаны и законструированы с учетом воздействия горизонтальной сейсмической силы.

Антикоррозийная защита строительных конструкций
Для обеспечения требуемой долговечности все металлические конструкции и необетонированные закладные и соединительные изделия должны быть покрыты антикоррозийными лакокрасочными материалами 1 группы - пентафталевые, глифталевые, эпокси- эфирные, алкидностирольные, масляные, масляно-битумные, алкидно-уретановые, нитроцеллюзные (лаки ПФ-170 и ПФ-171 с 10-15% алюминиевой пудры, эмали ПФ-115, ПФ-113, ПФ-1126, ПФ-1189 и др.).
Все работы выполнять в соответствии с указаниями главы СНиП 2.03.11-85.

Защита деревянных элементов и изделий от возгорания и гниения
Все деревянные конструкции и изделия здания должны быть защищены от гниения, поражения насекомыми и дереворазрушающими грибами, а также от возгорания в соответствии с указаниями главы СНиП 2.03.11-85 "Защита строительных конструкций от коррозии". Для защиты деревянных конструкций от биологических агентов следует предусмотреть влагостойкое лакокрасочное покрытие или использовать влагобиозащитные пропиточные составы. В этих целях рекомендуется использовать пропиточные составы марки ТХЭФ-ПТ или марки БК (буроугольная композиция).

Противопожарные мероприятия
Все противопожарные мероприятия предусмотрены согласно главы МКС ЧТ 21-01-2007.*

Настоящий проект выполнен в соответствии с действующими нормами и правилами в том числе по взрыво-пожарной безопасности

Гл.инженер проекта Шомили У.

Согласовано

Взамен инв

Подпись и дата

Инв. подл

ТЕХНИКО –ЭКОНОМИЧЕСКИЕ ПОКАЗАТЕЛИ

НАИМЕНОВАНИЕ	КОЛИЧЕСТВО м²
Площадь застройки	19,18
Строительный обь?м	43,3
Общая площадь	16,66
Расчетная площадь	10,34
Полезная площадь	10,34

ХАРАКТЕРИСТИКА ИНЖЕНЕРНО - ГЕОЛОГИЧЕСКИХ УСЛОВИЙ

Согласно заключению по архивным материалом об инженерно геологических изысканиях площадки строительства участок проектируемого строительство расположен в юго-западной районе Дангара .
Рельеф участка сравнительно ровный, с небольшими колебаниями в микрорельефе.
В геологическом строений принимают участке аллювиально-пролювиальные отложение. Грунты в основании фундаментов до разведанной глубины 5 м являются неоднородной.
Глинистый грунты участка обладают просадочными свойствами, в основном, при дополнительных нагрузках.Суммарная величина от собственного веса более 5,0см.Тип грунтовых условий по проявлению посадочных свойств II (второй). Крутизна откосов и траншей в зависимости глубина отрывки составляет:

для суглинка - до 1.5м 1:0.0, до 3.0м 1:0.5, до 5.0м 1:0.75. для галечника - до 1.5м 1:0.5, до 3.0м 1:1, до 5.0м 1:1. (МКС ЧТ 50-01-2007) При наличии в основании глинистых грунтов рекомендуется применение ленточные фундаменты. При углублении до кровли галечника, подготовка оснований не требуется.

Современные физико-геологические процессы на участке и прилегающей к нему территории не отмечены, за исключением хозяйственной деятельности человека (искусственные выемки, насыпи грунтов, посадки фруктовых деревьев). При проектировании предусмотреть пересадку фруктовых деревьев из контура проектируемого здания .


Ведомость отделки фасадов

Фасад	Элементы	Отделка	Колер
Все фасады	Стены	Штукатурка, окраска фасадными красками (дождик) - AMY TERAZIT	Код: 223и 230
	Цоколь , крыльца	Штукатурка и фасадными красками	
	Заполнение оконных и дверных проемов (наружные)	Металлопластик	
	Кровли	Деревянная кровля опшивка из профилированный настил	
	Водослив с подоконников	Облицовка кровельной жестью , окраска эмалевой краской за 2 раза	


АС

Изм.	Кол.уч.	Лист	№ док.	Подп.	Дата	АС		
						"Баркарорсозии пойгоххои обкашии Лохур-0,Лохур-1,Лохур-2 ва Лохур-3 дар нохияи Рудаки"		
Разработ.		Фрайдунпсев О.				Насосной станции Лохур-0. Архитектурно-строительная часть.	Стадия: РП	Лист: 2 / Листов: 11
ГИП		Шомили У.						
Нач. отдел		Шомили У.				Дежурное помещение. Общие данные.продолжение	ГУП "Проектный Институт "Точикгипроводхоз" Душанбе - 2026	
Норм. контр.		Хайбаров С.						


Фасад А-Б

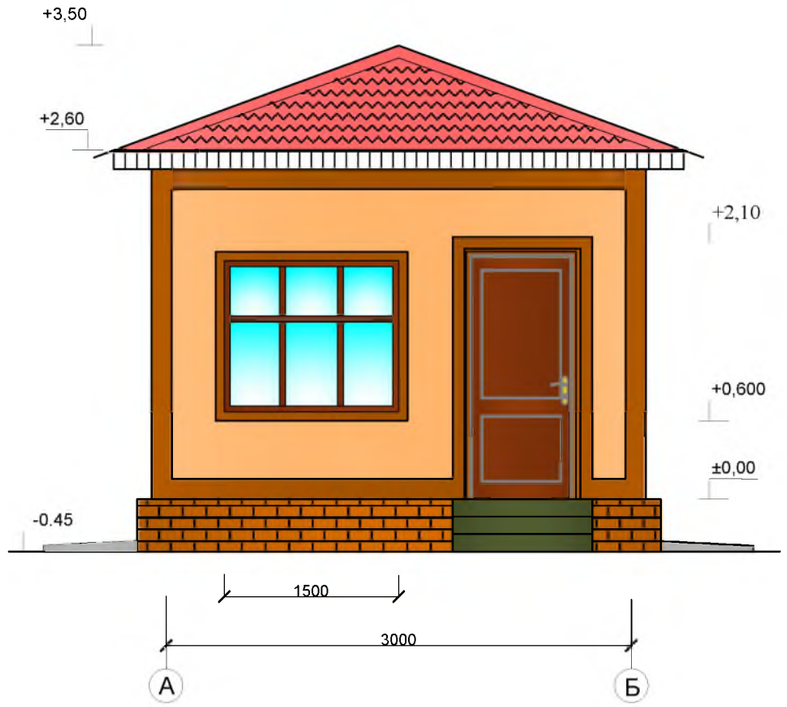

План кровля

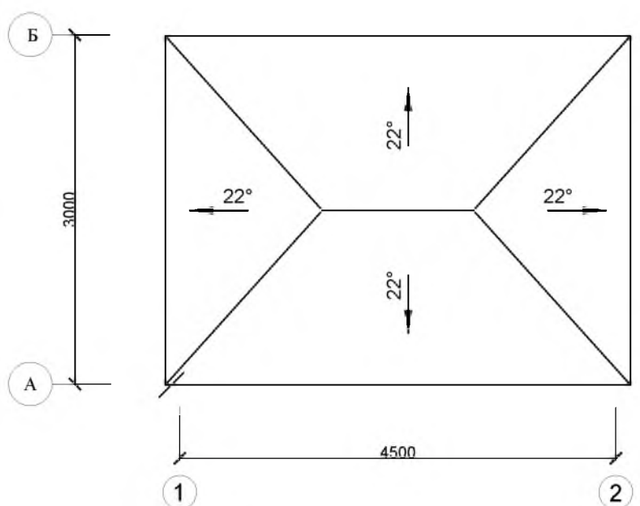

Фасад Б-А

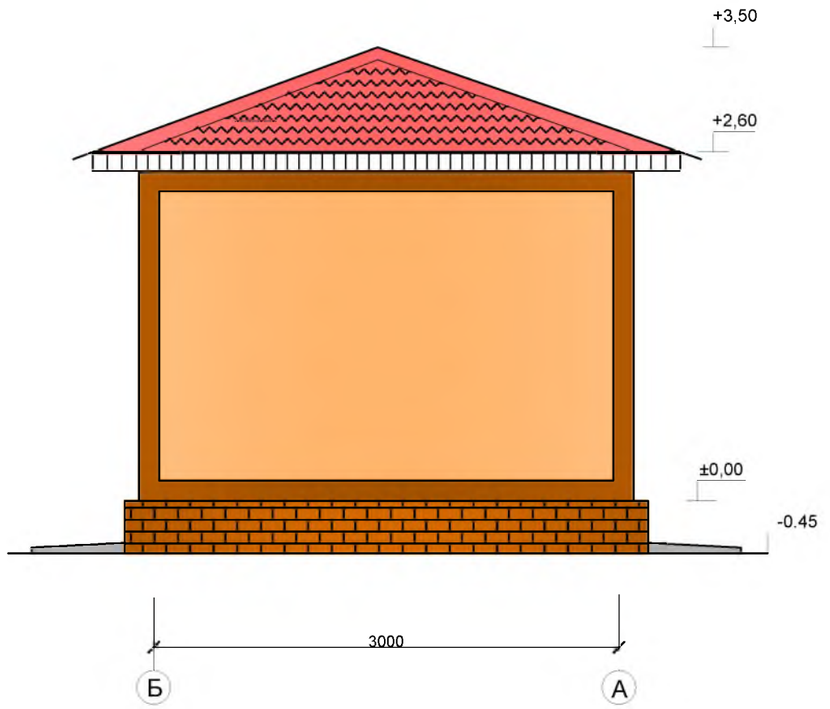

НАРУЖНАЯ ОТДЕЛКА ФАСАДОВ

1. Наружные стены улучшенная штукатурка с последующей фасадной покраской фирмы ТЕКС.
2. Цоколь улучшенная штукатурка с последующей фактурной окраской фирмы ТЕКС.
3. Крыльцо бетонная стяжка.
4. Кровля из оцинкованных листов.
5. Окна пластиковые
6. Двери из металлопластика

Согласовано

Инв. подл | Подпись и дата | Взамен инв.


АС

						АС
						"Баркарорсозии пойгоххои обкашии Лохур-0,Лохур-1,Лохур-2 ва Лохур-3 дар нохияи Рудаки"
Изм.	Кол.уч.	Лист	№ док.	Подп.	Дата	
Разработ.		Фрайдуншоев О.				Насосной станции Лохур-0. Архитектурно-строительная часть.
ГИП		Шомили У.				
Нач. отдел		Шомили У.				Дежурное помещение. Фасад А-Б и Б-А. План кровля.
Норм. контр.		Хайбаров С.				


Стадия	Лист	Листов
РП	3	11

ГУП "Проектный Институт "Точикгипроводхоз" Душанбе - 2026

Фасад 1-2

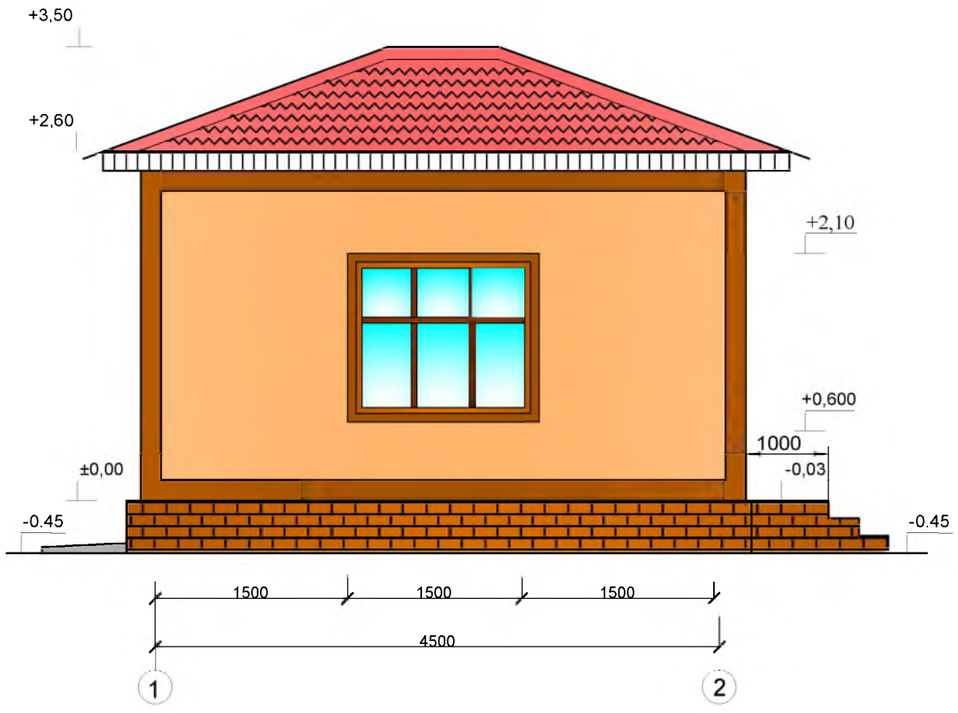

Фасад 2-1

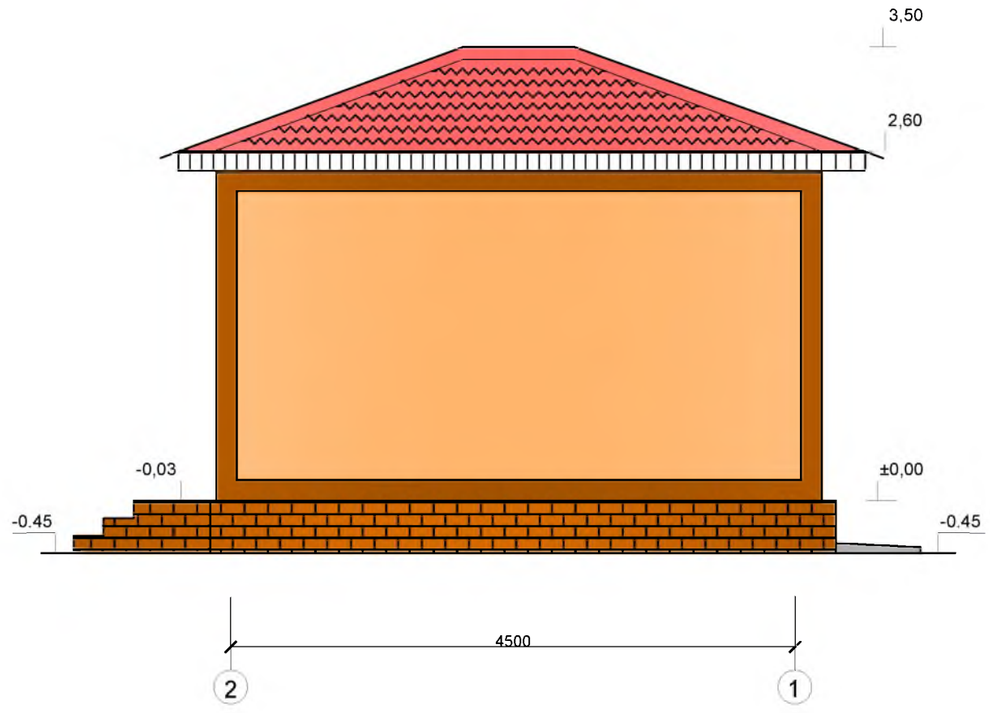

Согласовано

Взамен инв.

Подпись и дата

Инв. подл


AC

						AC
						"Баркарорсозии пойгоххои обкашии Лохур-0,Лохур-1,Лохур-2 ва Лохур-3 дар нохияи Рудаки"
Изм.	Кол.уч.	Лист	№ док.	Подп.	Дата	
Разработ.		Фрайдуншоев О.				Насосной станции Лохур-0. Архитектурно-строительная часть.
ГИП		Шомили У.				
Нач. отдел		Шомили У.				
Норм. контр.		Хайбаров С.				Дежурное помещение. Фасад 1-2 и 2-1


Стадия	Лист	Листов
РП	4	11

ГУП "Проектный Институт "Точикгипроводхоз" Душанбе - 2026

Фасад А-Б

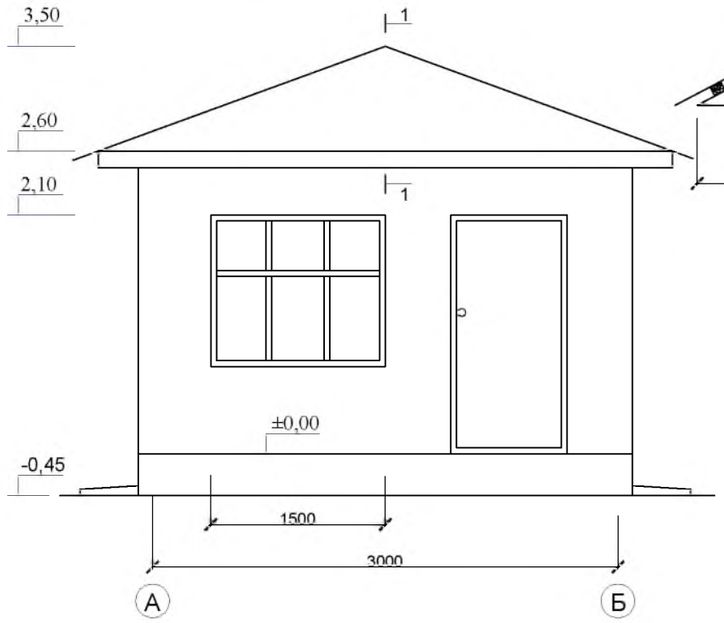

1-1

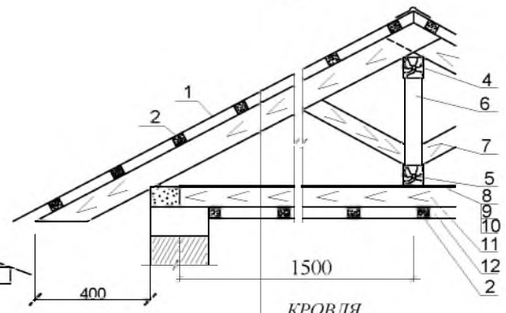


КРОВЛЯ

1 Металлочерепица t=0,4мм
2 Брусок 80х30 шаг 350
3 Стропильная нога 50х150
4 Верхний прогон 100х200
5 Нижний прогон 100х200
6 Стойка 150х150
7 Подкосы стойки 150х100
8 Глиносоломенная стяжка t=6см
9 Рубероид 1 слой
10 Горбыли
11 Мауэрлат 150х70
12 Гипсокартон


Спецификация

№№	Обозначение	Наименование	Ед. изм	Кол-во	Примечание
		Кровля			
1	ГОСТ 30340-95	Металлочерепица t=0,4 мм	м²	23,0	
2	ГОСТ 8466-66	Брусок 80х30 шаг350	м³	0,08	Lобщ=30600мм
3	ГОСТ 8466-66	Стропильная нога 50х150	м³	0,18	Lобщ=24000мм
4	ГОСТ 8466-66	**Верхний прогон 100х200**	шт/м³	1/0,026	Lобщ=1300мм
5	ГОСТ 8466-66	Нижний прогон 100х200	шт/м³	1/0,026	Lобщ=1300мм
6	ГОСТ 8466-66	Стойка 150х150	шт/м³	2/0,032	Lобщ=700мм
7	ГОСТ 8466-66	**Подкосы стойки 150х100**	шт/м³	4/0,05	Lобщ=850мм
8		Глиносоломенная стяжка	м2	17,5	
9		Рубероид 1 слой	м2	17.5	
10	ГОСТ 8466-66	Горбыли	м3	0,48	
11	ГОСТ 8466-66	Мауэрлат 150х70	м3	0,147	
12		Гипсокартон	м2	12	
		Сейсмопояс			
13	ГОСТ 26633-85	Бетон В15	м3	1,04	
14	ГОСТ 5781-81	Арматура ø10 А III	кг	34,55	
15	ГОСТ 5781-81	Арматура ø6 А I	кг	6,22	

Схема рассположения стропил

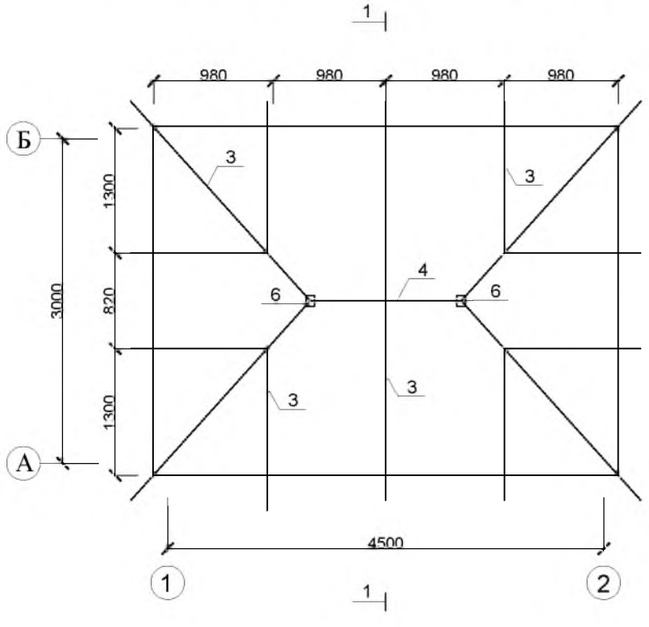

Сейсмопояс

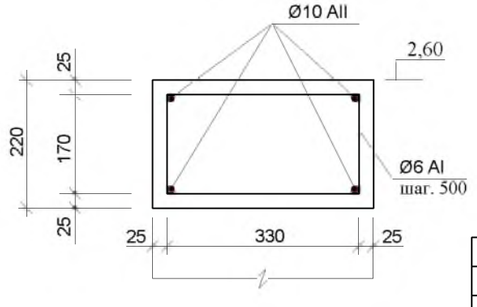

Согласовано

Взамен инв.

Подпись и дата

Инв. подл


АС

						АС
						"Баркарорсозии пойгоххои обкашии Лохур-0,Лохур-1,Лохур-2 ва Лохур-3 дар нохияи Рудаки"
Изм.	Кол.уч.	Лист	№ док.	Подп.	Дата	
Разработ.		Фрайдунпоев О.				Насосной станции Лохур-0. Архитектурно-строительная часть.
ГИП		Шомили У.				
Нач. отдел		Шомили У.				Дежурное помещение. Фасад А-Б. Схема расположения стропил. Спецификация.
Норм. контр.		Хайбаров С.				


Стадия	Лист	Листов
РП	5	11

ГУП "Проектный Институт "Точикгипроводхоз" Душанбе - 2026

ПЛАН на отм. ±0,000

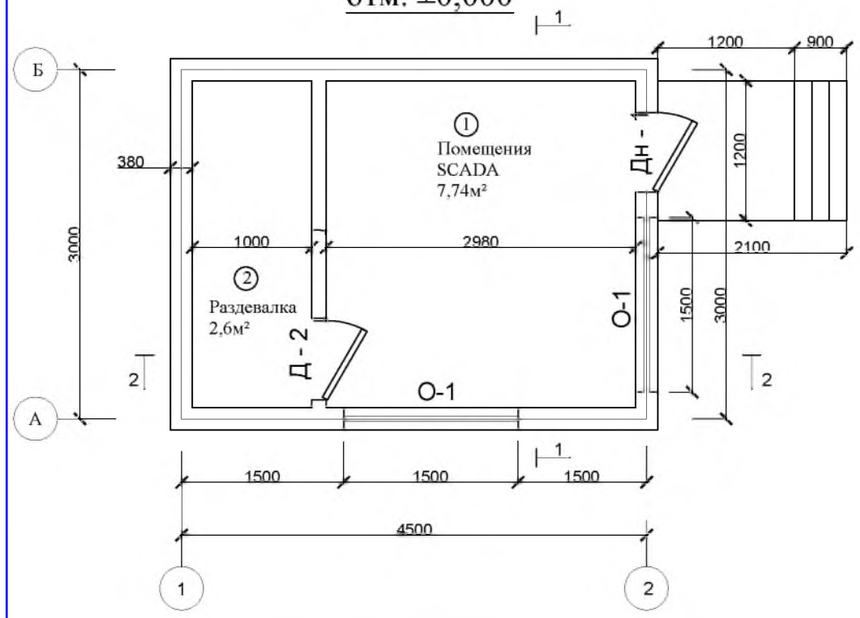

План фундамента

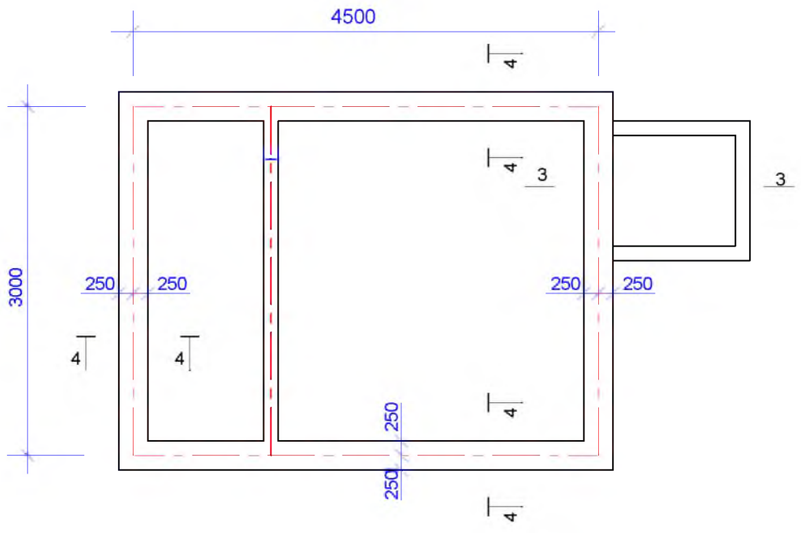

Ведомость объемов работ

N/N n/n	НАИМЕНОВАНИЕ	Ед изм	Кол-во	Примечание
1	Выемка грунта под фундамент	м3	12,0	
2	Обратная качественная засыпка	м3	7.0	
3	Стены из кирпичана цементном растворе В5	м3	17.0	
4	Ленточный фундаментна бетоне В15 t=0,5м	м3	5.4	
5	Порог из бетона В15	м3	0,4	
6	Отмостка вокруг домика из бетона В15	м3	1,5	
7	Окно пластиковый 150х150	шт	2	
8	Дверь металлопластиковый 210х100см	шт	1	
9	Дверь металлический 210х100см	шт	1	
10	Полы: -цементная стяжка t=2см	м2	12.23	
	-подготовка из бетона В7,5 t=10см	м3	1.0	
	-гравийная подготовка t=10см	м3	1.1	
11	Ламинат t=8мм	м2	11	
12	Внутренняя отделка			
	а)штукатурка стен	м2	53	
	б)Шпаклевка стен и водоэмуционной краской	м2	53	
13	Наружная отделка			
	а) штукатурка стен известково-цементно-песчанным раствором	м2	38	
	б) Шпаклевка	м2	38	
14	Покраска потолка а) эмулционной краской	м2	12	
15	Гидроизоляция верх фундамента на цем.раствором сост 1/3	м2	6,0	
16	Гидроизоляция фундамента обмазочная за 2 раза	м2	26,0	

Экспликация помещение

№п/п	Наименование	Ед изм	Кол-во	Примечание
1	Комната SCADA	м²	7,74	
2	Раздевалка	м²	2,6	

Примечания: *Все деревянные элементы должны быть антисептированы и покрыты сернокислым аммонием с целью огнезащиты.*
Защитную обработку деревянных конструкций выполнить в соответствии с требованиями СНиП 2.03.11-85 гл.3 и СНиП 2.01.02-85 п.1.8

АС

Изм.	Кол. уч	Лист	№ док.	Подп.	Дата	Восстановление насосной станции "Лохур-0" Архитектурно-строительная часть Дежурное помещение. План фундамента.	Лист 6


Согласовано

Взамен инв.


Подпись и дата

Инв. подл

Разрез 1-1

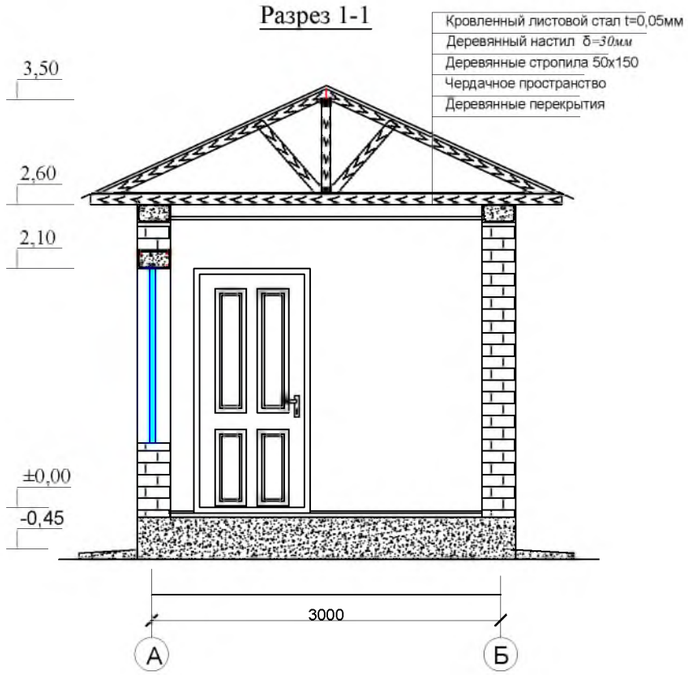


Разрез 2-2

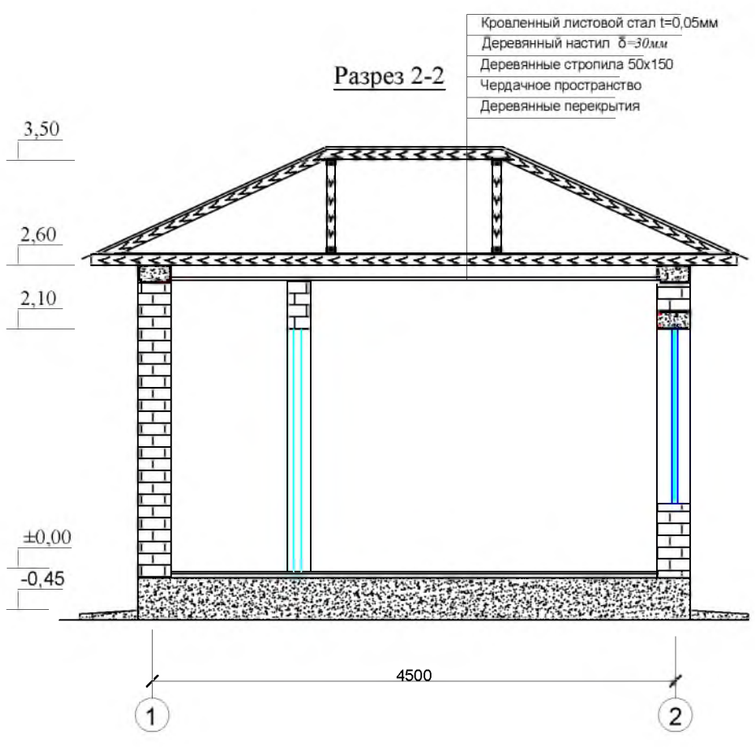


Спецификация заполнения оконных и дверных проемов

№ поз.	Наименование	Размеры проема (ммхмм)	Количество		Всего	Примечание
			1 этаж	2 этаж		
1	Дн-1	1000 х 2100	1	1	1	Металлопластика
2	Д-2	1000 х 2100	1	1	1	деревянная
3	О-1	1500х 1500	1	1	1	Металлопластика


О-1

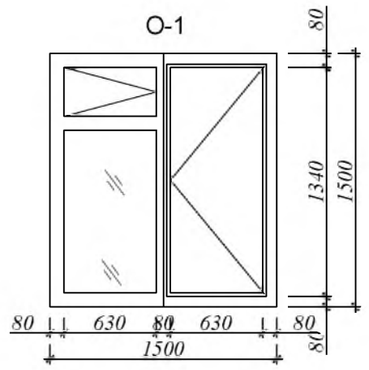

Дн - 1

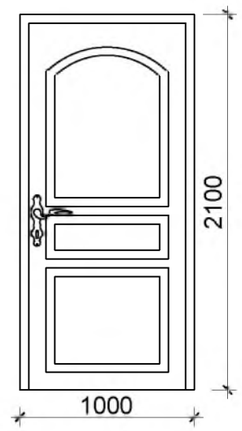

Д - 2

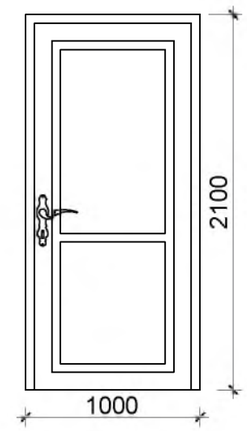

Примечание:

1.Все окна и двери оборудуются навесами, ручками для открывания, замками в заводских условиях.
2. Размеры блоков окон и дверей даны по размеру проемов. Фирмам-изготовителям уточнить габариты блоков по месту, оставить монтажный зазор.

Согласовано

Взамен инв.

Подпись и дата

Инв. подл


АС

Изм.	Кол.уч.	Лист	№ док.	Подп.	Дата	АС
						"Баркарорсозии пойгоххои обкашии Лохур-0,Лохур-1,Лохур-2 ва Лохур-3 дар нохияи Рудаки"
Разработ.		Фрайдунпоев О.				Насосной станции Лохур-0. Архитектурно-строительная часть.
ГИП		Шомили У.				
Нач. отдел		Шомили У.				Дежурное помещение. Окн-1. Др-1 и 2. Спецификация оконных и дверных проемов.
Норм. контр.		Хайбаров С.				

Стадия	Лист	Листов
РП	7	11

ГУП "Проектный Институт "Точикгипроводхоз" Душанбе - 2026

ПЛАН
расположения деревянных балок

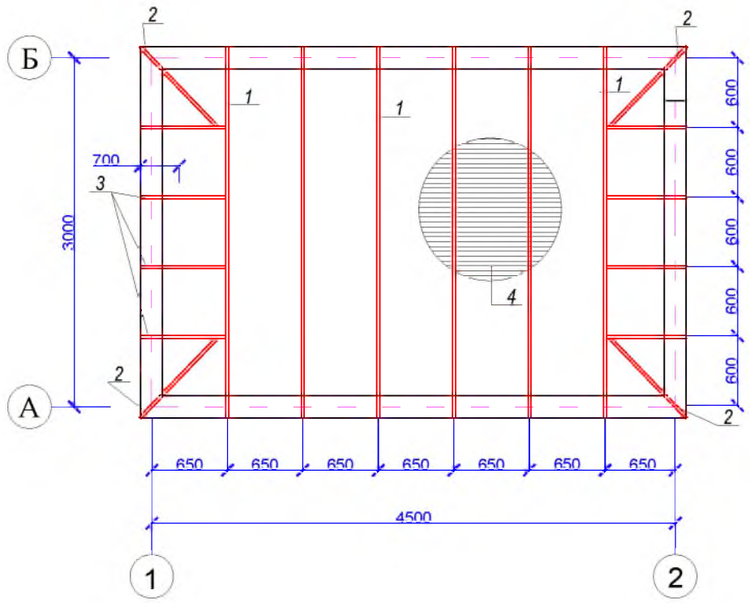

СПЕЦИФИКАЦИЯ РАСХОД МАТЕРИАЛОВ ДЕРЕВЯННЫХ БАЛОК

	Наименование	Сечение мм х мм	Колич шт	Длина м		Объём м³	Прим
				на один	всего		
1	Деревяные балки	50х150	6,0	3400	0,0255	0,153	
2	Деревяные балки	50х150	4,0	850	0,0063	0,025	
3	Деревяные балки	50х150	8,0	650	0,0048	0,039	
4	Черный потолок	20х120	-	-	-	0,213	

Примечания: *Все деревянные элементы должны быть антисептированы и покрыты сернокислым аммонием с целью огнезащиты. Защитную обработку деревянных конструкций выполнить в соответствии с требованиями СНиП 2.03.11-85 гл.3 и СНиП 2.01.02-85 п.1.8*

Согласовано

Взамен инв.

Подпись и дата

Инв. подл


АС

						АС
						"Баркарорсозии пойгоххои обкашии Лохур-0,Лохур-1,Лохур-2 ва Лохур-3 дар нохияи Рудаки"
Изм.	Кол.уч.	Лист	№ док.	Подп.	Дата	
Разработ.		Фрайдунпоев О.				Насосной станции Лохур-0. Архитектурно-строительная часть.
ГИП		Шомили У.				
Нач. отдел		Шомили У.				Дежурное помещение. План расположения деревянных балок. Спецификация
Норм. контр.		Хайбаров С.				


Стадия	Лист	Листов
РП	8	11

ГУП "Проектный Институт "Точикгипроводхоз" Душанбе - 2026

РАЗВЁРТКА СТЕН ПО ОСИ "А-Б "

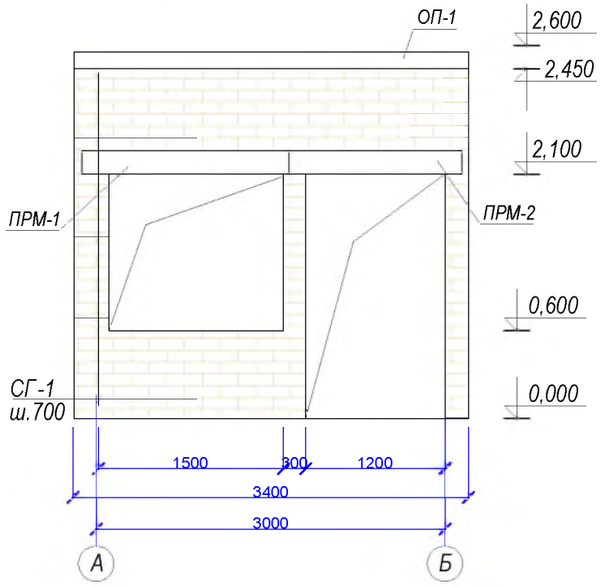


РАЗВЁРТКА СТЕН ПО ОСИ "1-2 "

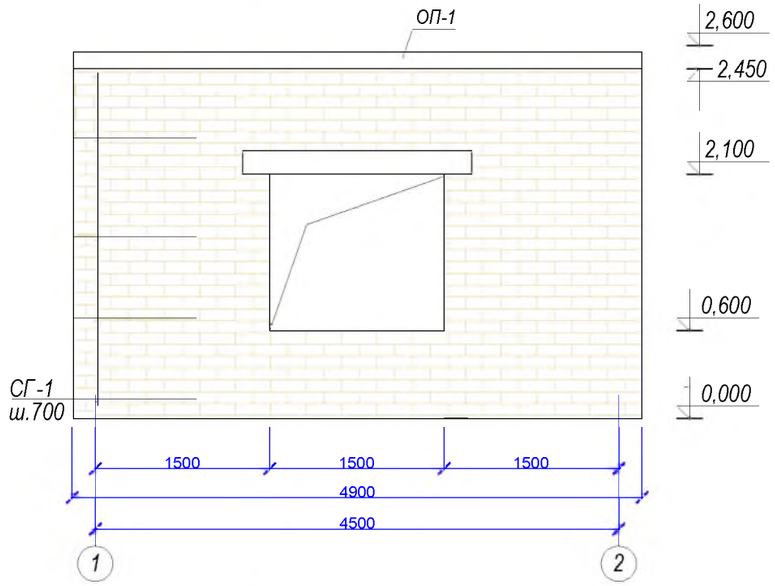


СПЕЦИФИКАЦИЯ РАСХОД МАТЕРИАЛОВ СЕТКА СГ-1.

Марка поз.	Обозначение	Наименование		Кол	Масса ед., кг	
		Сетка Сг-1		90		
		Сг-1 (на 1п.м)		1		
1		Ø 5 Вр-1	L=1000	5	0,155	0,775
2		Ø 3 Вр -1	L= 370	3	0,052	0,05772


РАЗВЁРТКА СТЕН ПО ОСИ "Б-А "

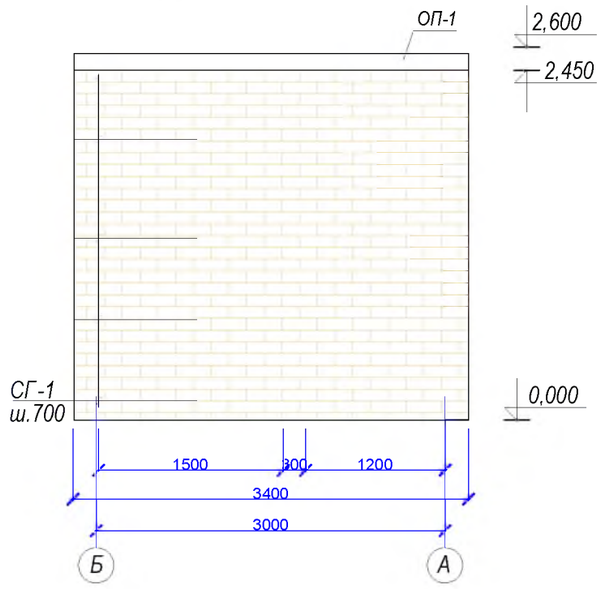

РАЗВЁРТКА СТЕН ПО ОСИ "2-1 "

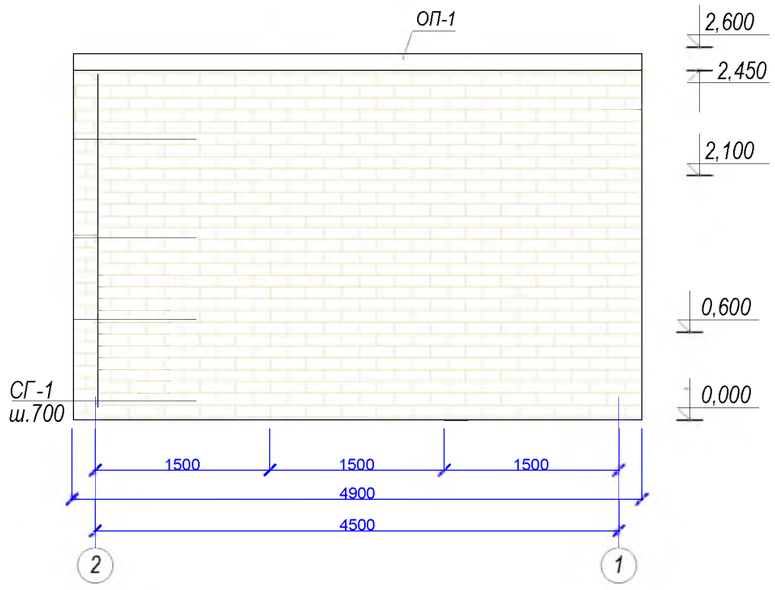

СГ-1 (на 1 п.м.)

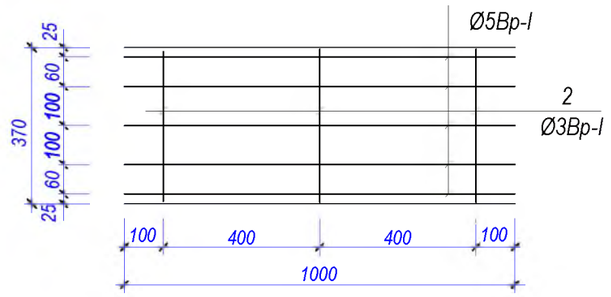

ПРИМЕЧАНИЕ:

1. Стены выполнить из кирпича толщ. 380 мм
2. Бетонирование сердечников выполняется после кладки кирпича .
3. Сетка горизонтальная СГ-1, ставить после 2 ряда кладки, далее шагом 700мм

Согласовано

Взамен инв.

Подпись и дата

Инв. подл

AC

AC

"Баркарорсозии пойгоххои обкашии Лохур-0,Лохур-1,Лохур-2 ва Лохур-3 дар нохияи Рудаки"

Изм.	Кол.уч.	Лист	№ док.	Подп.	Дата
Разработ.		Фрайдунпосев О.			
ГИП		Шомили У.			
Нач. отдел		Шомили У.			
Норм. контр.		Хайбаров С.			


Насосной станции Лохур-0.
Архитектурно-строительная часть.

Стадия	Лист	Листов
РП	9	11


Дежурное помещение.
Фрагмент армирование перемычек.
Спецификация расхода материалов

ГУП "Проектный Институт "Точикгипроводхоз"
Душанбе - 2026

3-3

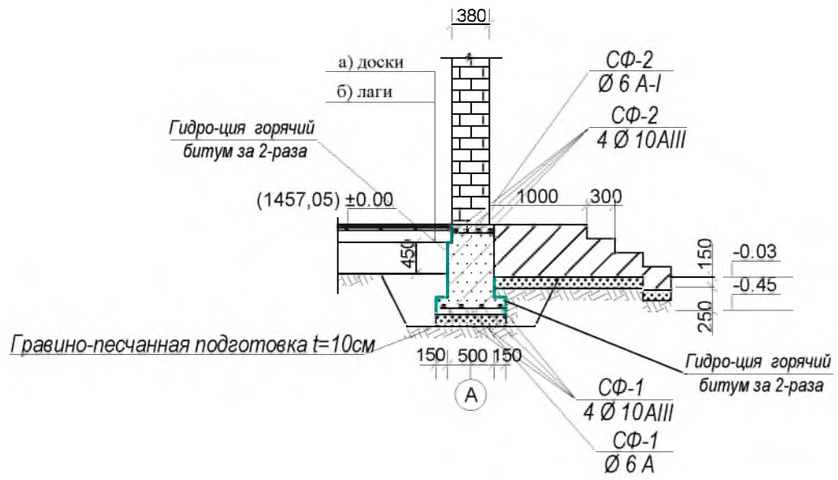


4-4

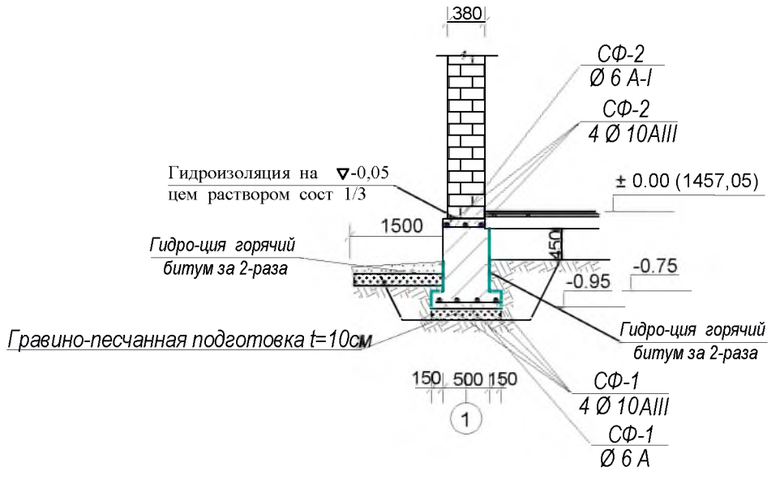


СПЕЦИФИКАЦИЯ РАСХОД МАТЕРИАЛОВ НА КОНСТРУКЦИИ ФУНДАМЕНТОВ ФЛ - 1

Марка поз.	Обозначение	Наименование	Кол	Масса ед., кг	
		Фундамент Фл - 1	15,0		п.м
Сф - 1		Сф - 1 (на 1 п. м)			
1		Ø 10 A III L= 1000	4	0,617	2,47
2		Ø 6 A I L= 700	5	0,222	0,777
		Фундамент Фл - 1	15,0		п.м
Сф - 2		Сф - 2 (на 1 п. м)			
1		Ø 10 A III L= 1000	3	0,617	1,851
2		Ø 6 A I L= 400	5	0,222	0,444

Сетка СФ-1 (на 1 пог. м.)

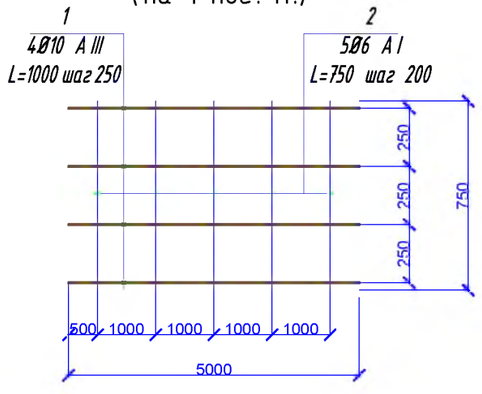

Сетка Сф-2 (на 1 пог.м.)

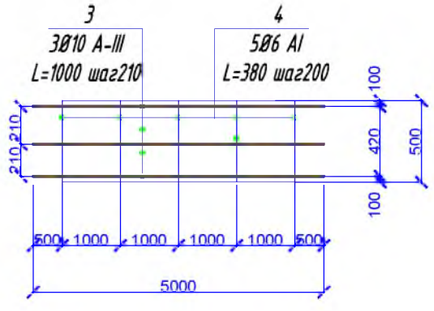


Согласовано

Инв. подл | Подпись и дата | Взамен инв.


АС

Изм.	Кол.уч	Лист	№ док	Поди	Дата	Восстановление насосной станции "Лохур-0" Архитектурно-строительная часть Дежурное помещение. Разрезы 3-3 и 4-4. Спецификация	Лист 10


ФРАГМЕНТ АРМИРОВАНИЕ ПЕРЕМЫЧЕК ПРМ - 2. (1шт)

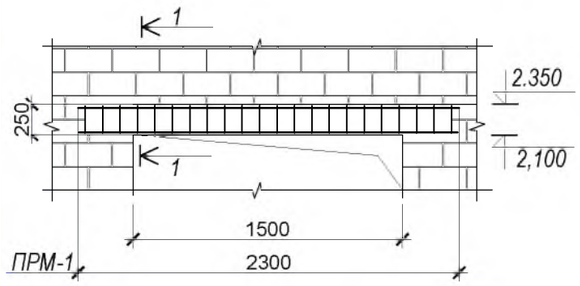


ФРАГМЕНТ АРМИРОВАНИЕ ПЕРЕМЫЧЕК ПРМ - 2. (3шт)

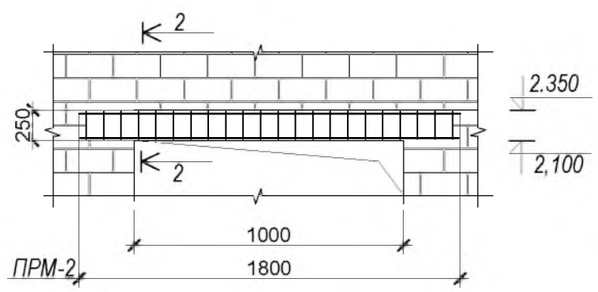


ПРМ - 1 (1-1)

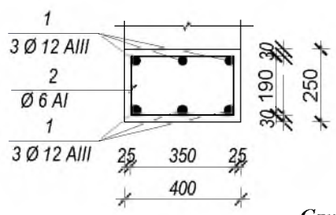

ПРМ - 2 (2-2)

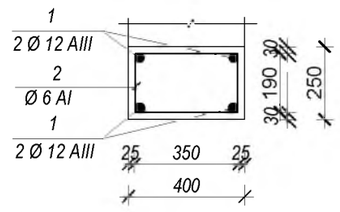

Слуховое окно

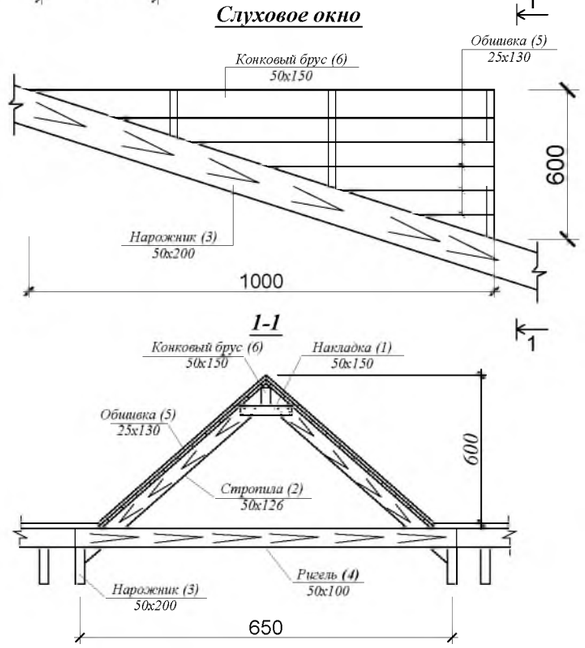

ПРИМЕЧАНИЕ

1. Для повешения плотности бетона он должен подвергаться уплотнит с помощью вибратором
2. Бетонирование сердечник и балок должен выполнить непрерывно
3. Арматуры вязать вязальной проволокой во всех пересечениях
4. Сварные соединения стержней по длине выполнить с разбежкой не менее 1 м.
5. Данный лист рассматривать совместно с листом КЖ

СПЕЦИФИКАЦИЯ РАСХОД МАТЕРИАЛОВ ПЕРЕМЫЧЕК

Марка поз.	Обозначение	Наименование		Кол	Масса ед., кг	
		Перемычек монолитная Прм-1		2		шт.
Прм - 1		Прм-1 (на 1 шт.)				
1		Ø 12 A III	L= 2300	6	0,888	12,25
2		Ø 6 A I	L= 1080	12	0,222	2,90
		Бетон кл. В - 15			0,23	м³
		Перемычек монолитная Прм-2		1		шт.
Прм - 2		Прм-2 (на 1 шт.)				
1		Ø 12 A III	L= 1800	4	0,888	6,40
2		Ø 6 A I	L= 1080	9	0,222	2,16
		Бетон кл. В - 15			0,18	м³

Спецификация слуховых окон

№ п/п	Наименование	Сечение мм х мм	Колич. шт.	Длина в м.		Объём м³	Примеч.
				на один	всего		
		Расход на 1 слуховое окно			2шт		
1	Накладка	50x150	1	0.30	0.30	0.002	
2	Стропила	50x126	--	--	-	-	
3	Нарожник	50x200	2	1,3	2,6	0,026	
4	Ригель	50x100	1	0,8	0,8	0,004	
5	Обшивка	25x130	--	--	10,0	0,032	
6	Коньковый брус	50x150	1	1,2	1,2	0,036	

АС

Изм.	Кол. уч	Лист	№ док.	Подп.	Дата	Восстановление насосной станции "Лохур-0" Архитектурно-строительная часть Дежурное помещение. Перемычки ПРМ-1 и 2. Спецификация расход материалов ОП-1.	Лист 11