АГЕНТСТВО ПО МЕЛИОРАЦИИ И ИРРИГАЦИИ
ПРИ ПРАВИТЕЛЬСТВЕ РЕСПУБЛИКИ ТАДЖИКИСТАН

ГУП "ПРОЕКТНЫЙ ИНСТИТУТ
"ТАДЖИКГИПРОВОДХОЗ"

РАБОЧИЙ ПРОЕКТ

"Баркарорсозии пойгоххои обкашии Лохур-0,Лохур-1,Лохур-2 ва Лохур-3 дар нохияи Рудаки"

АЛЬБОМ-1

Насосной станции Лохур-0.
Технологическая часть (ТХ)

ДУШАНБЕ-2026

АГЕНТСТВО ПО МЕЛИОРАЦИИ И ИРРИГАЦИИ
ПРИ ПРАВИТЕЛЬСТВЕ РЕСПУБЛИКИ ТАДЖИКИСТАН

ГУП "ПРОЕКТНЫЙ ИНСТИТУТ
"ТАДЖИКГИПРОВОДХОЗ"

РАБОЧИЙ ПРОЕКТ

"Баркарорсозии пойгоххои обкашии Лохур-0,Лохур-1,Лохур-2 ва Лохур-3 дар нохияи Рудаки"

АЛЬБОМ-1

Насосной станции Лохур-0.
Технологическая часть (ТХ)

ГЛ. ИНЖЕНЕР ИНСТИТУТА: ХАЙБАРОВ С.

ГЛ. ИНЖЕНЕР ПРОЕКТА: ШОМИЛИ У.

ДУШАНБЕ-2026

Таб. 1

Ведомость основных комплектов рабочих чертежей		
Обозначение	**Наименование**	**Примечание**
1	2	3
.ПЗ	Пояснительная записка	Книга-1
ТГИ	Инженерно-топогеодезический изысканий	Книга-2
ИГИ	Инженерно-геологический и гидрогеологичекий изысканий	Книга-3
ТХ	**Насосной станции Лохур-0.** Технологическая часть	Альбом-1
ГР	**Насосной станции Лохур-0.** Гидротехническое решение	Альбом-2
АС	**Насосной станции Лохур-0. Архитектурно-строительная часть**	Альбом-3
АС	**Насосной станции Лохур-0. Дежурное помещение Архитектурно-строительная часть**	Альбом-4
АС	**Насосной станции Лохур-0. Уборная на 1-го очко Архитектурно-строительная часть**	Альбом-5
ЭО	Электротехническая часть	Альбом-6
СМ	Сметная документация	Книга-4

Таб. 2

Ведомость рабочих чертежей основного комплекта **ТХ**		
Лист	**Наименование**	**Примечание**
1	2	3
1	Общие данные	
2	План площадка насосной станции М1:500. Экспликация и ведомость объёмов работ.	
3	План размещение гидромеханического оборудование насосной станции М1:100.	
4	План размещение гидромеханического оборудование насосной станции М1:100.	
5	Продольный профиль напорного трубопровода с ПК0+00 по ПК0+90.Ведомость объёмов работ.	
6	Характиристика насоса Д2000-21 (16НДн)	
7	Монтажный чертеж насоса Д2000-21 (16НДн)	
8	Фундамент под агрегат.Ведомость объёмов работ	
9	Установочный чертёж вакуум-насоса ВВН1-6. Спецификация	
10	Разводка трубопроводов вакуум-системы. Спецификация	
11	Установочный чертёж дренажного-насоса. Спецификация	
12	Спецификация оборудования и материалов	

Настоящий проект выполнен в соответствии с дествующими нормами и правилами, в том числе по взрыво - пожарной безопасности.

Гл. инженер проекта Шомили У.

Таб.3

Ведомость ссылочных и прилагаемых документов		
Обозначение	Наименование	Примечание
	Ссылочные документы	
ГОСТ 10704-91	Трубы металлические	
ГОСТ 9466-75	Электроды для дуговой сварки сталей и наплавки	
	классификация и общие технические условия	
ГОСТ 19903-74	Лист стальная	
30ч906бр	Задвижки с электроприводом	
ГОСТ 8509-93	Уголки стальные горячекатаные равнопрочные	
	Прилагаемые документы	
ТХ.СО-1	Спецификация основного оборудования насосной станции	2-листов

						ТХ
						"Баркарорсозии пойгоххои обкашии Лохур-0,Лохур-1,Лохур-2 ва Лохур-3 дар нохияи Рудаки"
Изм.	Кол.уч.	Лист	№ док.	Подп.	Дата	
Разработ.			**Фрайдунпоев О.**			Насосной станции Лохур-0. Технологическая часть (ТХ).
ГИП			Шомили У.			
Нач. отдел			Шомили У.			Общие данные.
Норм. контр.			Хайбаров С.			

Стадия	Лист	Листов
РП	1	12

ГУП "Проектный Институт "Точикгипроводхоз" Душанбе - 2026


Согласовано

Взамен инв.

Подпись и дата

Инв. подл

План площадка насосной станции Лохур-0 I-го подъема
М1:500

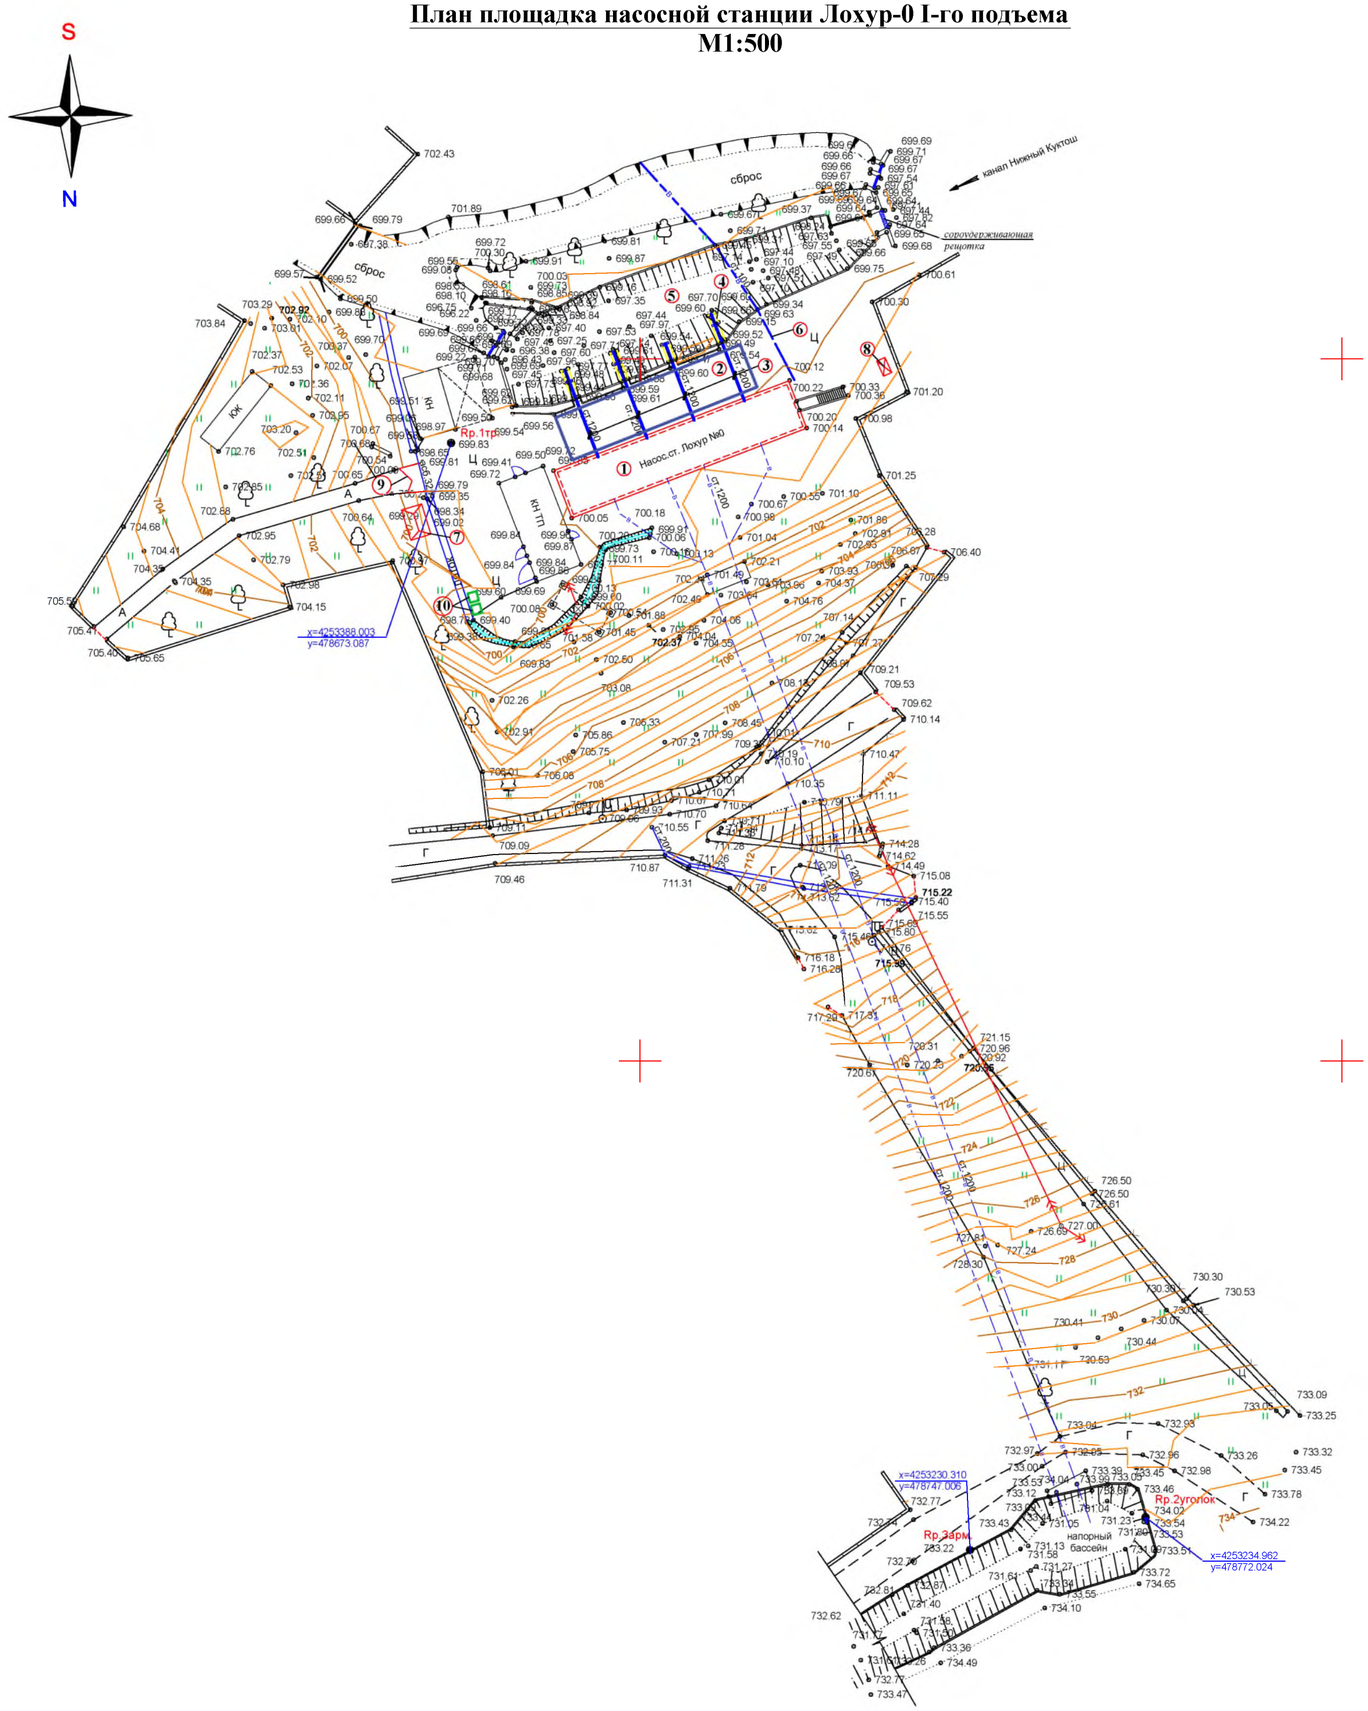

Экспликация здании и сооружении

№ п/п	Наименование	Ед. измер.	Кол-во	Примечание
1	**Здание насосной станции** раз:7,0х36,0м	шт	1,0	**Существующий подлежит снос**
2	**Здание насосной станции** раз:6,5х30,0м	шт	1,0	**Проектируемый**
3	Всасывающий трубопровод Ø=1200мм, (4-нитки)	пм	53,0	Существующий подлежит замена
4	**Служебная площадка раз:1,3х4,40м**	шт	4,0	Существующий подлежит восстановление
5	**Аванкамера раз: 7,0х58,0м**	шт	1,0	Существующий подлежит восстановление
6	Сбросной труба РТН Ø=1000мм	пм	55,0	Существующий сохраняется
7	Дежурное помещение раз : 3,5 х 4,0м	шт	1,0	Проектируемый
8	**Уборная на 1-о очко раз:1,30х2.35х3.0м**	шт	1,0	Проектируемый
9	Мусорный контейнер	шт	2,0	Проектируемый
10	**Металлическая ворота В=4,0м,Н=2,0м**	шт	1,0	Проектируемый

Ведомость объёмов работ

№ п/п	Наименование	Ед. изм	кол-во	Примечание
1	Разборка и восстановление внутри-площадочный асфальтобетонная покрытия t=10,0см (Вср=12м) с учетом площадка НС	м²	3384,0	Lоб=282,0м
2	**Устройства основания автодорога из гравийно песчаной смеси t=10см** - щебня t=5см	м² м²	3384,0	
3	Асфалтобетонная покрытия крупнозернистый t=6,0см мелкозернистый t=4,0см	м² м²	3384,0	
4	Установка **сетчатое ограждение территории В=2,0м, Н=2,0м**	пм/ шт	251/ 126	см. лист.
5	Приобретение и установка металлические ворота раз:4,0х2,0м	шт	1	см. лист.
6	Установка мусорного контейнера раз:3х2м	шт	2	Рыночное
7	Устройство здание дежурное помещение раз:3,0х4,5м	шт	1	см.лист-
8	Устройство здание уборное раз:1,3х1,8м	шт	1	см.лист-

УСЛОВНЫЕ ОБОЗНАЧЕНИЯ

- Напорный и всасывающий трубопровод
- Сбросной труба
- Сетчатое ограждение
- А - Внутри площадочная подъездная асфальтная дорога

Согласовано


Взамен инв.

Подпись и дата

Инв. подл.

							ТХ
							"Баркарорсозии пойгоххои обкашии Лохур-0,Лохур-1,Лохур-2 ва Лохур-3 дар нохияи Рудаки"
Изм.	Кол.уч.	Лист	№ док.	Подп.	Дата		
Разработ.		Фрайдунзода О.				Насосной станции Лохур-0. Технологическая часть (ТХ).	Стадия: РП; Лист: 2; Листов: 12
ГИП		Шомили У.					
Нач. отдел		Шомили У.				План площадка насосной станции М1:500. Экспликация и ведомость объёмов работ.	ГУП "Проектный Институт "Точикгипроводхоз" Душанбе - 2026
Норм. контр.		Хайбаров С.					

Существующие положение план размещение гидромеханического оборудование насосной станции Ляхур-0.
М1:100.

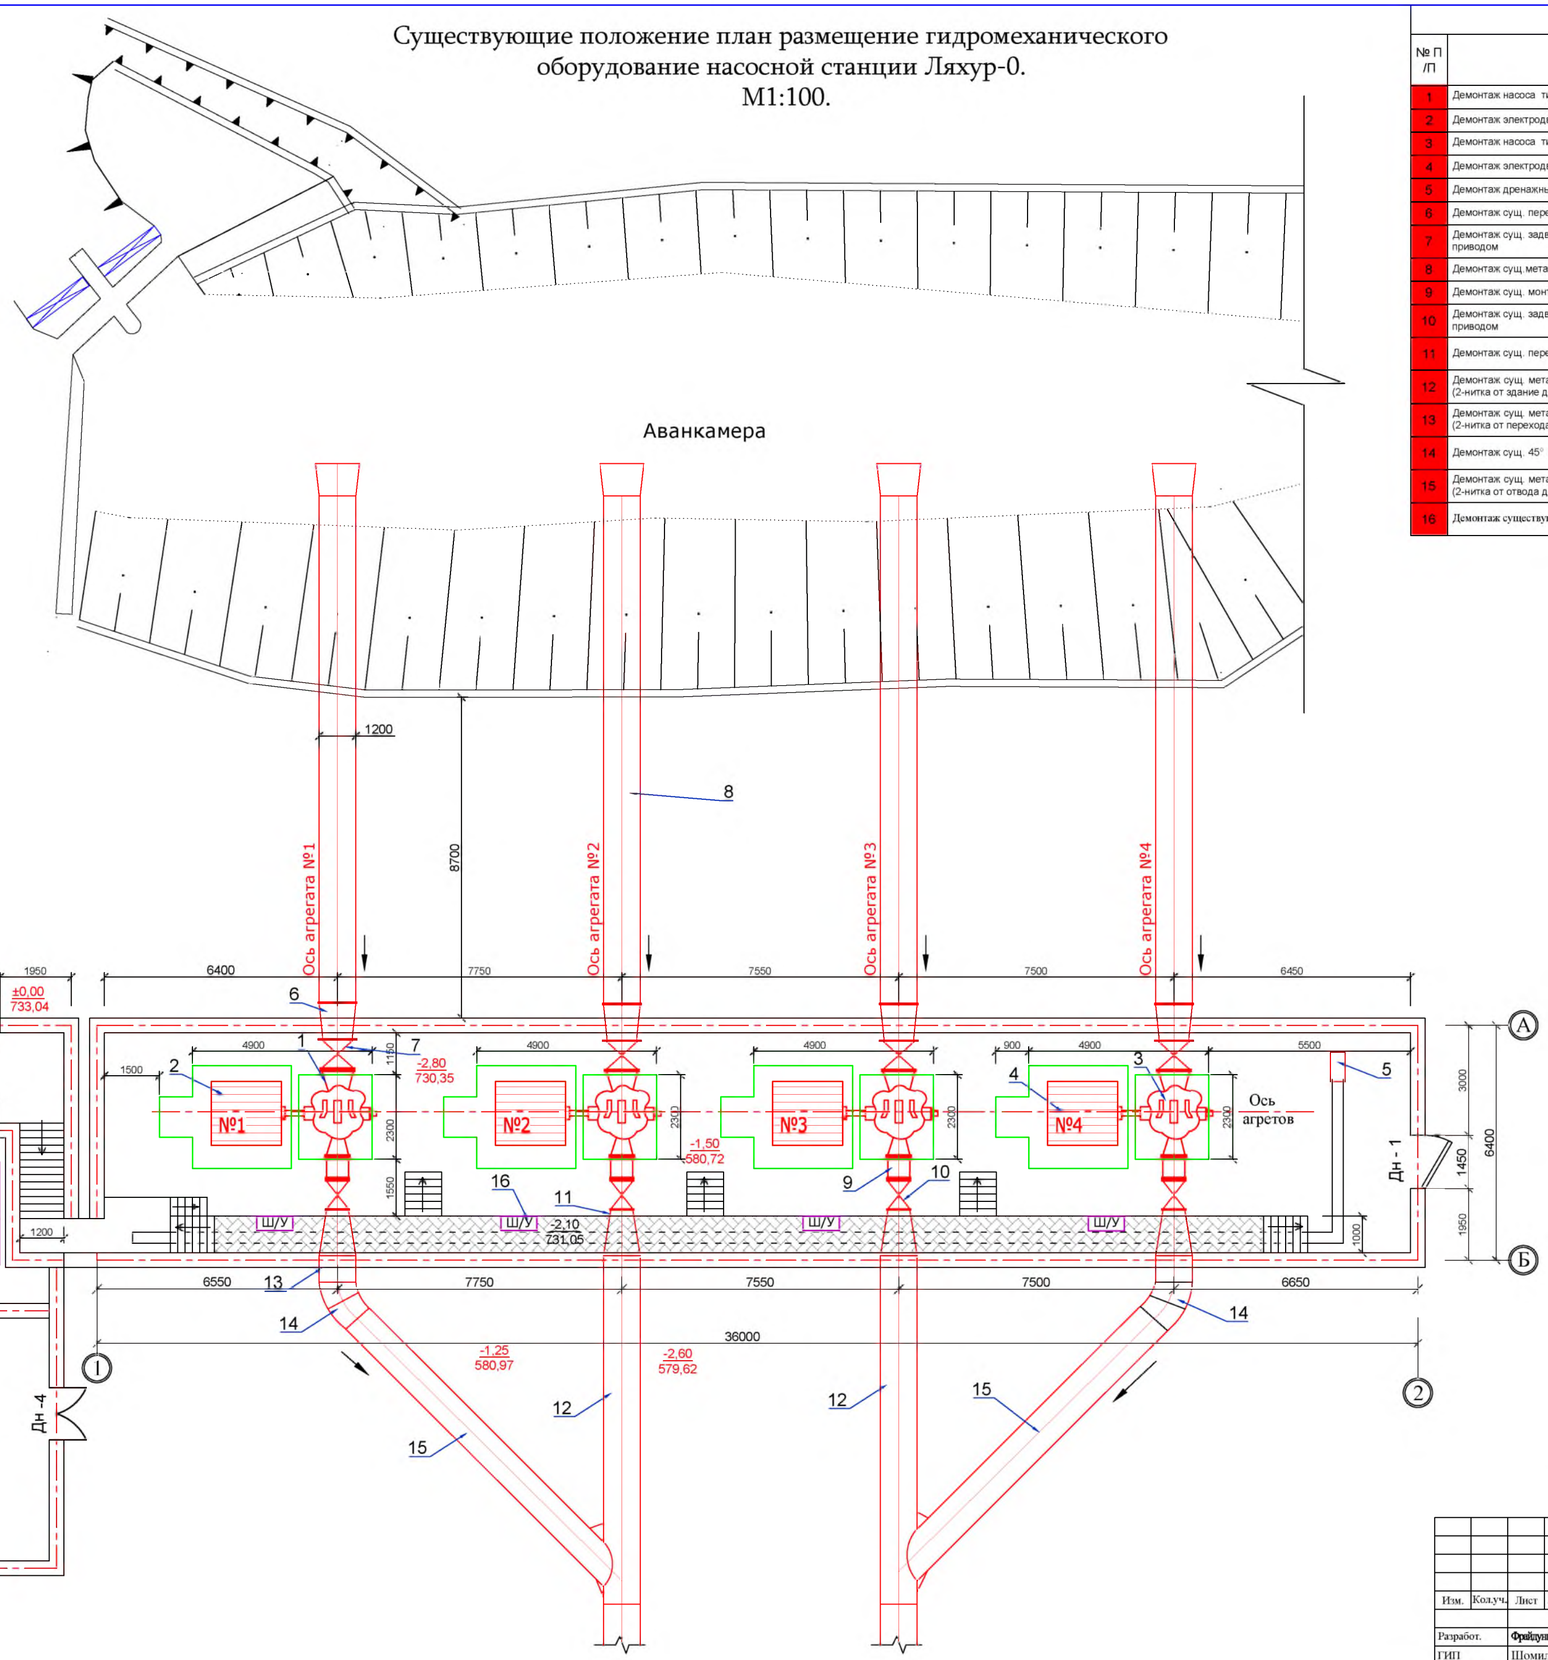

Ведомость объёмов демонтажных работ

№ П /П	Наименование	Ед. изм	Масса оборудования, кг	Примечание
1	Демонтаж насоса типа Д6300-80 (24НДс) 3- шт	кг	26298,0	Агрегат №1,2,3
2	Демонтаж электродвигатель мощность N=1000кВт 3-шт	кг	19500,0	Агрегат №1; №2 и №3
3	Демонтаж насоса типа Д4000-95 (22НДс) 1- шт	кг	4960,0	Агрегат №4
4	Демонтаж электродвигатель мощность N=1000кВт 1-шт	кг	3350,0	Агрегат №4
5	Демонтаж дренажный насос	шт	1,0	
6	Демонтаж сущ. переход косой Ø=800х1200мм, Ру=1,0МПа	шт	4,0	всасывающая линия
7	Демонтаж сущ. задвижка фланцевая Ø=400мм, Ру=1,0МПа с электро-приводом	шт	4,0	всасывающая линия
8	Демонтаж сущ.металлическая труба Ø=1200мм, 4-нитки	пм	53,0	всасывающая линия
9	Демонтаж сущ. монтажная вставка Ø=500мм	шт	4,0	Напорная линия
10	Демонтаж сущ. задвижка фланцевая Ø=500мм, Ру=1,0МПа с электро-приводом	шт	4,0	Напорная линия
11	Демонтаж сущ. переход концентрические Ø=500х1200мм, Ру=1,0МПа	шт	4,0	Напорная линия
12	Демонтаж сущ. металлический напорный трубопровод Øу=1200мм, (2-нитка от здание до точка соединение)	пм	19,0	
13	Демонтаж сущ. металлический напорный трубопровод Øу=1200мм, (2-нитка от перехода до отвода)	пм	2,60	
14	Демонтаж сущ. 45° Ø=1200мм, Ру=1,0МПа	шт	2,0	Напорная линия
15	Демонтаж сущ. металлический напорный трубопровод Øу=1200мм, (2-нитка от отвода до точка соединение)	пм	26,0	
16	Демонтаж существующий электрические щиты	шт	4,0	

Примечание


1. Данный лист рассматривать совместно с листом- 3,4,5 и ТХ.СО

ТХ

Изм.	Колуч.	Лист	№ док.	Подп.	Дата	ТХ		
						"Баркарорсозии пойгоххои обкашии Лохур-0,Лохур-1,Лохур-2 ва Лохур-3 дар нохияи Рудаки"		
Разработ.		Файзуллоева О.				Насосной станции Лохур-0. Технологическая часть (ТХ).	Стадия	Лист	Листов
ГИП		Шомили У.					РП	3	12
Нач. отдел		Шомили У.				План размещение гидромеханического оборудование насосной станции М1:100.	ГУП "Проектный Институт "Точикгипроводхоз" Душанбе - 2026		
Норм. контр.		Хайбаров С.							

Согласовано

Инв. подл | Подпись и дата | Взамен инв.

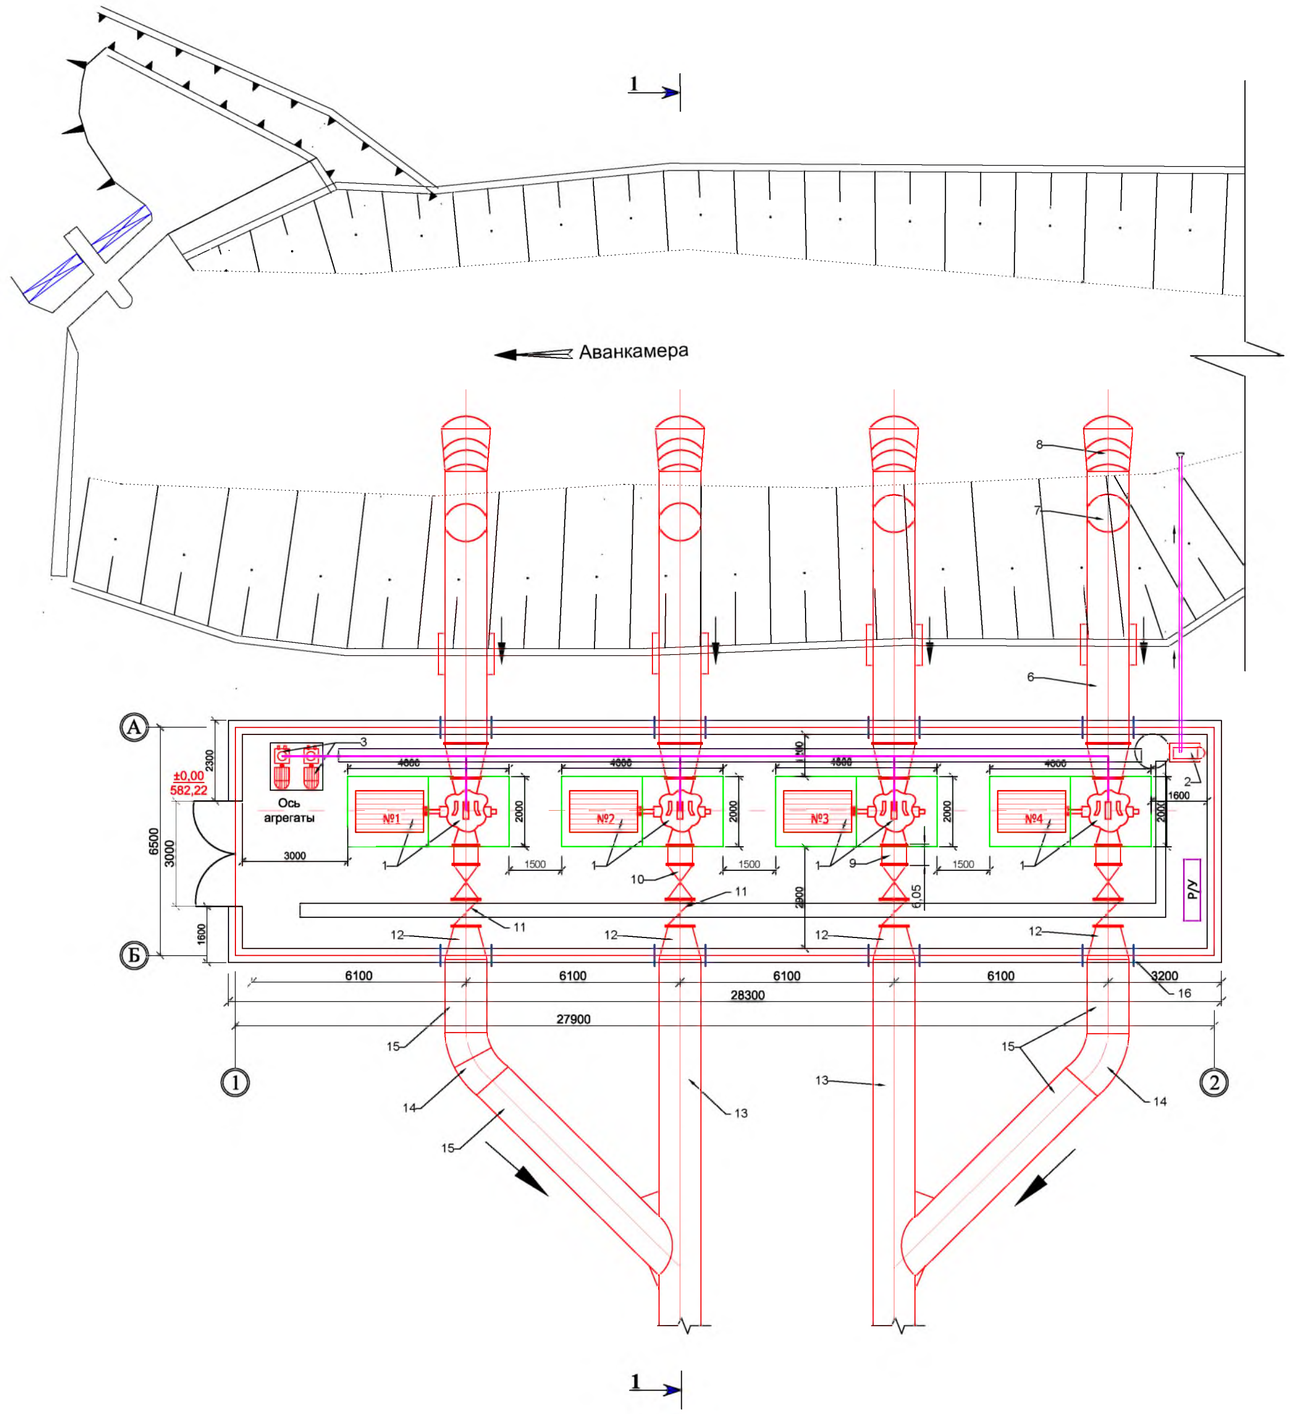

Примечание


1. Данный лист рассматривать совместно с листом- 3,4,5 и ТХ.СО

ТХ

						ТХ	
						"Баркарорсозии пойгоххои обкашии Лохур-0,Лохур-1,Лохур-2 ва Лохур-3 дар нохияи Рудаки"	
Изм.	Колуч.	Лист	№ док.	Подп.	Дата		
Разработ.		Фейдуллоев О.				Насосной станции Лохур-0. Технологическая часть (ТХ).	Стадия: РП; Лист: 4; Листов: 12
ГИП		Шомили У.					
Нач. отдел		Шомили У.					
Норм. контр.		Хайбаров С.				План размещение гидромеханического оборудование насосной станции М1:100.	ГУП "Проектный Институт "Точикгипроводхоз" Душанбе - 2026

Согласовано

Инв. подл | Подпись и дата | Взамен инв.

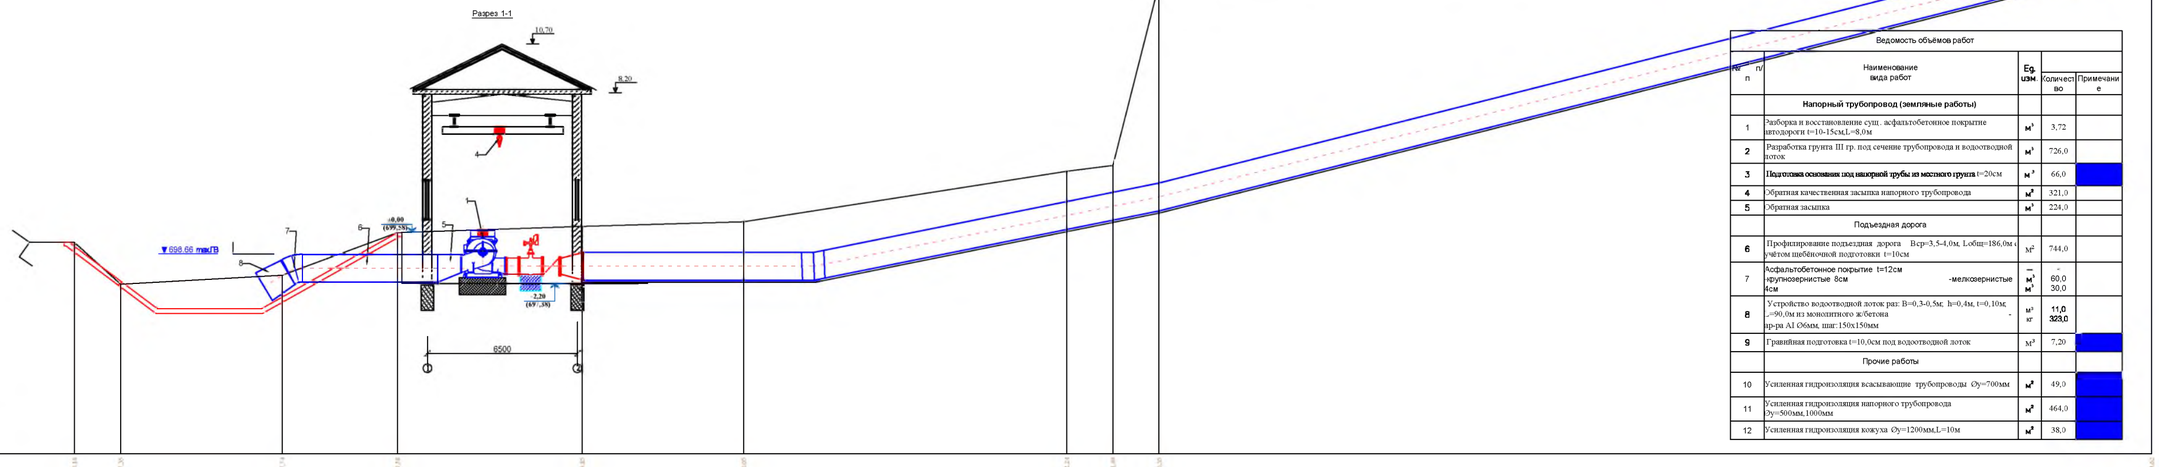


Масштаб:
верт. 1:100
гор. 1:100

Ведомость объёмов работ

№ п/п	Наименование вида работ	Ед. изм.	Количество	Примечание
	Напорный трубопровод (земляные работы)			
1	Разборка и восстановление сущ. асфальтобетонное покрытие автодороги t=10-15см,L=8,0м	м³	3,72	
2	Разработка грунта III гр. под сечение трубопровода и водоотводной лоток	м³	726,0	
3	**Подготовка основания под напорной трубы из местного грунта** t=20см	м²	66,0	
4	Обратная качественная засыпка напорного трубопровода	м³	321,0	
5	Обратная засыпка	м³	224,0	
	Подъездная дорога			
6	Профилирование подъездная дорога Bср=3,5-4,0м, Lобщ=186,0м с учётом щебёночной подготовки t=10см	м²	744,0	
7	Асфальтобетонное покрытие t=12см -крупнозернистые 8см -мелкозернистые 4см	— м² м²	- 60,0 30,0	
8	Устройство водоотводной лоток раз: B=0,3-0,5м; h=0,4м, t=0,10м, L=90,0м из монолитного ж/бетона -нр-ра AI Ø6мм, шаг:150х150мм	м³ кг	**11,0** **323,0**	
9	Гравийная подготовка t=10,0см под водоотводной лоток	м²	7,20	
	Прочие работы			
10	Усиленная гидроизоляция всасывающие трубопроводы Øу=700мм	м²	49,0	
11	Усиленная гидроизоляция напорного трубопровода Øу=500мм,1000мм	м²	464,0	
12	Усиленная гидроизоляция кожуха Øу=1200мм,L=10м	м²	38,0	

| | | |

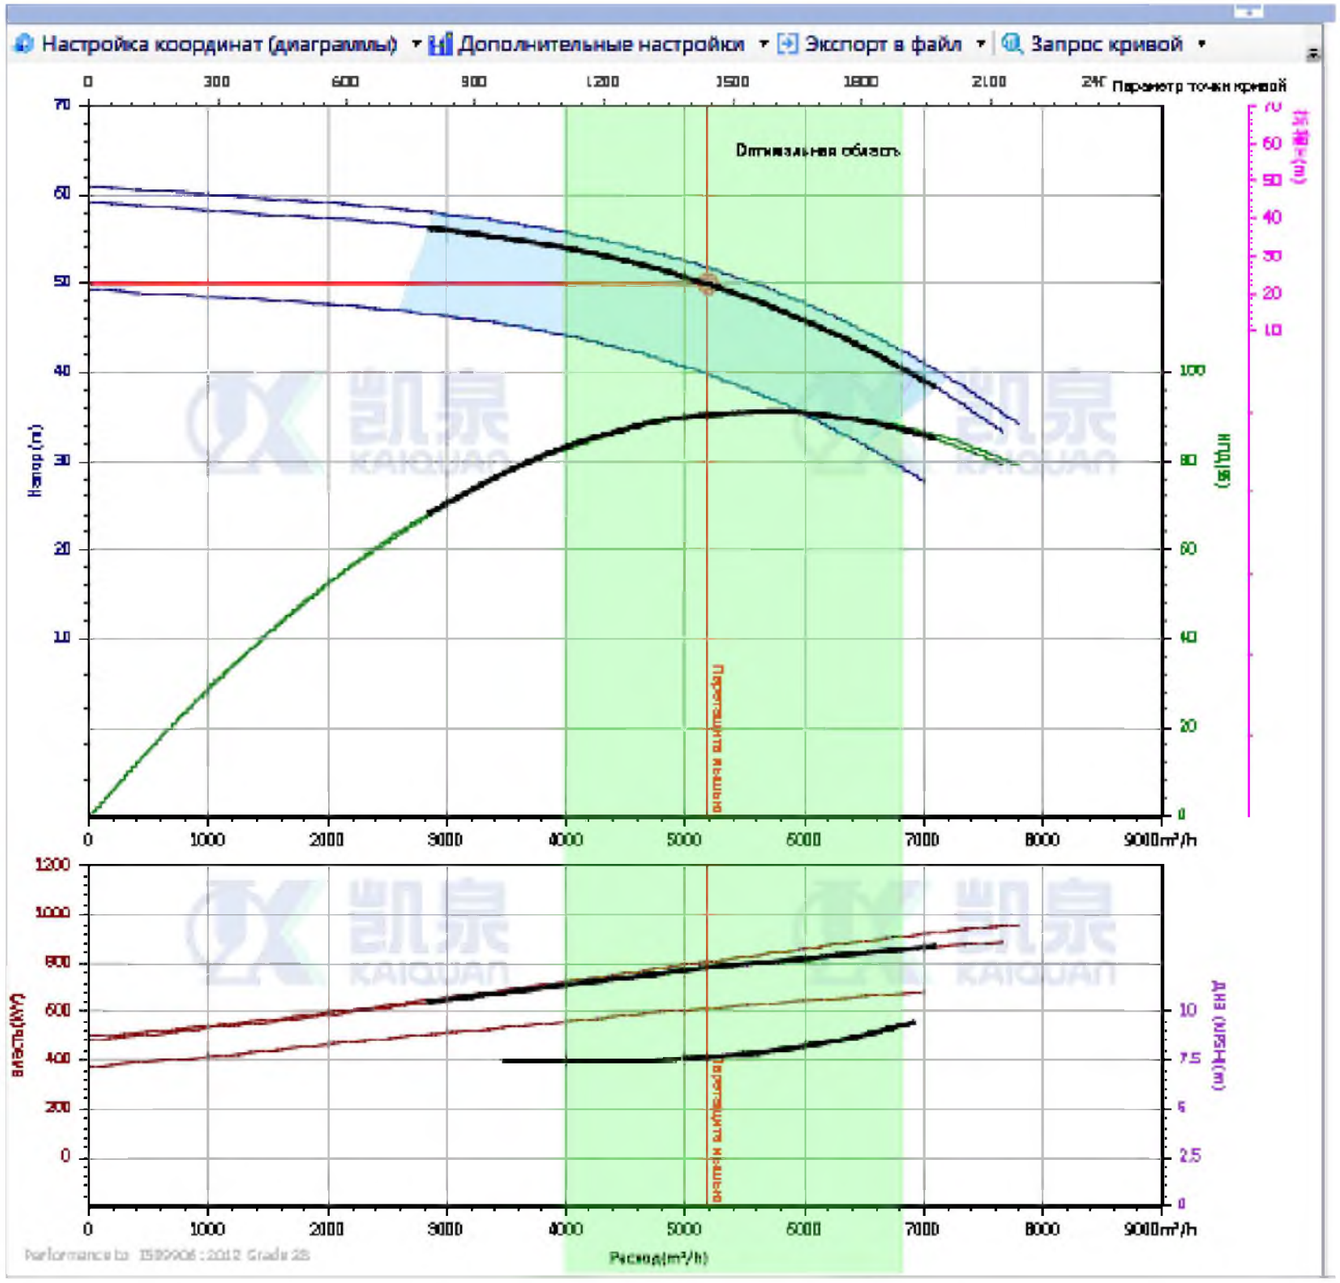

TX

						TX
						"Баркарорсозии пойгоххои обкашии Лохур-0,Лохур-1,Лохур-2 ва Лохур-3 дар нохияи Рудаки"
Изм.	Кол.уч.	Лист	№ док.	Подп.	Дата	
Разработ.		Фрайдуншоев О.				Насосной станции Лохур-0. Технологическая часть (ТХ).
ГИП		Шомили У.				
Нач. отдел		Шомили У.				Характиристика насоса Д2000-21 (16НДн)
Норм. контр.		Хайбаров С.				

Стадия	Лист	Листов
РП	6	12


ГУП "Проектный Институт "Точикгипроводхоз" Душанбе - 2026

Взамен инв.


Подпись и дата

Инв. подл


Общий вид агрегата

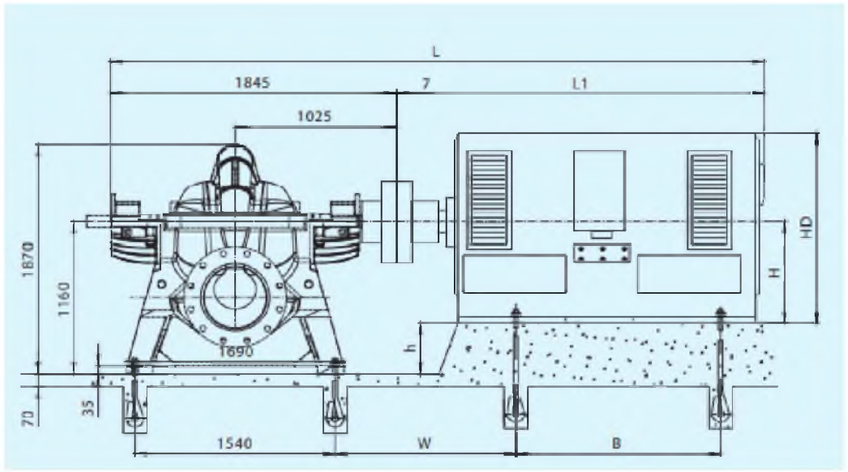

План рама агрегата

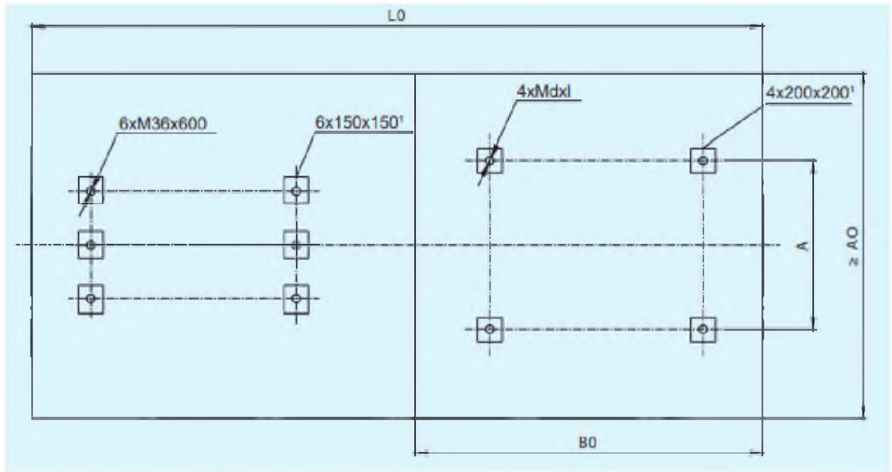


Вид с боку

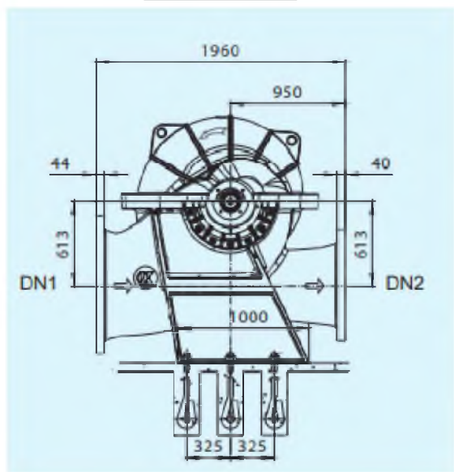


Типоразмер насоса	Диаметр рабочего колеса, мм	Подача (Q)		Напор (H), м	Частота вращения, об/мин	Мощность, кВт		Эффек-тивность (η), %	NPSHr, м	Масса, кг
		м³/ч	л/с			на валу насоса	электро-двигателя (P)			
KQSN800-M17S	600	3323	1538	51	990	550,6	900	84	7,8	3846
		5538	1846	45		748,2		91		
		6646	885	34		700, 7		88		

Типоразмер насоса	Электродвигатель				Габаритные размеры, мм												Масса, кг
	Модель	Напряж., В	Степень защиты	Мощность, кВт	L	L1	L0	A0	B0	W	A	B	h	H	HD	dxl	Эл. двиг.
KQSN800-M17S	YKK560-6	6k	IP54/IP44	900-1000	4612	2760	4800	2000	2400	1025	1000	1400	600	560	2200	M36X600	7850

Размеры фланцевого присоединения стороны всасывания DN1

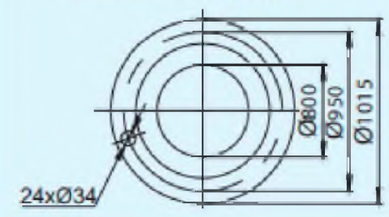

Размеры фланцевого присоединения стороны нагнетания DN2

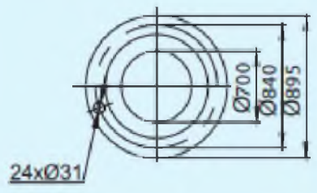

Примечание

1. Данный лист рассматривать совместно с листом- 2,3,6 и ТХ.СО

ТХ


Изм.	Кол.уч.	Лист	№ док.	Подп.	Дата	ТХ		
						"Баркарорсозии пойгоххои обкашии Лохур-0,Лохур-1,Лохур-2 ва Лохур-3 дар нохияи Рудаки"		
Разработ.		Фрайдуншоев О.				Насосной станции Лохур-0. Технологическая часть (ТХ).	Стадия	Лист	Листов
ГИП		Шомили У.					РП	7	12
Нач. отдел		Шомили У.				Монтажный чертеж насоса Д2000-21 (16НДн)	ГУП "Проектный Институт "Точикгипроводхоз" Душанбе - 2026		
Норм. контр.		Хайбаров С.							

Взамен инв.


Подпись и дата

Инв. подл

План фундамента (б/м)

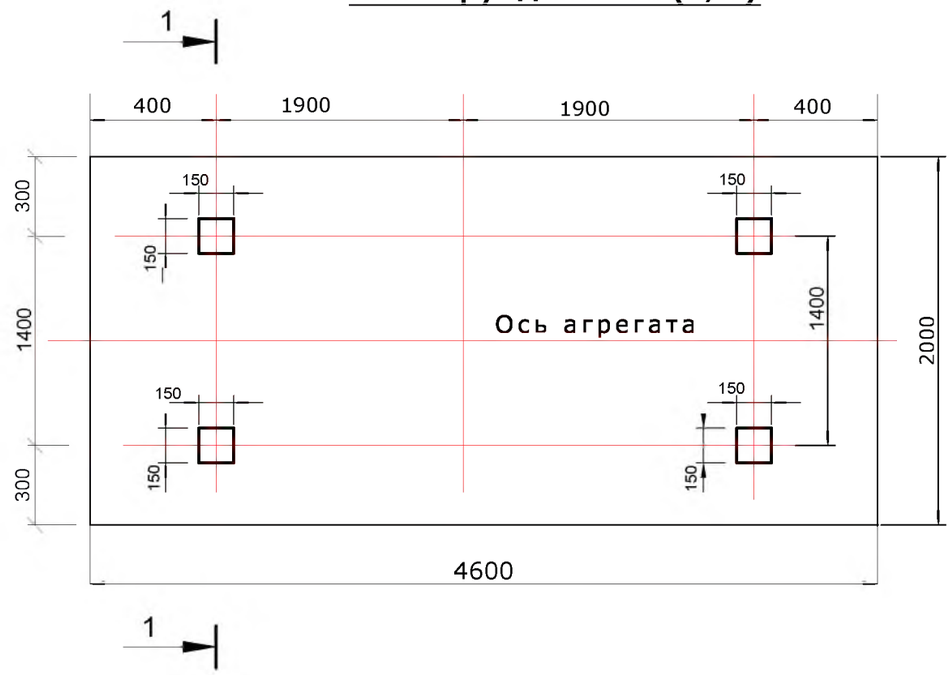

Разрез 1-1 (б/м)

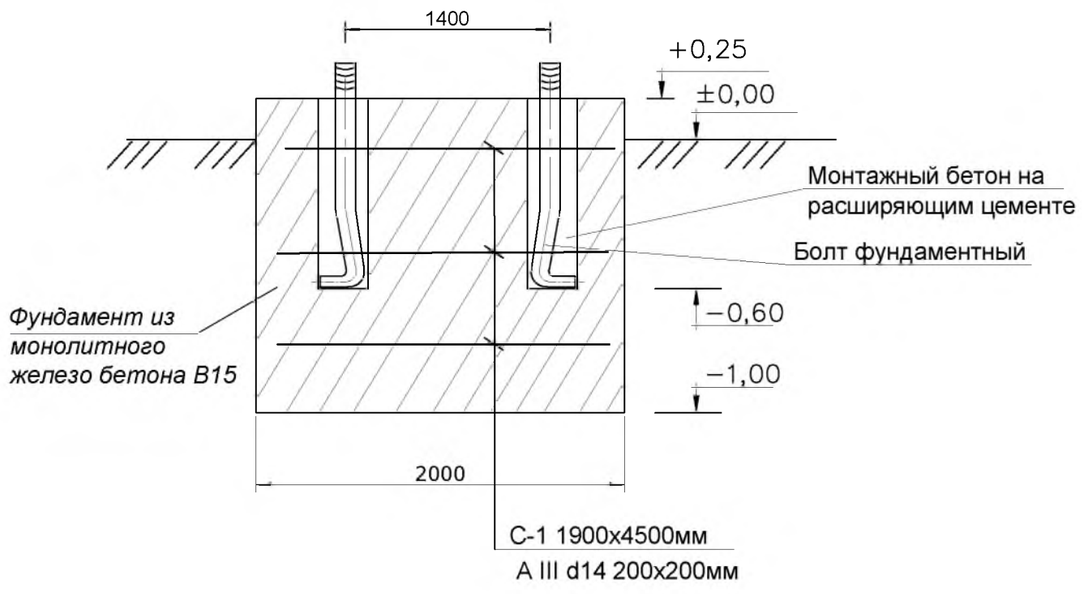

Ведомость объёмов работ дано на 1-го фундамента

N п/п	Наименование работ.	Ед изм	Кол-во	Примечание
1	Монолитный бетон В15 - F150 -W 6	м³	11,50	На 1 фундамент
2	Монтажный бетон на расширяющемся цементе	м³	0,10	На 1 фундамент
3	Болт фундаментный М30х600. ГОСТ 24379.1-80 шт.6	кг	27,30	На 1 фундамент
4	Гайка Ø30 ГОСТ 5927-80* шт. 4	кг	1,34	На 1 агрегат
5	Шайба Ø30 ГОСТ 24379.1-80 шт.4	кг	1,98	На 1 агрегат
6	Сетка С-1 раз:1900х2500 ячейки 200/200 из Арм-а AIII Ø14мм ГОСТ5781-82 3-шт (1-шт=111,32кг)	кг	334,0	На 1 агрегат
7	Шайба Ø30 ГОСТ 24379.1-80 шт.4	кг	9,50	На 1 агрегат

Всего - 4 шт

Примечание

1. Данный лист рассматривать совместно с листом ТХ-3,4,5
2. Местоположение отверстий под анкерные болты уточняются по полученному оборудованию
3. Анкерные болты необходимо прикрепить с арматурной сетки фундамента

ТХ


						ТХ
						"Баркарорсозии пойгоххои обкашии Лохур-0,Лохур-1,Лохур-2 ва Лохур-3 дар нохияи Рудаки"
Изм.	Кол.уч.	Лист	№ док.	Подп.	Дата	
Разработ.		Фрайдунпоев О.				Насосной станции Лохур-0. Технологическая часть (ТХ).
ГИП		Шомили У.				
Нач. отдел		Шомили У.				Фундамент под агрегат. Ведомость объёмов работ
Норм. контр.		Хайбаров С.				

Стадия	Лист	Листов
РП	8	12


ГУП "Проектный Институт "Точикгипроводхоз" Душанбе - 2026

Взамен инв. | Подпись и дата | Инв. подл


Сечение 1-1

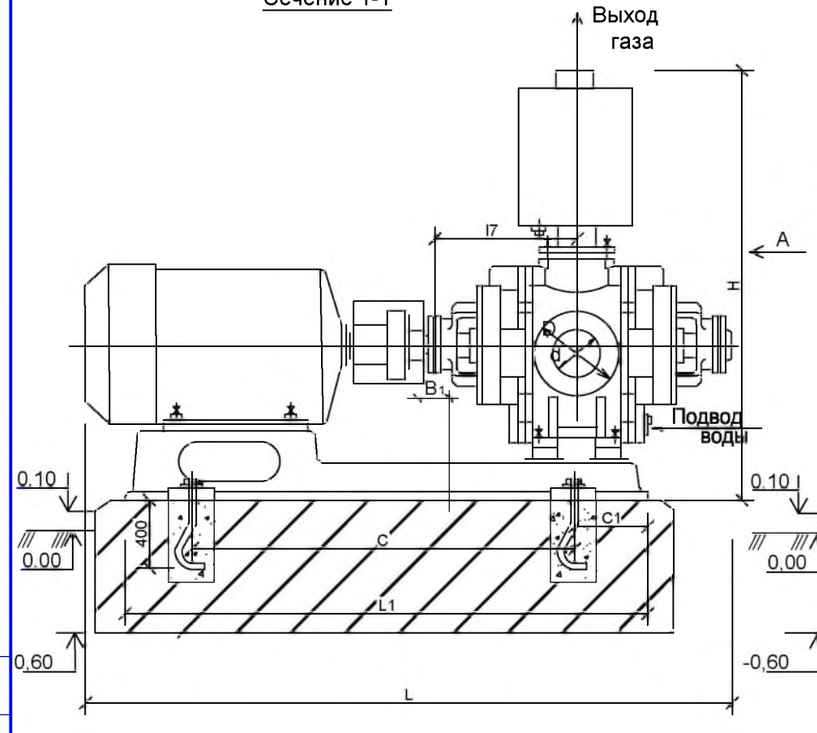

Вид по А

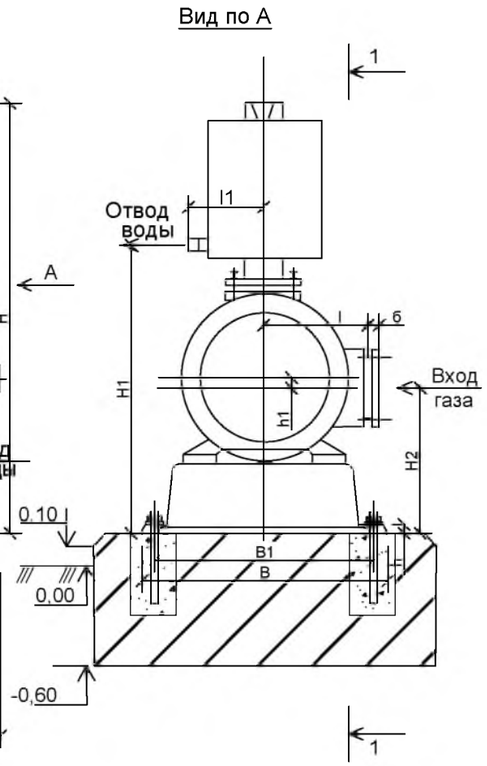

План фундамента на 2 агрегата

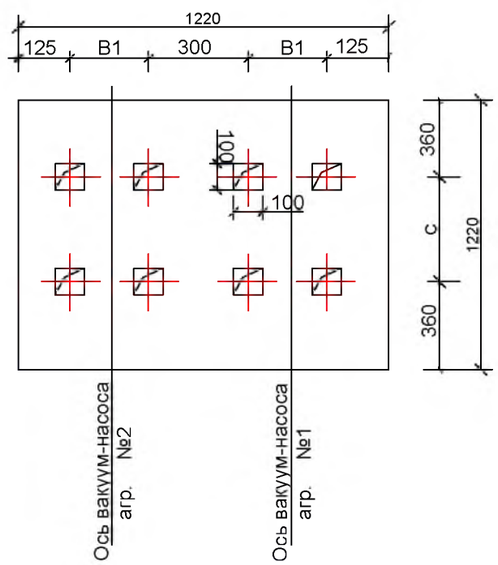

Спецификация

№№	Обозначение	Наименование	Кол-во	Масса ед.кг	Примечание
3		Фундамент бетонный	1		
4		Детали			
5	ГОСТ 5915-70	Гайка М12 кл2-011	8	0,0154	0,1232
6	ГОСТ 6402-70	Шайба М12 Л65Г	16	0,00627	0,05
7	ГОСТ 24379,0-80	Болт М12х500Вст3ПС	8	0,52	4,16
		Материалы			
8		Бетон В15 F50 м3	1,10		
9		Монтажный бетон В12.5 м3	0,04		
10		Изоляция боковых поверх-ностей фундамента.			
		Обмазка горячим битумом за 2 раза м2	3,5		

Габаритные и присоединительные размеры (мм)

Марка насоса	L	L_1	B	B_1	H	H_1	H_2	C	C_1	C_2	l	l_1	l_2	l_3	l_4	l_5	l_6	l_7	в	h	h_1	d	d_1	D	D_1	d_2	n
ВВН1-6	1435	1250	590	518	980	680	340	1050	180	82	200	212,5	250	171	145	100	152	390	18	30	15.5	110	G3/4-B	205	170	18	4

масса -590кг

Примечание:

1.Спецификация составлена из условия установки 2-х агрегатов

2.Относительной отметке 0,00 (пол здания) соответствует абсолютная отм.548,56

3.Размещение вакуум- насоса уточняется по полученному оборудованию.

4.Гидроизоляция фундамента -окраска горячим битумом за 2 раза по грунтовке из разжиженного битума

5.Данный лист рассматривать совместно с листами-3 и 9

ТХ

Изм.	Кол.уч.	Лист	№ док.	Поди.	Дата	**ТХ**			
						"Баркарорсозии пойгоххои обкашии Лохур-0,Лохур-1,Лохур-2 ва Лохур-3 дар нохияи Рудаки"			
Разработ.		Фрайдунпоев О.				Насосной станции Лохур-0. Технологическая часть (ТХ).	Стадия	Лист	Листов
							РП	9	12
ГИП		Шомили У.							
Нач. отдел		Шомили У.				Установочный чертёж вакуум-насоса ВВН1-6. Спецификация	ГУП "Проектный Институт "Точикгипроводхоз" Душанбе - 2026		
Норм. контр.		Хайбаров С.							


Согласовано

Взамен инв.

Подпись и дата

Инв. подл


Аксонометрическая схема
разводки вакуум-системы

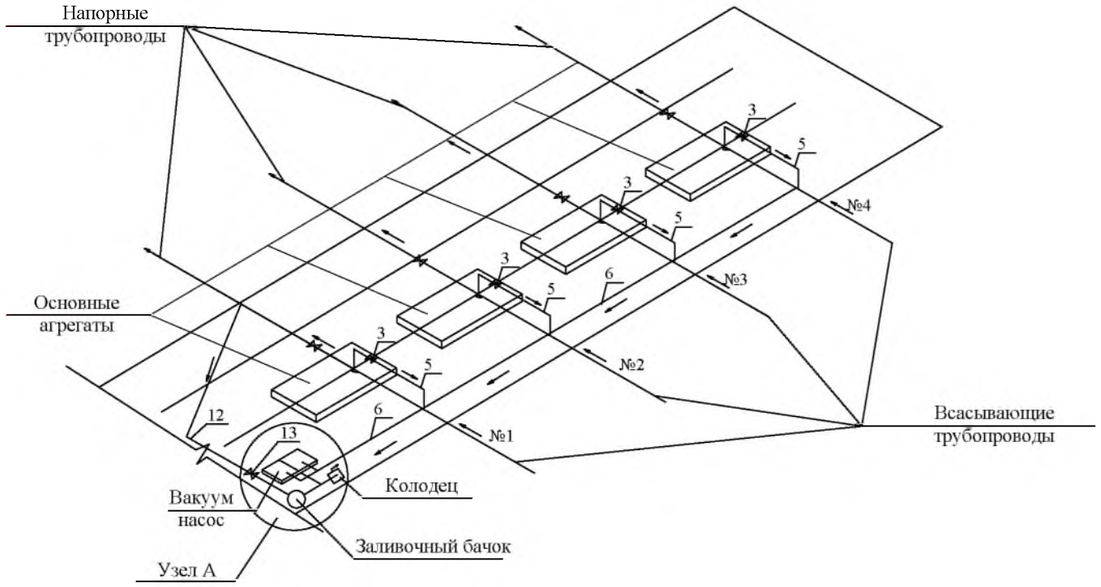


Спецификация

№№	Обозначение	Наименование	Кол-во	Масса ед.кг	Примечание
		Оборудование			
1	15ч8бр	Вентиль Д=70мм Ру=1.0МПа	2	6,8	13,60
2		Обратный клапан Д=80ммРу=1,0МПа	2	10,2	20,4
3	15кч18р	Вентиль Д=25мм Ру=1,0МПа	7	1.40	11,20
13	15кч18р	Вентиль Д=32мм Ру=1,0МПа	1	2,10	2,10
		Материалы и изделия			
4	ГОСТ 8955-75	Муфта D=800мм	4	1,0	4.0
5	ГОСТ3262-75	Труба 25х2,8 L=10000мм	1	25,0	25,0
6	ГОСТ10704-91	Труба 75х3.5 L=44300мм	1	6,26	277,32
7	ГОСТ 17376-2001	Тройник 80х80х3,2 L=172мм	1	2,50	2,50
8	ГОСТ 17375-83	Отвод 80х5,0 а = 90°	2	2,0	4,0
9	ГОСТ 8758-75	Муфта переходная 15х25	4	0,16	0,80
10	ГОСТ 8961-75	Контргайка 25	5	0,01	0,05
11	ТП 820-3-5 ал.3	Заливочный бачок	1	125	125
12	ГОСТ10704-91	Труба 32х3.5 L=8000мм	1	24,0	24,0
14	ГОСТ10704-91	Труба 114х4 L=4000мм	1	43.4	43.4

Вид по 1-1

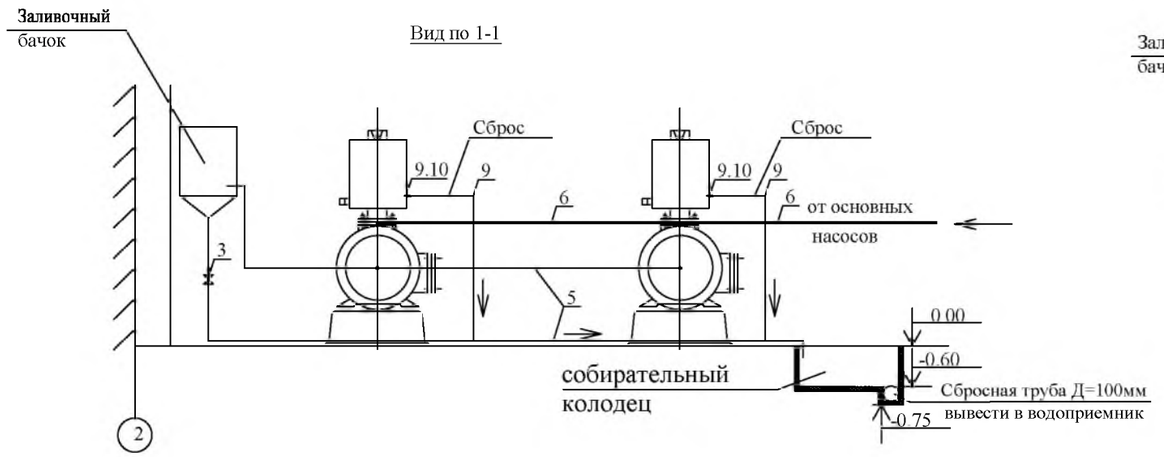

План (Узел А)

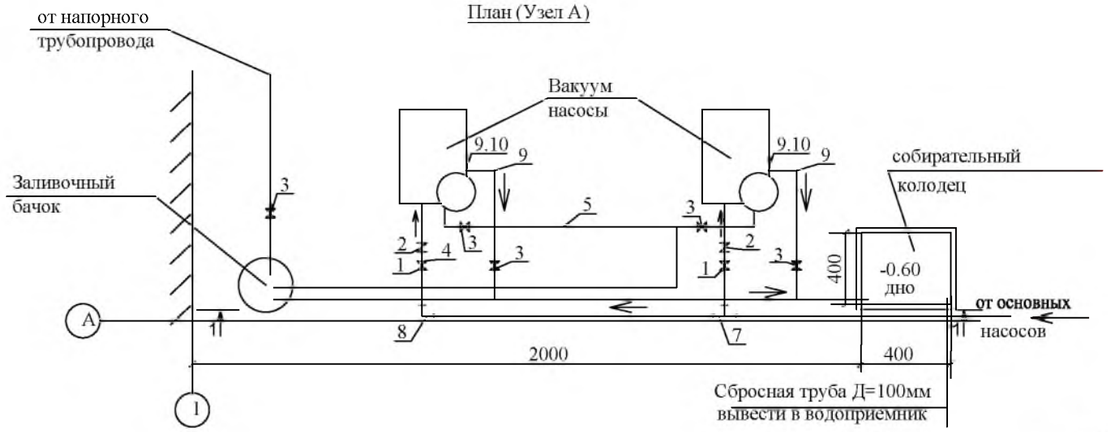

Примечание:
1.При монтаже длины труб уточняются
2.Трубы Ду=25мм гнуть по месту
3.Фундамент под вакуум-насосы ВВН 1-3 см.лист7
4.К собирательному колодцу подключить кабельные каналы для отвода воды из них

ТХ


Изм.	Кол.уч.	Лист	№ док.	Подп.	Дата	"Баркарорсозии пойгоххои обкашии Лохур-0,Лохур-1,Лохур-2 ва Лохур-3 дар нохияи Рудаки"			
Разработ.		Фрайдунзода О.				Насосной станции Лохур-0. Технологическая часть (ТХ).	Стадия	Лист	Листов
ГИП		Шомили У.					РП	10	12
Нач. отдел		Шомили У.				Разводка трубопроводов вакуум-системы. Спецификация	ГУП "Проектный Институт "Точикгипроводхоз" Душанбе - 2026		
Норм. контр.		Хайбаров С.							


Согласовано

Взамен инв.

Подпись и дата

Инв. подл

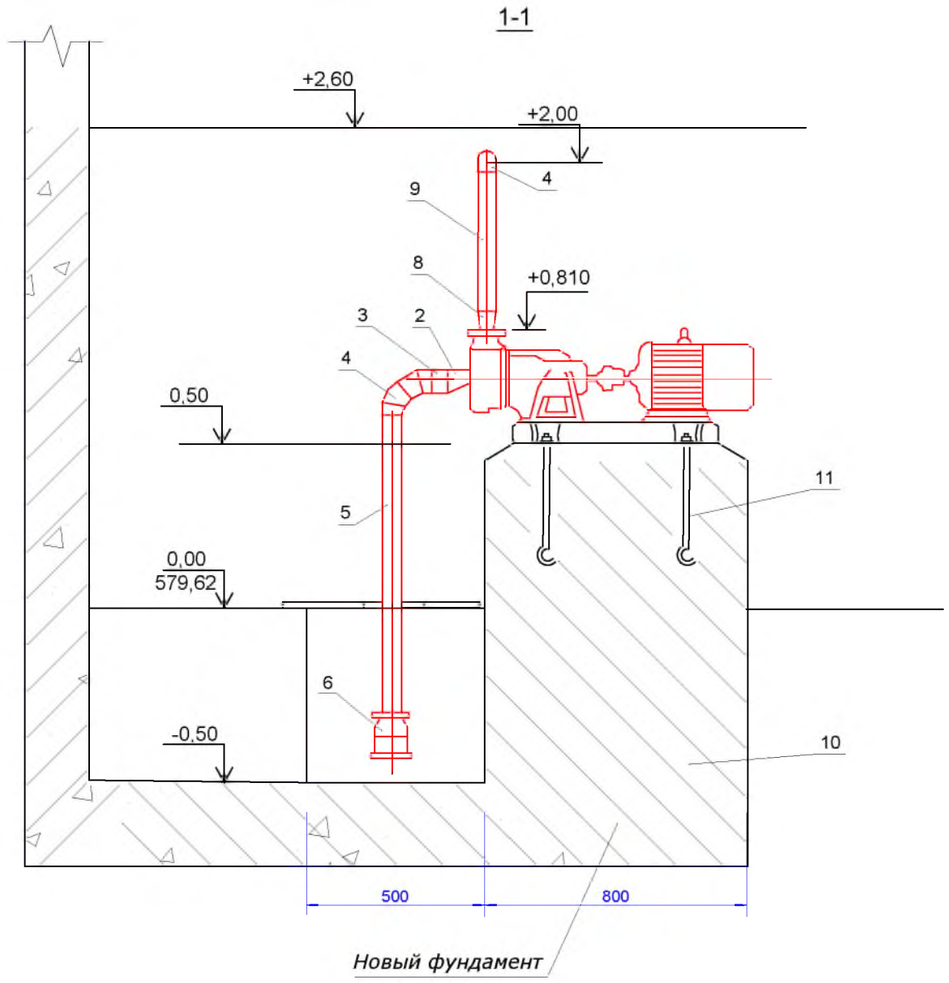

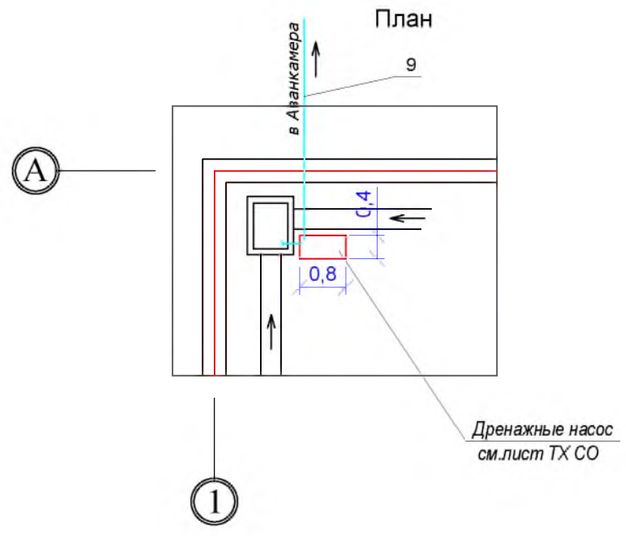

Спецификация

№№	Обозначение	Наименование	Кол-во	Масса ед.кг	Примечание
		Стандартные изделия			
1	ГОСТ 12817-80	Фланец 40-0,25МПа	1	1,04	
2		Муфты переходные 40х50мм	1	0,128	
3	ГОСТ 8957-75	Труба 50х3,0 **ГОСТ3262-75**	1		L=200,0мм
4	ГОСТ 12820-80	Отвод 90° 57х3,0	2	0,40	
5	ГОСТ 8946-75	Труба 50х3,0 **ГОСТ3262-75**	1		L=800,0мм
6		Приёмный клапан d=50мм	1		
7		Фланец 32-0,25МПа	1	1,04	
8		Муфты переходные 32х50мм	1		
9		Труба 50х3,0 **ГОСТ3262-75**	1		L=6200,0мм
10		Монолитный бетон В15	1		0,32м³
11		Анкерный болты М14	4		

Примечание:

1. Отметке ±0,00 соответствует отметка пола камеры 579,62

2. Дренажной насос с эл/двигателем включено в СО (поз 4)

						ТХ
						"Баркарорсозии пойгоххои обкашии Лохур-0,Лохур-1,Лохур-2 ва Лохур-3 дар нохияи Рудаки"
Изм.	Кол.уч.	Лист	**№ док.**	Подп.	Дата	
Разработ.		**Фрайдунзода О.**				Насосной станции Лохур-0. Технологическая часть (ТХ).
ГИП		Шомили У.				
Нач. отдел		Шомили У.				Установочный чертёж дренажного-насоса. Спецификация
Норм. контр.		Хайбаров С.				

Стадия	Лист	Листов
РП	11	12

ГУП "Проектный Институт "Точикгипроводхоз" Душанбе - 2026

Согласовано

Взамен инв.

Подпись и дата

Инв. подл

Спецификация оборудования и материалов

№№ П/П	Наименование и техническая характеристика оборудования и материалов Завод-изготовитель (для импортного оборудования-страна, фирма)	Тип, марка оборудования, обозначение документа и опросного листа	Наименование ед.изм.	Код	Код завода изготовителя	Цена единицы тыс.руб.	Кол-во	Масса единицы оборудования, кг	Примечание
	Оборудование								
1	Насос типа Д-горизонталные одно ступенчатые с раб.колесо Dк=615,8мм, корпус из высокопровочный чугун (ВЧ. 40-60) Q=5184м³/ч; H=50м, n=990.об/мин, (рабочий колесо насоса из нержавейший сталь) с электродвигателями мощностью N=1000 кВт. напряжение U=6000В; n=1000об/мин с учетом заводской рамы и транспортировкой до объекта и подготовка машин к испытанию сдачей под наладку и пуску для соединение к электросети **(агрегаты №1; №2; №3 и №4 Левого вращение китайского производства)**	KQSN800-M17S YKK560-6	шт				4,0	11696,0	46784,0кг
2	Дренажный центробежный насос типа К 20/18 Q=20м³/час, H=18м. с раб.колесо Dк=129мм, n=2900об/мин мощность эл. двигателя типа 4А80В2 N=2,2 кВт. напряжение U=220/380В; n=3000об/мин	К 20/18 (2К-9) 4А80В2	шт				1,0	68,0	68,0кг
3	Вакуум насос произв. всас.6,0м³/мин с электродвигатель мощ. N=18,5кВт, напряжение U=220/380В n=1500.об/мин	**ВВН1-6 4А160М4У3**	шт				2,0	590,0	1180,0кг
4	Приобретение и монтаж грузоподъемное оборудование до 10тн (таль электрический), эл.двигатель механизм подъема АСВ 52-4 N=14,0кВт, электродвигатель предвижения АОЛ 2-11-4 N=1,2кВт, n=1500об/мин	ТЭ 10-921	комп.				1,0	765,0	765,0кг
	Всасывающая линия								
5	Переход косой Dy=800х1200х7мм, L=1000мм	**ТП (типовой проектный насосных станции)**	шт				4,0	226,0	904,0кг
6	Металлическая труба Øн=1220х7мм, L=6200м	ГОСТ 10704-91	шт				4,0	1298,28	5193,12кг
7	Отвод 30° Øн=1220х7мм, L=964мм	МН2877-62	шт				4,0	203,0	812,0кг
8	Переход концентрический Dy=1200х1400х7мм, L=475мм	МН2883-62	шт				4,0	129,0	516.0кг
	Напорная линия								
9	Монтажная вставка Dy=700мм, L=605мм	AVK PN 16	шт				4,0	170,0	680,0кг
10	Задвижка стальная фланцевая Ø=700мм, L=800мм Ру=1,0МПа,с электроприводом	**30ч915бр**	шт				4,0	1320,0	5280.0кг
11	Приобретение и монтаж обратный клапан фланцевый Dy=700мм, Ру=1,6мПа	КО700.16-3311	шт				4,0	1005,0	4020,0кг
12	Переход концентрический Dy=700х1200х9мм, L=1181мм	МН2883-62	шт				4,0	290,0	1160,0кг
13	Металлическая труба Øн=1020х14мм, L=12000м	ГОСТ 10704-91	шт				2,0	4996,8	9993,60кг
14	Отвод 45° Øн=1200х14мм, L=1492мм	МН2878-62	шт				2,0	624,0	1248,0кг
15	Металлическая труба Øн=1220х14мм, L=9600мм	ГОСТ 10704-91	шт				2,0	3997,44	7994,88кг
16	Сальниковые проход из металлическая труба Øн=1420х10мм, L=600мм	ГОСТ 10704-91	шт				4,0	208,62	834,48кг

ПРИМЕЧАНИЕ:

1. Учесть электроды 3% от всего веса металлоконструкции.
2. Учесть масленную краску для металлоконструкции.
3. Данный лист рассматривать совместно с лист-2,3,4,5,5а,6 и 7

Согласовано

Взамен инв


Подпись и дата

Инв. подл

Изм.	Кол.уч.	Лист	№ док.	Подп.	Дата	ТХ		
						"Баркарорсозии пойгоххои обкашии Лохур-0,Лохур-1,Лохур-2 ва Лохур-3 дар нохияи Рудаки"		
Разработ.		Фойдушоев О.				Насосной станции Лохур-0. Технологическая часть (ТХ).	Стадия	Лист	Листов
ГИП		Шомили У.					РП	12	12
Нач. отдел		Шомили У.				Спецификация оборудования и материалов	ГУП "Проектный Институт "Точикгипроводхоз" Душанбе - 2026		
Норм. контр.		Хайбаров С.							

Формат А3

Характеристика насоса типа Д KQSN800-M17S n=1000 об/мин

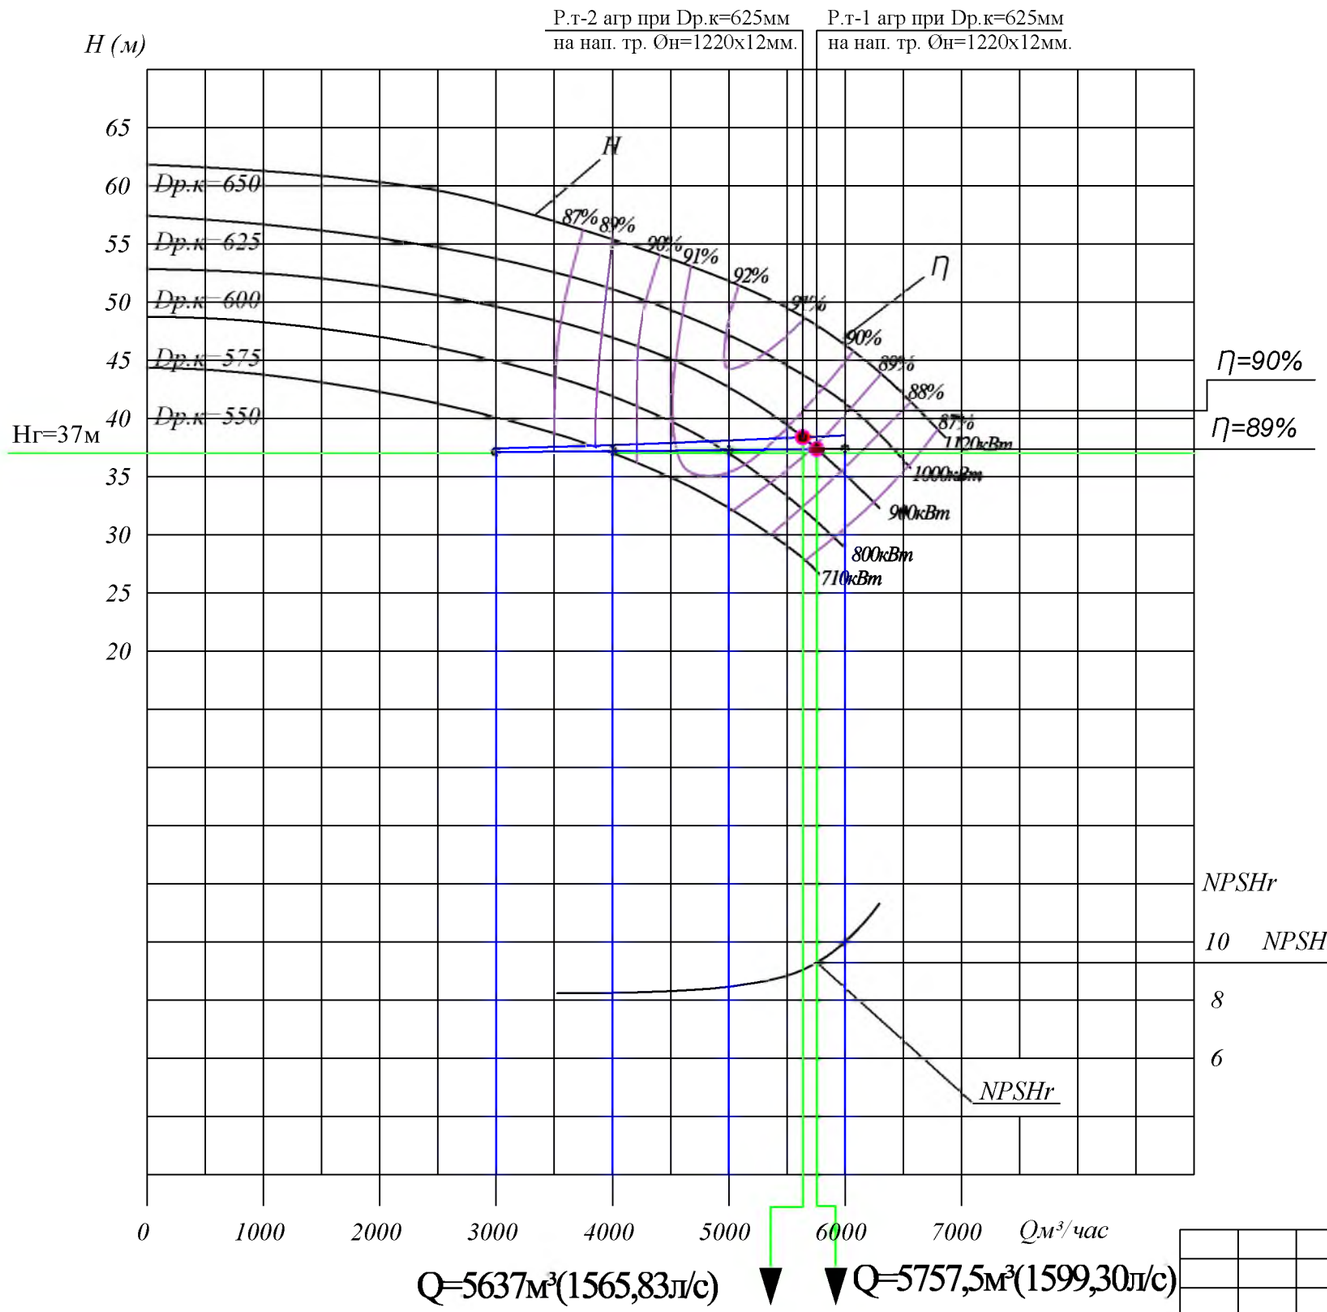

Определение манометрический напор и расчетный расход насоса типа Д KQSN800-M17S

Q л/сек	Q м³/час	Hгео. м	L, км	Dтр.в,мм	i на 1км, в м	∑i,в м	H,ман в м при 1-го агрегат	Примечание
		При работе 1-го агрегата						
833,33	3000,0	37,0	0,172	1220х12	0,50	0,103	37,103	
1111,11	4000,0	37,0	0,172	1220х12	0,85	0,175	37,175	
1388,89	5000,0	37,0	0,172	1220х12	1,30	0,27	37,27	
1666,67	6000,0	37,0	0,172	1220х12	1,87	0,38	37,38	
		При работе 2-х агрегатов						
833,33	3000,0	37,0	0,172	1220х12	0,50	0,412	37,412	
1111,11	4000,0	37,0	0,172	1220х12	0,85	0,7	37,7	
1388,89	5000,0	37,0	0,172	1220х12	1,30	1,08	38,08	
1666,67	6000,0	37,0	0,172	1220х12	1,87	1,52	38,52	

ТХ

"Баркарорсозии пойгоххои обкашии Лохур-0,Лохур-1,Лохур-2 ва Лохур-3 дар нохияи Рудаки"

Изм.	Кол.уч.	Лист	№ док.	Поди.	Дата
Разработ.		Фрайдунпоев О.			
ГИП		Шомили У.			
Нач. отдел		Шомили У.			
Норм. контр.		Хайбаров С.			

Насосной станции Лохур-0.
Технологическая часть (ТХ).

Стадия	Лист	Листов
РП	1	1

Рабочая характеристика насоса типа KQSN800-M17S

ГУП "Проектный Институт "Точикгипроводхоз"
Душанбе - 2026