АГЕНТСТВО ПО МЕЛИОРАЦИИ И ИРРИГАЦИИ
ПРИ ПРАВИТЕЛЬСТВЕ РЕСПУБЛИКИ ТАДЖИКИСТАН

ГУП "ПРОЕКТНЫЙ ИНСТИТУТ
"ТАДЖИКГИПРОВОДХОЗ"

РАБОЧИЙ ПРОЕКТ

"Баркарорсозии пойгоххои обкашии Лохур-0,Лохур-1,Лохур-2 ва Лохур-3 дар нохияи Рудаки"

АЛЬБОМ-1

Аванкамера насосной станции Лохур-1.
Гидротехническое решения.

ДУШАНБЕ-2026

АГЕНТСТВО ПО МЕЛИОРАЦИИ И ИРРИГАЦИИ
ПРИ ПРАВИТЕЛЬСТВЕ РЕСПУБЛИКИ ТАДЖИКИСТАН

ГУП "ПРОЕКТНЫЙ ИНСТИТУТ
"ТАДЖИКГИПРОВОДХОЗ"

РАБОЧИЙ ПРОЕКТ

"Баркарорсозии пойгоххои обкашии Лохур-0,Лохур-1,Лохур-2 ва Лохур-3 дар нохияи Рудаки"

АЛЬБОМ-1

Аванкамера насосной станции Лохур-1.
Гидротехническое решения.

ГЛ. ИНЖЕНЕР ИНСТИТУТА: ХАЙБАРОВ С.

ГЛ. ИНЖЕНЕР ПРОЕКТА: ШОМИЛИ У.

ДУШАНБЕ-2026

Таб. 1

Ведомость основных комплектов рабочих чертежей		
Обозначение	**Наименование**	**Примечание**
1	2	3
.ПЗ	Пояснительная записка	Книга-1
ТГИ	Инженерно-топогеодезический изыскания	Книга-2
ИГИ	Инженерно-геологический и гидрогеологичекий изысканий	Книга-3
ТХ	**Насосной станции Лохур-1.** Технологическая часть	Альбом-1
ГР	**Насосной станции Лохур-1.** Гидротехническое решение	Альбом-2
АС	**Насосной станции Лохур-1. Архитектурно-строительная часть**	Альбом-3
АС	**Насосной станции Лохур-1. Дежурное помещение Архитектурно-строительная часть**	Альбом-4
АС	**Насосной станции Лохур-1. Уборная на 1-го очко Архитектурно-строительная часть**	Альбом-5
ЭО	Электротехническая часть	Альбом-6
СМ	Сметная документация	Книга-4

Таб. 2

Ведомость рабочих чертежей основного комплекта **ТХ**		
Лист	**Наименование**	**Примечание**
1	2	3
1	Общие данные	
2	План площадка насосной станции М1:500. Экспликация и ведомость объёмов работ.	
3	Разрез в осях 1 -2. М1:100. Ведомость объёмов демонтажных работ.	
4	Сороудерживающая решетка. Спецификация.	
5	Ограждение ОГ-1. Спецификация.	

Таб.3

Ведомость ссылочных и прилагаемых документов		
Обозначение	Наименование	Примечание
	Ссылочные документы	
ГОСТ 10704-91	Трубы металлические	
ГОСТ 9466-75	Электроды для дуговой сварки сталей и наплавки	
	классификация и общие технические условия	
ГОСТ 19903-74	Лист стальная	
30ч906бр	Задвижки с электроприводом	
ГОСТ 8509-93	Уголки стальные горячекатаные равнопрочные	
	Прилагаемые документы	
ТХ.СО-1	Спецификация основного оборудования насосной станции	2-листов

Настоящий проект выполнен в соответствии с
дествующими нормами и правилами,
в том числе по взрыво - пожарной безопасности.

Гл. инженер проекта Шомили У.

						"Баркарорсозии пойгоххои обкашии Лохур-0,Лохур-1,Лохур-2 ва Лохур-3 дар нохияи Рудаки"
Изм.	Кол.уч.	Лист	№ док.	Подп.	Дата	
Разработ.		Фрайдунпоев О.				Аванкамера насосной станции Лохур-1. Гидротехническое решения.
ГИП		Шомили У.				
Нач. отдел		Шомили У.				
Норм. контр.		Хайбаров С.				Общие данные.

Стадия	Лист	Листов
РП	1	5

ГУП "Проектный Институт "Точикгипроводхоз" Душанбе - 2026

Согласовано


Взамен инв.

Подпись и дата

Инв. подл

План аванкамера насосной станции Лохур-1 II-го подъема

М1:250

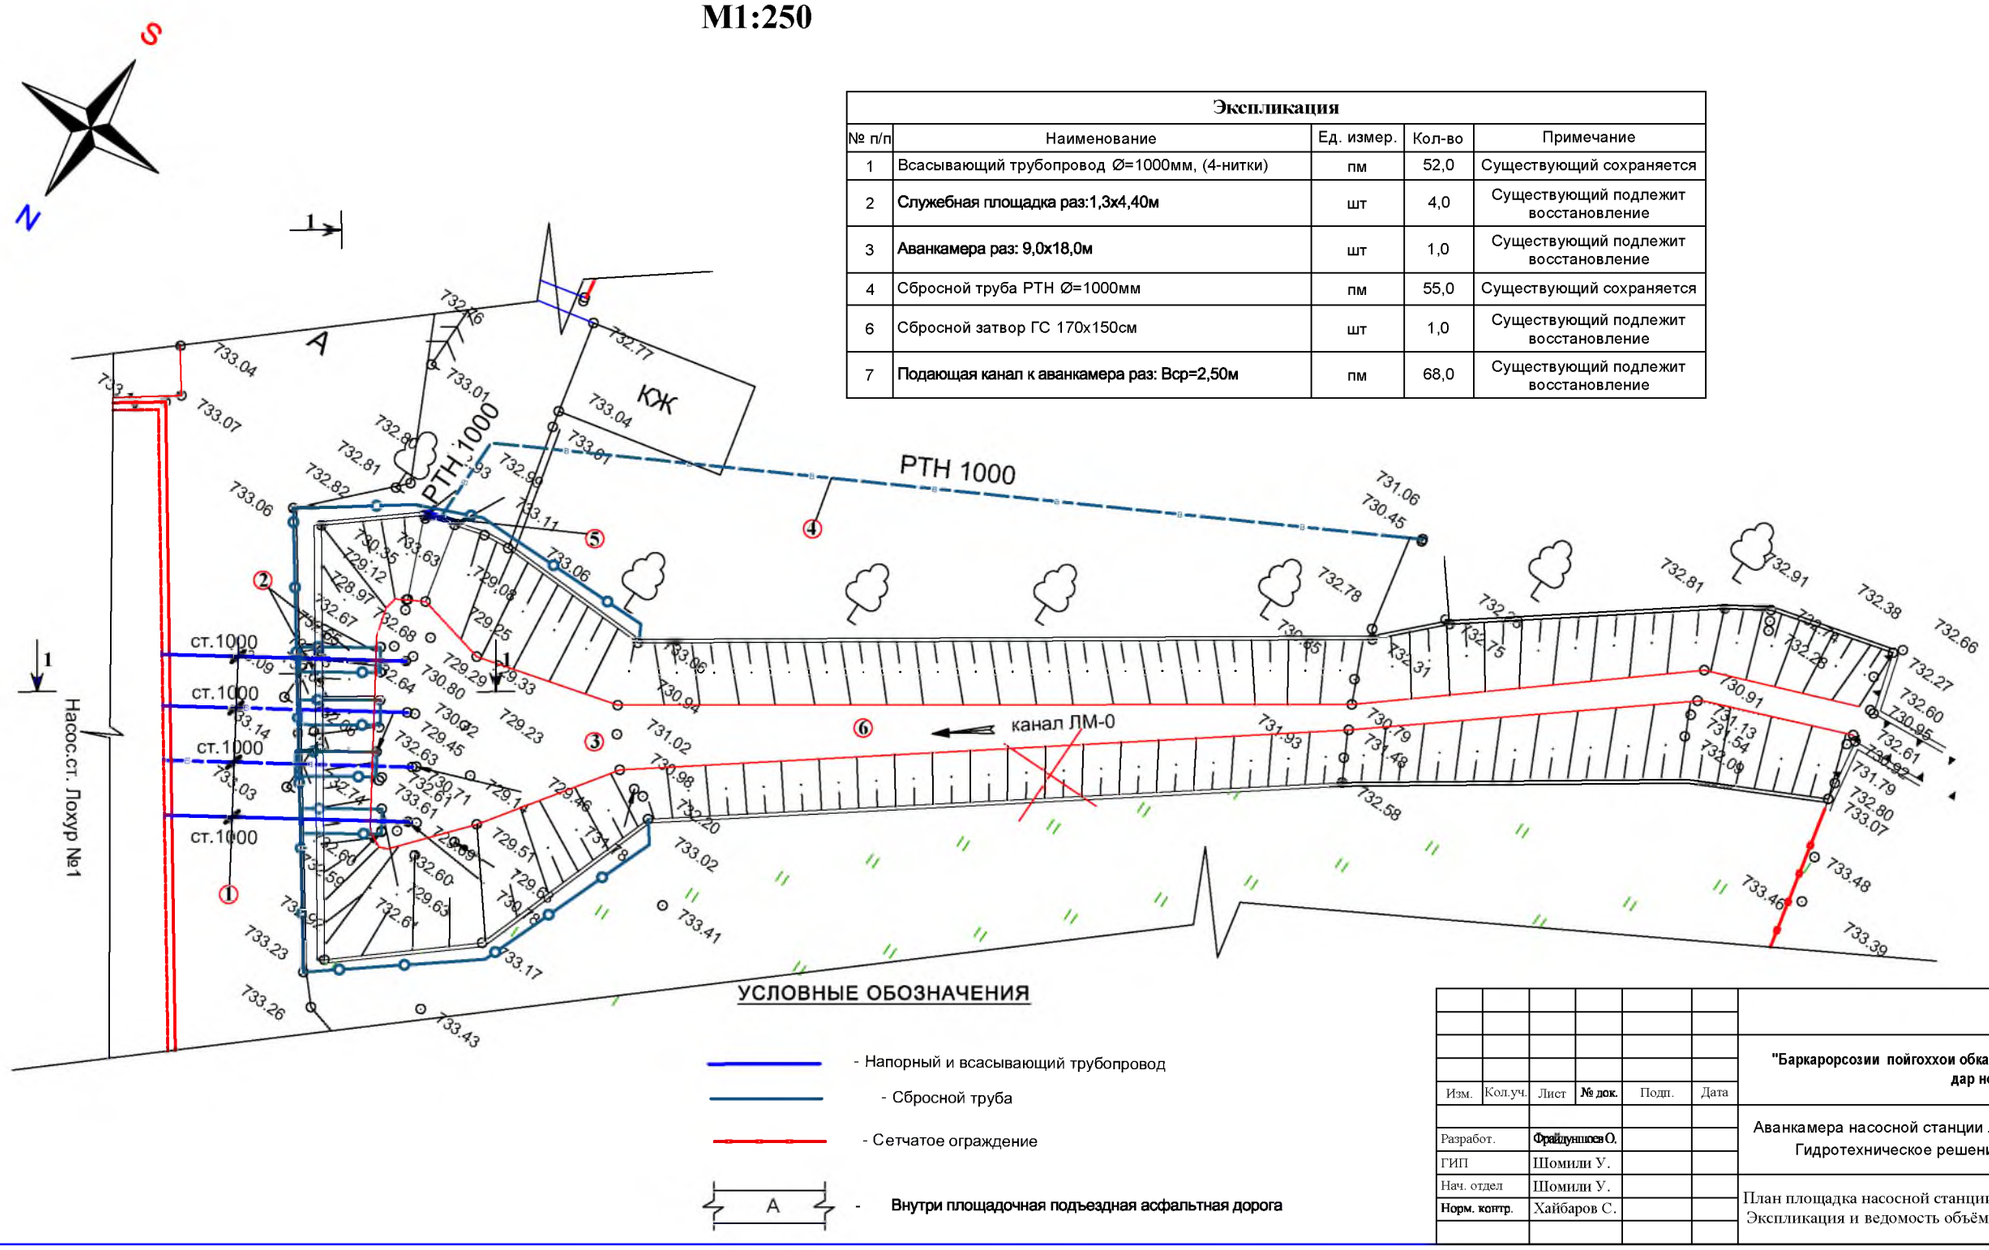

Экспликация

№ п/п	Наименование	Ед. измер.	Кол-во	Примечание
1	Всасывающий трубопровод Ø=1000мм, (4-нитки)	пм	52,0	Существующий сохраняется
2	**Служебная площадка раз:1,3х4,40м**	шт	4,0	Существующий подлежит восстановление
3	**Аванкамера раз: 9,0х18,0м**	шт	1,0	Существующий подлежит восстановление
4	Сбросной труба РТН Ø=1000мм	пм	55,0	Существующий сохраняется
6	Сбросной затвор ГС 170х150см	шт	1,0	Существующий подлежит восстановление
7	**Подающая канал к аванкамера раз: Вср=2,50м**	пм	68,0	Существующий подлежит восстановление

УСЛОВНЫЕ ОБОЗНАЧЕНИЯ

- Напорный и всасывающий трубопровод
- Сбросной труба
- Сетчатое ограждение
- А — **Внутри площадочная подъездная асфальтная дорога**

Согласовано

Взамен инв.

Подпись и дата

Инв. подл

Изм.	Кол.уч.	Лист	№ док.	Подп.	Дата
Разработ.		Файзуллоев О.			
ГИП		Шомили У.			
Нач. отдел		Шомили У.			
Норм. контр.		Хайбаров С.			


"Баркарорсозии пойгоххои обкашии Лохур-0,Лохур-1,Лохур-2 ва Лохур-3 дар нохияи Рудаки"

Аванкамера насосной станции Лохур-1. Гидротехническое решения.

Стадия	Лист	Листов
РП	2	5

План площадка насосной станции М1:500. Экспликация и ведомость объёмов работ.

ГУП "Проектный Институт "Точикгипроводхоз" Душанбе - 2026

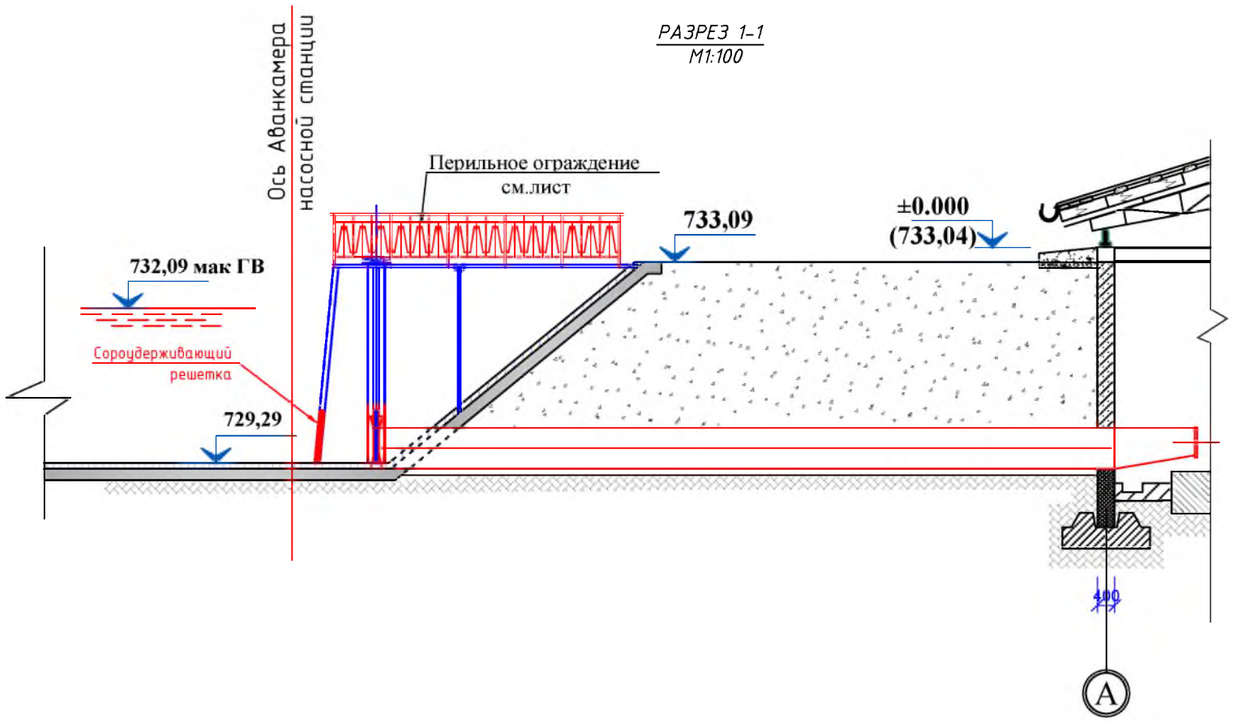

Ведомость объёмов

№ п /п	Наименование	Ед. изм	Масса оборудования, кг	Примечание
1	Демонтаж существующие ограждение	пм	65,0	
2	Установка перильное ограждение	пм	108,0	
3	Установка новый шит затвора ГС 100х100см	шт	4,0	
4	Изготовление и установка сороудерживающие рещетки раз :1,25х1,5м	шт	4,0	
5	Очистка от заиление дно аванкамера насосной стации в ручную t=20см	м³	31,0	
6	Устройство бетонная облицовка дно по всей площади аванкамера t=10см из бетона В20	м³	16,0	
7	Устройство сетки 5Вр-1 шаг150мм	м²	156,0	
8	Анкер из арматуры AIII Ø10мм, шаг 800мм,L=200мм -244шт	кг	30,2	

Примечание


1. Данный лист рассматривать совместно с листом- 2,3,6 и ТХ.СО
2. Нумерация позиции см.ТХ.СО.

Согласовано


Инв. подл | Подпись и дата | Взамен инв.

Изм.	Кол.уч.	Лист	№ док.	Подп.	Дата	"Баркарорсозии пойгоххои обкашии Лохур-0,Лохур-1,Лохур-2 ва Лохур-3 дар нохияи Рудаки"		
Разработ.		Фрайдунпосв О.				Аванкамера насосной станции Лохур-1. Гидротехническое решения.	Стадия	Лист	Листов
							РП	3	5
ГИП		Шомили У.							
Нач. отдел		Шомили У.				Разрез в осях 1 -2. М1:100. Ведомость объёмов демонтажных работ.	ГУП "Проектный Институт "Точикгипроводхоз" Душанбе - 2026		
Норм. контр.		Хайбаров С.							


Сороудерживающая решетка

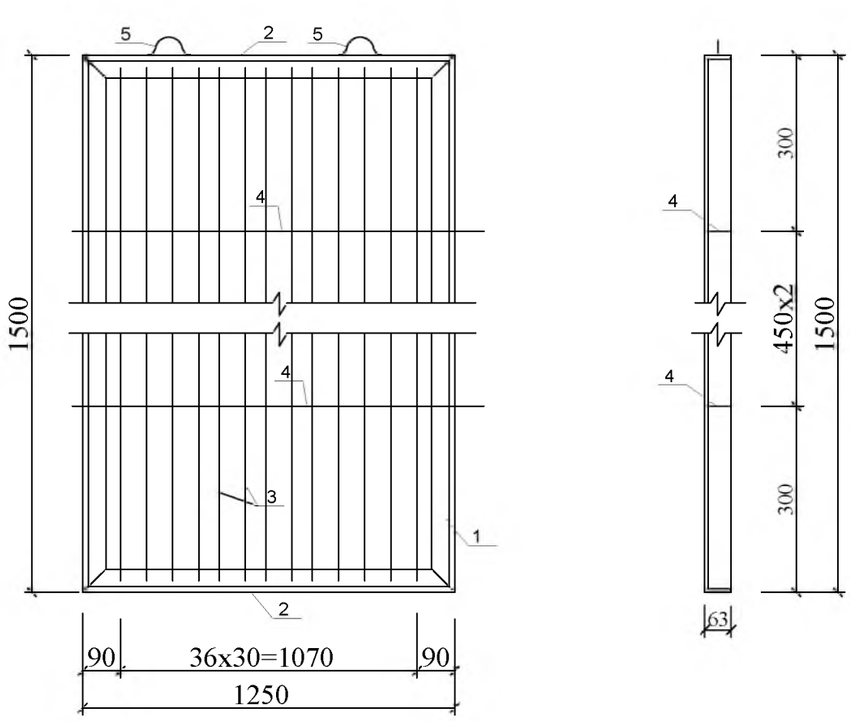


Деталь 3

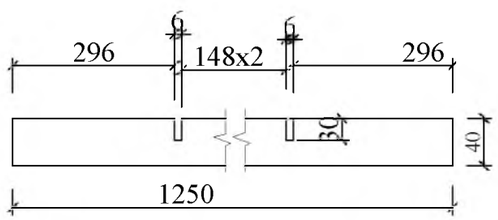

Деталь 5

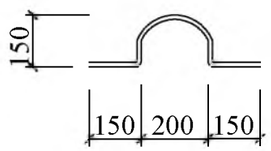

Деталь 4

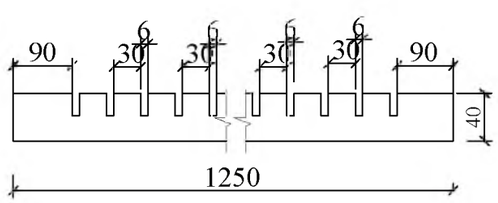

Спецификация на одну сороудерживающую решетку

Марка. поз.	Обозначение	Наименование	Кол.	Масса ед. кг.	Приме-чание
1	ГОСТ 8509-72	Уголок 63х5 L=3,0м	2	14,43	28,86кг
2	ГОСТ 8509-72	Уголок 63х5 L=2,5м	2	12,02	24,04кг
3	ГОСТ 103-76	Полоса 5х40 L=1,50м	36	2,35	84,78кг
4	ГОСТ 103-76	Полоса 5х40 L=1,25м	2	1,96	3,93кг
5	ГОСТ 5781-91	Арматура Ø AIII 16 L=650мм	2	1,027	2,054кг
		Электроды			2,0кг

Изготовить сороудерживающие решетки -4шт

Согласовано

Взам. инв. №

Подпись. и дата


Инв. № подл.

						"Баркарорсозии пойгоххои обкашии Лохур-0,Лохур-1,Лохур-2 ва Лохур-3 дар нохияи Рудаки"
Изм.	Кол.уч.	Лист	№ док.	Подп.	Дата	
Разработ.		Фрайдунпосев О.				Аванкамера насосной станции Лохур-1. Гидротехническое решения.
ГИП		Шомили У.				
Нач. отдел		Шомили У.				
Норм. контр.		Хайбаров С.				Сороудерживающая решетка. Спецификация.


Стадия	Лист	Листов
РП	4	5

ГУП "Проектный Институт "Точикгипроводхоз" Душанбе - 2026


Секция перильного ограждения

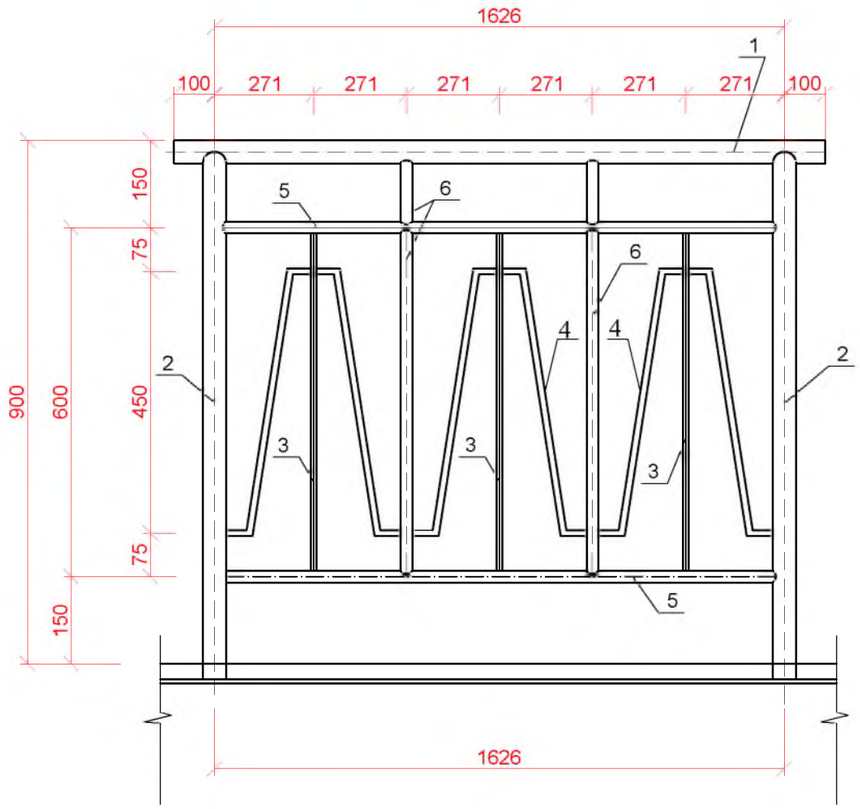

Деталь, поз. 2

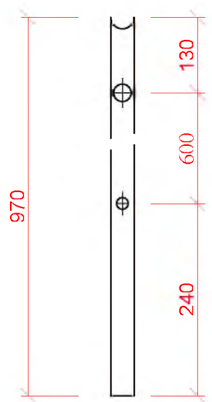

Деталь, поз. 4

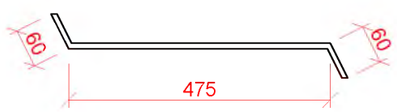

Спецификация на 1 секцию перильного ограждения

Марка Поз.	Обозначение	Наименование	ОГ 1		Примеч.
			Кол	Масса ед. кг	
		Детали			
1		Труба $\frac{32x2,0\ ГОСТ10704\text{-}91}{Вст3сп\ ГОСТ380\text{-}88}$ l=1826	1	2,69	
2		Труба $\frac{40x2,5\ ГОСТ10704\text{-}91}{Вст3сп\ ГОСТ380\text{-}88}$ l=970	2	2,24	4,48кг
3		Труба $\frac{15x1,4\ ГОСТ10704\text{-}91}{ГОСТ380\text{-}88\ Вст3сп}$ l=600	3	0,282	0,85 кг
4		Ø12 AI ГОСТ 5781-82, ℓ=595	6	0,49	3,17кг
5		Труба $\frac{25x2,0\ ГОСТ10704\text{-}91}{Вст3сп\ ГОСТ380\text{-}88}$ l=1620	2	1,83	3,67кг
6		Труба $\frac{25x2,0\ ГОСТ10704\text{-}91}{Вст3сп\ ГОСТ380\text{-}88}$ l=720	2	0,81	1,63 кг
7		Окраска перильного ограждения	1	-	16,49кг
8	ГОСТ 9467-75	Электроды Э-42, 2 %		0,40	

Примечание:

1. ØГ 1 - ограждение предназначено по контуру сооружение вес - 16,49 кг
2. Сварные швы выполнять ручной дуговой сваркой по ГОСТ 5264-80 по всему контуру соприкасания деталей.
3. Все размеры даны в мм
4. Изготовит **67**шт ограждение ОГ-1

Согласовано

Взам. инв. №

Подпись. и дата

Инв. № подл.

Изм.	Кол.уч.	Лист	№ док.	Подп.	Дата
Разработ.		Фрайдунпосев О.			
ГИП		Шомили У.			
Нач. отдел		Шомили У.			
Норм. контр.		Хайбаров С.			

"Баркарорсозии пойгоххои обкашии Лохур-0,Лохур-1,Лохур-2 ва Лохур-3 дар нохияи Рудаки"

Аванкамера насосной станции Лохур-1. Гидротехническое решения.

Стадия	Лист	Листов
РП	5	5

Ограждение ОГ-1. Спецификация.

ГУП "Проектный Институт "Точикгипроводхоз" Душанбе - 2026