**АГЕНТСТВО ПО МЕЛИОРАЦИИ И ИРРИГАЦИИ**
**ПРИ ПРАВИТЕЛЬСТВЕ РЕСПУБЛИКИ ТАДЖИКИСТАН**

**ГУП "ПРОЕКТНЫЙ ИНСТИТУТ**
**"ТАДЖИКГИПРОВОДХОЗ"**

# РАБОЧИЙ ПРОЕКТ

## "Баркарорсозии пойгоххои обкашии Лохур-0,Лохур-1,Лохур-2 ва Лохур-3 дар нохияи Рудаки"

**АЛЬБОМ-1**

**Насосной станции Лохур-1.**

**ДЕЖУРНОЕ ПОМЕЩЕНИЕ.**

**ДУШАНБЕ-2026**

**АГЕНТСТВО ПО МЕЛИОРАЦИИ И ИРРИГАЦИИ**
**ПРИ ПРАВИТЕЛЬСТВЕ РЕСПУБЛИКИ ТАДЖИКИСТАН**

**ГУП "ПРОЕКТНЫЙ ИНСТИТУТ**
**"ТАДЖИКГИПРОВОДХОЗ"**

# РАБОЧИЙ ПРОЕКТ

## "Баркарорсозии пойгоххои обкашии Лохур-0,Лохур-1,Лохур-2 ва Лохур-3 дар нохияи Рудаки"

**АЛЬБОМ-1**

**Насосной станции Лохур-1.**

**ДЕЖУРНОЕ ПОМЕЩЕНИЕ.**

ГЛ. ИНЖЕНЕР ИНСТИТУТА: ХАЙБАРОВ С.

ГЛ. ИНЖЕНЕР ПРОЕКТА: ШОМИЛИ У.

**ДУШАНБЕ-2026**

Таб. 1

| Ведомость основных комплектов рабочих чертежей | | |
|---|---|---|
| **Обозначение** | **Наименование** | **Примечание** |
| 1 | 2 | 3 |
| .ПЗ | Пояснительная записка | Книга-1 |
| ТГИ | Инженерно-топогеодезический изысканий | Книга-2 |
| ИГИ | Инженерно-геологический и гидрогеологичекий изысканий | Книга-3 |
| ТХ | **Насосной станции Лохур-1.** Технологическая часть | Альбом-1 |
| ГР | **Насосной станции Лохур-1.** Гидротехническое решение | Альбом-2 |
| АС | **Насосной станции Лохур-1. Архитектурно-строительная часть** | Альбом-3 |
| АС | **Насосной станции Лохур-1. Дежурное помещение Архитектурно-строительная часть** | Альбом-4 |
| АС | **Насосной станции Лохур-1. Уборная на 1-го очко Архитектурно-строительная часть** | Альбом-5 |
| ЭО | Электротехническая часть | Альбом-6 |
| СМ | Сметная документация | Книга-4 |

Ведомость рабочих чертежей основного комплекта


Таб.3

| Лист | Наименование | Примечание |
|---|---|---|
| 1 | **Дежурное помещение**.Общие данные | |
| 2 | **Дежурное помещение**.Продолжение общие данные | |
| 3 | Дежурное помещение. Фасад А-Б и Б-А. План кровля. | |
| 4 | Дежурное помещение.Фасады 1-2 и 2-1. | |
| 5 | Дежурное помещение. Фасад А-Б. Схема расположения стропил. Спецификация. | |
| 6 | Дежурное помещение. План. План фундамента.Ведомость объемов работ. | |
| 7 | Дежурное помещение. Окн-1. Др-1 и 2. Спецификация оконных и дверных проемов. | |
| 8 | Дежурное помещение. План расположения деревянных балок. Спецификация | |
| 9 | Дежурное помещение. Фрагмент армирование перемычек. Спецификация расхода материалов | |
| 10 | Дежурное помещение. Разрезы 3-3 и 4-4. Спецификация | |
| 11 | Дежурное помещение. Перемычки ПРМ-1 и 2 .Спецификация расход материалов ОП-1 | |

Настоящий проект выполнен в соответствии с действующими нормами и правилами в том числе по взрыво-пожарной безопасности

Гл.инженер проекта Шомили У .

Детали полов
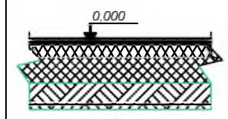
| Наименование или номер помещения по проекту | Тип по проекту | | Схема | Элементы и их толщина | м² |
|---|---|---|---|---|---|
| | 1 | этаж |   | 1. Ламинат<br>2. Цементная стяжка<br>3. подготовка из бетона-[illegible]<br>4. Гравийно–песчанная подготовка | 11 |

Ведомость отделки помещений

| | Наименование или номер помещения | Потолок | | Стены и перегородки | | Примечания |
|---|---|---|---|---|---|---|
| | | Площадь | Вид отделки | Площадь | Вид отделки | |
| 1 | Помещение дежурная | 12,0 | Шпатлевка с последующей водоэмульсионной окраской | 91,0 | Шпаклевка с последующей водоэмульсионной краской | |

Согласовано

Взамен инв

Подпись и дата

Инв. подл

| Изм. | Кол.уч. | Лист | № док. | Подп. | Дата | АС | | |
|---|---|---|---|---|---|---|---|---|
| | | | | | | "Баркарорсозии пойгоххои обкашии Лохур-0,Лохур-1,Лохур-2 ва Лохур-3 дар нохияи Рудаки" | | |
| Разработ. | | Фрайдунпоев О. | | | | Насосной станции Лохур-1. Архитектурно-строительная часть. | Стадия: РП | Лист: 1 / Листов: 11 |
| ГИП | | Шомили У. | | | | | | |
| Нач. отдел | | Шомили У. | | | | Дежурное помещение. Общие данные | ГУП "Проектный Институт "Точикгипроводхоз" Душанбе - 2026 | |
| Норм. контр. | | Хайбаров С. | | | | | | |

Исходные данные

Проект разработан для строительства в
IIВ климатическом районе с расчетной температурой -16°С.
Площадка строительства характеризуется следующими данными:
- вес снегового покрова для II-го района - 0,7 кПа;
- скоростное давление ветра для II-района - 0,30 кПа;
В основании фундаментов залегают грунты;
Сейсмичность стройплощадки - 7 балл
Степень огнестойкости здания - I.
Класс ответственности здания - II.

Строительные конструкции
Здание запроектировано в комплексном конструктивном решении.
Фундаменты - монолитные железобетонные из бетона класса В 15.
Сейсмопояс - монолитные железобетонные из бетона класса В 15.
Отмостка - бетонная по слою щебня толщиной 150 мм, шириной 1,50 м.
Стены из кирпичные кладки.
Перекрытие - деревянное из балок сечением 50х150 мм.
Кровля - из волнистой оцинкованной кровельной стали t=0,4-0,5мм.
Оконные блоки - индивидуального изготовления из пластика.
Дверные блоки - индивидуального изготовления из металлопластика.
Крыльца из бетона класса В15.

Антисейсмические мероприятия
Антисейсмические мероприятия предусмотрены в соответствии с требованиями главы МКС ЧТ 22-07-2007 "Строительство в сейсмических районах. Нормы проектирования". Несущие элементы железобетонного каркаса рассчитаны и законструированы с учетом воздействия горизонтальной сейсмической силы.

Антикоррозийная защита строительных конструкций
Для обеспечения требуемой долговечности все металлические конструкции и необетонированные закладные и соединительные изделия должны быть покрыты антикоррозийными лакокрасочными материалами 1 группы - пентафталевые, глифталевые, эпокси- эфирные, алкидностирольные, масляные, масляно-битумные, алкидно-уретановые, нитроцеллюзные (лаки ПФ-170 и ПФ-171 с 10-15% алюминиевой пудры, эмали ПФ-115, ПФ-113, ПФ-1126, ПФ-1189 и др.).
Все работы выполнять в соответствии с указаниями главы СНиП 2.03.11-85.

Защита деревянных элементов и изделий от возгорания и гниения
Все деревянные конструкции и изделия здания должны быть защищены от гниения, поражения насекомыми и дереворазрушающими грибами, а также от возгорания в соответствии с указаниями главы СНиП 2.03.11-85 "Защита строительных конструкций от коррозии". Для защиты деревянных конструкций от биологических агентов следует предусмотреть влагостойкое лакокрасочное покрытие или использовать влагобиозащитные пропиточные составы. В этих целях рекомендуется использовать пропиточные составы марки ТХЭФ-ПТ или марки БК (буроугольная композиция).

Противопожарные мероприятия
Все противопожарные мероприятия предусмотрены согласно главы МКС ЧТ 21-01-2007*.

Настоящий проект выполнен в соответствии с действующими нормами и правилами в том числе по взрыво-пожарной безопасности

Гл.инженер проекта Шомили У.

Согласовано

Взамен инв

Подпись и дата

Инв. подл

## ТЕХНИКО –ЭКОНОМИЧЕСКИЕ ПОКАЗАТЕЛИ

| НАИМЕНОВАНИЕ | КОЛИЧЕСТВО м² |
|---|---|
| Площадь застройки | 19,18 |
| Строительный обь?м | 43,3 |
| Общая площадь | 16,66 |
| Расчетная площадь | 10,34 |
| Полезная площадь | 10,34 |

ХАРАКТЕРИСТИКА ИНЖЕНЕРНО - ГЕОЛОГИЧЕСКИХ УСЛОВИЙ

Согласно заключению по архивным материалом об инженерно геологических изысканиях площадки строительства участок проектируемого строительство расположен в юго-западной районе Дангара .

Рельеф участка сравнительно ровный, с небольшими колебаниями в микрорельефе.

В геологическом строений принимают участке аллювиально-пролювиальные отложение. Грунты в основании фундаментов до разведанной глубины 5 м являются неоднородной.

Глинистый грунты участка обладают просадочными свойствами, в основном, при дополнительных нагрузках.Суммарная величина от собственного веса более 5,0см.Тип грунтовых условий по проявлению посадочных свойств II (второй). Крутизна откосов и траншей в зависимости глубина отрывки составляет:

для суглинка - до 1.5м 1:0.0, до 3.0м 1:0.5, до 5.0м 1:0.75. для галечника - до 1.5м 1:0.5, до 3.0м 1:1, до 5.0м 1:1. (МКС ЧТ 50-01-2007) При наличии в основании глинистых грунтов рекомендуется применение ленточные фундаменты. При углублении до кровли галечника, подготовка оснований не требуется.

Современные физико-геологические процессы на участке и прилегающей к нему территории не отмечены, за исключением хозяйственной деятельности человека (искусственные выемки, насыпи грунтов, посадки фруктовых деревьев). При проектировании предусмотреть пересадку фруктовых деревьев из контура проектируемого здания .


Ведомость отделки фасадов

| Фасад | Элементы | Отделка | Колер |
|---|---|---|---|
| Все фасады | Стены | Штукатурка, окраска фасадными красками (дождик) - AMY TERAZIT | Код: 223и 230 |
| | Цоколь , крыльца | Штукатурка и фасадными красками | |
| | Заполнение оконных и дверных проемов (наружные ) | Металлопластик | |
| | Кровли | Деревянная кровля опшивка из профилированный настил | |
| | Водослив с подоконников | Облицовка кровельной жестью , окраска эмалевой краской за 2 раза | |


АС

| Изм. | Кол.уч. | Лист | № док. | Подп. | Дата | АС | | |
|---|---|---|---|---|---|---|---|---|
| | | | | | | "Баркарорсозии пойгоххои обкашии Лохур-0,Лохур-1,Лохур-2 ва Лохур-3 дар нохияи Рудаки" | | |
| Разработ. | | Фрайдунпсев О. | | | | Насосной станции Лохур-1. Архитектурно-строительная часть. | Стадия: РП | Лист: 2 / Листов: 11 |
| ГИП | | Шомили У. | | | | | | |
| Нач. отдел | | Шомили У. | | | | Дежурное помещение. Общие данные.продолжение | ГУП "Проектный Институт "Точикгипроводхоз" Душанбе - 2026 | |
| Норм. контр. | | Хайбаров С. | | | | | | |


## Фасад А-Б

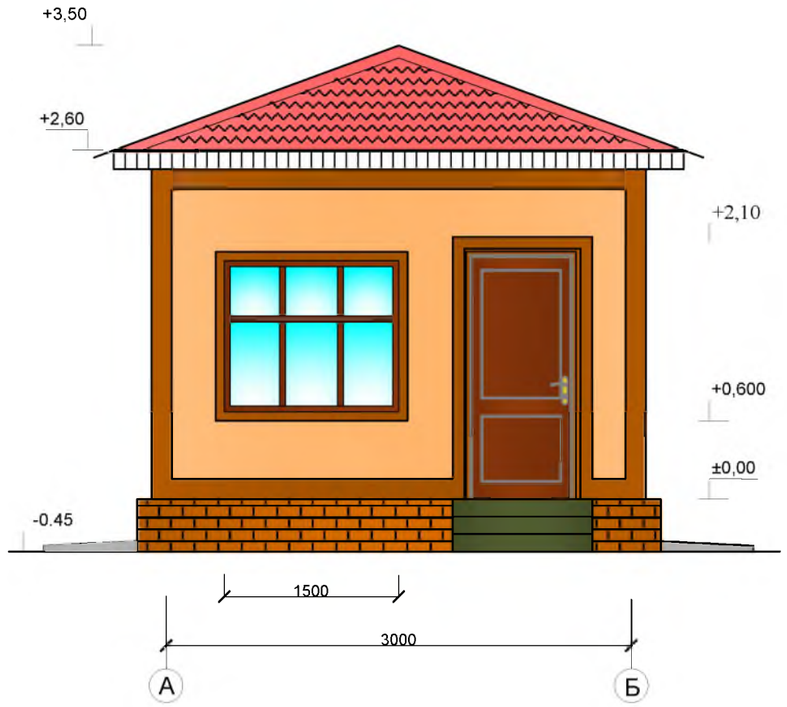


## План кровля

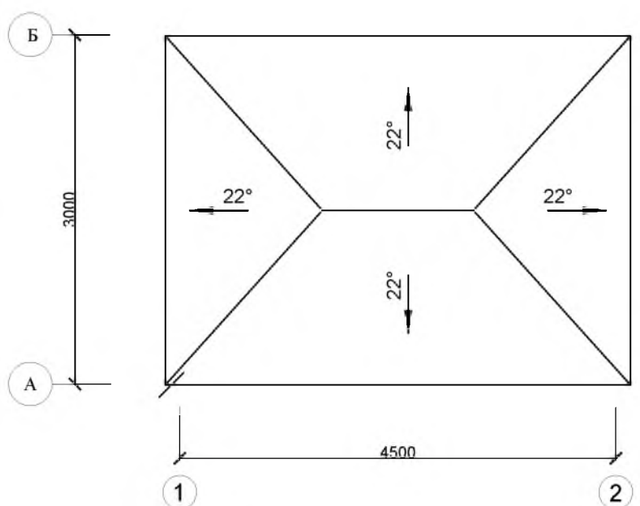


## Фасад Б-А

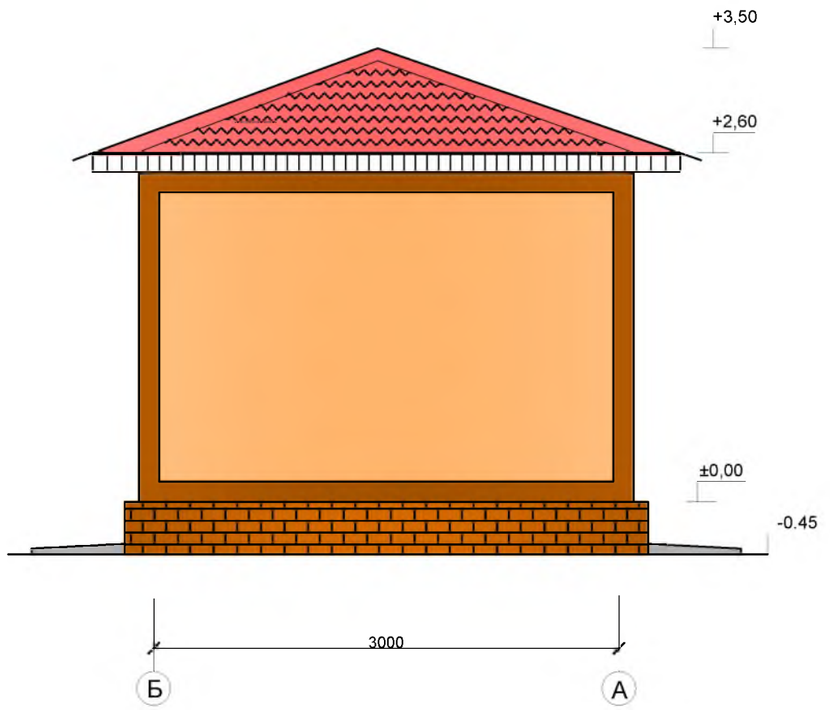


## НАРУЖНАЯ ОТДЕЛКА ФАСАДОВ

1. Наружные стены улучшенная штукатурка с последующей фасадной покраской фирмы ТЕКС.
2. Цоколь улучшенная штукатурка с последующей фактурной окраской фирмы ТЕКС.
3. Крыльцо бетонная стяжка.
4. Кровля из оцинкованных листов.
5. Окна пластиковые
6. Двери из металлопластика

Согласовано

Взамен инв.

Подпись и дата

Инв. подл


АС

| | | | | | | |
|---|---|---|---|---|---|---|
| | | | | | | **АС** |
| | | | | | | **"Баркарорсозии пойгоххои обкашии Лохур-0,Лохур-1,Лохур-2 ва Лохур-3 дар нохияи Рудаки"** |
| Изм. | Кол.уч. | Лист | № док. | Подп. | Дата | |
| Разработ. | | Фрайдуншоев О. | | | | Насосной станции Лохур-1. Архитектурно-строительная часть. |
| ГИП | | Шомили У. | | | | |
| Нач. отдел | | Шомили У. | | | | Дежурное помещение. Фасад А-Б и Б-А. План кровля. |
| Норм. контр. | | Хайбаров С. | | | | |


| Стадия | Лист | Листов |
|---|---|---|
| РП | 3 | 11 |

**ГУП "Проектный Институт "Точикгипроводхоз" Душанбе - 2026**

## Фасад 1-2

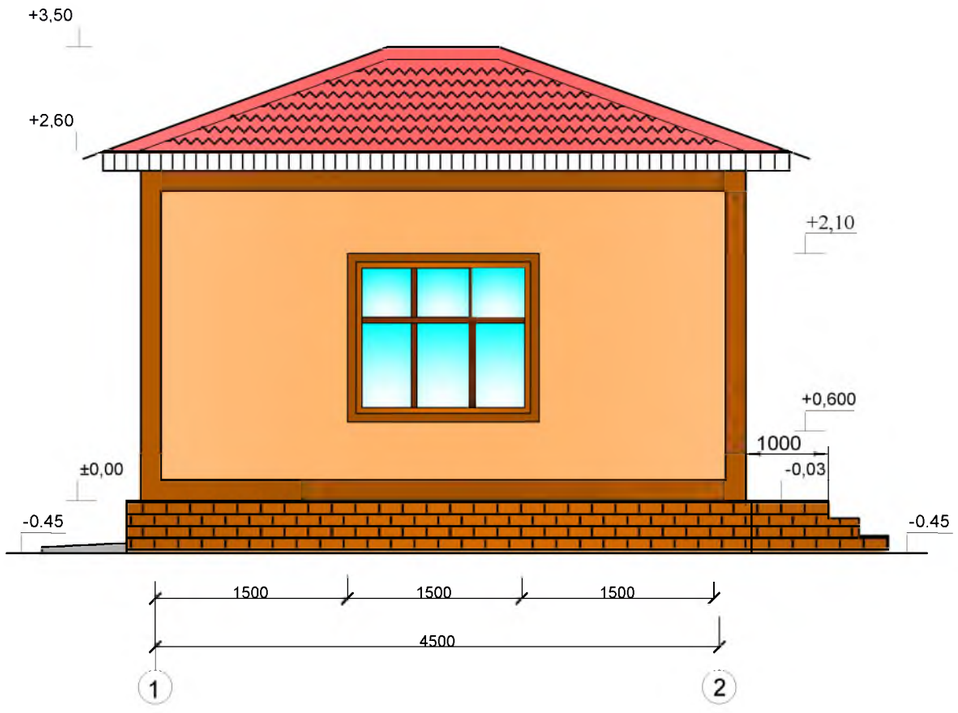


## Фасад 2-1

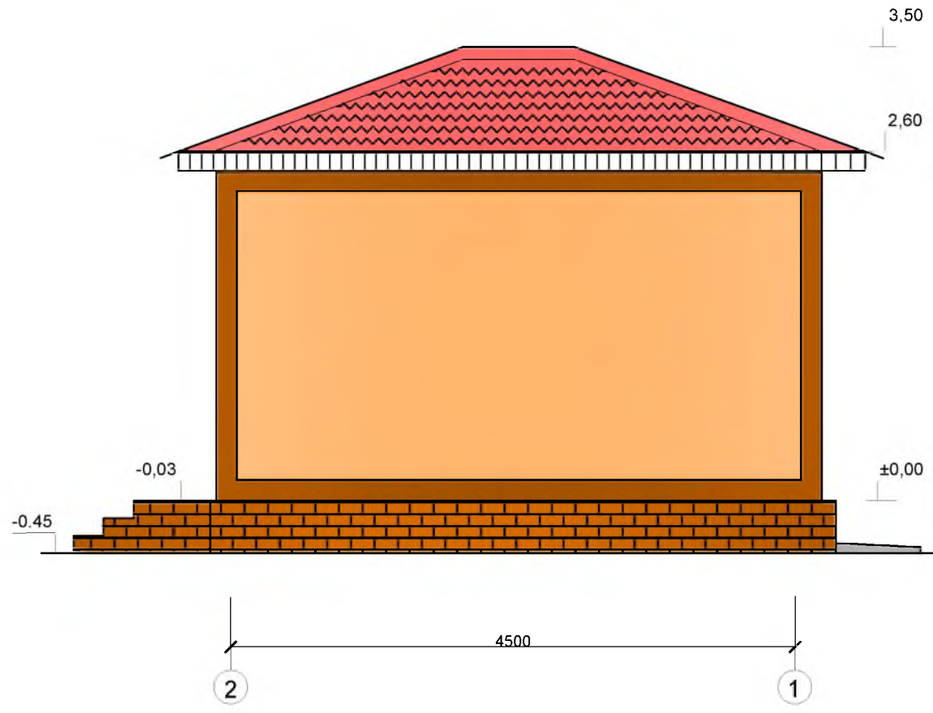


Согласовано

Взамен инв.

Подпись и дата

Инв. подл


AC

| | | | | | | |
|---|---|---|---|---|---|---|
| | | | | | | **AC** |
| | | | | | | **"Баркарорсозии пойгоххои обкашии Лохур-0,Лохур-1,Лохур-2 ва Лохур-3 дар нохияи Рудаки"** |
| Изм. | Кол.уч. | Лист | № док. | Подп. | Дата | |
| Разработ. | | Фрайдуншоев О. | | | | Насосной станции Лохур-1. Архитектурно-строительная часть. |
| ГИП | | Шомили У. | | | | |
| Нач. отдел | | Шомили У. | | | | |
| Норм. контр. | | Хайбаров С. | | | | Дежурное помещение. Фасад 1-2 и 2-1 |


| Стадия | Лист | Листов |
|---|---|---|
| РП | 4 | 11 |

**ГУП "Проектный Институт "Точикгипроводхоз" Душанбе - 2026**

## Фасад А-Б

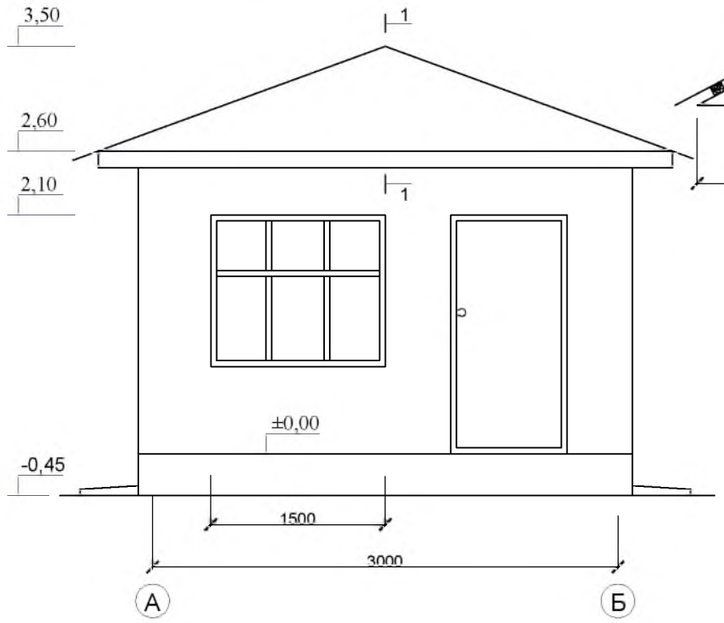


## 1-1

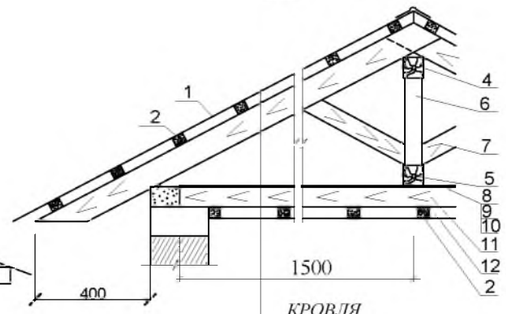



*КРОВЛЯ*

1 Металлочерепица t=0,4мм
2 Брусок 80х30 шаг 350
3 Стропильная нога 50х150
4 Верхний прогон 100х200
5 Нижний прогон 100х200
6 Стойка 150х150
7 Подкосы стойки 150х100
8 Глиносоломенная стяжка t=6см
9 Рубероид 1 слой
10 Горбыли
11 Мауэрлат 150х70
12 Гипсокартон


Спецификация

| №№ | Обозначение | Наименование | Ед. изм | Кол-во | Примечание |
|---|---|---|---|---|---|
| | | **Кровля** | | | |
| 1 | ГОСТ 30340-95 | Металлочерепица t=0,4 мм | м² | 23,0 | |
| 2 | ГОСТ 8466-66 | Брусок 80х30 шаг350 | м³ | 0,08 | Lобщ=30600мм |
| 3 | ГОСТ 8466-66 | Стропильная нога 50х150 | м³ | 0,18 | Lобщ=24000мм |
| 4 | ГОСТ 8466-66 | **Верхний прогон 100х200** | шт/м³ | 1/0,026 | Lобщ=1300мм |
| 5 | ГОСТ 8466-66 | Нижний прогон 100х200 | шт/м³ | 1/0,026 | Lобщ=1300мм |
| 6 | ГОСТ 8466-66 | Стойка 150х150 | шт/м³ | 2/0,032 | Lобщ=700мм |
| 7 | ГОСТ 8466-66 | **Подкосы стойки 150х100** | шт/м³ | 4/0,05 | Lобщ=850мм |
| 8 | | Глиносоломенная стяжка | м2 | 17,5 | |
| 9 | | Рубероид 1 слой | м2 | 17.5 | |
| 10 | ГОСТ 8466-66 | Горбыли | м3 | 0,48 | |
| 11 | ГОСТ 8466-66 | Мауэрлат 150х70 | м3 | 0,147 | |
| 12 | | Гипсокартон | м2 | 12 | |
| | | **Сейсмопояс** | | | |
| 13 | ГОСТ 26633-85 | Бетон В15 | м3 | 1,04 | |
| 14 | ГОСТ 5781-81 | Арматура ø10 А III | кг | 34,55 | |
| 15 | ГОСТ 5781-81 | Арматура ø6 А I | кг | 6,22 | |

## Схема расположения стропил

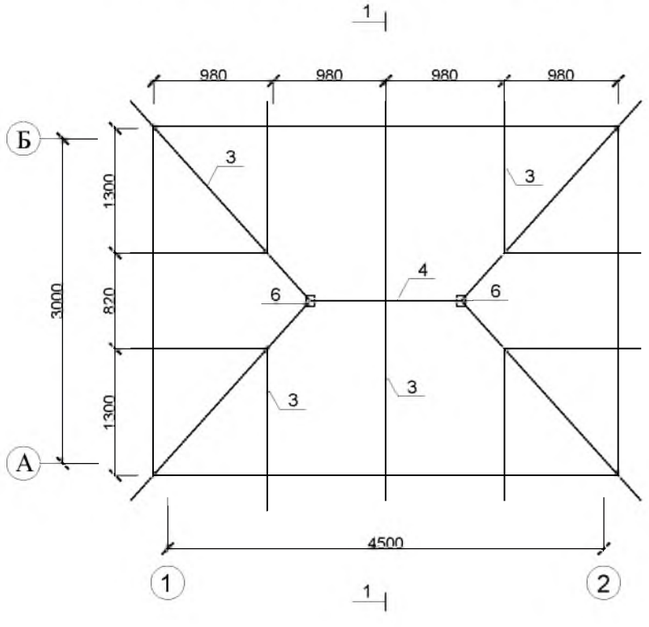


## Сейсмопояс

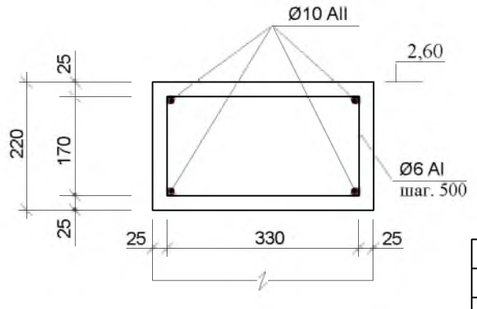


Согласовано

Инв. подл | Подпись и дата | Взамен инв.


AC

| | | | | | | |
|---|---|---|---|---|---|---|
| | | | | | | **AC** |
| | | | | | | **"Баркарорсозии пойгоххои обкашии Лохур-0,Лохур-1,Лохур-2 ва Лохур-3 дар нохияи Рудаки"** |
| Изм. | Кол.уч. | Лист | № док. | Подп. | Дата | |
| Разработ. | | Фрайдунпоев О. | | | | Насосной станции Лохур-1. Архитектурно-строительная часть. |
| ГИП | | Шомили У. | | | | |
| Нач. отдел | | Шомили У. | | | | Дежурное помещение. Фасад А-Б. Схема расположения стропил. Спецификация. |
| Норм. контр. | | Хайбаров С. | | | | |


| Стадия | Лист | Листов |
|---|---|---|
| РП | 5 | 11 |

**ГУП "Проектный Институт "Точикгипроводхоз" Душанбе - 2026**

## ПЛАН на отм. ±0,000

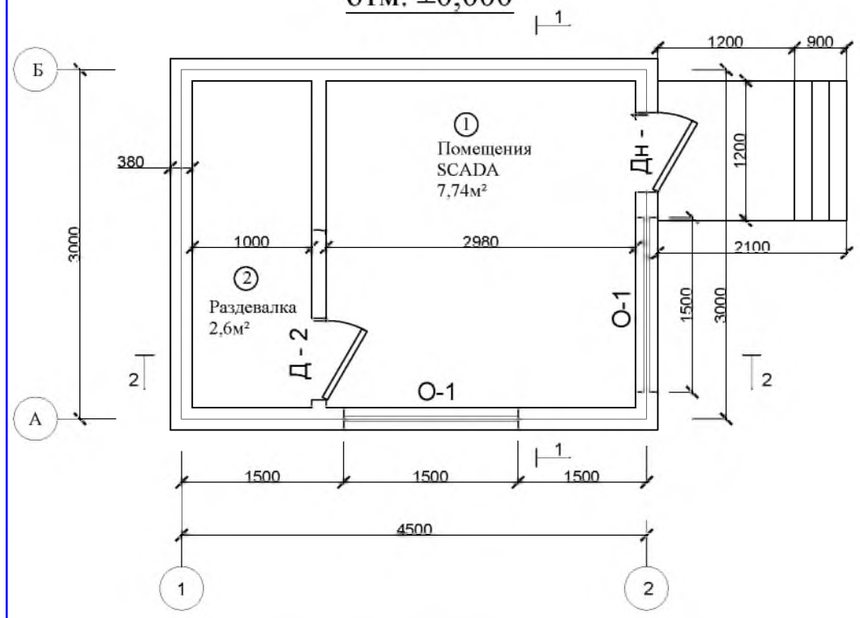


## План фундамента

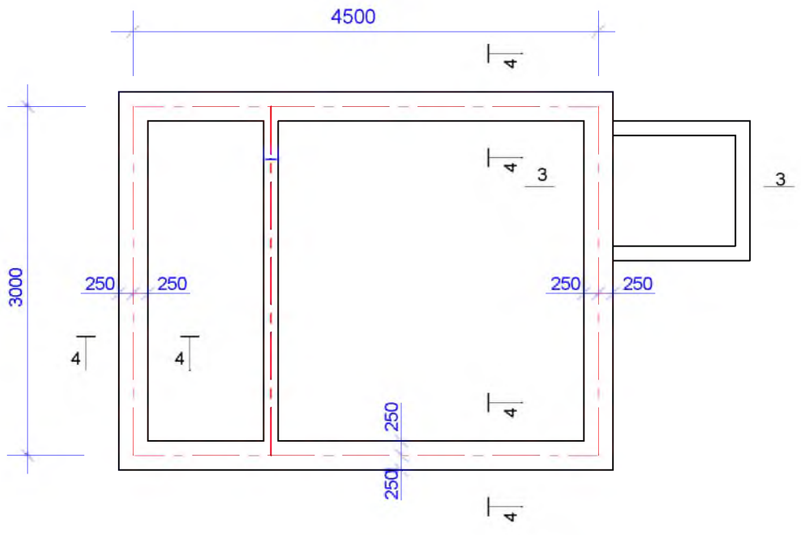


Ведомость объемов работ

| N/N n/n | НАИМЕНОВАНИЕ | Ед изм | Кол-во | Примечание |
|---|---|---|---|---|
| 1 | Выемка грунта под фундамент | м3 | 12,0 | |
| 2 | Обратная качественная засыпка | м3 | 7.0 | |
| 3 | Стены из кирпичана цементном растворе В5 | м3 | 17.0 | |
| 4 | Ленточный фундаментна бетоне В15 t=0,5м | м3 | 5.4 | |
| 5 | Порог из бетона В15 | м3 | 0,4 | |
| 6 | Отмостка вокруг домика из бетона В15 | м3 | 1,5 | |
| 7 | Окно пластиковый 150х150 | шт | 2 | |
| 8 | Дверь металлопластиковый 210х100см | шт | 1 | |
| 9 | Дверь металлический 210х100см | шт | 1 | |
| 10 | Полы: -цементная стяжка t=2см | м2 | 12.23 | |
| | -подготовка из бетона В7,5 t=10см | м3 | 1.0 | |
| | -гравийная подготовка t=10см | м3 | 1.1 | |
| 11 | Ламинат t=8мм | м2 | 11 | |
| 12 | Внутренняя отделка | | | |
| | а)штукатурка стен | м2 | 53 | |
| | б)Шпаклевка стен и водоэмуционной краской | м2 | 53 | |
| 13 | Наружная отделка | | | |
| | а) штукатурка стен известково-цементно-песчанным раствором | м2 | 38 | |
| | б) Шпаклевка | м2 | 38 | |
| 14 | Покраска потолка а) эмулционной краской | м2 | 12 | |
| 15 | Гидроизоляция верх фундамента на цем.раствором сост 1/3 | м2 | 6,0 | |
| 16 | Гидроизоляция фундамента обмазочная за 2 раза | м2 | 26,0 | |
| | | | | |

## Экспликация помещение

| №п/п | Наименование | Ед изм | Кол-во | Примечание |
|---|---|---|---|---|
| 1 | Комната SCADA | м² | 7,74 | |
| 2 | Раздевалка | м² | 2,6 | |

***Примечания:*** *Все деревянные элементы должны быть антисептированы и покрыты сернокислым аммонием с целью огнезащиты.*
*Защитную обработку деревянных конструкций выполнить в соответствии с требованиями СНиП 2.03.11-85 гл.3 и СНиП 2.01.02-85 п.1.8*


АС

| Изм. | Кол. уч | Лист | № док. | Подп. | Дата | Восстановление насосной станции "Лохур-1" Архитектурно-строительная часть Дежурное помещение. План фундамента. | Лист 6 |
|---|---|---|---|---|---|---|---|


Согласовано

Инв. подл | Подпись и дата | Взамен инв.

## Разрез 1-1

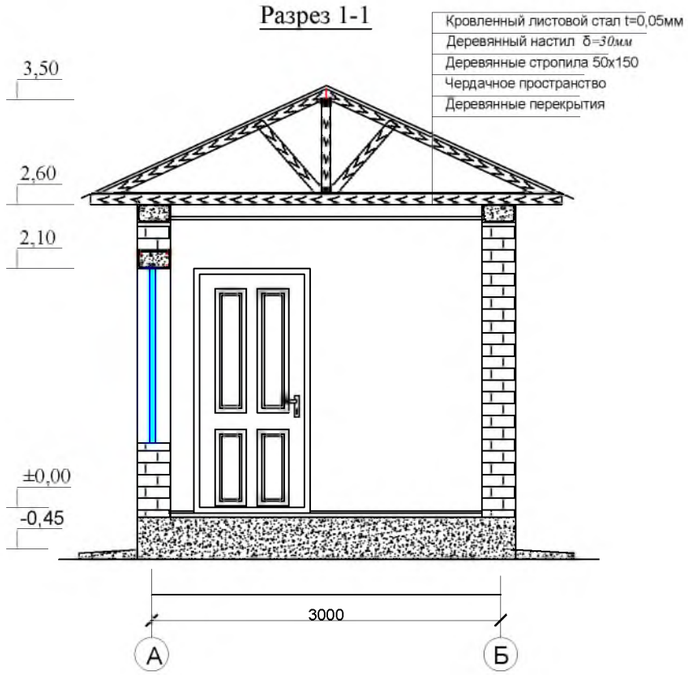




## Разрез 2-2

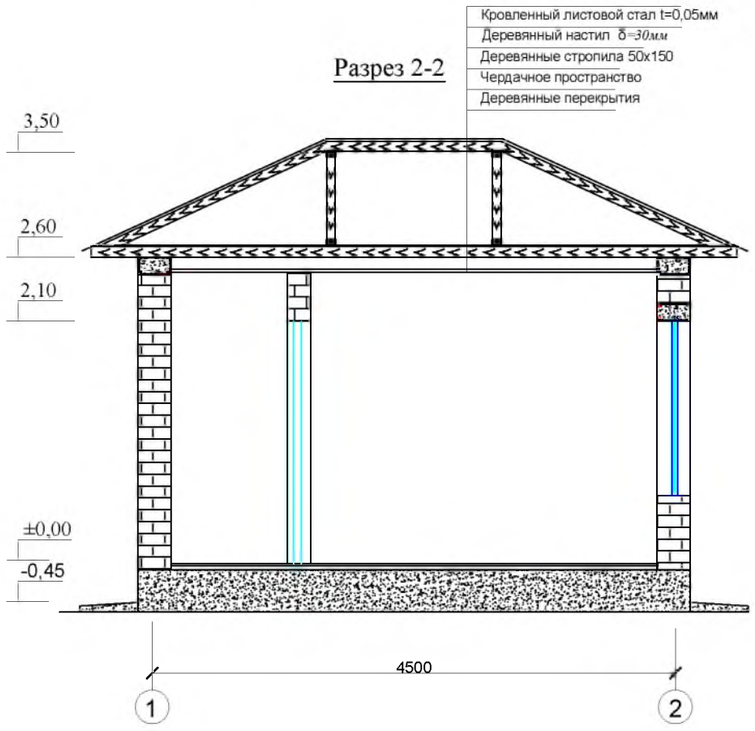



## Спецификация заполнения оконных и дверных проемов

| № поз. | Наименование | Размеры проема (ммхмм) | Количество | | Всего | Примечание |
|---|---|---|---|---|---|---|
| | | | 1 этаж | 2 этаж | | |
| 1 | Дн-1 | 1000 х 2100 | 1 | 1 | 1 | Металлопластика |
| 2 | Д-2 | 1000 х 2100 | 1 | 1 | 1 | деревянная |
| 3 | О-1 | 1500х 1500 | 1 | 1 | 1 | Металлопластика |

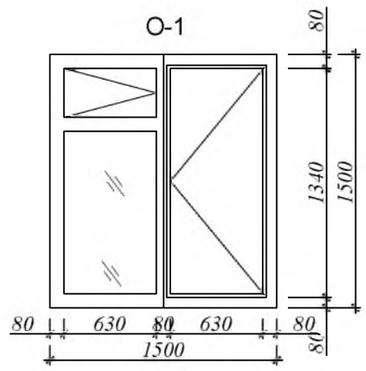

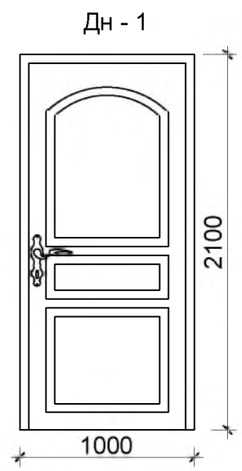
*Примечание:*

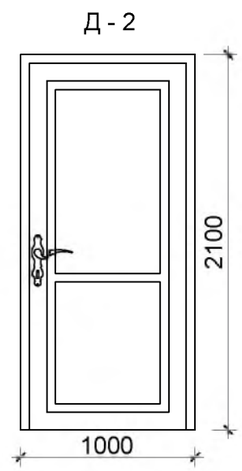*1.Все окна и двери оборудуются навесами, ручками для открывания, замками в заводских условиях.*

*2. Размеры блоков окон и дверей даны по размеру проемов. Фирмам-изготовителям уточнить габариты блоков по месту, оставить монтажный зазор.*

Согласовано

Инв. подл | Подпись и дата | Взамен инв.


АС

| | | | | | | |
|---|---|---|---|---|---|---|
| | | | | | | **АС** |
| | | | | | | **"Баркарорсозии пойгоххои обкашии Лохур-0,Лохур-1,Лохур-2 ва Лохур-3 дар нохияи Рудаки"** |
| Изм. | Кол.уч. | Лист | № док. | Подп. | Дата | |
| Разработ. | | Фрайдунпоев О. | | | | Насосной станции Лохур-1. Архитектурно-строительная часть. |
| ГИП | | Шомили У. | | | | |
| Нач. отдел | | Шомили У. | | | | Дежурное помещение. Окн-1. Др-1 и 2. Спецификация оконных и дверных проемов. |
| Норм. контр. | | Хайбаров С. | | | | |

| Стадия | Лист | Листов |
|---|---|---|
| РП | 7 | 11 |

**ГУП "Проектный Институт "Точикгипроводхоз" Душанбе - 2026**

# ПЛАН
## расположения деревянных балок

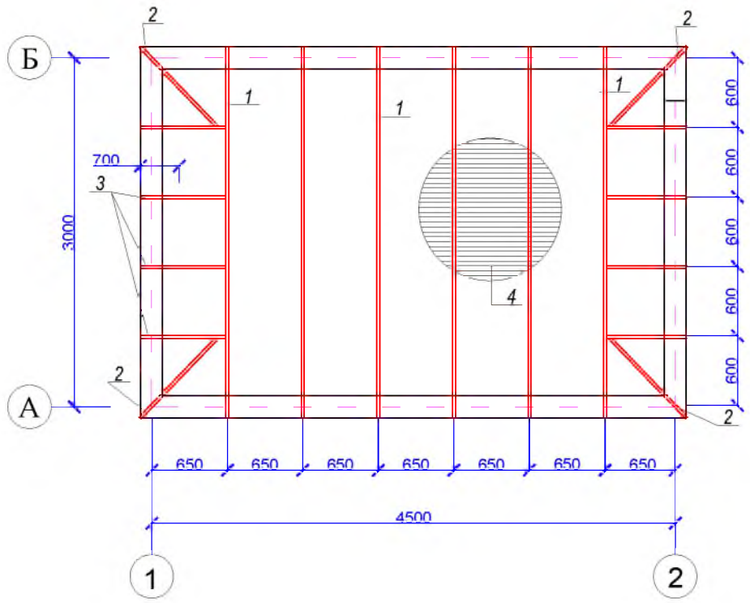


## СПЕЦИФИКАЦИЯ РАСХОД МАТЕРИАЛОВ ДЕРЕВЯННЫХ БАЛОК

| | Наименование | Сечение мм х мм | Колич шт | Длина м | | Объём $м^3$ | Прим |
|---|---|---|---|---|---|---|---|
| | | | | на один | всего | | |
| 1 | Деревяные балки | 50х150 | 6,0 | 3400 | 0,0255 | 0,153 | |
| 2 | Деревяные балки | 50х150 | 4,0 | 850 | 0,0063 | 0,025 | |
| 3 | Деревяные балки | 50х150 | 8,0 | 650 | 0,0048 | 0,039 | |
| 4 | Черный потолок | 20х120 | - | - | - | 0,213 | |

***Примечания:*** *Все деревянные элементы должны быть антисептированы и покрыты сернокислым аммонием с целью огнезащиты. Защитную обработку деревянных конструкций выполнить в соответствии с требованиями СНиП 2.03.11-85 гл.3 и СНиП 2.01.02-85 п.1.8*

Согласовано

Взамен инв.

Подпись и дата

Инв. подл


АС

| | | | | | | |
|---|---|---|---|---|---|---|
| | | | | | | **АС** |
| | | | | | | "Баркарорсозии пойгоххои обкашии Лохур-0,Лохур-1,Лохур-2 ва Лохур-3 дар нохияи Рудаки" |
| Изм. | Кол.уч. | Лист | № док. | Подп. | Дата | |
| Разработ. | | Фрайдунпоев О. | | | | Насосной станции Лохур-1. Архитектурно-строительная часть. |
| ГИП | | Шомили У. | | | | |
| Нач. отдел | | Шомили У. | | | | Дежурное помещение. План расположения деревянных балок. Спецификация |
| Норм. контр. | | Хайбаров С. | | | | |


| Стадия | Лист | Листов |
|---|---|---|
| РП | 8 | 11 |

**ГУП "Проектный Институт "Точикгипроводхоз" Душанбе - 2026**


РАЗВЁРТКА СТЕН ПО ОСИ "А-Б "

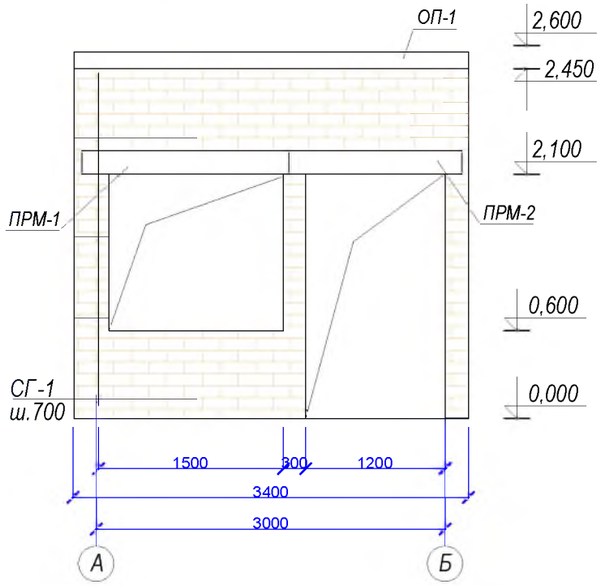



РАЗВЁРТКА СТЕН ПО ОСИ "1-2 "

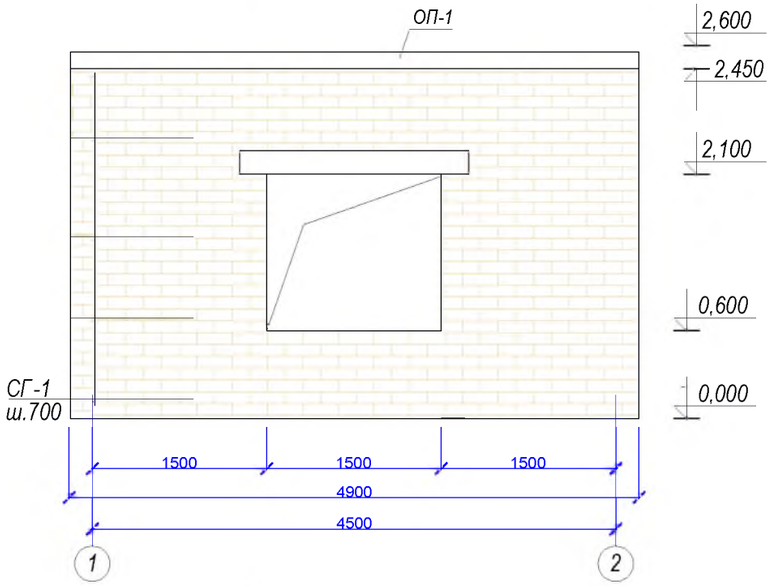


РАЗВЁРТКА СТЕН ПО ОСИ "Б-А "

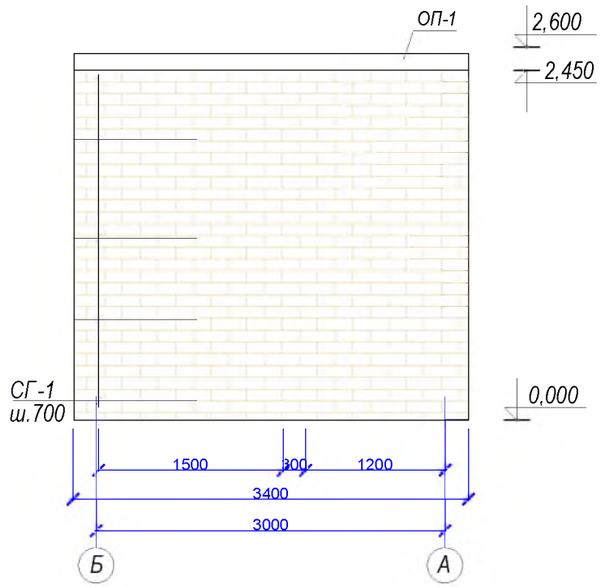



РАЗВЁРТКА СТЕН ПО ОСИ "2-1 "

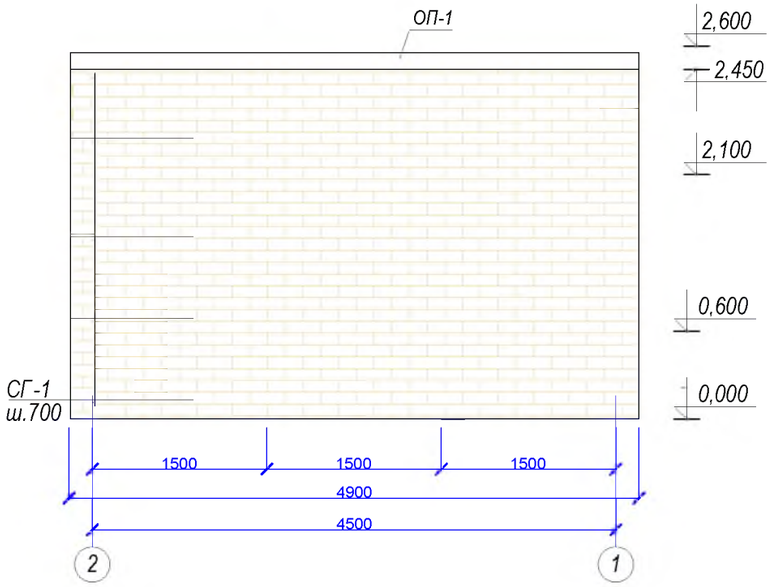


## СПЕЦИФИКАЦИЯ РАСХОД МАТЕРИАЛОВ СЕТКА СГ-1.

| Марка поз. | Обозначение | Наименование | | Кол | Масса ед., кг | |
|---|---|---|---|---|---|---|
| | | Сетка Сг-1 | | 90 | | |
| | | Сг-1 (на 1п.м) | | 1 | | |
| 1 | | Ø 5 Вр-1 | L=1000 | 5 | 0,155 | 0,775 |
| 2 | | Ø 3 Вр -1 | L= 370 | 3 | 0,052 | 0,05772 |
| | | | | | | |
| | | | | | | |

СГ-1 (на 1 п.м.)

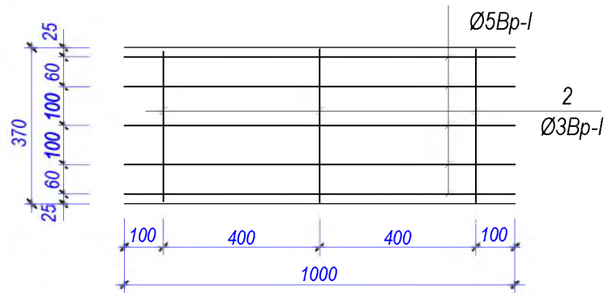


ПРИМЕЧАНИЕ:

1. Стены выполнить из кирпича толщ. 380 мм
2. Бетонирование сердечников выполняется после кладки кирпича .
3. Сетка горизонтальная СГ-1, ставить после 2 ряда кладки, далее шагом 700мм

Согласовано

Взамен инв.

Подпись и дата

Инв. подл


AC

| Изм. | Кол.уч. | Лист | № док. | Подп. | Дата | AC |
|---|---|---|---|---|---|---|
| | | | | | | "Баркарорсозии пойгоххои обкашии Лохур-0,Лохур-1,Лохур-2 ва Лохур-3 дар нохияи Рудаки" |
| Разработ. | | Фрайдунпоев О. | | | | Насосной станции Лохур-1. Архитектурно-строительная часть. |
| ГИП | | Шомили У. | | | | |
| Нач. отдел | | Шомили У. | | | | Дежурное помещение. Фрагмент армирование перемычек. Спецификация расхода материалов |
| Норм. контр. | | Хайбаров С. | | | | |


| Стадия | Лист | Листов |
|---|---|---|
| РП | 9 | 11 |

ГУП "Проектный Институт "Точикгипроводхоз" Душанбе - 2026

## 3-3

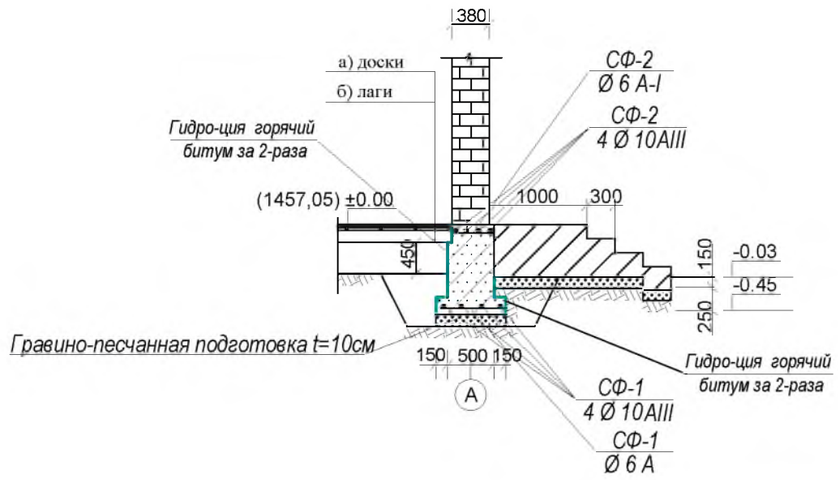



## 4-4

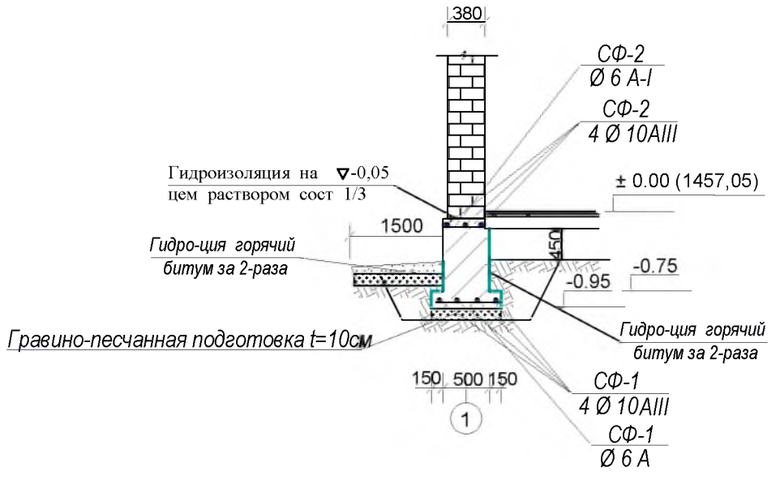



## СПЕЦИФИКАЦИЯ РАСХОД МАТЕРИАЛОВ НА КОНСТРУКЦИИ ФУНДАМЕНТОВ ФЛ - 1

| Марка поз. | Обозначение | Наименование | Кол | Масса ед., кг | |
|---|---|---|---|---|---|
| | | Фундамент Фл - 1 | 15,0 | | п.м |
| Сф - 1 | | Сф - 1 ( на 1 п. м) | | | |
| 1 | | Ø 10 A III L= 1000 | 4 | 0,617 | 2,47 |
| 2 | | Ø 6 A I L= 700 | 5 | 0,222 | 0,777 |
| | | | | | |
| | | Фундамент Фл - 1 | 15,0 | | п.м |
| Сф - 2 | | Сф - 2 ( на 1 п. м) | | | |
| 1 | | Ø 10 A III L= 1000 | 3 | 0,617 | 1,851 |
| 2 | | Ø 6 A I L= 400 | 5 | 0,222 | 0,444 |

## Сетка СФ-1 (на 1 пог. м.)

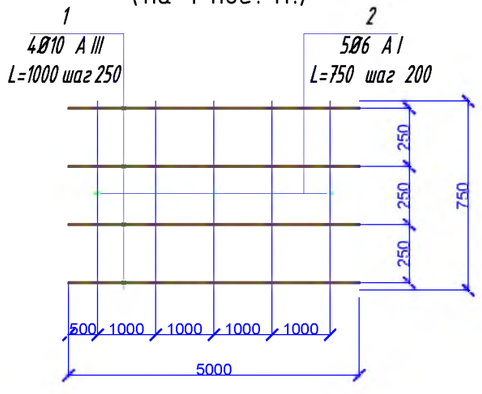


## Сетка Сф-2 (на 1 пог.м.)

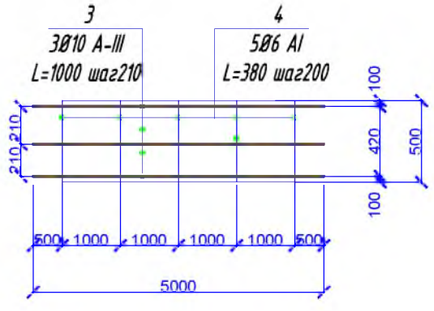


Согласовано

Взамен инв.


Подпись и дата

Инв. подл


АС

| Изм. | Кол.уч | Лист | № док | Поди | Дата | Восстановление насосной станции "Лохур-1" Архитектурно-строительная часть Дежурное помещение. Разрезы 3-3 и 4-4. Спецификация | Лист 10 |
|---|---|---|---|---|---|---|---|


## ФРАГМЕНТ АРМИРОВАНИЕ ПЕРЕМЫЧЕК ПРМ - 2. (1шт)

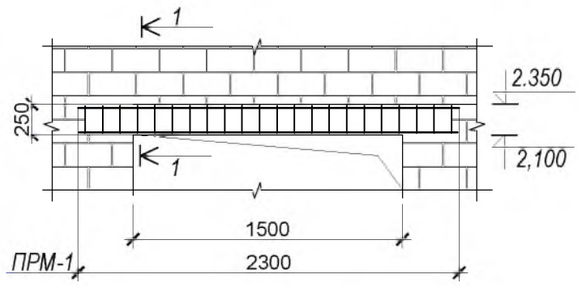



## ФРАГМЕНТ АРМИРОВАНИЕ ПЕРЕМЫЧЕК ПРМ - 2. (3шт)

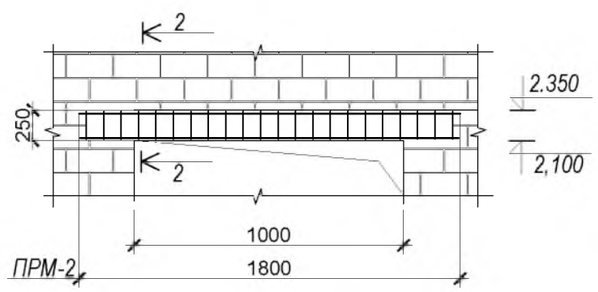



## ПРМ - 1 (1-1)

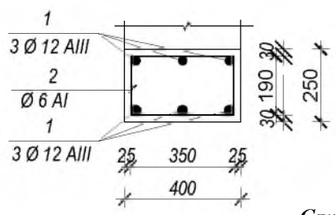


## ПРМ - 2 (2-2)

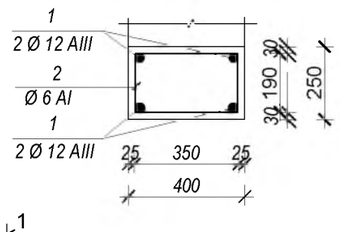


## Слуховое окно

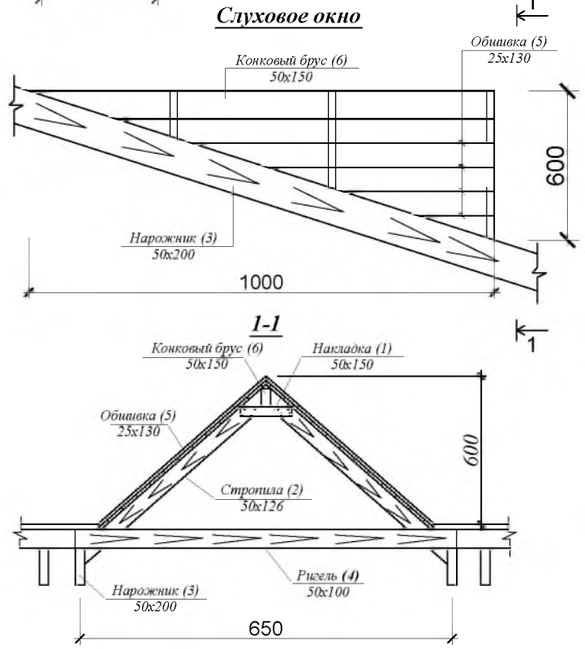


## ПРИМЕЧАНИЕ

1. Для повешения плотности бетона он должен подвергаться уплотнит с помощью вибратором
2. Бетонирование сердечник и балок должен выполнить непрерывно
3. Арматуры вязать вязальной проволокой во всех пересечениях
4. Сварные соединения стержней по длине выполнить с разбежкой не менее 1 м.
5. Данный лист рассматривать совместно с листом КЖ

## СПЕЦИФИКАЦИЯ РАСХОД МАТЕРИАЛОВ ПЕРЕМЫЧЕК

| Марка поз. | Обозначение | Наименование | | Кол | Масса ед., кг | |
|---|---|---|---|---|---|---|
| | | Перемычек монолитная Прм-1 | | 2 | | шт. |
| Прм - 1 | | Прм-1 (на 1 шт. ) | | | | |
| 1 | | Ø 12 A III | L= 2300 | 6 | 0,888 | 12,25 |
| 2 | | Ø 6 A I | L= 1080 | 12 | 0,222 | 2,90 |
| | | Бетон кл. В - 15 | | | 0,23 | м³ |
| | | Перемычек монолитная Прм-2 | | 1 | | шт. |
| Прм - 2 | | Прм-2 (на 1 шт. ) | | | | |
| 1 | | Ø 12 A III | L= 1800 | 4 | 0,888 | 6,40 |
| 2 | | Ø 6 A I | L= 1080 | 9 | 0,222 | 2,16 |
| | | Бетон кл. В - 15 | | | 0,18 | м³ |

## Спецификация слуховых окон

| № п/п | Наименование | Сечение мм х мм | Колич. шт. | Длина в м. | | Объём м³ | Примеч. |
|---|---|---|---|---|---|---|---|
| | | | | на один | всего | | |
| | | Расход на 1 слуховое окно | | | 2шт | | |
| 1 | Накладка | 50x150 | 1 | 0.30 | 0.30 | 0.002 | |
| 2 | Стропила | 50x126 | -- | -- | - | - | |
| 3 | Нарожник | 50x200 | 2 | 1,3 | 2,6 | 0,026 | |
| 4 | Ригель | 50x100 | 1 | 0,8 | 0,8 | 0,004 | |
| 5 | Обшивка | 25x130 | -- | -- | 10,0 | 0,032 | |
| 6 | Коньковый брус | 50x150 | 1 | 1,2 | 1,2 | 0,036 | |

АС

| Изм. | Кол. уч | Лист | № док. | Подп. | Дата | Восстановление насосной станции "Лохур-1" Архитектурно-строительная часть Дежурное помещение. Перемычки ПРМ-1 и 2. Спецификация расход материалов ОП-1. | Лист 11 |
|---|---|---|---|---|---|---|---|