АГЕНТСТВО ПО МЕЛИОРАЦИИ И ИРРИГАЦИИ
ПРИ ПРАВИТЕЛЬСТВЕ РЕСПУБЛИКИ ТАДЖИКИСТАН

ГУП "ПРОЕКТНЫЙ ИНСТИТУТ
"ТАДЖИКГИПРОВОДХОЗ"

РАБОЧИЙ ПРОЕКТ

"Баркарорсозии пойгоххои обкашии Лохур-0,Лохур-1,Лохур-2 ва Лохур-3 дар нохияи Рудаки"

АЛЬБОМ-1

Насосной станции Лохур-1.
Технологическая часть (ТХ)

ДУШАНБЕ-2026

АГЕНТСТВО ПО МЕЛИОРАЦИИ И ИРРИГАЦИИ
ПРИ ПРАВИТЕЛЬСТВЕ РЕСПУБЛИКИ ТАДЖИКИСТАН

ГУП "ПРОЕКТНЫЙ ИНСТИТУТ
"ТАДЖИКГИПРОВОДХОЗ"

РАБОЧИЙ ПРОЕКТ

"Баркарорсозии пойгоххои обкашии Лохур-0,Лохур-1,Лохур-2 ва Лохур-3 дар нохияи Рудаки"

АЛЬБОМ-1

Насосной станции Лохур-1.
Технологическая часть (ТХ)

ГЛ. ИНЖЕНЕР ИНСТИТУТА: ХАЙБАРОВ С.

ГЛ. ИНЖЕНЕР ПРОЕКТА: ШОМИЛИ У.

ДУШАНБЕ-2026

Таб. 1

Ведомость основных комплектов рабочих чертежей		
Обозначение	**Наименование**	**Примечание**
1	2	3
.ПЗ	Пояснительная записка	Книга-1
ТГИ	Инженерно-топогеодезический изысканий	Книга-2
ИГИ	Инженерно-геологический и гидрогеологичекий изысканий	Книга-3
ТХ	**Насосной станции Лохур-1.** Технологическая часть	Альбом-1
ГР	**Насосной станции Лохур-1.** Гидротехническое решение	Альбом-2
АС	**Насосной станции Лохур-1. Архитектурно-строительная часть**	Альбом-3
АС	**Насосной станции Лохур-1. Дежурное помещение Архитектурно-строительная часть**	Альбом-4
АС	**Насосной станции Лохур-1. Уборная на 1-го очко Архитектурно-строительная часть**	Альбом-5
ЭО	Электротехническая часть	Альбом-6
СМ	Сметная документация	Книга-4

Таб. 2

Ведомость рабочих чертежей основного комплекта **ТХ**		
Лист	**Наименование**	**Примечание**
1	2	3
1	Общие данные	
2	**План площадка насосной станции М1:500. Экспликация и** ведомость объёмов работ.	
3	**План размещение гидромеханического оборудование насосной станции М1:100.**	
4	**Разрез в осях 1 -2. М1:100. Ведомость объёмов демонтажных работ**	
5	Характеристика насоса типа KQSN800-M17-625	
6	Монтажный чертеж насоса KQSN800-M17-625	
7	Характеристика насоса типа KQSN700-M9J-869	
8	Монтажный чертеж насоса KQSN700-M9J-869	
9	**Фундамент под агрегат.Ведомость объёмов работ**	
10	**План насосной станции. План дренажная система. М1:100**	
11	**Установочный чертёж дренажного-насоса. Спецификация**	
12	Конструкция камера обратного клапана. **Ведомость объёмов работ. Спецификация.**	
13	Конструкция колодец обратного клапана	

Настоящий проект выполнен в соответствии с
дествующими нормами и правилами,
в том числе по взрыво - пожарной безопасности.

Гл. инженер проекта Шомили У.

Таб.3

Ведомость ссылочных и прилагаемых документов		
Обозначение	Наименование	Примечание
	Ссылочные документы	
ГОСТ 10704-91	Трубы металлические	
ГОСТ 9466-75	Электроды для дуговой сварки сталей и наплавки	
	классификация и общие технические условия	
ГОСТ 19903-74	Лист стальная	
30ч906бр	Задвижки с электроприводом	
ГОСТ 8509-93	Уголки стальные горячекатаные равнопрочные	
	Прилагаемые документы	
ТХ.СО-1	**Спецификация основного оборудования насосной станции**	2-листов

						ТХ
						"Баркарорсозии пойгоххои обкашии Лохур-0,Лохур-1,Лохур-2 ва Лохур-3 дар нохияи Рудаки"
Изм.	Кол.уч.	Лист	№ док.	Подп.	Дата	
Разработ.		Фрайдуншоев О.				Насосной станции Лохур-1. Технологическая часть (ТХ).
ГИП		Шомили У.				
Нач. отдел		Шомили У.				
Норм. контр.		Хайбаров С.				Общие данные.

Стадия	Лист	Листов
РП	1	12

ГУП "Проектный Институт "Точикгипроводхоз" Душанбе - 2026

Согласовано


Взамен инв.

Подпись и дата

Инв. подл

План площадка насосной станции Лохур-1 II-го подъема

М1:500

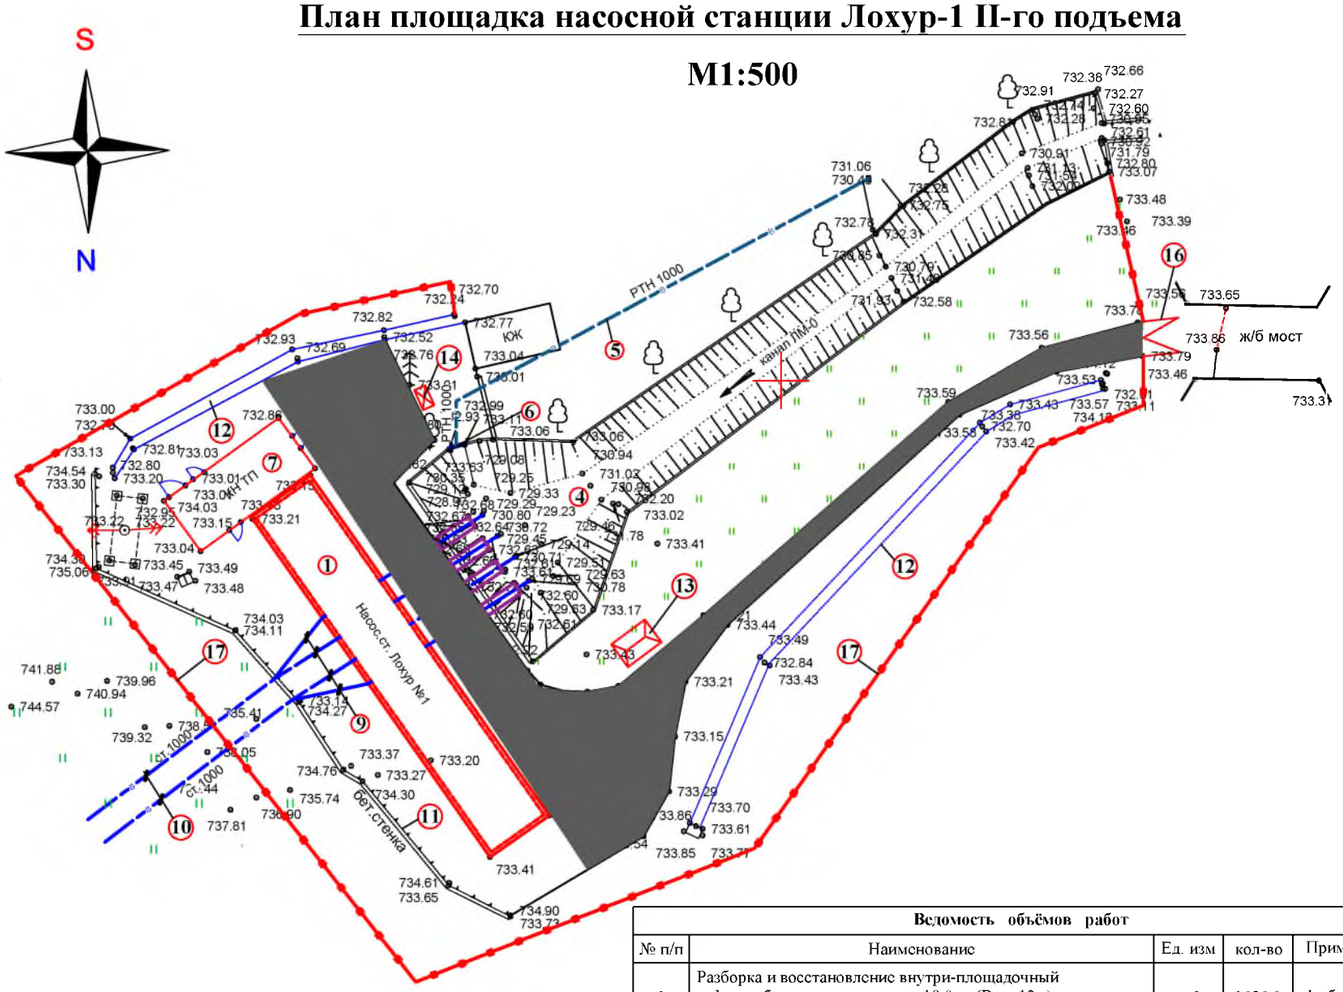

Экспликация здании и сооружении

№ п/п	Наименование	Ед. измер.	Кол-во	Примечание
1	Здание насосной станции раз:7,80х45,0м	шт	1,0	Существующий подлежит восстановление
2	Всасывающий трубопровод Ø=1000мм, (4-нитки)	пм	52,0	Существующий сохраняется
3	Служебная площадка раз:1,3х4,40м	шт	4,0	Существующий подлежит восстановление
4	Аванкамера раз: 9,0х18,0м	шт	1,0	Существующий подлежит восстановление
5	Сбросной труба РТН Ø=1000мм	пм	55,0	Существующий сохраняется
6	Сбросной затвор ГС 170х150см	шт	1,0	Существующий подлежит восстановление
7	Здание трансформаторная подстанция раз: 6,70х15,0м	шт	1,0	Существующий подлежит восстановление
8	Внутри площадочная подъездная асфальтная дорога Зср=4,0-26,0м	пм	282,0	Существующий подлежит восстановление
9	Напорный водовод D=1000мм (от здание НС до точ. подключение 4-нитки)	пм	34,0	Существующий сохраняется
10	Напорный водовод D=1000мм (от точ. подключение до напорный бассейн 2-нитки)	пм	542,0	Существующий сохраняется
11	Бетонная стенка t=40см	пм	70,0	Существующий сохраняется
12	Бетонный лоток ЛР-100	пм	108,0	Существующий сохраняется
13	Дежурное помещение раз: 3,5 х 4,0м	шт	1,0	Проектируемый
14	Уборная на 1-о очко раз:1,30х2.35х3.0м	шт	1,0	Проектируемый
15	Мусорный контейнер	шт	2,0	Проектируемый
16	Металлическая ворота В=4,0м,Н=2,0м	шт	1,0	Проектируемый
17	Ограждение территории	пм	251,0	Проектируемый

Ведомость объёмов работ

№ п/п	Наименование	Ед. изм	кол-во	Примечание
1	Разборка и восстановление внутри-площадочный асфальтобетонная покрытия t=10,0см (Вср=12м) с учетом площадка НС	м²	1656.0	Lоб=138,0м
2	Устройства основания автодорога из гравийно песчаной смеси t=10см - щебня t=5см	м² м²	1656.0	
3	Асфалтобетонная покрытия крупнозернистый t=6,0см мелкозернистый t=4,0см	м² м²	1656.0	
4	Установка сетчатое ограждение территории В=2,0м, Н=2,0м	пм/ шт	251/ 126	см. лист.
5	Приобретение и установка металлические ворота раз:4,0х2,0м	шт	1	см. лист.
6	Установка мусорного контейнера раз:3х2м	шт	2	Рыночное
7	Устройство здание дежурное помещение раз:3,0х4,5м	шт	1	см.лист-
8	Устройство здание уборное раз:1,3х1,8м	шт	1	см.лист-

УСЛОВНЫЕ ОБОЗНАЧЕНИЯ

- Напорный и всасывающий трубопровод
- Сбросной труба
- Сетчатое ограждение
- A — Внутри площадочная подъездная асфальтная дорога


Изм.	Кол.уч.	Лист	№ док.	Подп.	Дата	ТХ		
						"Баркарорсозии пойгоххои обкашии Лохур-0,Лохур-1,Лохур-2 ва Лохур-3 дар нохияи Рудаки"		
Разработ.		Файдуллоев О.				Насосной станции Лохур-1. Технологическая часть (ТХ).	Стадия	Лист	Листов
ГИП		Шомили У.					РП	2	12
Нач. отдел		Шомили У.				План площадка насосной станции М1:500. Экспликация и ведомость объёмов работ.	ГУП "Проектный Институт "Точикгипроводхоз" Душанбе - 2026		
Норм. контр.		Хайбаров С.							

Согласовано

Взамен инв.

Подпись и дата

Инв. подл

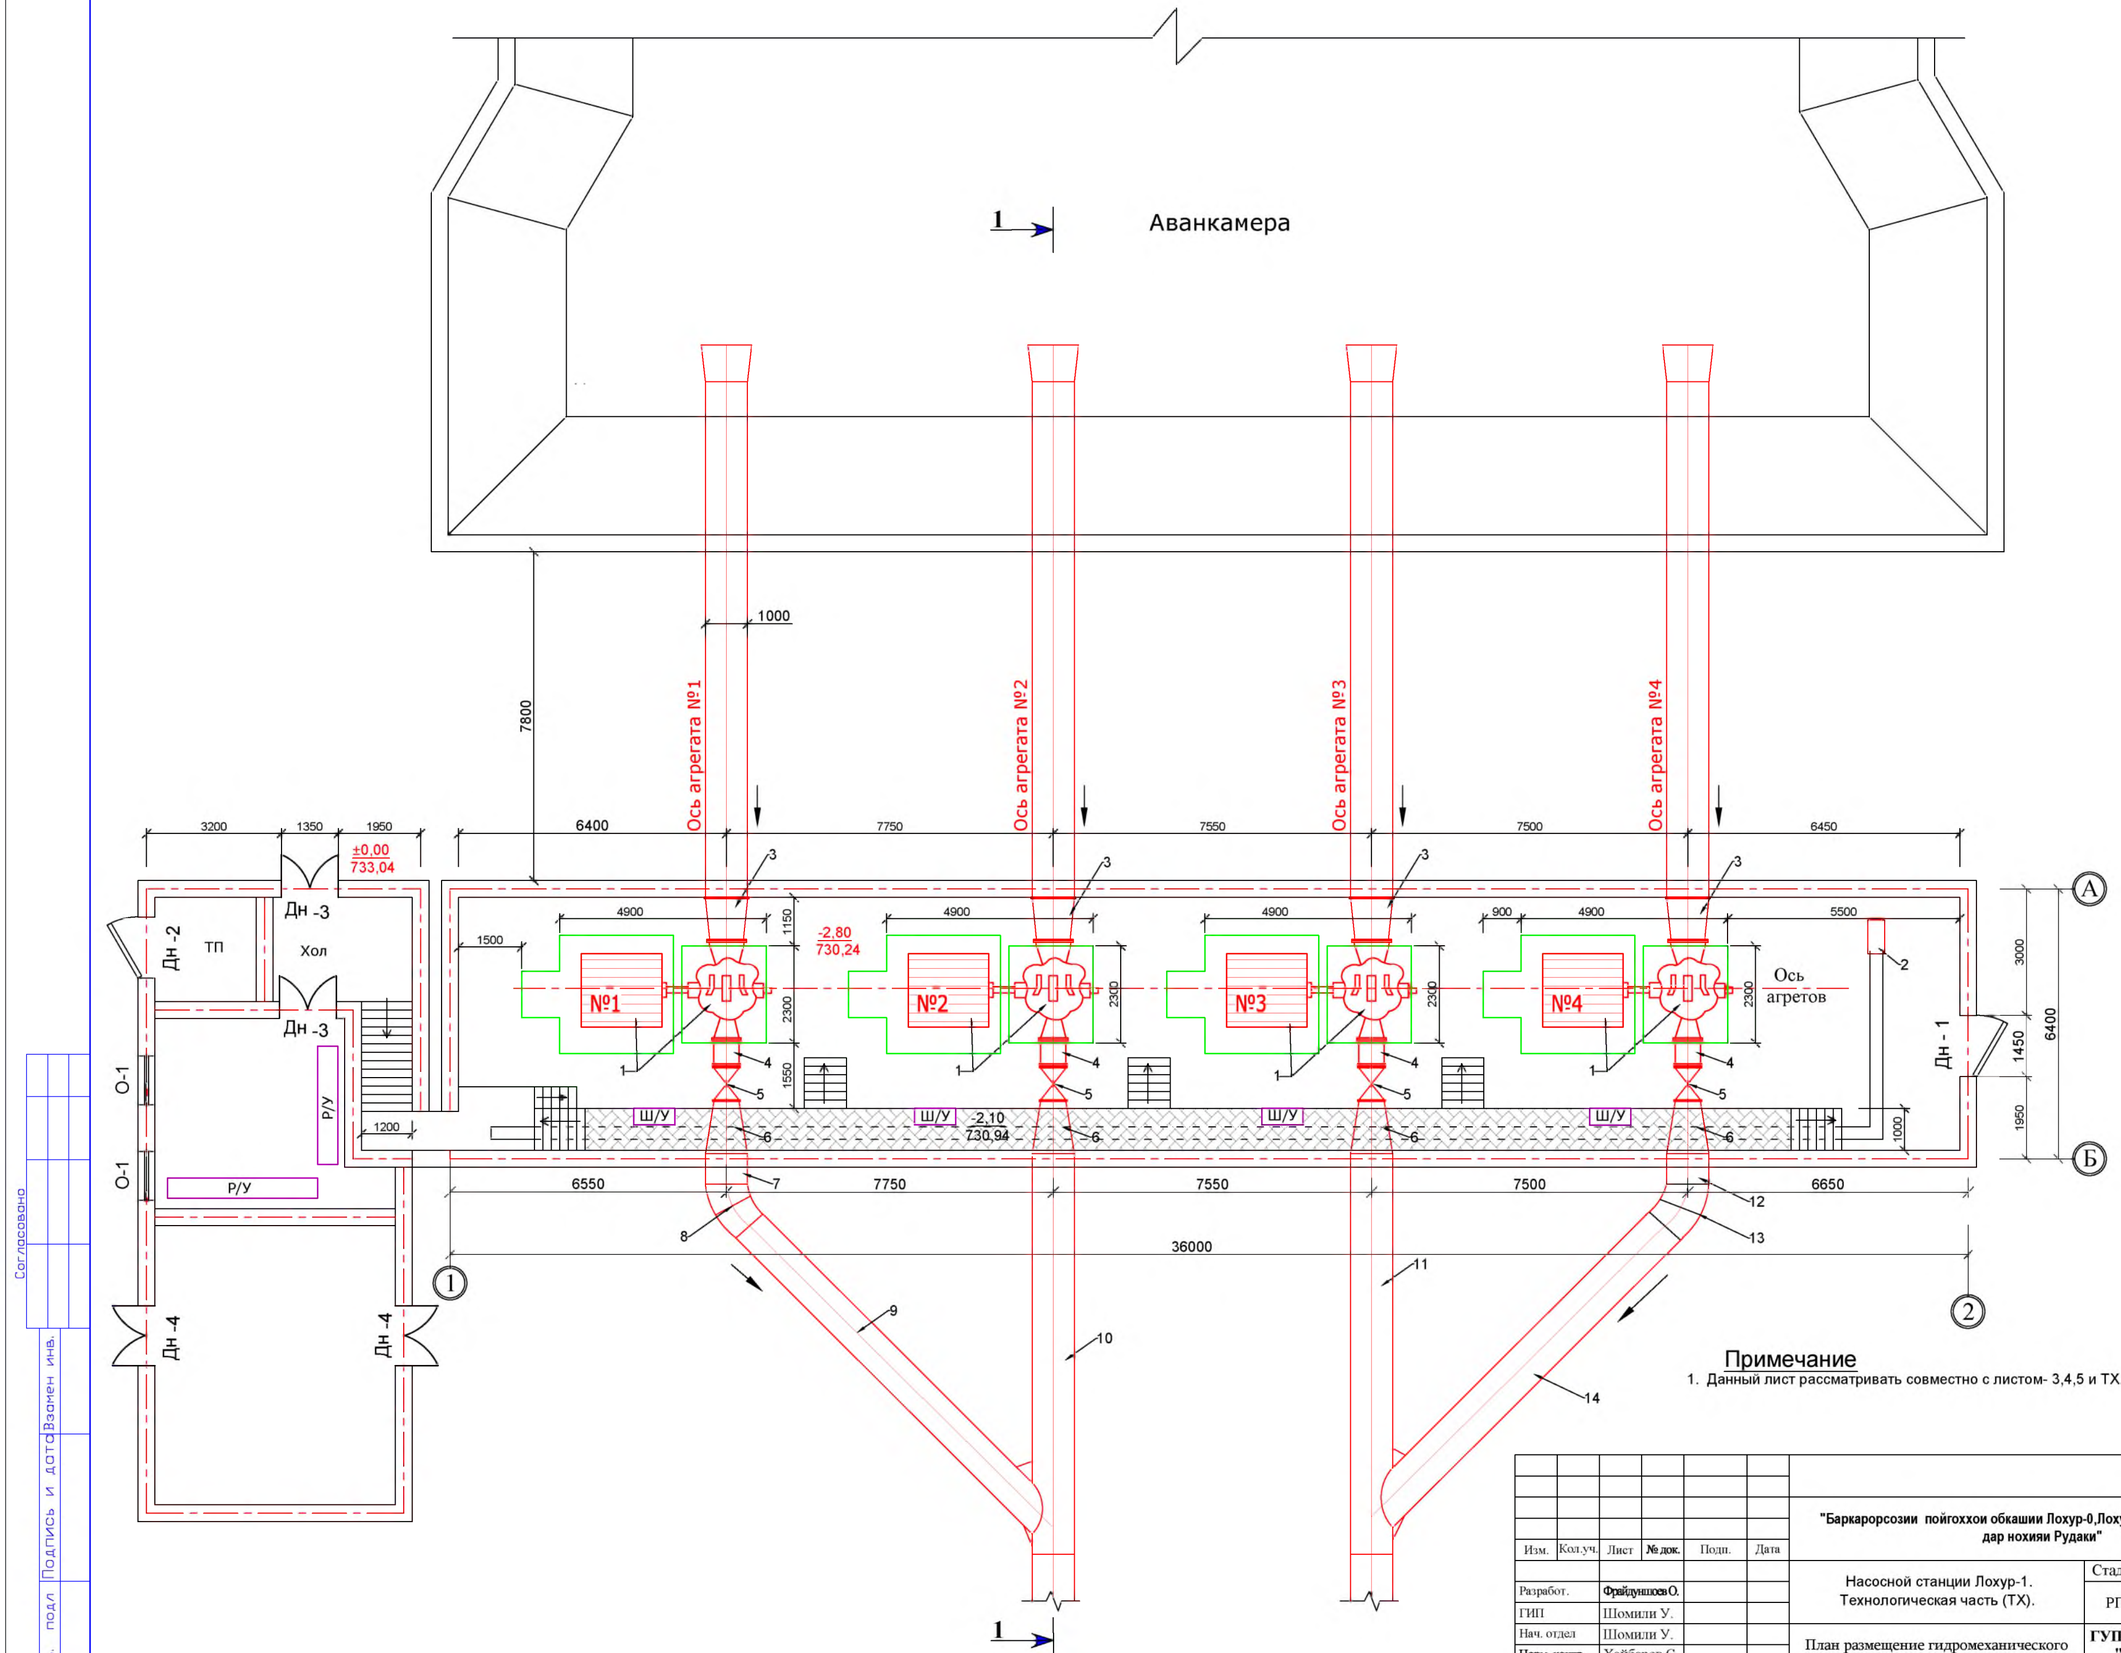

						ТХ
						"Баркарорсозии пойгоххои обкашии Лохур-0,Лохур-1,Лохур-2 ва Лохур-3 дар нохияи Рудаки"
Изм.	Кол.уч.	Лист	№ док.	Подп.	Дата	
Разработ.		Фрайдушоев О.				Насосной станции Лохур-1. Технологическая часть (ТХ).
ГИП		Шомили У.				
Нач. отдел		Шомили У.				
Норм. контр.		Хайбаров С.				План размещение гидромеханического оборудование насосной станции М1:100.


Стадия	Лист	Листов
РП	3	12

ГУП "Проектный Институт "Точикгипроводхоз" Душанбе - 2026


Согласовано

Инв. подл | Подпись и дата | Взамен инв.

РАЗРЕЗ в осях А –Б М1:100

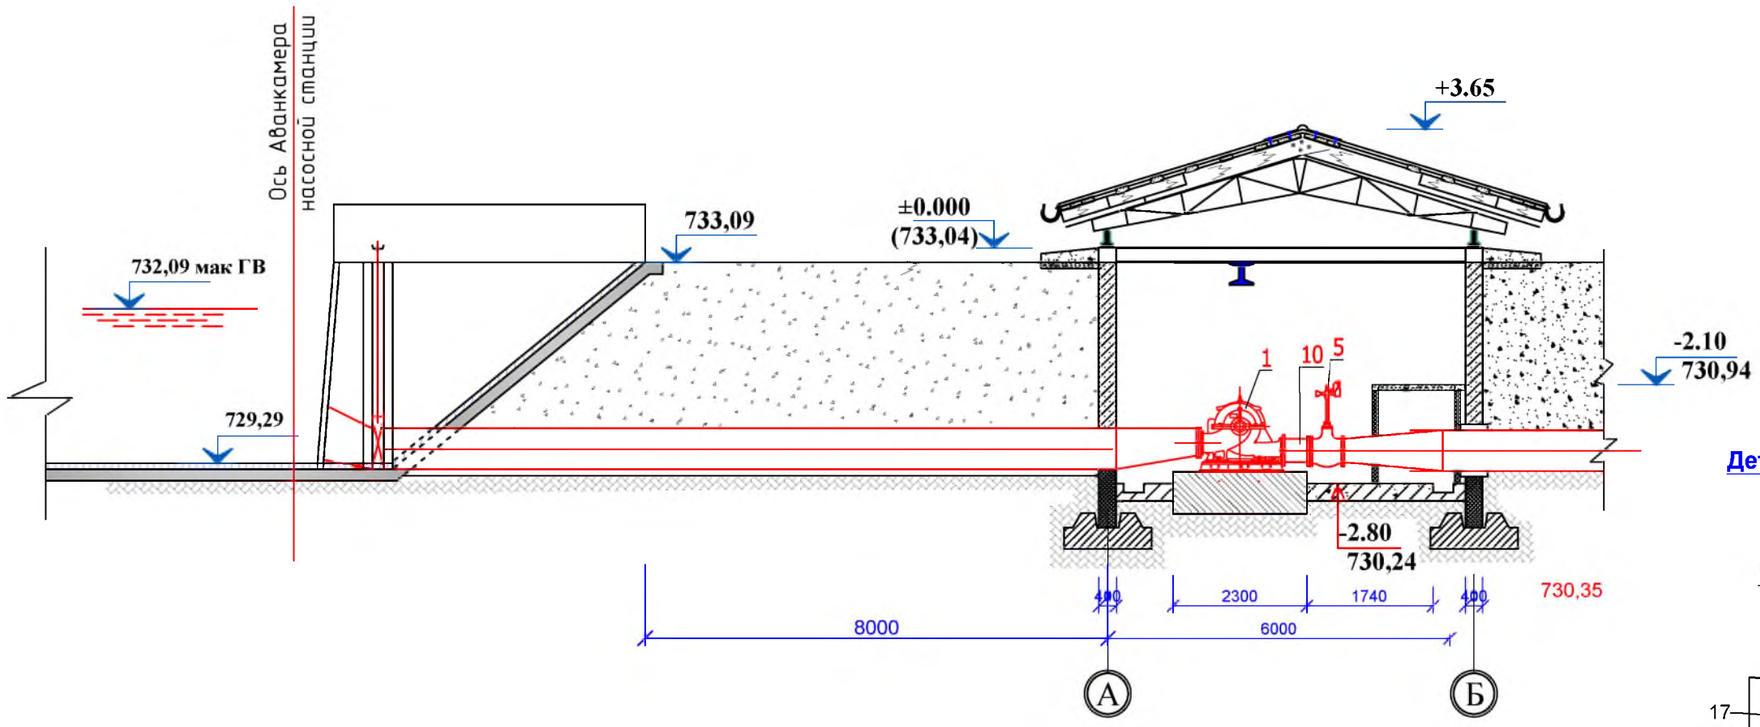

Деталировка колодец обратного клапана
М1:100

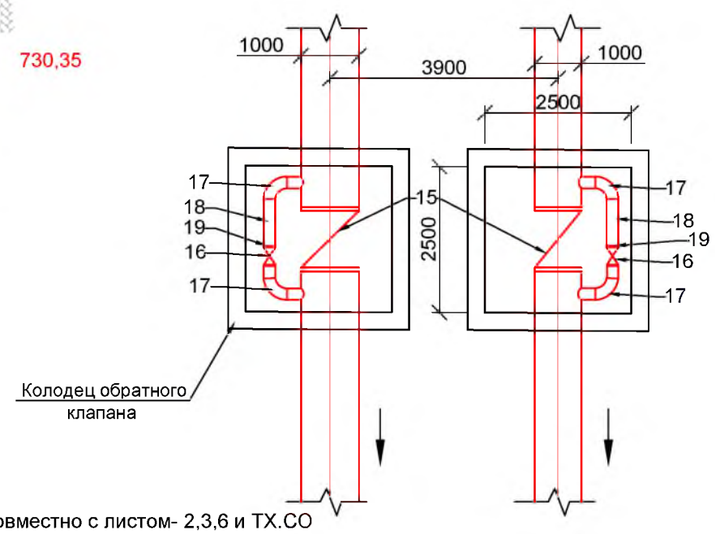

Ведомость объёмов демонтажных работ

№ П /П	Наименование	Ед. изм	Масса оборудования, кг	Примечание
1	Демонтаж насоса типа Д6300-80 (24НДс) 3-шт	кг	26298,0	Агрегат №1,2,3
2	Демонтаж электродвигатель мощность N=1000кВт 3-шт	кг	19500,0	Агрегат №1; №2 и №3
3	Демонтаж насоса типа Д4000-95 (22НДс) 1-шт	кг	4960,0	Агрегат №4
4	Демонтаж электродвигатель мощность N=1000кВт 1-шт	кг	3350,0	Агрегат №4
5	Демонтаж дренажный насос	шт	-	
6	Демонтаж сущ. переход косой Ø=800х1000мм, Ру=1,0МПа	шт	4,0	всасывающая линия
7	Демонтаж сущ. монтажная вставка Ø=600мм	шт	4,0	Напорная линия
8	Демонтаж сущ. задвижка фланцевая Ø=400мм, Ру=1,0МПа с электро-приводом	шт	4,0	Напорная линия
9	Демонтаж существующий электрическсие щиты	шт	4,0	
10	Демонтаж сущ. металлический напорный трубопровод Øу=1000мм, (4-нитка от здание до точка соединение)	пм	42,0	
11	Разломка и разборка существующий фундамент под оборудование в ручную с вывозом на расстоянии до 1,0км	м³	37,03	

Примечание

1. Данный лист рассматривать совместно с листом- 2,3,6 и ТХ.СО
2. Нумерация позиции см.ТХ.СО.

						ТХ
						"Баркарорсозии пойгоххои обкашии Лохур-0,Лохур-1,Лохур-2 ва Лохур-3 дар нохияи Рудаки"
Изм.	Кол.уч.	Лист	№ док.	Подп.	Дата	
Разработ.		Фрайдунпося О.				Насосной станции Лохур-1. Технологическая часть (ТХ).
ГИП		Шомили У.				
Нач. отдел		Шомили У.				
Норм. контр.		Хайбаров С.				Разрез в осях 1 -2. М1:100. Ведомость объёмов демонтажных работ


Стадия	Лист	Листов
РП	4	12

ГУП "Проектный Институт "Точикгипроводхоз" Душанбе - 2026

Согласовано

Инв. подл | Подпись и дата | Взамен инв.

Характеристика насоса типа KQSN800-M17S-625

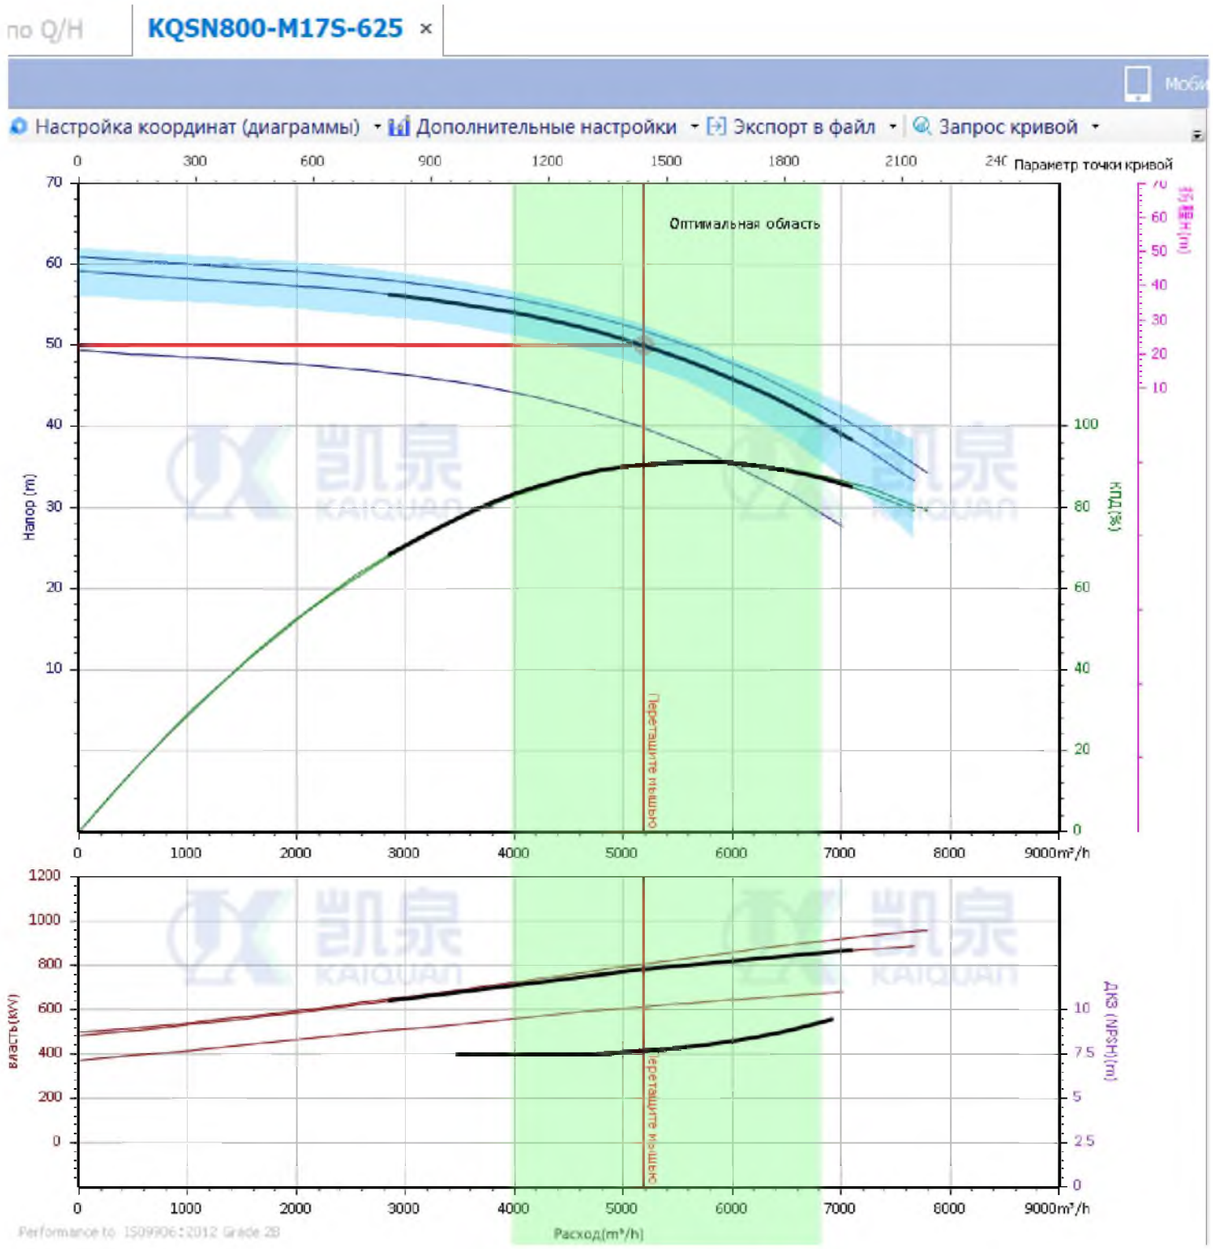

Согласовано

Взамен инв.

Подпись и дата


Инв. подл

						ТХ
						"Баркарорсозии пойгоххои обкашии Лохур-0,Лохур-1,Лохур-2 ва Лохур-3 дар нохияи Рудаки"
Изм.	Кол.уч.	Лист	№ док.	Подп.	Дата	
Разработ.		Фрайдуншоев О.				Насосной станции Лохур-1. Технологическая часть (ТХ).
ГИП		Шомили У.				
Нач. отдел		Шомили У.				
Норм. контр.		Хайбаров С.				Характеристика насоса типа KQSN800-M17-625


Стадия	Лист	Листов
РП	5	12

ГУП "Проектный Институт "Точикгипроводхоз" Душанбе - 2026


Монтажный чертёж агрегата KQSN800-M17 S-625

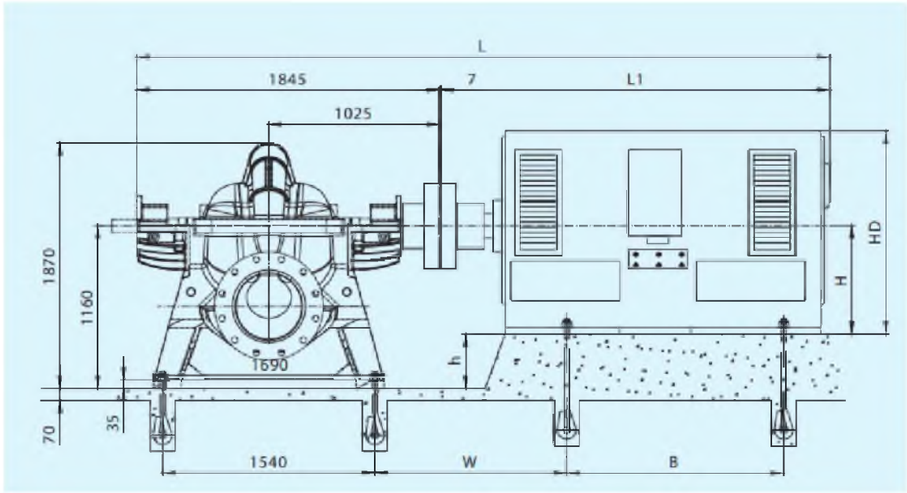

Вид с боку

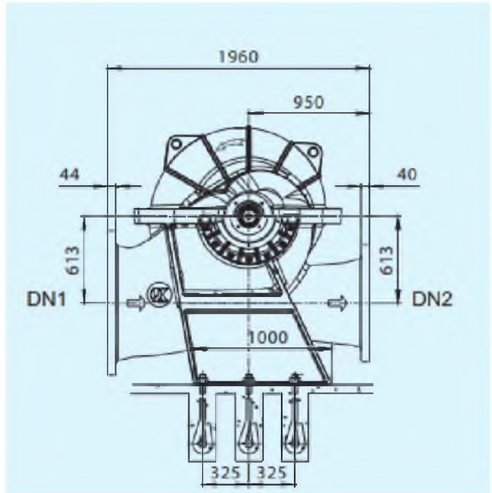


Рама агрегата типа KQSN800-M17S-625

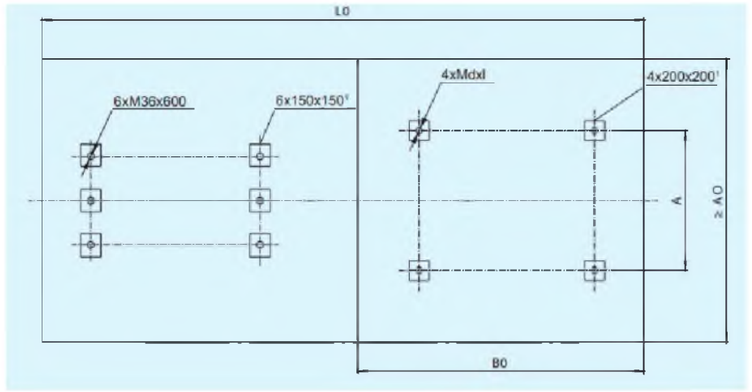


Типоразмер насоса	Диаметр рабочего колеса, мм	Подача (Q)		Напор (H), м	Частота вращения, об/мин	Мощность, кВт		Эффек-тивность (η), %	NPSHr, м	Масса, кг
		м³/ч	л/с			на валу насоса	электро-двигателя (P)			
KQSN800-M17S	625	3462	1603	55	990	615,0	1000	85	7,9	3848
		5769	1923	49		841,1		91, 5		
		6923	923	37		792,0		88		

Типоразмер насоса	Электродвигатель				Габаритные размеры, мм											Масса, кг
	Модель	Напряж., В	Степень защиты	Мощность, кВт	L	L1	L0	A0	B0	W	A	B	h	H	HD	dxl	Эл. двиг.
KQSN800 -M17S	YKK560-6	6k	IP54/IP44	900-1000	4612	2760	4800	2000	2400	1025	1000	1400	600	560	2200	M36X600	7850

Размеры фланцевого присоединения стороны всасывания DN1

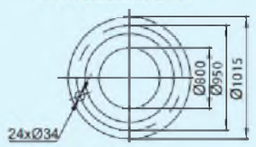

Размеры фланцевого присоединения стороны нагнетания DN2

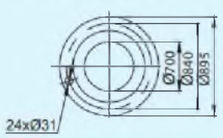

Взамен инв.

Подпись и дата

Инв. подл

Изм.	Кол.уч.	Лист	№ док.	Подп.	Дата
Разработ.		Фрайдуншоев О.			
ГИП		Шомили У.			
Нач. отдел		Шомили У.			
Норм. контр.		Хайбаров С.			

ТХ

"Баркарорсозии пойгоххои обкашии Лохур-0,Лохур-1,Лохур-2 ва Лохур-3 дар нохияи Рудаки"


Насосной станции Лохур-1. Технологическая часть (ТХ).

Стадия	Лист	Листов
РП	6	12

Монтажный чертеж насоса KQSN800-M17-625


ГУП "Проектный Институт "Точикгипроводхоз" Душанбе - 2026

Монтажный чертёж агрегата KQSN700-M9J-869

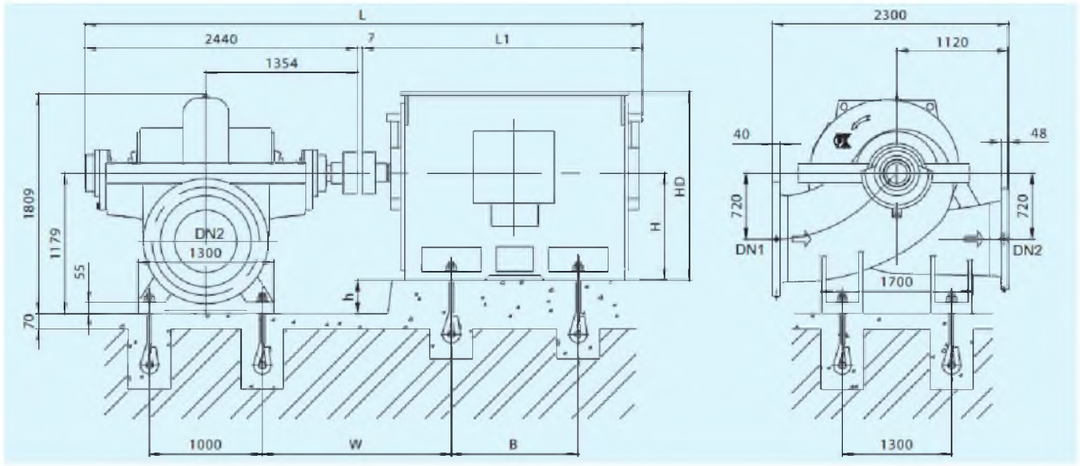

Вид с боку


Рама агрегата типа KQSN700-M9J-869

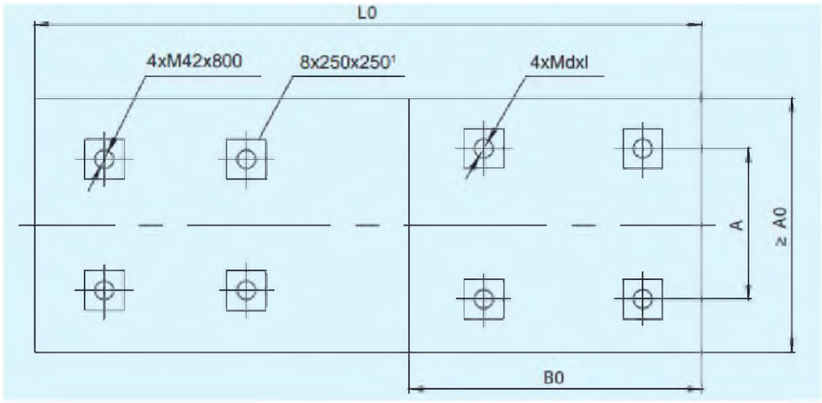


Типоразмер насоса	Диаметр рабочего колеса, мм	Подача (Q)		Напор (H), м	Частота вращения, об/мин	Мощность, кВт		Эффек-тивность (η), %	NPSHr, м	Масса, кг
		м³/ч	л/с			на валу насоса	электро-двигателя (P)			
KQSN700-M9J	799	1963	545	51	740	337,7	560	80,5	4,2	5402
		3272	909	44		451,6		86,0		
		3927	1091	37		488,2		82,0		

Типоразмер насоса	Электродвигатель				Габаритные размеры, мм												Масса, кг
	Модель	Напряж., В	Степень защиты	Мощность, кВт	L	L1	L0	A0	B0	W	A	B	h	H	HD	dxl	Эл. двиг.
KQSN700-M9J	Y500-8	6k	IP23	500–710	4989	2550	5000	1800	2500	1586	900	1250	580	500	1655	36x600	4500

Размеры фланцевого присоединения стороны всасывания DN1

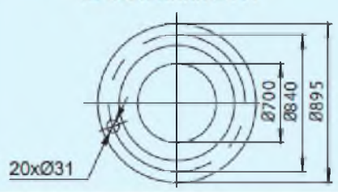

Размеры фланцевого присоединения стороны нагнетания DN2

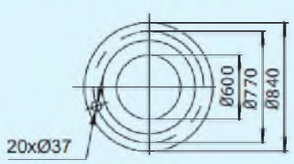

Взамен инв.

Подпись и дата


Инв. подл

						ТХ
						"Баркарорсозии пойгоххои обкашии Лохур-0,Лохур-1,Лохур-2 ва Лохур-3 дар нохияи Рудаки"
Изм.	Кол.уч.	Лист	№ док.	Подп.	Дата	
Разработ.		Фрайдуншоев О.				Насосной станции Лохур-1. Технологическая часть (ТХ).
ГИП		Шомили У.				
Нач. отдел		Шомили У.				
Норм. контр.		Хайбаров С.				Монтажный чертеж насоса KQSN700-M9J-869


Стадия	Лист	Листов
РП	8	12

ГУП "Проектный Институт "Точикгипроводхоз" Душанбе - 2026

План фундамента (б/м)

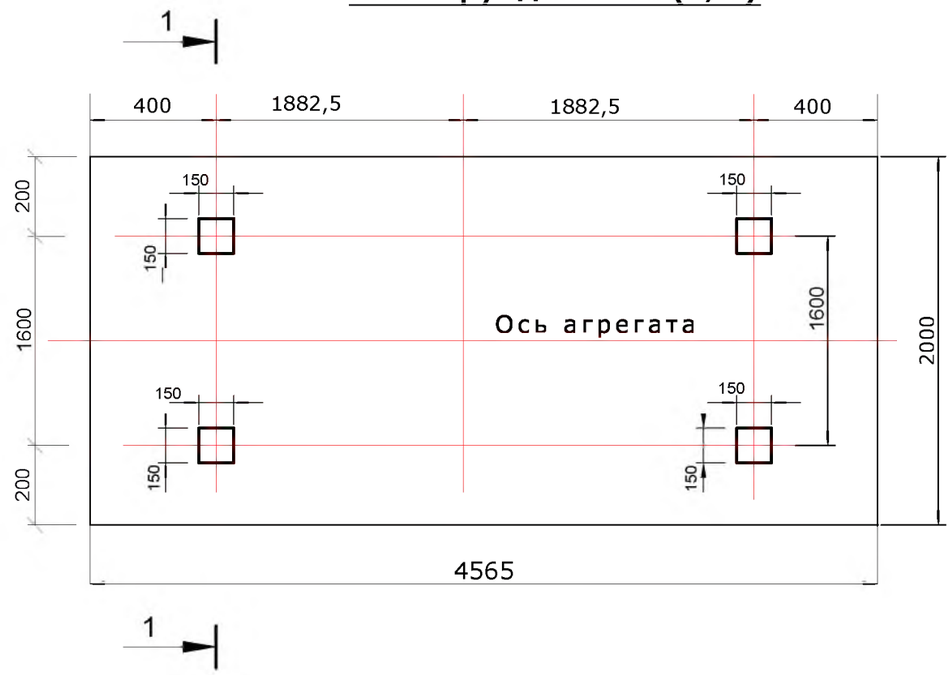

Разрез 1-1 (б/м)

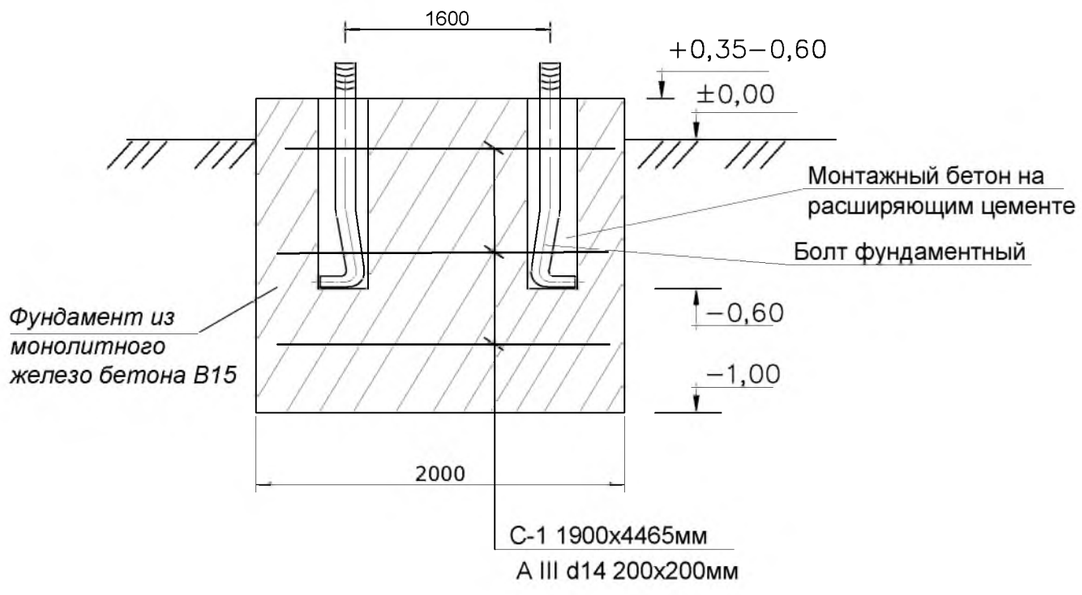

Ведомость объёмов работ дано на 1-го фундамента

N п/п	Наименование работ.	Ед изм	Кол-во	Примечание
1	Монолитный бетон В15 - F150 -W 6	м³	13,24	На 1 фундамент
2	Монтажный бетон на расширяющемся цементе	м³	0,10	На 1 фундамент
3	Болт фундаментный М30х600. ГОСТ 24379.1-80 шт.6	кг	27,30	На 1 фундамент
4	Гайка Ø30 ГОСТ 5927-80* шт. 4	кг	1,34	На 1 агрегат
5	Шайба Ø30 ГОСТ 24379.1-80 шт.4	кг	1,98	На 1 агрегат
6	Сетка С-1 раз:1090х2430 ячейки 200/200 из Арм-а AIII Ø14мм ГОСТ5781-82 3-шт (1-шт=102,85кг)	кг	308,55	На 1 агрегат
7	Шайба Ø30 ГОСТ 24379.1-80 шт.4	кг	9,50	На 1 агрегат

Всего - 4 шт

Примечание

1. Данный лист рассматривать совместно с листом ТХ-3,4,5
2. В сметы учитывать демонтаж, разломка и разборки существующие фундаментные агрегаты раз:2,30х4,9х1,0м -11,27м3х4шт=45,0м3
3. Местоположение отверстий под анкерные болты уточняются по полученному оборудованию
4. Анкерные болты необходимо прикрепить с арматурной сетки фундамента

Взамен инв.

Подпись и дата


Инв. подл

						ТХ
						"Баркарорсозии пойгоххои обкашии Лохур-0,Лохур-1,Лохур-2 ва Лохур-3 дар нохияи Рудаки"
Изм.	Кол.уч.	Лист	№ док.	Подп.	Дата	
Разработ.		Фрайдунпоев О.				Насосной станции Лохур-1. Технологическая часть (ТХ).
ГИП		Шомили У.				
Нач. отдел		Шомили У.				
Норм. контр.		Хайбаров С.				Фундамент под агрегат. Ведомость объёмов работ


Стадия	Лист	Листов
РП	9	12

ГУП "Проектный Институт "Точикгипроводхоз" Душанбе - 2026

План насосной станции
М1:100

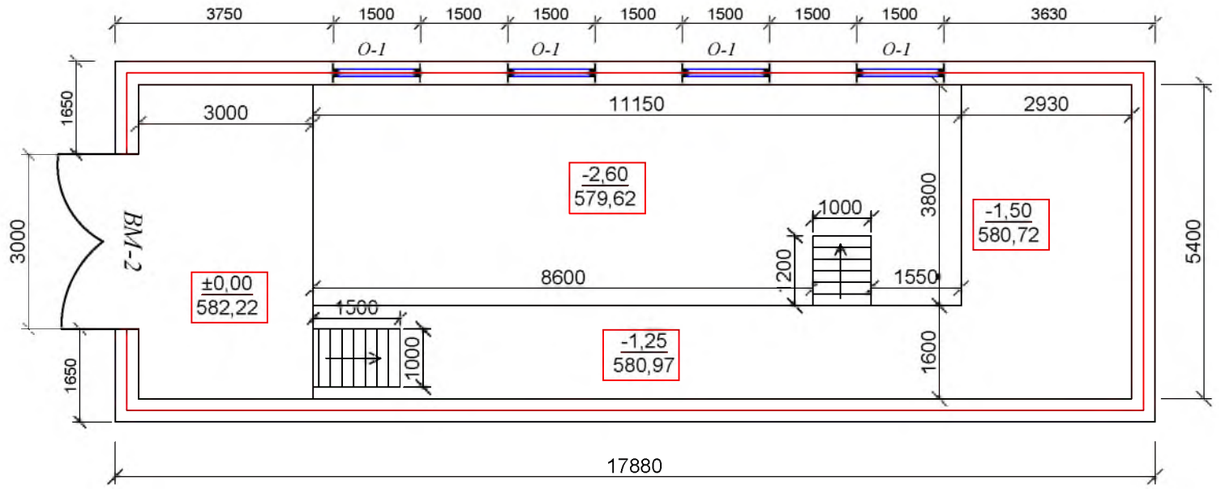

План дренажная система
М1:100

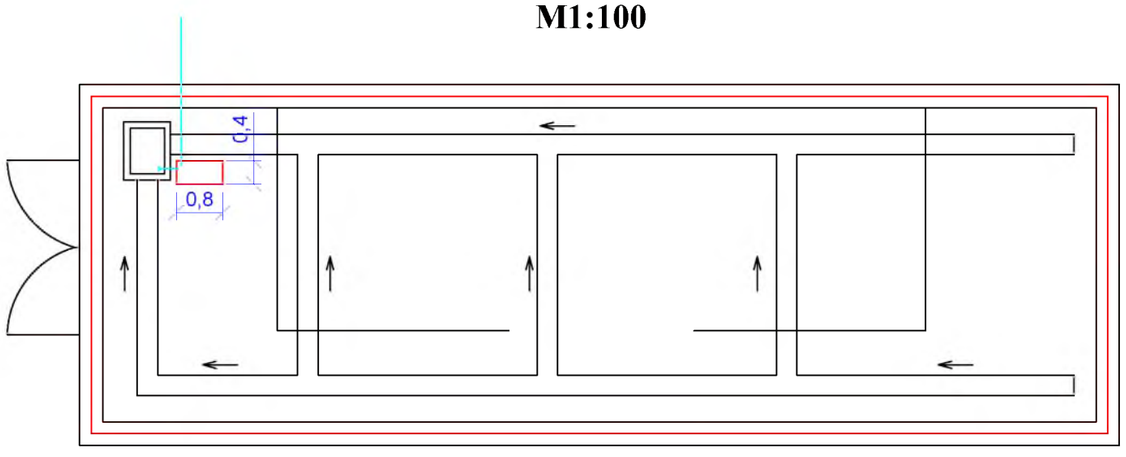

Примечание

1. Данный лист рассматривать совместно с листом- 2,3,6 и ТХ.СО

						ТХ
						"Баркарорсозии пойгоххои обкашии Лохур-0,Лохур-1,Лохур-2 ва Лохур-3 дар нохияи Рудаки"
Изм.	Кол.уч.	Лист	**№ док.**	Поди.	Дата	
						Насосной станции Лохур-1. Технологическая часть (ТХ).
Разработ.		**Фрайдунпоев О.**				
ГИП		Шомили У.				
Нач. отдел		Шомили У.				
Норм. контр.		Хайбаров С.				План насосной станции. План дренажная система. М1:100


Стадия	Лист	Листов
РП	10	12

ГУП "Проектный Институт "Точикгипроводхоз" Душанбе - 2026


Согласовано

Инв. подл | Подпись и дата | Взамен инв.

1-1

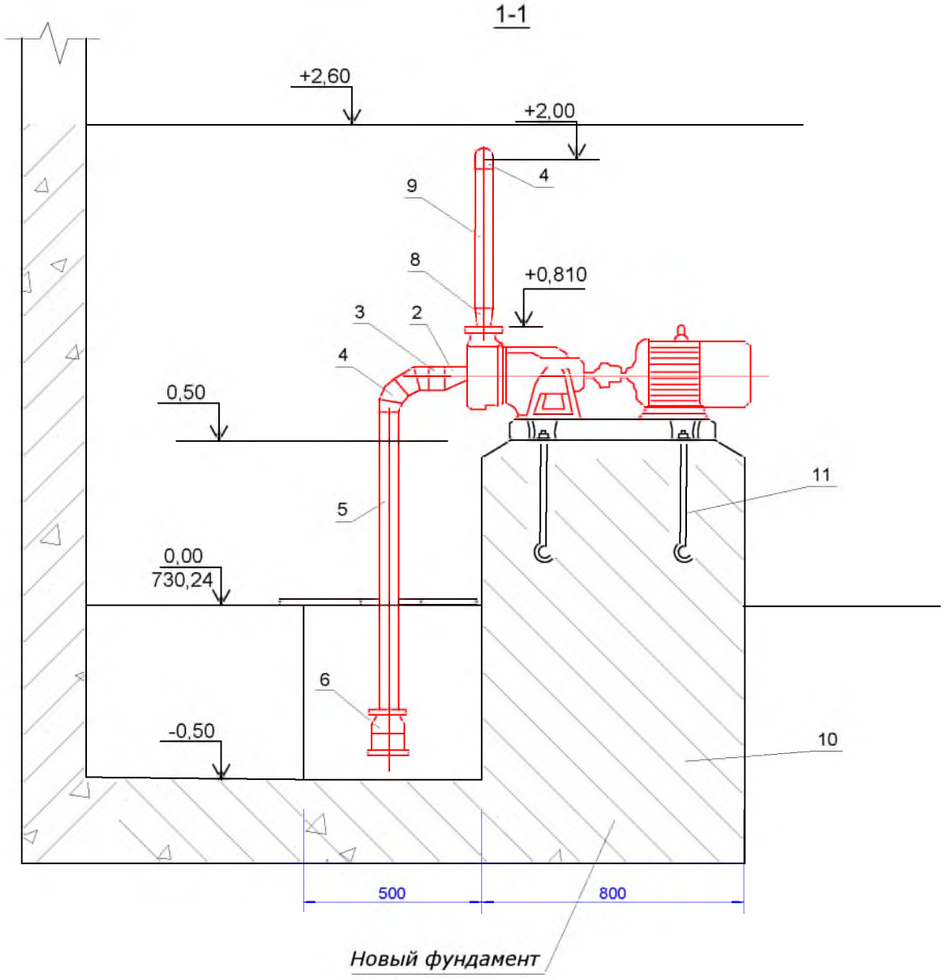

План

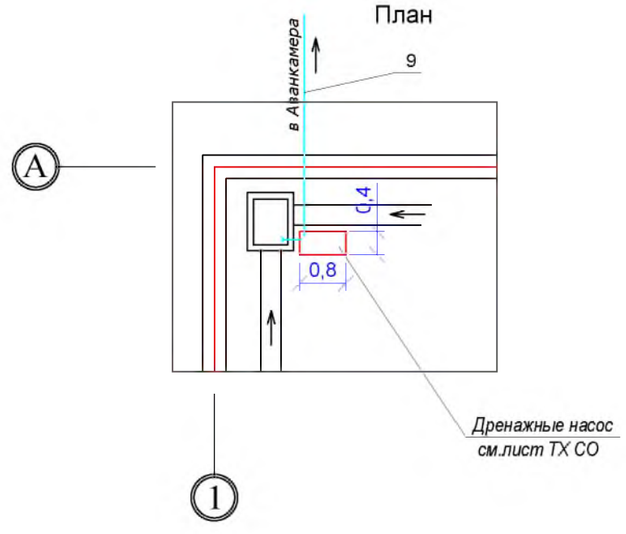

Спецификация

№№	Обозначение	Наименование	Кол-во	Масса ед.кг	Примечание
		Стандартные изделия			
1	ГОСТ 12817-80	Фланец 40-0,25МПа	1	1,04	
2		Муфты переходные 40х50мм	1	0,128	
3	ГОСТ 8957-75	Труба 50х3,0 **ГОСТ3262-75**	1		L=200,0мм
4	ГОСТ 12820-80	Отвод 90° 57х3,0	2	0,40	
5	ГОСТ 8946-75	Труба 50х3,0 **ГОСТ3262-75**	1		L=800,0мм
6		Приёмный клапан d=50мм	1		
7		Фланец 32-0,25МПа	1	1,04	
8		Муфты переходные 32х50мм	1		
9		Труба 50х3,0 **ГОСТ3262-75**	1		L=6200,0мм
10		Монолитный бетон В15	1		0,32м³
11		Анкерный болты М14	4		

Примечание:

1. Отметке ±0,00 соответствует отметка пола камеры 579,62

2. Дренажной насос с эл/двигателем включено в СО (поз 4)

						ТХ
						"Баркарорсозии пойгоххои обкашии Лохур-0,Лохур-1,Лохур-2 ва Лохур-3 дар нохияи Рудаки"
Изм.	Кол.уч.	Лист	№ док.	Подп.	Дата	
Разработ.		Фрайдунпосев О.				Насосной станции Лохур-1. Технологическая часть (ТХ).
ГИП		Шомили У.				
Нач. отдел		Шомили У.				
Норм. контр.		Хайбаров С.				Установочный чертёж дренажного-насоса. Спецификация

Стадия	Лист	Листов
РП	11	12

ГУП "Проектный Институт "Точикгипроводхоз" Душанбе - 2026

Согласовано


Взамен инв.

Подпись и дата

Инв. подл

План водопроводного колодца (2500x2500 mm)

Разрез 1 - 1

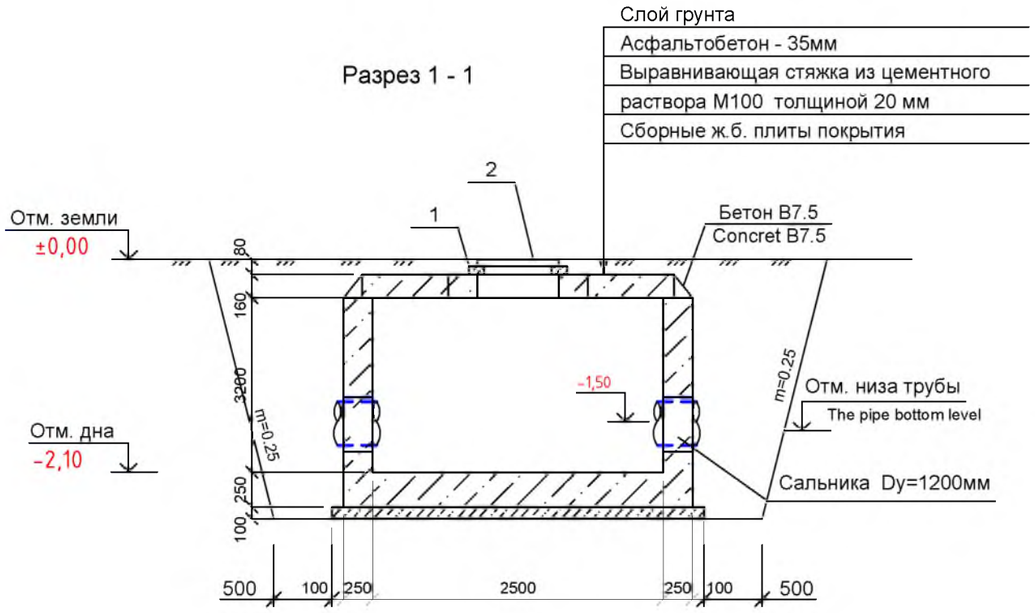

План котлована водопроводного колодца (2500x2500 mm)



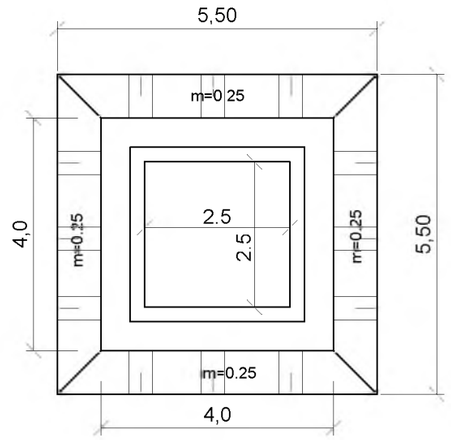


Схема расположения плит покрытия водопроводного колодца

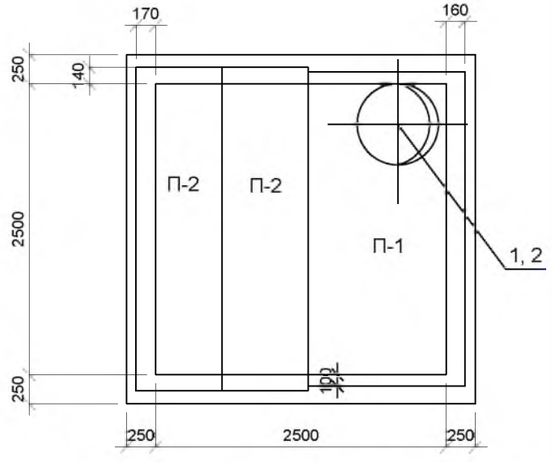

План водопроводного колодца

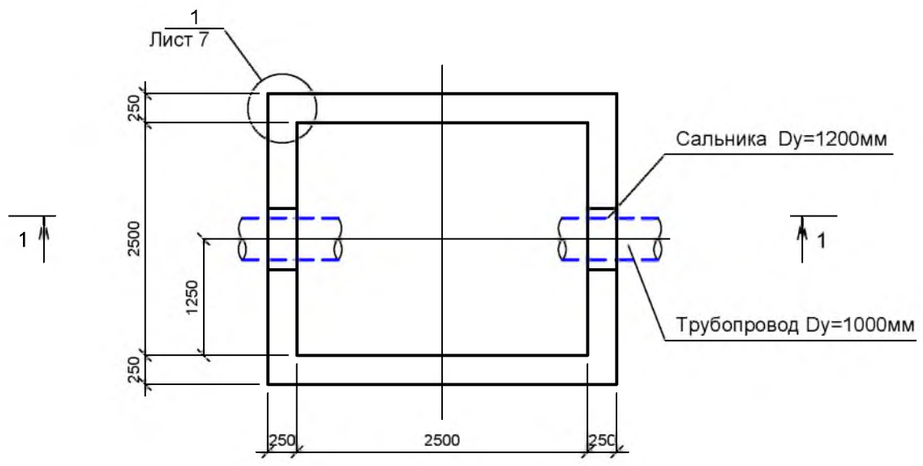

Спецификация плит покрытия

Марка	Обозначение	Наименование	Кол-во	Масса ед. кг.	Примеч.
	Сборные ж.б. конструкции Precast concrete structures				
П1	901-09-11.84, ал. V	Cover plate Плита покрытия П24-5Б	1	1450	
П2	3.006.1-2.87, вып. 2	Cover plate Плита покрытия П24д-5	2	930	
1	3.900-3, вып. 7	Support ring Кольцо опорное КЦО-1	1	50	
		Metal structures Металлические конструкции			
2	GOST 3634-99	Люк "Т" d=700 мм	1	69	

*** Ведомость объемов работ и спецификация дано на 1-шт всего-2шт

*** Данный лист рассматривается совместно с листами 3 и 7.

Ведомость объемов работ

№ ПП	Наименование	Ед. изм	Кол-во	Примечание
1	Разработка грунта II-кат	м³	67,0	5% Вручную
2	Обратная засыпка	м³	40,0	
3	Гидроизоляция битумом 2-раза по наружных поверхностям соприкасающийся с грунтом	м²	35,2	

						ТХ
						"Баркарорсозии пойгоххои обкашии Лохур-0,Лохур-1,Лохур-2 ва Лохур-3 дар нохияи Рудаки"
Изм.	Кол.уч.	Лист	№ док.	Подп.	Дата	
Разработ.		Фойдунпоев О.				Насосной станции Лохур-1. Технологическая часть (ТХ).
ГИП		Шомили У.				
Нач. отдел		Шомили У.				
Норм. контр.		Хайбаров С.				Конструкция камера обратного клапана Ведомость объёмов работ. Спецификация.

Стадия	Лист	Листов
РП	12	12

ГУП "Проектный Институт "Точикгипроводхоз" Душанбе - 2026


Согласовано


Взамен инв.

Подпись и дата

Инв. подл


Water supply manhole (2500x2500 mm)

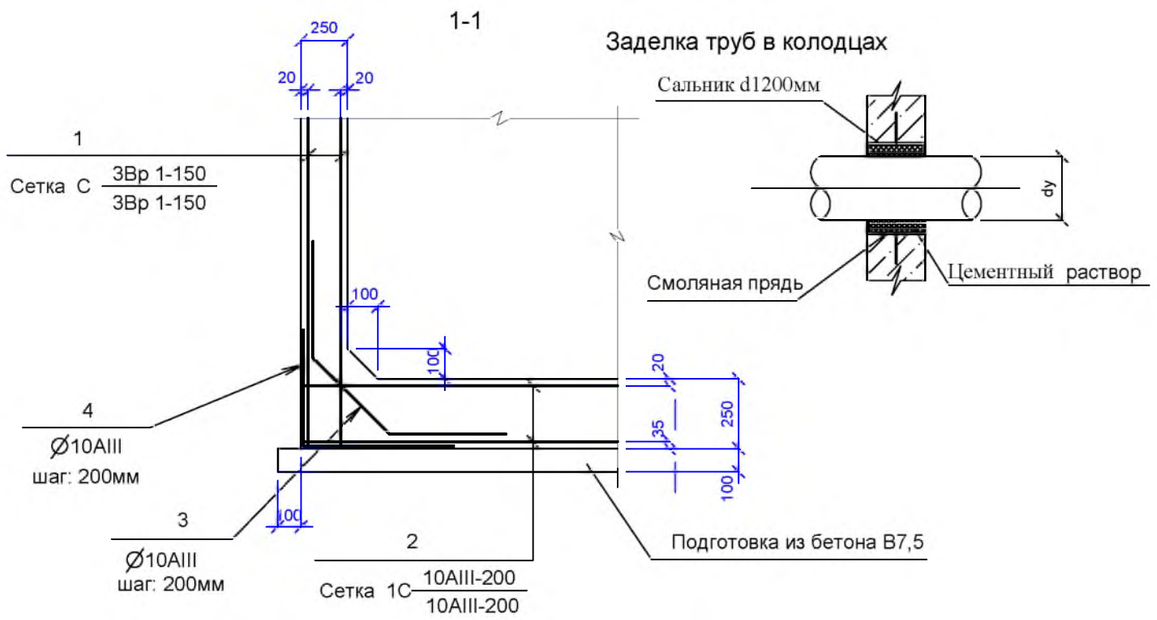

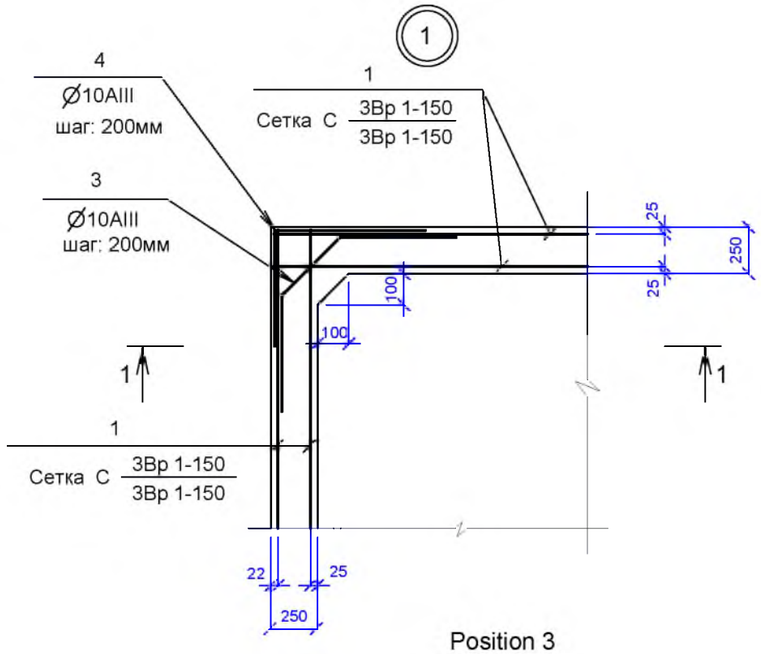


Position 3

Ø 10AIII

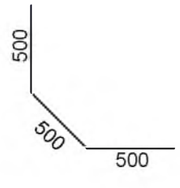

Position 4

Ø 10AIII

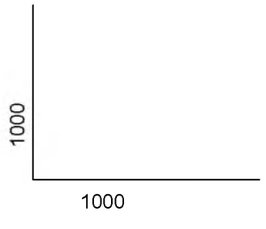

Спецификация на колодец Specification for the manhole

Поз. Position	Обозначение Designation	Наименование Name	Кол-во Number	Примеч. Remarks
		Сборочные единицы		
1	GOST 8478-81	Арм. сетка С 3Вр 1-150 / 3Вр 1-150	74,0 m2	60,0кг
2	GOST 23279-85	Арм. сетка1С 10AIII-200 / 10AIII-200	18,0 m2	111,06кг
3	GOST 5781-82*	Ø10AIII L=1500	84 pcs.	0,93 kg
4		Ø10AIII L=2000	96 pcs.	1,23 kg
5		Установка сальника d=1200мм	2,0	
		Материалы Materials		
		Concrete Бетон B15, W4, F100 (днище bottom)	2,25	m^3
		Concrete Бетон B15, W4, F100 (стенки wall)	8,80	m^3
		Concrete (preparation) Бетон B7,5, W4, F100 (подготовка)	1,02	m^3

Расход арматуры на колодец

N,N п/п	Наименование	Количество на колодец	Примеч.
1	Арматурная сталь Ø10AIII	307,8 kg	
2	,, Ø3BpI	60,0 kg	
	Итого Total	340,1 kg	

Примечание

1. Стены и днище колодца выполнить из бетона В15
2. Арматуру сеток в местах установки сальников вырезать и приварить к сальникам.
3. Узел 1 см.лист №6

ТК

Изм.	Кол.уч	Лист	№ док	Поди	Дата	Насосной станции Лохур-1. Технологическая часть (ТХ). Конструкция колодец обратного клапана	Лист 13

Согласовано

Взамен инв.

Подпись и дата

Инв. подл

Спецификация оборудования и материалов

№ № П/П	Наименование и техническая характеристика оборудования и материалов Завод-изготовитель (для импортного оборудования-страна, фирма)	Тип, марка оборудования, обозначение документа и опросного листа	Наимено-вание ед.изм.	Код	Код завода изготовителя	Цена единицы тыс.руб.	Кол- во	Масса единицы оборудования, кг	Примечание
	Оборудование								
1	Насос типа Д-горизонталные одно ступенчатые с раб.колесо Dк=615,8мм, корпус из высокопровочный чугун (ВЧ. 40-60) Q=5184м³/ч; H=50м, n=990.об/мин, (рабочий колесо насоса из нержавейший сталь) с электродвигателями мощностью N=1000 кВт. напряжение U=6000В; n=1000об/мин с учетом заводской рамы и транспортировкой до объекта и подготовка машин к испытанию сдачей под наладку и пуску для соединение к электросети **(агрегаты №1; №2 и №3 Левого вращение китайского производства)**	KQSN800-M17S-625 YKK560-6	шт				3,0	11698,0	35094,0кг
	Насос типа Д-горизонталные одно ступенчатые с раб.колесо Dк=862,8мм, корпус из высокопровочный чугун (ВЧ. 40-60) Q=3600м³/ч; H=50м, n=740.об/мин, (рабочий колесо насоса из нержавейший сталь) с электродвигателями мощностью N=560 кВт. напряжение U=6000В; n=750об/мин с учетом заводской рамы и транспортировкой до объекта и подготовка машин к испытанию сдачей под наладку и пуску для соединение к электросети **(агрегаты №4 Левого вращение китайского производства)**	KQSN700-M9J-869 Y500-8	шт				1,0	9902,0	9902,0кг
2	Дренажный центробежный насос типа К 20/18 Q=20м³/час, H=18м. с раб.колесо Dк=129мм, n=2900об/мин мощность эл. двигателя типа 4А80В2 N=2,2 кВт. напряжение U=220/380В; n=3000об/мин	К 20/18 (2К-9) 4А80В2	шт				1,0	68,0	68,0кг
	Всасывающая линия								
3	Переход концентрический Dy=800x1000x7мм, L=470мм	МН2883-62	шт				4,0	109,0	436,0кг
	Напорная линия								
4	Монтажная вставка Dy=600мм, L=274мм на напорной линии	AVK	шт				4,0	95,0	380,0кг
5	Задвижка стальная фланцевая Ø=600мм, L=800мм Ру=1,0МПа,с электроприводом	**30ч915бр**	шт				4,0	1320,0	5280.0кг
6	Переход концентрический Dy=600x1000x7мм, L=917мм	МН2883-62	шт				4,0	230,0	920.0кг
7	Металлическая труба Øн=1020x7мм, L=700м	ГОСТ 10704-91	шт				1,0	174,9	122,0кг
8	Отвод 45° Øн=1000x6мм, L=1240мм	МН2878-62	шт				1,0	187,0	-
9	Металлическая труба Øн=1020x7мм, L=10000мм	ГОСТ 10704-91	шт				1,0	174,9	1749,0кг
10	Металлическая труба Øн=1020x7мм, L=9500мм	ГОСТ 10704-91	шт				1,0	174,9	1661,0кг
11	Металлическая труба Øн=1020x7мм, L=9500мм	ГОСТ 10704-91	шт				1,0	174,9	1661,0кг
12	Металлическая труба Øн=1020x7мм, L=700м	ГОСТ 10704-91	шт				1,0	174,9	122,0кг
13	Отвод 45° Øн=1000x6мм, L=1240мм	МН2878-62	шт				1,0	187,0	-
14	Металлическая труба Øн=1020x14мм, L=10000мм	ГОСТ 10704-91	шт				1,0	416,4	4164,0кг
	Колодец обратного клапан								
15	Приобретение и монтаж обратный клапан фланцевый Dy=1000мм, Ру=1,6мПа	КО1000.16-4311	шт				2,0	1300,0	2600,0кг
16	Приобретение и монтаж задвижки Dy=100мм,Ру=1,0Мпа на сбросной линии	30ч6бр	шт				2,0	39,5	79,0кг
17	Отвод 90° Øy=100x6мм, L=300мм	**ГОСТ 17375-83***	шт				4,0	3,80	15,20кг
18	Металлическая труба Øн=114x7мм, L=1600мм	**ГОСТ 10704-91**	шт				2,0	29,552	59,104кг
19	Фланец стальной приварной Dy=100мм,Ру=1,6мПа	**ГОСТ 12820-80**	шт				4,0	4,73	18,92кг
	Болты и Гаек М16 L=75мм	**ГОСТ 12820-80**	шт				32,0	0,149 /0,033	4,77 / 1,06кг

ПРИМЕЧАНИЕ:

1. Учесть электроды 3% от всего веса металлоконструкции.
2. Учесть масленную краску для металлоконструкции.
3. Данный лист рассматривать совместно с лист-2,3,4,5,5а,6 и 7

Изм.	Кол.уч.	Лист	№ док.	Подп.	Дата	ТХ		
						"Баркарорсозии пойгоххои обкашии Лохур-0,Лохур-1,Лохур-2 ва Лохур-3 дар нохияи Рудаки"		
Разработ.		Фрайдунпоев О.				Насосной станции Лохур-1. Технологическая часть (ТХ).	Стадия	Лист	Листов
ГИП		Шомили У.					РП	12	12
Нач. отдел		Шомили У.				Спецификация оборудования и материалов	ГУП "Проектный Институт "Точикгипроводхоз" Душанбе - 2026		
Норм. контр.		Хайбаров С.							


Согласовано

Взамен инв

Подпись и дата

Инв. подл

Характеристика насоса типа Д KQSN800-M17S n=1000 об/мин

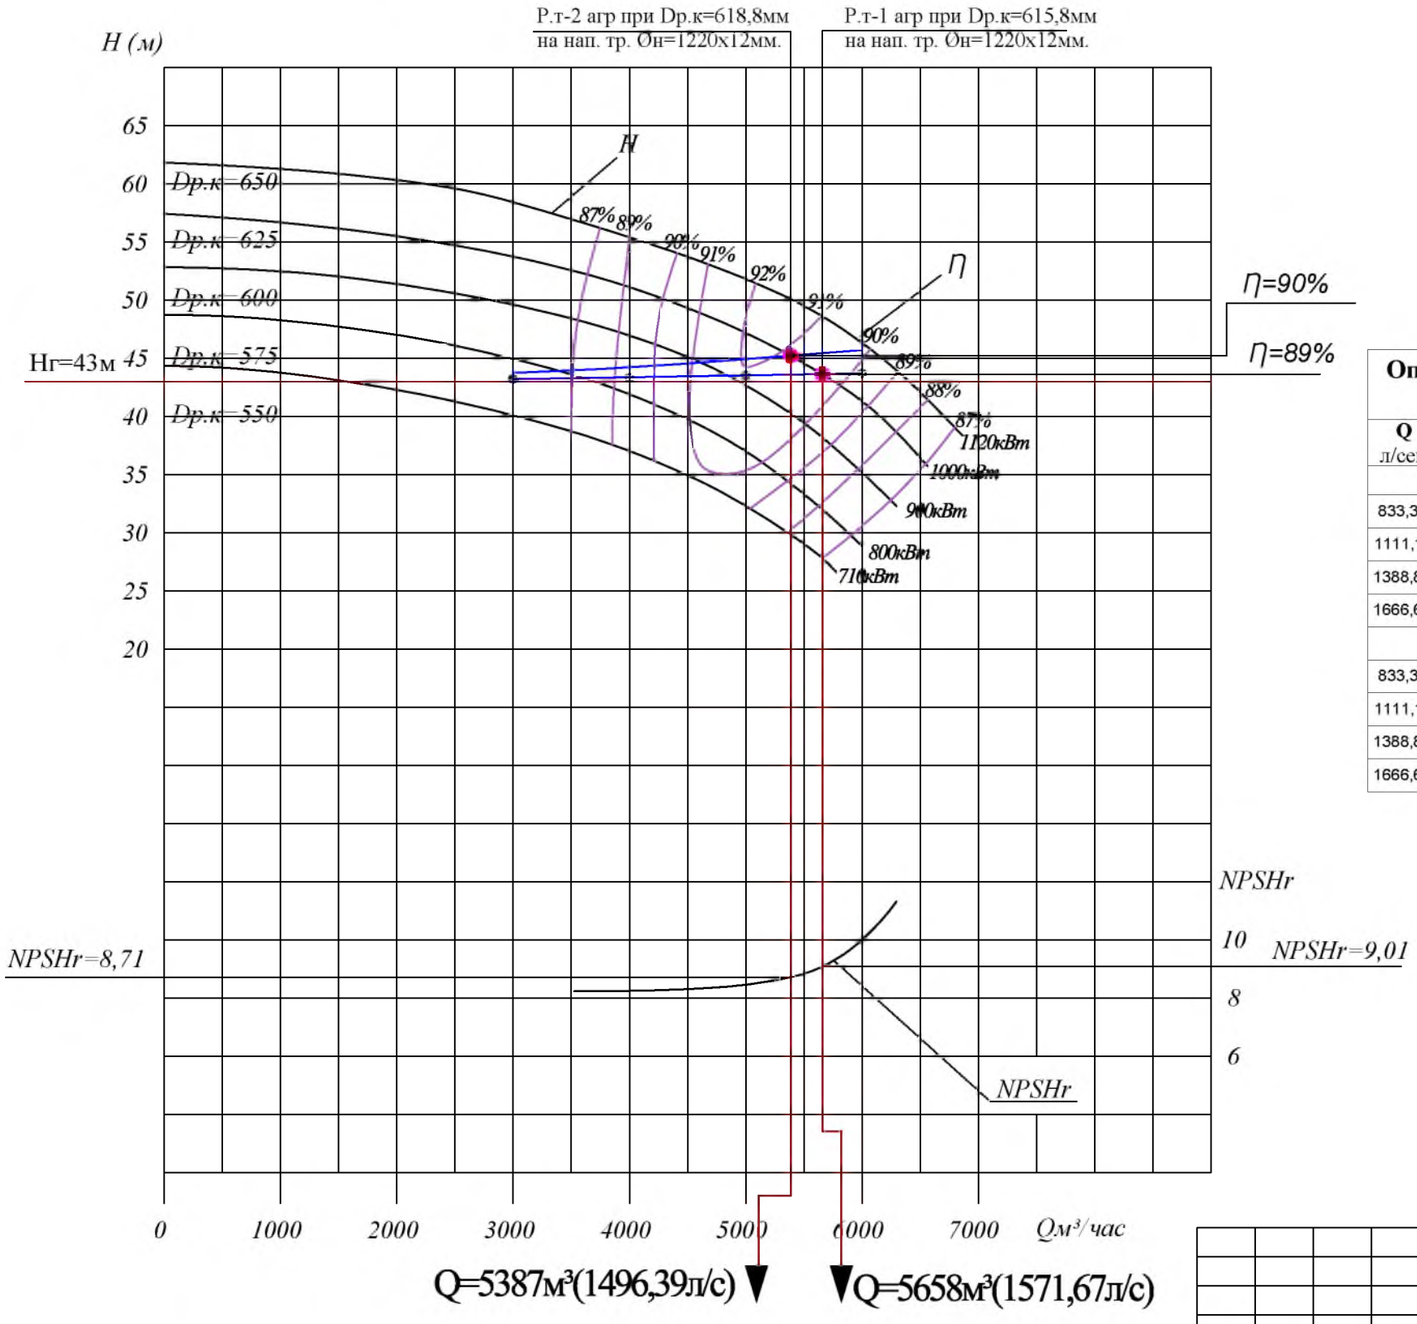

Определение манометрический напор и расчетный расход насоса типа Д KQSN800-M17S

Q л/сек	Q м³/час	Hгео. м	L, км	Dтр.мм	i на 1км, в м	∑i,в м	Н,ман в м при 1-го агрегат	Примечание
		При работе 1-го агрегата						
833,33	3000,0	43,0	0,299	1220х12	0,50	0,18	43,18	
1111,11	4000,0	43,0	0,299	1220х12	0,85	0,30	43,30	
1388,89	5000,0	43,0	0,299	1220х12	1,30	0,47	43,47	
1666,67	6000,0	43,0	0,299	1220х12	1,87	0,67	43,67	
		При работе 2-х агрегатов						
833,33	3000,0	43,0	0,299	1220х12	0,50	0,72	43,72	
1111,11	4000,0	43,0	0,299	1220х12	0,85	1,20	44,20	
1388,89	5000,0	43,0	0,299	1220х12	1,30	1,88	44,88	
1666,67	6000,0	43,0	0,299	1220х12	1,87	2,68	45,68	

Изм.	Кол.уч.	Лист	№ док.	Подп.	Дата
Разработ.		Фрайдуншоев О.			
ГИП		Шомили У.			
Нач. отдел		Шомили У.			
Норм. контр.		Хайбаров С.			

ТХ

"Баркарорсозии пойгоххои обкашии Лохур-0,Лохур-1,Лохур-2 ва Лохур-3 дар нохияи Рудаки"


Насосной станции Лохур-1. Технологическая часть (ТХ).

Стадия	Лист	Листов
РП	1	1

Рабочая характеристика насоса типа KQSN800-M17S

ГУП "Проектный Институт "Точикгипроводхоз" Душанбе - 2026

Характеристика насоса типа Д KQSN700-M9J n=750 об/мин

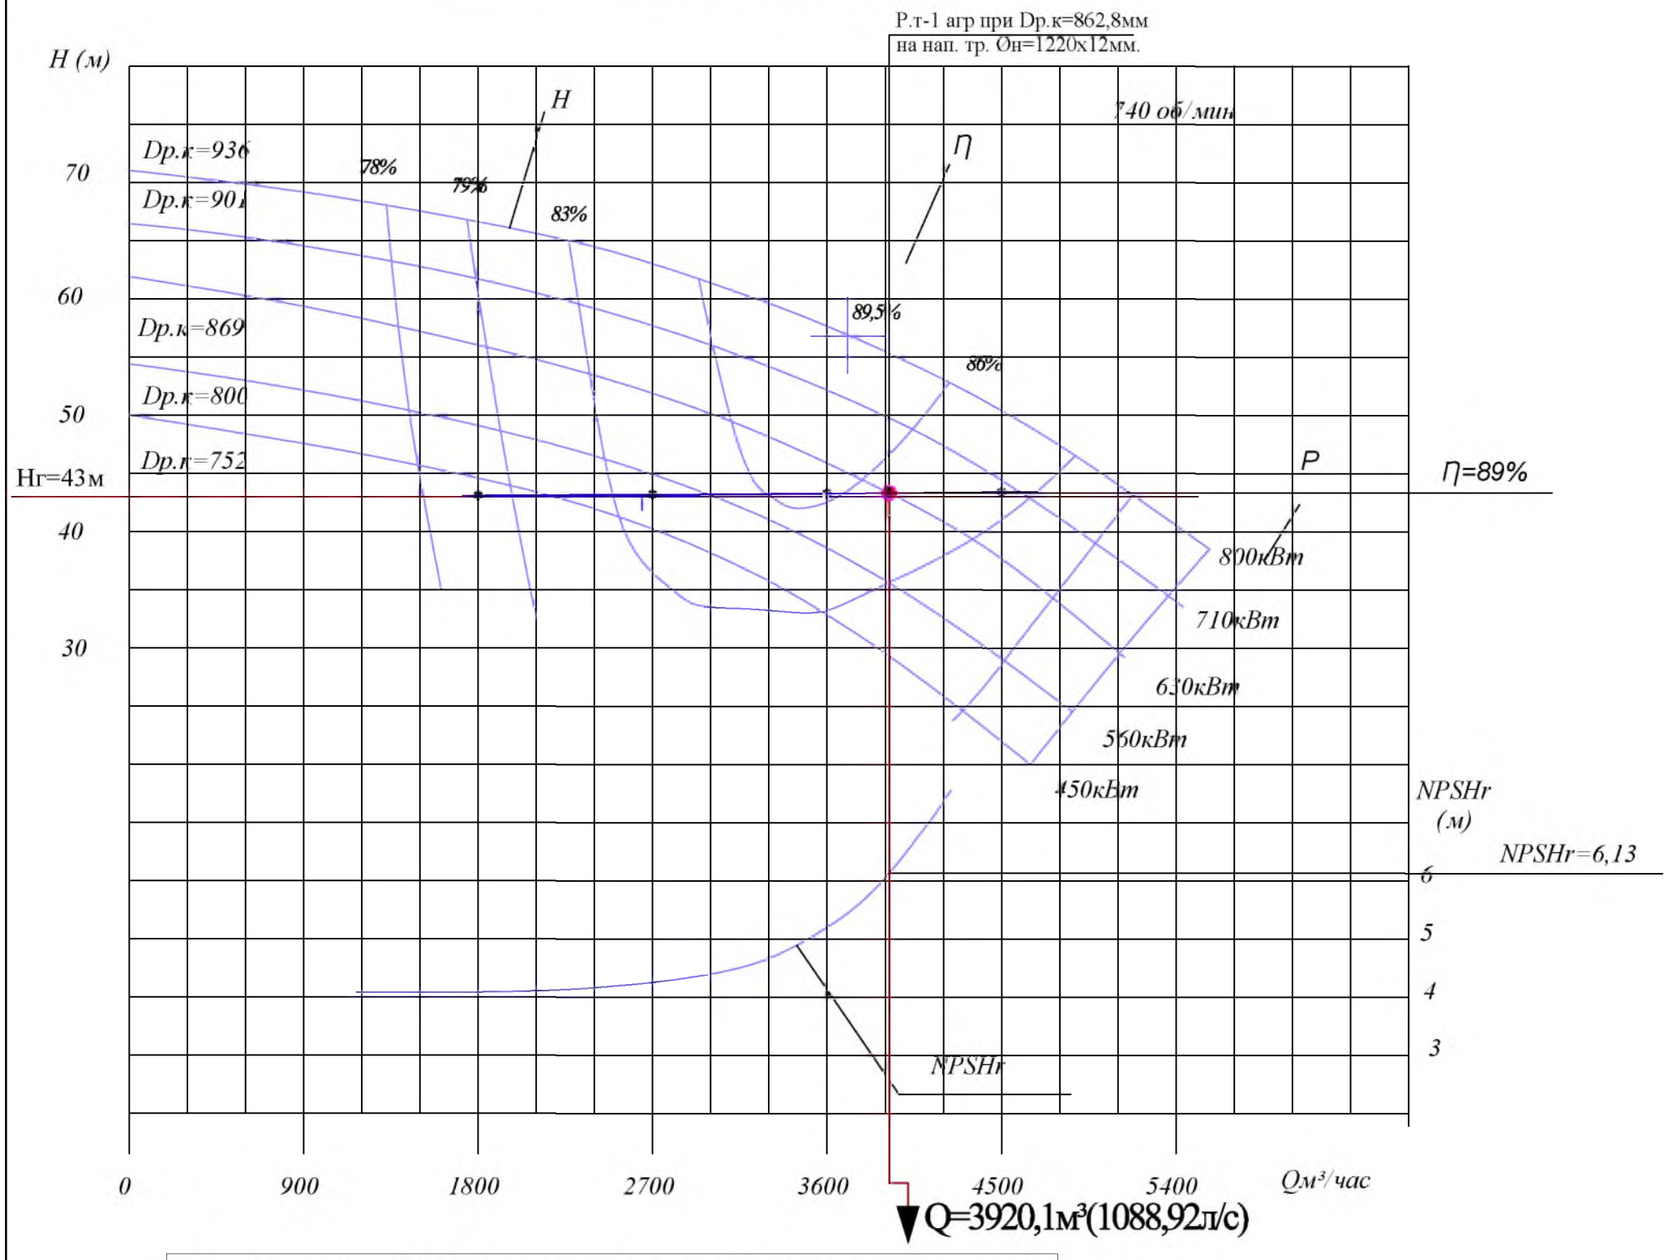

Определение манометрический напор и расчетный расход насоса типа Д KQSN700-M9J

Q л/сек	Q м³/час	Hгео. м	L, км	Dтр.в,мм	i на 1км, в м	∑i,в м	Н,ман в м при 1-го агрегат	Примечание
		При работе 1-го агрегата						
500,0	1800,0	43,0	0,299	1220х12	0,20	0,072	43,072	
750,0	2700	43,0	0,299	1220х12	0,413	0,15	43,15	
1000,0	3600,0	43,0	0,299	1220х12	0,7	0,25	43,25	
1250,0	4500,0	43,0	0,299	1220х12	1,06	0,38	43,38	

						ТХ
						"Баркарорсозии пойгоххои обкашии Лохур-0,Лохур-1,Лохур-2 ва Лохур-3 дар нохияи Рудаки"
Изм.	Кол.уч.	Лист	№ док.	Подп.	Дата	
Разработ.		Фрайдуншоев О.				Насосной станции Лохур-1. Технологическая часть (ТХ).
ГИП		Шомили У.				Стадия: РП; Лист: 2; Листов: 2
Нач. отдел		Шомили У.				
Норм. контр.		Хайбаров С.				Рабочая характеристика насоса типа KQSN700-M9J
						ГУП "Проектный Институт "Точикгипроводхоз" Душанбе - 2026