АГЕНТСТВО ПО МЕЛИОРАЦИИ И ИРРИГАЦИИ
ПРИ ПРАВИТЕЛЬСТВЕ РЕСПУБЛИКИ ТАДЖИКИСТАН

ГУП "ПРОЕКТНЫЙ ИНСТИТУТ
"ТАДЖИКГИПРОВОДХОЗ"

РАБОЧИЙ ПРОЕКТ

"Баркарорсозии пойгоххои обкашии Лохур-0,Лохур-1,Лохур-2 ва Лохур-3 дар нохияи Рудаки"

АЛЬБОМ-1

Насосной станции Лохур-1.

ДВОРОВАЯ УБОРНАЯ НА 1 ОЧКО.

ДУШАНБЕ-2026

АГЕНТСТВО ПО МЕЛИОРАЦИИ И ИРРИГАЦИИ
ПРИ ПРАВИТЕЛЬСТВЕ РЕСПУБЛИКИ ТАДЖИКИСТАН

ГУП "ПРОЕКТНЫЙ ИНСТИТУТ
"ТАДЖИКГИПРОВОДХОЗ"

РАБОЧИЙ ПРОЕКТ

"Баркарорсозии пойгоххои обкашии Лохур-0,Лохур-1,Лохур-2 ва Лохур-3 дар нохияи Рудаки"

АЛЬБОМ-1

Насосной станции Лохур-1.

ДВОРОВАЯ УБОРНАЯ НА 1 ОЧКО.

ГЛ. ИНЖЕНЕР ИНСТИТУТА: ХАЙБАРОВ С.

ГЛ. ИНЖЕНЕР ПРОЕКТА: ШОМИЛИ У.

ДУШАНБЕ-2026

Таб. 1

Ведомость основных комплектов рабочих чертежей		
Обозначение	**Наименование**	**Примечание**
1	2	3
.ПЗ	Пояснительная записка	Книга-1
ТГИ	Инженерно-топогеодезический изысканий	Книга-2
ИГИ	Инженерно-геологический и гидрогеологичекий изысканий	Книга-3
ТХ	**Насосной станции Лохур-1.** Технологическая часть	Альбом-1
ГР	**Насосной станции Лохур-1.** Гидротехническое решение	Альбом-2
АС	**Насосной станции Лохур-1. Архитектурно-строительная часть**	Альбом-3
АС	**Насосной станции Лохур-1. Дежурное помещение Архитектурно-строительная часть**	Альбом-4
АС	**Насосной станции Лохур-1. Уборная на 1-го очко Архитектурно-строительная часть**	Альбом-5
ЭО	Электротехническая часть	Альбом-6
СМ	Сметная документация	Книга-4

Ведомость рабочих чертежей основного комплекта

Таб.2

Лист	Наименование	Примечание
1	Уборная на одно очко. Общие данные	
2	Уборная на одно очко. План. Разрез 1-1. Ведомость объемов работ.	
3	Уборная на одно очко. Фасады 1-2 и Б-В. План стропил. Сечение по 2-2. Спецификация.	
4	Уборная на одно очко.Разрез а-а.План перекрытия выгреба. Балка БМ-1. Спецификация	
5	Уборная на одно очко.План освещения	

Ведомость основных комплектов рабочих чертежей

Таб.3

Обозначение	Наименование	Примечание
	Ссылочные документы	
ГОСТ 9466-75	Электроды для дуговой сварки сталей и наплавки	
	Классификация и общие технические условия	
ГОСТ 5681-83	Сталь прокатная толстолистовая	

Ведомость отделки помещений

	Наименование или номер помещения	Потолок		Стены и перегородки		Примечания
		Площадь	Вид отделки	Площадь	Вид отделки	
1	Дворовая уборная	1,76	Пластика	12,81	Штукатурка с последующей известковый краской	

ТЕХНИКО-ЭКОНОМИЧЕСКИЕ ПОКАЗАТЕЛИ

НАИМЕНОВАНИЕ	КОЛИЧЕСТВО M^2
Площадь застройки	5,76
Общая площадь	3,0
Рабочий площадь	1,76
Строительный обьём	19,25
± 0,000 верх	8,25
± 0,000 низ	11,0

Согласовано

Взамен инв

Подпись и дата

Инв. подл

Настоящий проект выполнен в соответствии с действующими нормами и правилами в том числе по взрыво-пожарной безопасности


Гл.инженер проекта Шомили У.

						АС
						"Баркарорсозии пойгоххои обкашии Лохур-0,Лохур-1,Лохур-2 ва Лохур-3 дар нохияи Рудаки"
Изм.	Кол.уч.	Лист	**№ док.**	Поди.	Дата	
Разработ.		**Фрайдунпоев О.**				Насосной станции Лохур-1. Архитектурно-строительная часть.
ГИП		Шомили У.				
Нач. отдел		Шомили У.				
Норм. контр.		Хайбаров С.				Уборная на одно очко. Общие данные


Стадия	Лист	Листов
РП	1	5

ГУП "Проектный Институт "Точикгипроводхоз" Душанбе - 2026

План М1:50

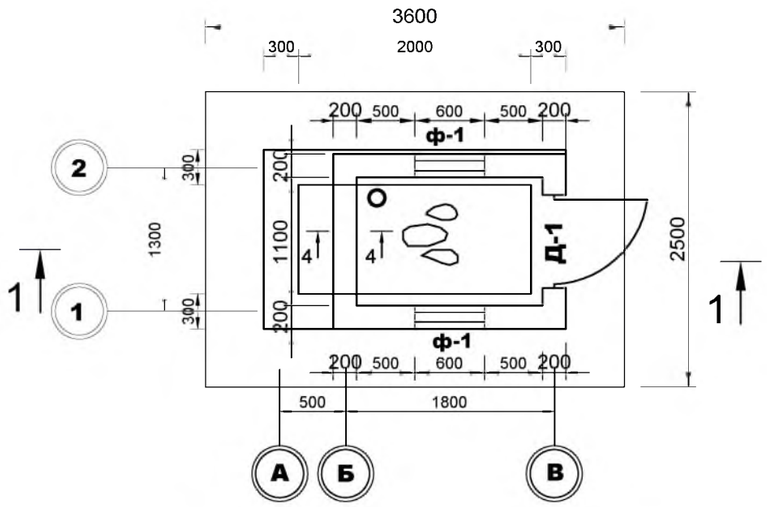

Разрез 1-1 М1:50

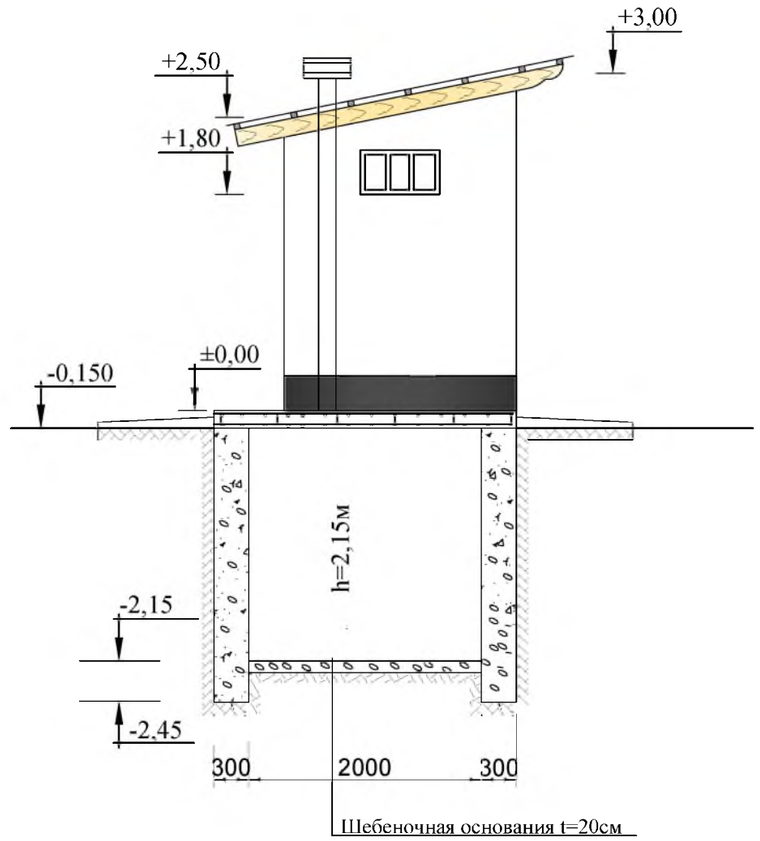

Ведомость объёмов работ

№ п/п	Наименование	Ед изм	Кол-во	Примеч
1	Выемка грунта	м³	10,0	
2	Основания из щебня t=20см	м³	0,36	
3	Монолитный бутобетон стены В15 F100 W4. (30% камень)	м³	5,16	
4	Кладка стен из цем. блока размером 400х200х200	м³	3,0	
5	Штукатурка наружных и внутренних стен уборная	м²	14,22	
6	Известковая окраска наружных и внутренних стен уборная	м²	14,22	
7	Окраска битумом цокольной части уборная	м²	2,16	
8	Бетонная отмоска из бетона В7,5,В=0,5м,t=7см	м³	0,43	

Согласовано

Взамен инв.

Подпись и дата


Инв. подл

						АС
						"Баркарорсозии пойгоххои обкашии Лохур-0,Лохур-1,Лохур-2 ва Лохур-3 дар нохияи Рудаки"
Изм.	Кол.уч.	Лист	№ док.	Подп.	Дата	
Разработ.		Фрайдуншоев О.				Насосной станции Лохур-1. Архитектурно-строительная часть.
ГИП		Шомили У.				
Нач. отдел		Шомили У.				Уборная на одно очко. План. Разрез 1-1. Ведомость объемов работ.
Норм. контр.		Хайбаров С.				


Стадия	Лист	Листов
РП	2	5

ГУП "Проектный Институт "Точикгипроводхоз" Душанбе - 2026

Фасад 1-2

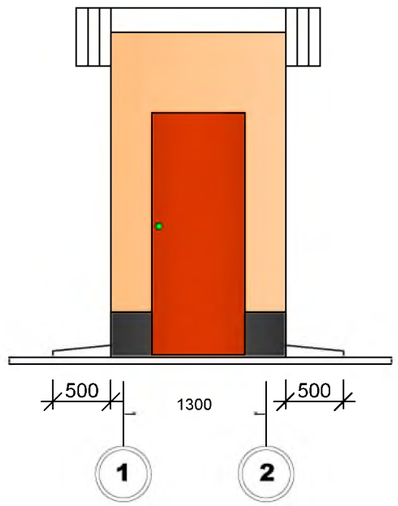


Фасад Б-В

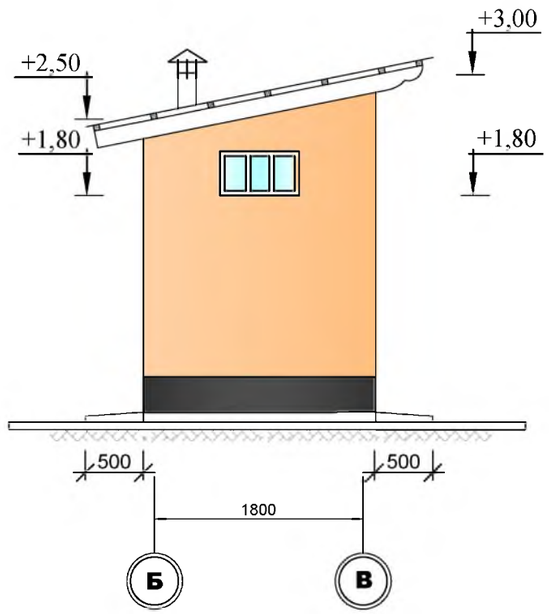


4-4 М1:25




План стропил М1:50

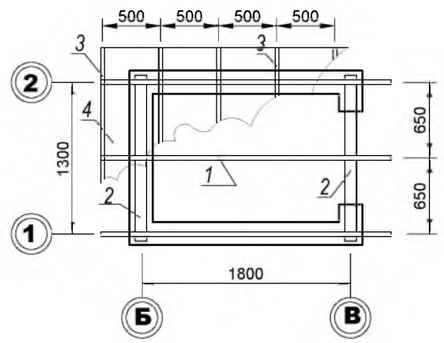

Сечение по 2-2

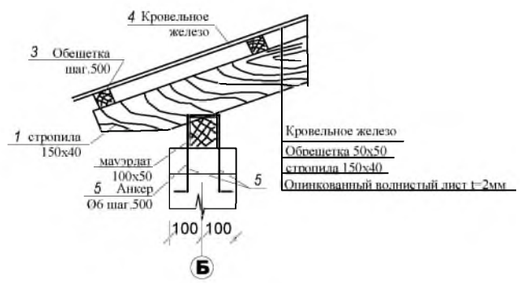

Зонтик

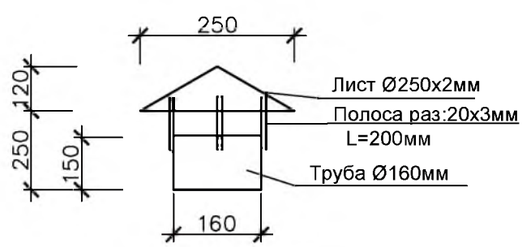

Спецификация оконных и дверных блоков

№ п/п	Обозначение	Наименование	Размер, мм	Кол-во шт	Примечание
1	Ф-1	Фрамуга	600х300	2	Пластиковые
2	Д-1	Дверной блок	800х2100	1	Пластиковые
		Зонтик			
3		Лист 250х2мм		1	V=0,13м²
4		Полоса раз:20х3мм L=200мм		4	Общий 0,36кг
5		Шурпы		8	

Спецификация деревянных элементов

№ п/п	Наименование элементов	Сечение мм	Кол. шт	Длина в м		Объём древесины м³
1	Стропильная нога	40х150	3	2,87	8,61	0,051
2	Мауэрлат	100х50	2	1,5	3,0	0,015
3	Обрешетка	50х50			16,0	0,04
4	Лист металлический волнистый м2					6,30м²
5	Анкер AI Ø6мм, L=800мм					1,06кг

ПРИМЕЧАНИЕ

***** Перемычки выполнить из бруска раз:1600х200х50мм -1шт**
***** Раз:1200х200х50мм -2шт**

Согласовано


Взамен инв.

Подпись и дата


Инв. подл

Изм.	Кол.уч.	Лист	№ док.	Подп.	Дата	АС		
						"Баркарорсозии пойгоххои обкашии Лохур-0,Лохур-1,Лохур-2 ва Лохур-3 дар нохияи Рудаки"		
Разработ.		Файдуллоев О.				Насосной станции Лохур-1. Архитектурно-строительная часть.	Стадия: РП	Лист: 3 / Листов: 5
ГИП		Шомили У.						
Нач. отдел		Шомили У.				Уборная на одно очко. Фасады 1-2 и Б-В. План стропил. Сечение по 2-2. Спецификация.	ГУП "Проектный Институт "Точикгипроводхоз" Душанбе - 2026	
Норм. контр.		Хайбаров С.						


а-а. М1:50

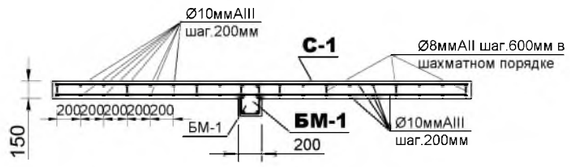


План перекрытия выгреба

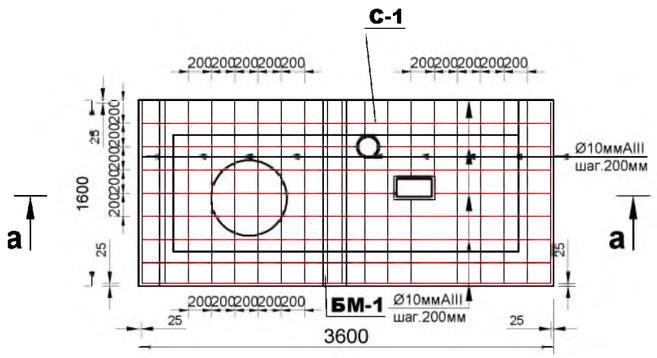

Балка БМ - 1

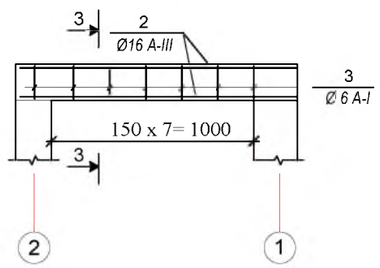

3-3.

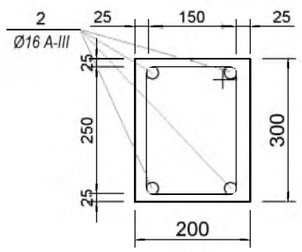

Спецификация

Марка поз.	Обозначение	Наименование	Кол.	Масса ед. кг	Примеч.
		БМ-1			
2	ГОСТ5781-82	Ø16 A-III L= 3550мм	4	5,57	22,29
3	ГОСТ5781-82	Ø 6 A-I L= 560мм	7	0,124	0,86
	ГОСТ26633- 91	Бетон В-15			0,096 м³

Спецификация

№ пп	Обозначение	Наименование	К-во	Масса ед. кг	Примечание общий масс. кг
С-1	ГОСТ23279-85	Ø10A-III 200 1550х3550мм Ø10A-III 200	2,0	33.2	66.5
2		Ø8A-III шаг.600,L=450мм	15	0,17	2,6
		Всего:			69,1кг
3		Полиэтиленовая труба Ø160мм, L=3200мм	1		
4		Установка чугунный люк	1		
5		Бетон В15			W=0,86м³

ПРИМЕЧАНИЕ

******Внутренние стены выгреба затереть цементным раствором с последующей обмазкой битумом.***

****** Для перекрытия выгреба защитный слой 25мм.***

****** Размеры дано в миллиметрах.***


Согласовано

Взамен инв.

Подпись и дата

Инв. подл

Изм.	Кол.уч.	Лист	№ док.	Подп.	Дата	АС		
						"Баркарорсозии пойгоххои обкашии Лохур-0,Лохур-1,Лохур-2 ва Лохур-3 дар нохияи Рудаки"		
Разработ.		Файдуллоев О.				Насосной станции Лохур-1. Архитектурно-строительная часть.	Стадия: РП	Лист: 4 / Листов: 5
ГИП		Шомили У.						
Нач. отдел		Шомили У.				Уборная на одно очко. Разрез а-а.План перекрытия выгреба. Балка БМ-1. Спецификация	ГУП "Проектный Институт "Точикгипроводхоз" Душанбе - 2026	
Норм. контр.		Хайбаров С.						

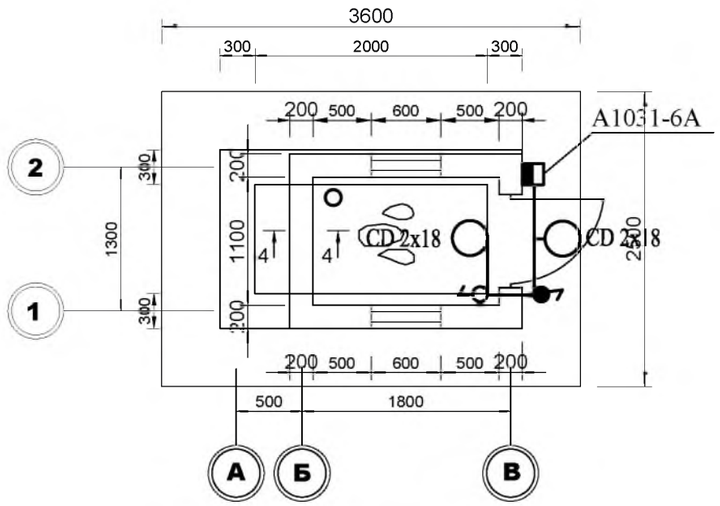

Марка поз.	Обозначение	Наименование	Кол.	Масса ед; кг	Приме-чание
1	Светильник с комп. люмин.лампой	CD 2x18	2	1.3	
2	Выключатель автоматический	A1031-6A	1	0.3	
3	Кабель	ВВГ-2х1,5	3		м
4	Выключ. герметичн.10А, 220В	А16-001УХЛ2	2		

Примечания:

1.Ввод 220 В в уборную предусматривается от ПСН.
2.В качестве вводного щита принят автоматический выключатель 1-фазный А1031-10А.
3. Сеть освещения выполнена кабелем марки АВВГ.
4. Высота установки:
 - выключателей - 1,5м.

Согласовано

Взамен инв.

Подпись и дата

Инв. подл

						АС
						"Баркарорсозии пойгоххои обкашии Лохур-0,Лохур-1,Лохур-2 ва Лохур-3 дар нохияи Рудаки"
Изм.	Кол.уч.	Лист	№ док.	Подп.	Дата	
Разработ.		Фрайдунпоев О.				Насосной станции Лохур-1. Архитектурно-строительная часть.
ГИП		Шомили У.				
Нач. отдел		Шомили У.				Уборная на одно очко. План освещения
Норм. контр.		Хайбаров С.				

Стадия	Лист	Листов
РП	5	5

ГУП "Проектный Институт "Точикгипроводхоз" Душанбе - 2026