АГЕНТСТВО ПО МЕЛИОРАЦИИ И ИРРИГАЦИИ
ПРИ ПРАВИТЕЛЬСТВЕ РЕСПУБЛИКИ ТАДЖИКИСТАН

ГУП "ПРОЕКТНЫЙ ИНСТИТУТ
"ТАДЖИКГИПРОВОДХОЗ"

РАБОЧИЙ ПРОЕКТ

"Баркарорсозии пойгоххои обкашии Лохур-0,Лохур-1,Лохур-2 ва Лохур-3 дар нохияи Рудаки"

АЛЬБОМ-1

Насосной станции Лохур-2.
Архитектурно-строительная часть.

ДУШАНБЕ-2026

АГЕНТСТВО ПО МЕЛИОРАЦИИ И ИРРИГАЦИИ
ПРИ ПРАВИТЕЛЬСТВЕ РЕСПУБЛИКИ ТАДЖИКИСТАН

ГУП "ПРОЕКТНЫЙ ИНСТИТУТ
"ТАДЖИКГИПРОВОДХОЗ"

РАБОЧИЙ ПРОЕКТ

"Баркарорсозии пойгоххои обкашии Лохур-0,Лохур-1,Лохур-2 ва Лохур-3 дар нохияи Рудаки"

АЛЬБОМ-1

Насосной станции Лохур-2.
Архитектурно-строительная часть.

ГЛ. ИНЖЕНЕР ИНСТИТУТА: ХАЙБАРОВ С.

ГЛ. ИНЖЕНЕР ПРОЕКТА: ШОМИЛИ У.

ДУШАНБЕ-2026

Таб. 1

Ведомость основных комплектов рабочих чертежей		
Обозначение	**Наименование**	**Примечание**
1	2	3
.ПЗ	Пояснительная записка	Книга-1
ТГИ	Инженерно-топогеодезический изыскания	Книга-2
ИГИ	Инженерно-геологический и гидрогеологичекий изысканий	Книга-3
ТХ	**Насосной станции Лохур-2.** Технологическая часть	Альбом-1
ГР	**Насосной станции Лохур-2.** Гидротехническое решение	Альбом-2
АС	**Насосной станции Лохур-2. Архитектурно-строительная часть**	Альбом-3
АС	**Насосной станции Лохур-2. Дежурное помещение Архитектурно-строительная часть**	Альбом-4
АС	**Насосной станции Лохур-2. Уборная на 1-го очко Архитектурно-строительная часть**	Альбом-5
ЭО	Электротехническая часть	Альбом-6
СМ	Сметная документация	Книга-4

Таб. 2

Ведомость рабочих чертежей основного комплекта **ТХ**		
Лист	**Наименование**	**Примечание**
1	2	3
1	Общие данные	
2	**План площадка насосной станции М1:500. Экспликация и** ведомость объёмов работ.	
3	**План размещение гидромеханического оборудование насосной станции М1:100.**	
4	**Разрез в осях 1 -2. М1:100. Ведомость объёмов демонтажных работ**	
5	План кровли (на отметке ±0,000). Спецификация водосточная элементов.	
6	Схема расположения деревянных элементов кровли. **Спецификация**	

Таб.3

Ведомость ссылочных и прилагаемых документов		
Обозначение	Наименование	Примечание
	Ссылочные документы	
ГОСТ 10704-91	Трубы металлические	
ГОСТ 9466-75	Электроды для дуговой сварки сталей и наплавки	
	классификация и общие технические условия	
ГОСТ 19903-74	Лист стальная	
30ч906бр	Задвижки с электроприводом	
ГОСТ 8509-93	Уголки стальные горячекатаные равнопрочные	
	Прилагаемые документы	

Согласовано

Взамен инв.

Подпись и дата


Инв. подл

Настоящий проект выполнен в соответствии с дествующими нормами и правилами, в том числе по взрыво - пожарной безопасности.

Гл. инженер проекта Шомили У.

Изм.	Кол.уч.	Лист	№ док.	Подп.	Дата	**АС**		
						"Баркарорсозии пойгоххои обкашии Лохур-0,Лохур-1,Лохур-2 ва Лохур-3 дар нохияи Рудаки"		
Разработ.		**Фрайдунпосев О.**				Насосной станции Лохур-2. Архитектурно-строительная часть.	Стадия: РП	Лист: 1 / Листов: 6
ГИП		Шомили У.						
Нач. отдел		Шомили У.				Общие данные.	**ГУП "Проектный Институт "Точикгипроводхоз" Душанбе - 2026**	
Норм. контр.		Хайбаров С.						

План площадка насосной станции Лохур-1 II-го подъема М1:500

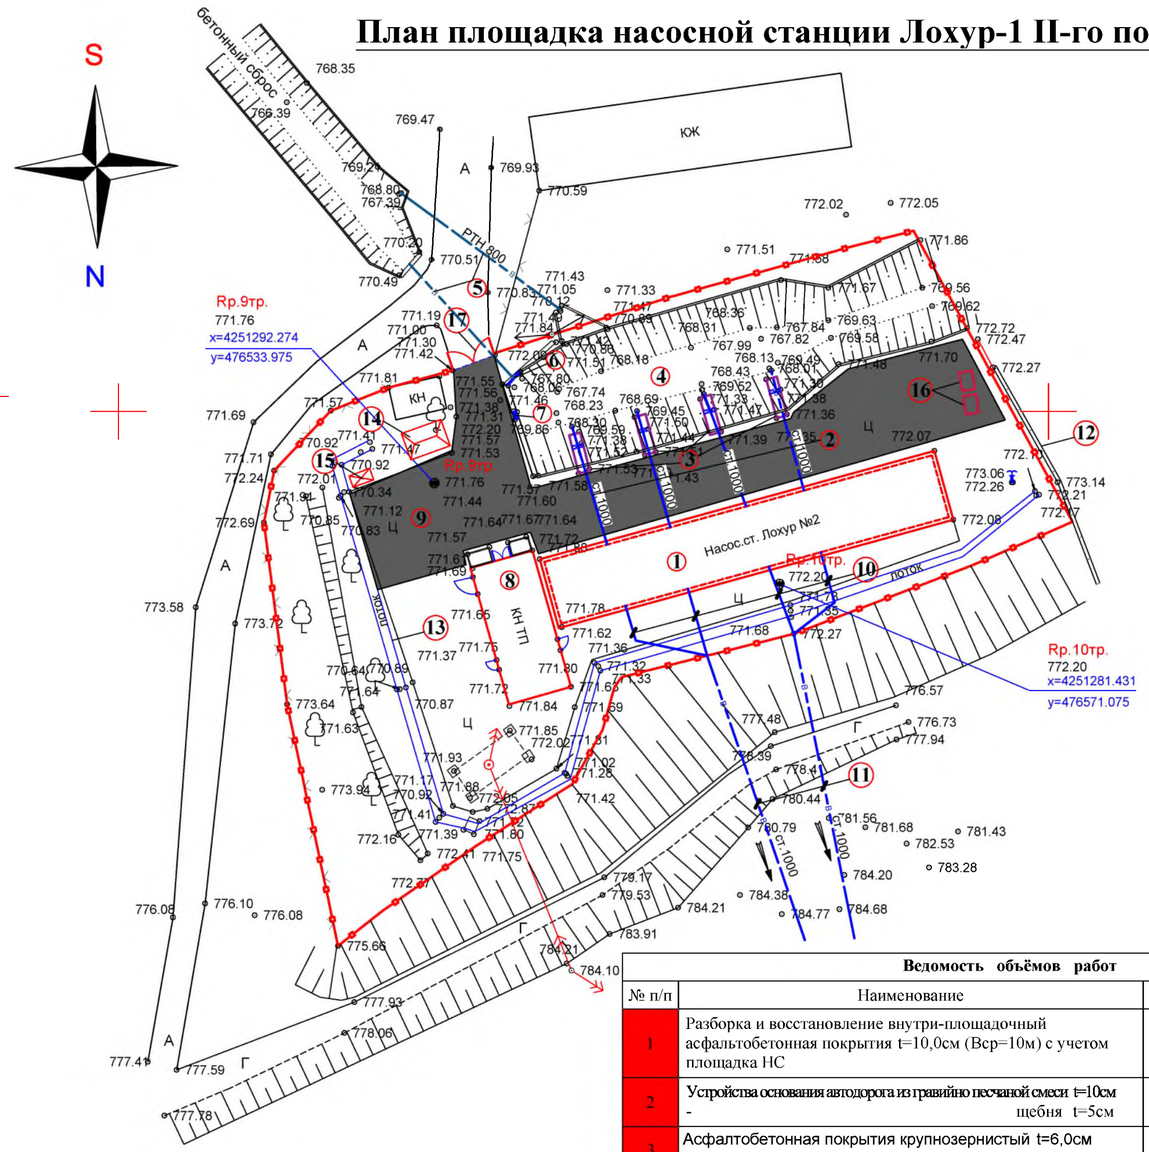

Ведомость объёмов работ

№ п/п	Наименование	Ед. изм	кол-во	Примечание
1	Разборка и восстановление внутри-площадочный асфальтобетонная покрытия t=10,0см (Вср=10м) с учетом площадка НС	м²	800.0	Lоб=80,0м
2	Устройства основания автодорога из гравийно песчаной смеси t=10см - щебня t=5см	м² м²	800.0	
3	Асфалтобетонная покрытия крупнозернистый t=6,0см мелкозернистый t=4,0см	м² м²	800.0	
4	Установка сетчатое ограждение территории В=2,0м, Н=2,0м	пм/ шт	504/ 202	см. лист.
5	Приобретение и установка металлические ворота раз:4,0х2,0м	шт	1	см. лист.
6	Установка мусорного контейнера раз:3х2м	шт	2	Рыночное
7	Устройство здание дежурное помещение раз:3,0х4,5м	шт	1	см.лист-
8	Устройство здание уборное раз:1,3х1,8м	шт	1	см.лист-

Экспликация здании и сооружении

№ п/п	Наименование	Ед. измер.	Кол-во	Примечание
1	Здание насосной станции раз:7,80х45,0м	шт	1,0	Существующий подлежит восстановление
2	Всасывающий трубопровод Ø=1000мм, (4-нитки)	пм	52,0	Существующий сохраняется
3	Служебная площадка раз:1,3х4,40м	шт	4,0	Существующий подлежит восстановление
4	Аванкамера раз: 5,0х35,0м	шт	1,0	Существующий подлежит восстановление
5	Сбросной труба РТН Ø=800мм	пм	40,0	Существующий сохраняется
6	Сбросной затвор ГС 1,60х3,0см	шт	1,0	Существующий подлежит восстановление
7	Сбросной затвор ГС 0,85х0,90см	шт	1,0	Существующий подлежит восстановление
8	Здание трансформаторная подстанция раз: 6,70х15,0м	шт	1,0	Существующий подлежит восстановление
9	Внутри площадочная подъездная асфальтная дорога Вср=8,0-70,0м	пм	80,0	Существующий подлежит восстановление
10	Напорный водовод D=1000мм (от здание НС до точ. подключение 4-нитки)	пм	40,0	Существующий сохраняется
11	Напорный водовод D=1000мм (от точ. подключение до напорный бассейн 2-нитки)	пм	354,0	Существующий сохраняется
12	Бетонная стенка t=40см	пм	30,0	Существующий сохраняется
13	Бетонный лоток ЛР-100	пм	121,0	Существующий сохраняется
14	Дежурное помещение раз: 3,5 х 4,0м	шт	1,0	Проектируемый
15	Уборная на 1-о очко раз:1,30х2.35х3.0м	шт	1,0	Проектируемый
16	Мусорный контейнер	шт	2,0	Проектируемый
17	Металлическая ворота В=4,0м,Н=2,0м	шт	1,0	Проектируемый
17	Ограждение территории	пм	504,0	Проектируемый

УСЛОВНЫЕ ОБОЗНАЧЕНИЯ

- Напорный и всасывающий трубопровод
- Сбросной труба
- Сетчатое ограждение
- A — Внутри площадочная подъездная асфальтная дорога


Изм.	Кол.уч.	Лист	№ док.	Подп.	Дата	АС
						"Баркарорсозии пойгоххои обкашии Лохур-0,Лохур-1,Лохур-2 ва Лохур-3 дар нохияи Рудаки"
Разработ.		Фрайдуншоев О.				Насосной станции Лохур-2. Архитектурно-строительная часть.
ГИП		Шомили У.				Стадия: РП; Лист: 2; Листов: 6
Нач. отдел		Шомили У.				
Норм. контр.		Хайбаров С.				План площадка насосной станции М1:500. Экспликация и ведомость объёмов работ.
						ГУП "Проектный Институт "Точикгипроводхоз" Душанбе - 2026

Согласовано

Взамен инв.

Подпись и дата

Инв. подл.

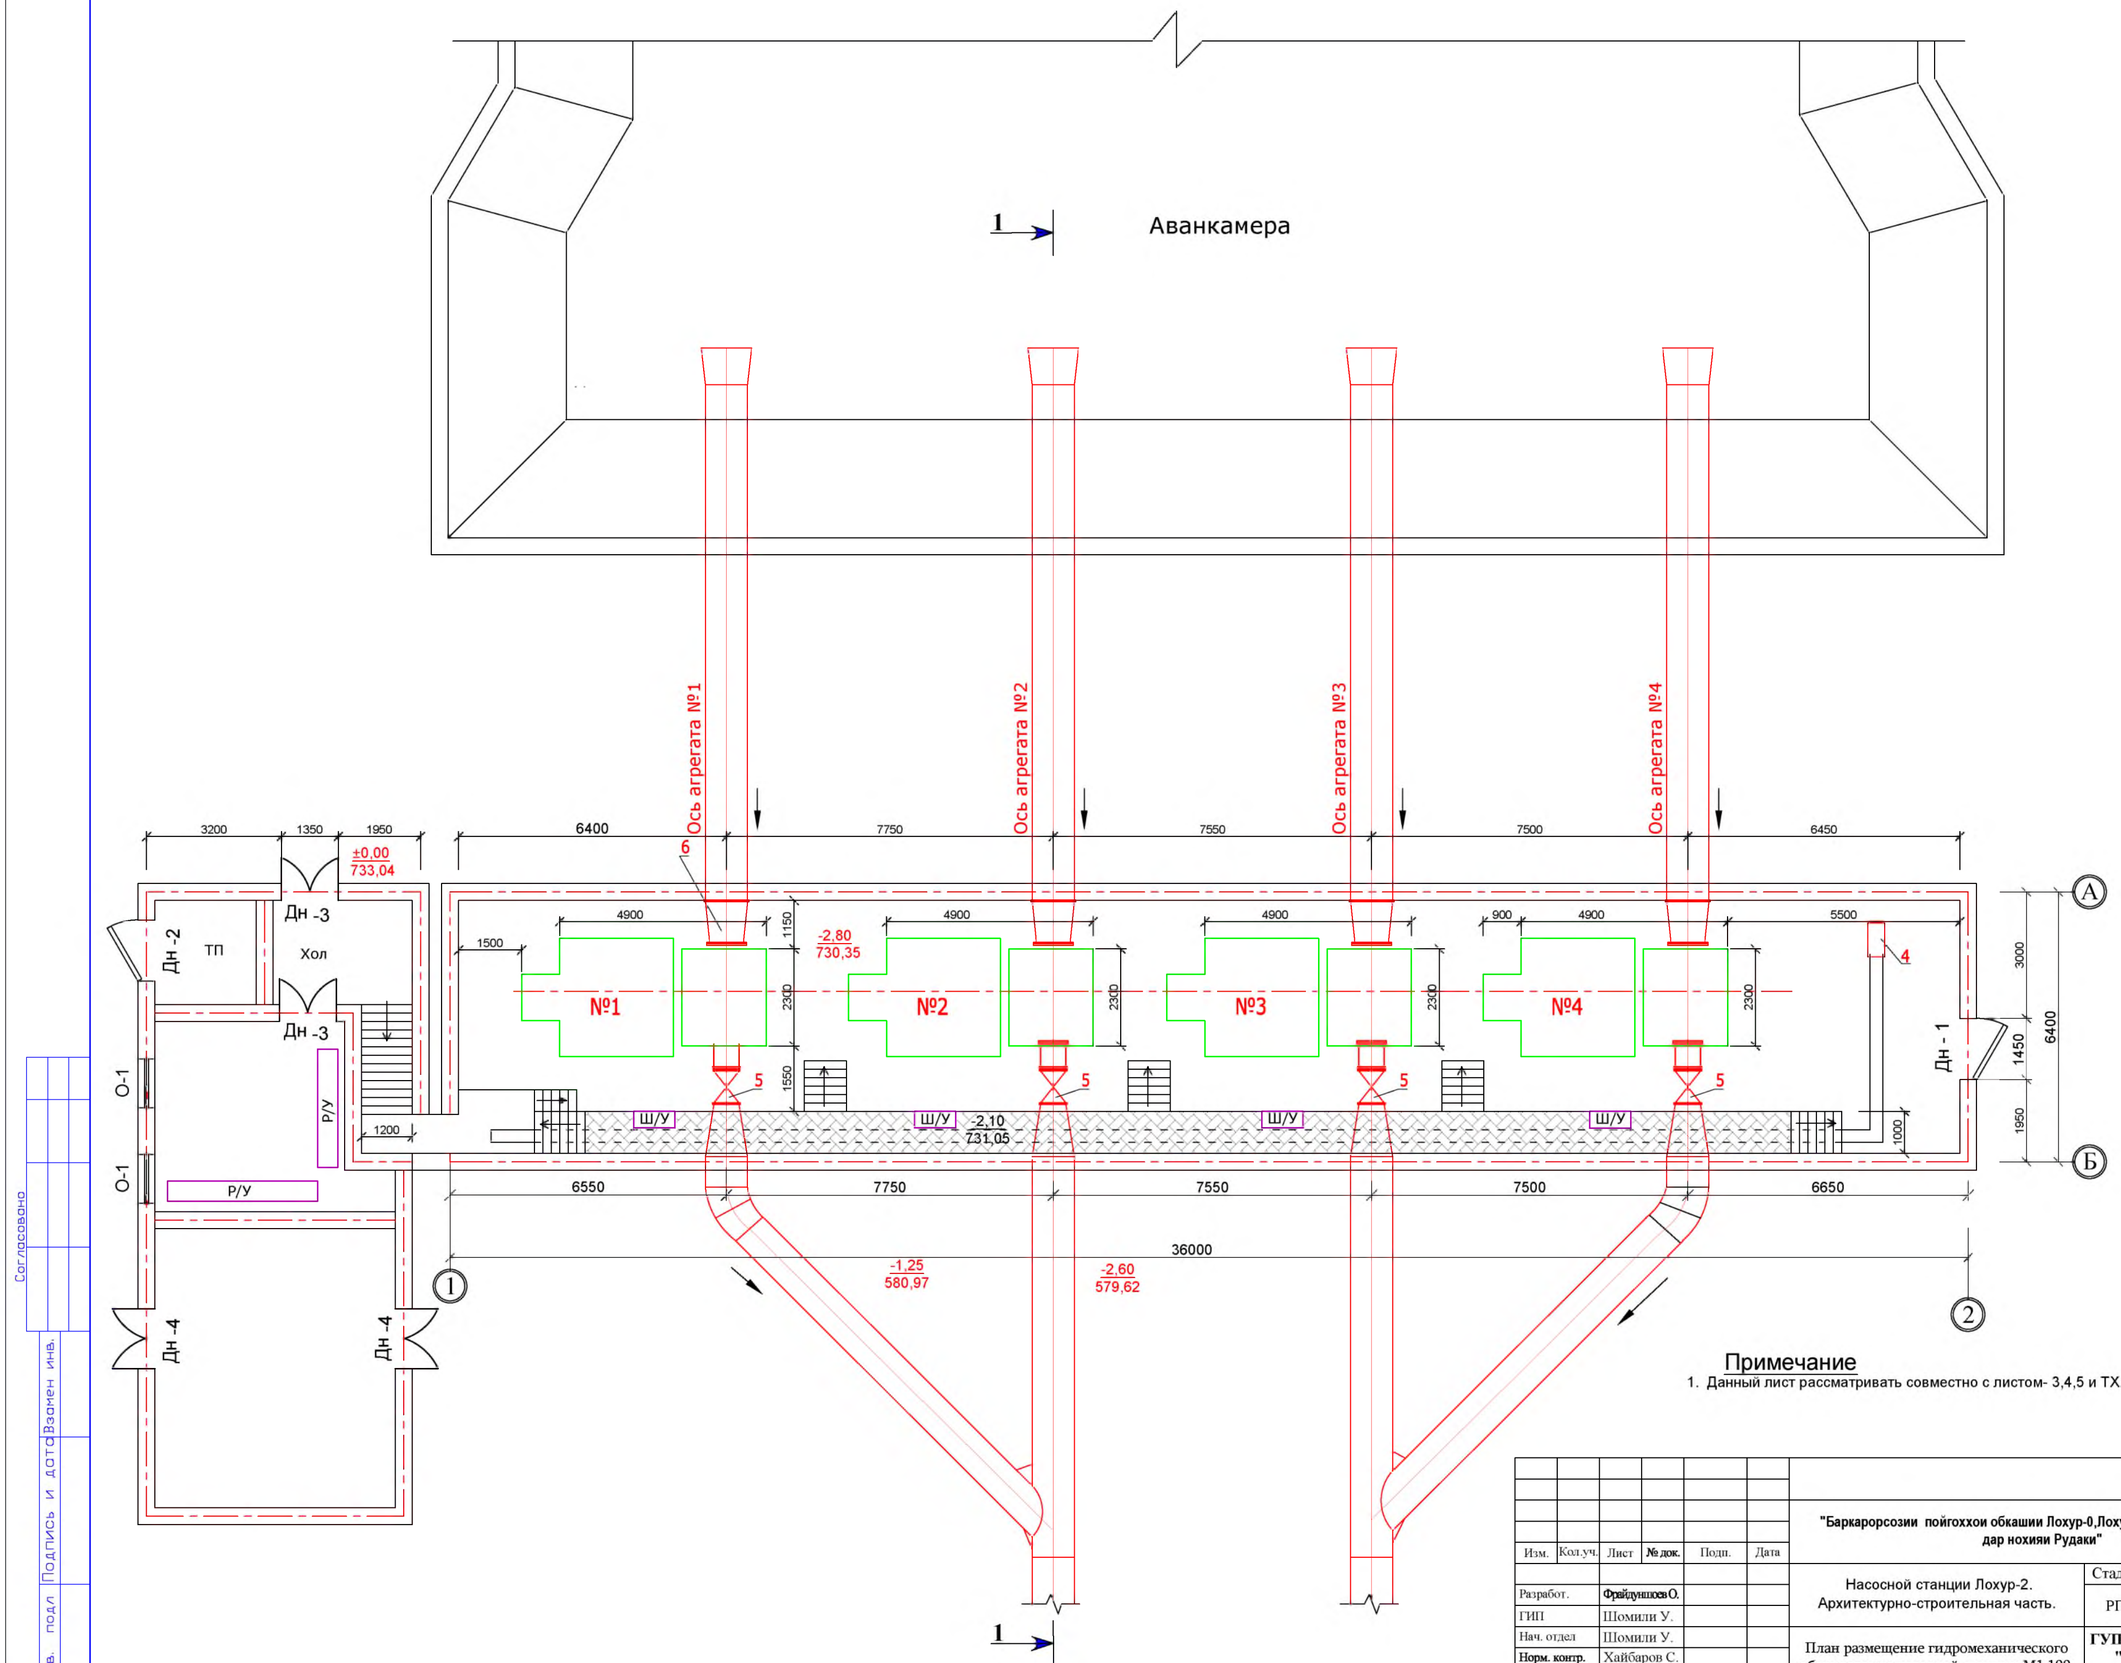

Примечание

1. Данный лист рассматривать совместно с листом- 3,4,5 и ТХ.СО


						АС
						"Баркарорсозии пойгоххои обкашии Лохур-0,Лохур-1,Лохур-2 ва Лохур-3 дар нохияи Рудаки"
Изм.	Кол.уч.	Лист	№ док.	Подп.	Дата	
Разработ.		Фрайдушоев О.				Насосной станции Лохур-2. Архитектурно-строительная часть.
ГИП		Шомили У.				
Нач. отдел		Шомили У.				
Норм. контр.		Хайбаров С.				План размещение гидромеханического оборудование насосной станции М1:100.


Стадия	Лист	Листов
РП	3	6

ГУП "Проектный Институт "Точикгипроводхоз" Душанбе - 2026

Согласовано

Инв. подл | Подпись и дата | Взамен инв.

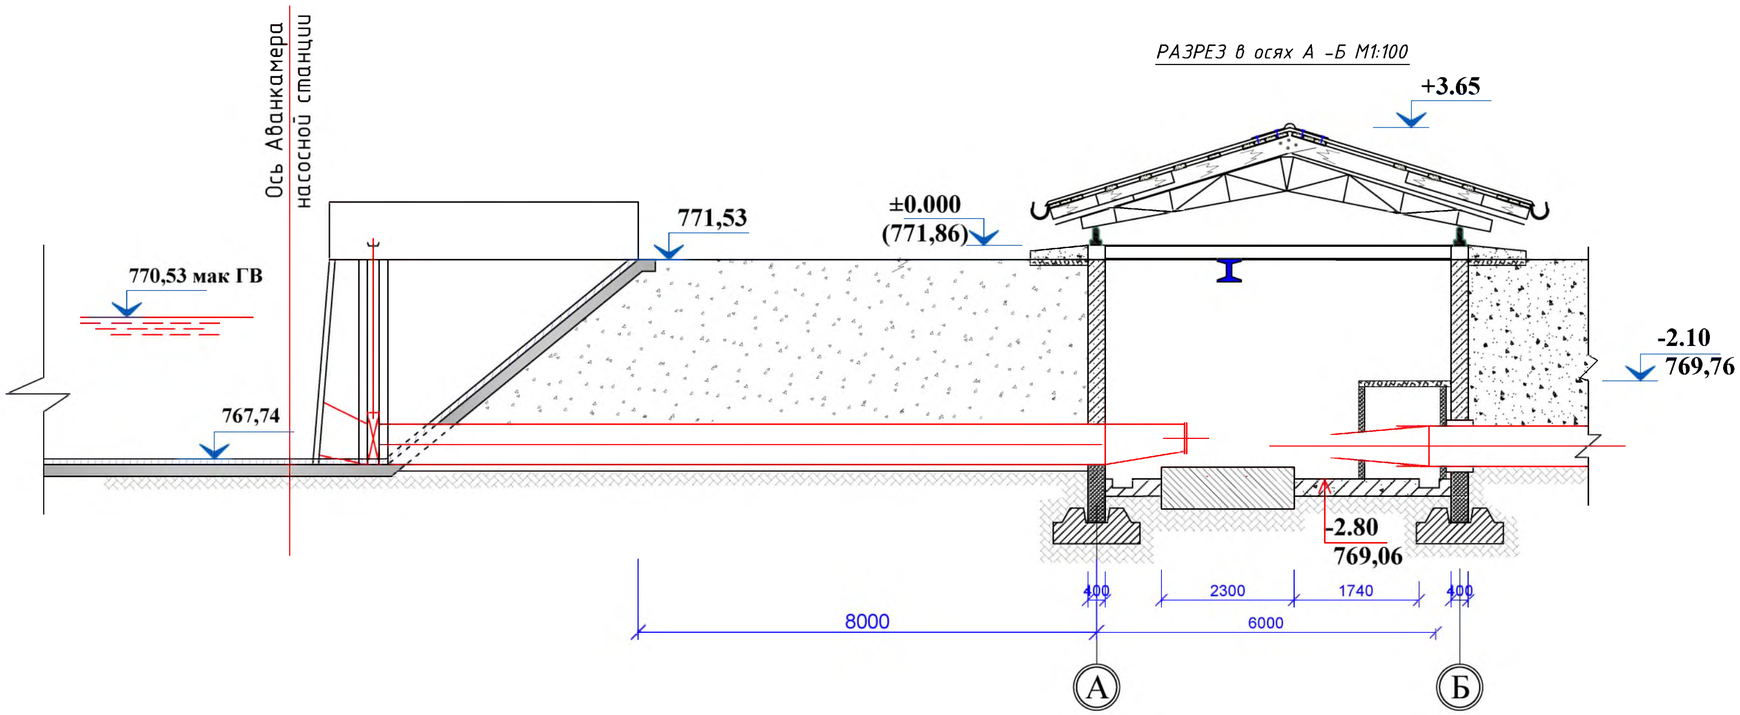

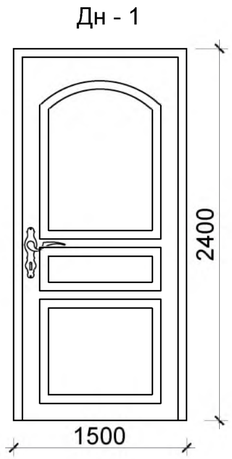

Ведомость объёмов работ

№ п /п	Наименование	Ед. изм	Кол-во	Примечание
1	Очистка от заиление t=10см дренажного канава раз: b=20см; h=30см; L=37пм.	м²	1,0	
2	Восстановление дно дренажного канава t=5см раз: b=20см; h=30см; L=37пм из бетона В15	м²	0,40	
3	Очистка внутренных стены и балки насосной станции	м²	293,0	
4	Шпатлёвка, грунтовка и водоэмульционая краска внутренних стены и балки	м²	293,0	
5	Устройство отмостка вокруг здания раз:100см t=10см из бетона В12,5	м³	8.40	
6	Очистка сальные мостики, лестницы и ограждения металлическим щеткой	м²	20,0	
7	Окраска стальны мостики, лестницы и ограждения за два раза	м²	20,0	
8	Очистка и окраска сущ. металлическая ферма раз:1,2х6,0м	м²	10,0	
9	Установка металлопластик диверные блоки раз:1500х2400мм	шт/ м²	1/ 3,6	-
10	Поправка существующие рельсовой путь	пм	72,0	
11	Замена сущ. вращательный колесо над рельсовой путь	шт	12,0	
12	Замена существующие крищы НС	шт	4,0	
	Устройство пола			
13	Устройство пола насосной станций из бетона В 15 t=10см	м³	15,0	

Спецификация заполнения оконных и дверных проемов

№ поз.	Наименование	Размеры проема (ммхмм)	Количество 1 этаж	Всего	Примечание
1	Дн-1	1500 х 2400	1	1	Металлопластика

Примечание

1. Данный лист рассматривать совместно с листом- 2,3,6 и ТХ.СО
2. Нумерация позиции см.ТХ.СО.

						АС
						"Баркарорсозии пойгоххои обкашии Лохур-0,Лохур-1,Лохур-2 ва Лохур-3 дар нохияи Рудаки"
Изм.	Кол.уч.	Лист	№ док.	Подп.	Дата	
Разработ.		Фрайдуншоев О.				Насосной станции Лохур-2. Архитектурно-строительная часть.
ГИП		Шомили У.				
Нач. отдел		Шомили У.				Разрез в осях 1 -2. М1:100. Ведомость объёмов демонтажных работ
Норм. контр.		Хайбаров С.				


Стадия	Лист	Листов
РП	4	6

ГУП "Проектный Институт "Точикгипроводхоз" Душанбе - 2026

Согласовано

Инв. подл | Подпись и дата | Взамен инв.

План кровли
(на отметке ±0,000)

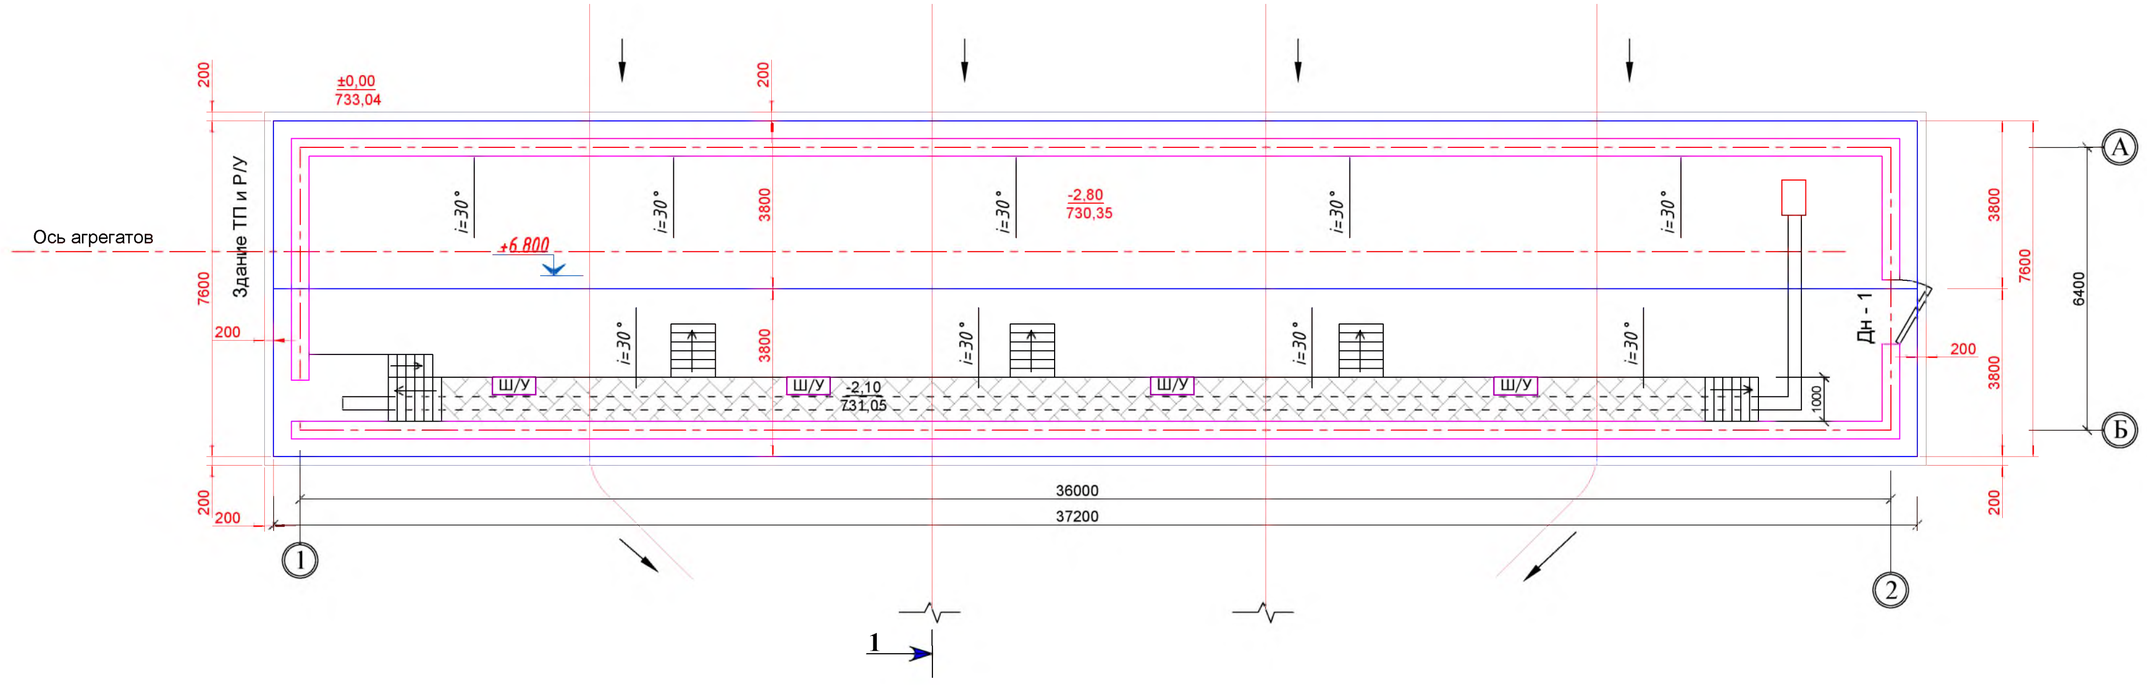

Спецификация водосточная элементов

	Наименование	Ед изм	К-во	Примеч
1	Желоб	пм	75,0	

Примечание

1. Данный лист рассматривать совместно с листом- 3,4,5 и ТХ.СО


Изм.	Кол.уч.	Лист	№ док.	Подп.	Дата	АС		
						"Баркарорсозии пойгоххои обкашии Лохур-0,Лохур-1,Лохур-2 ва Лохур-3 дар нохияи Рудаки"		
Разработ.		Файдуллоев О.				Насосной станции Лохур-2. Архитектурно-строительная часть.	Стадия	Лист	Листов
ГИП		Шомили У.					РП	5	6
Нач. отдел		Шомили У.				План кровли (на отметке ±0,000). Спецификация водосточная элементов.	ГУП "Проектный Институт "Точикгипроводхоз" Душанбе - 2026		
Норм. контр.		Хайбаров С.							

Согласовано


Инв. подл | Подпись и дата | Взамен инв.

Схема расположения деревянных элементов кровли

(на отметке +1,250)

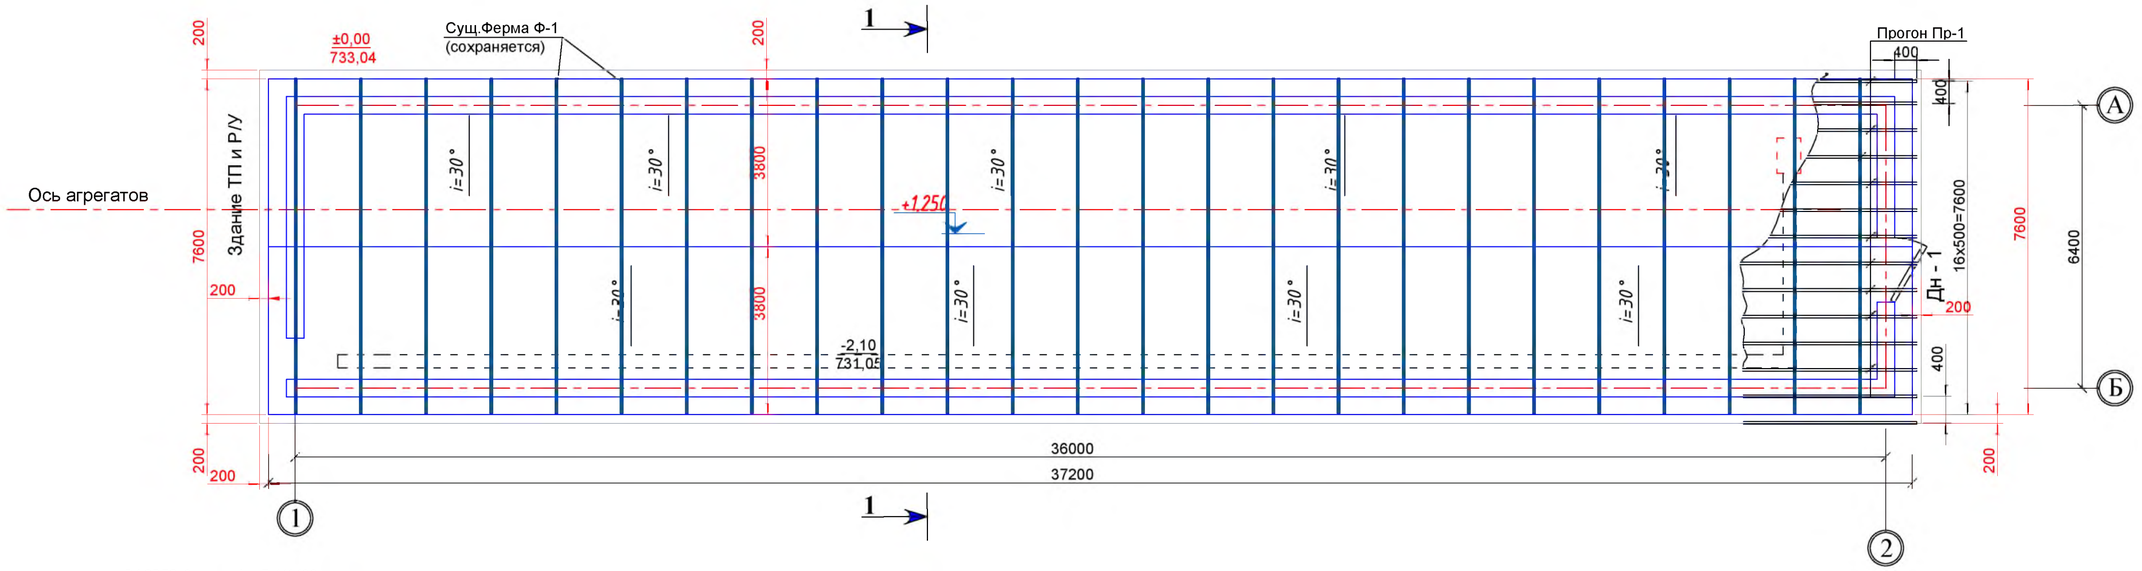

РАЗРЕЗ в осях А -Б М1:100

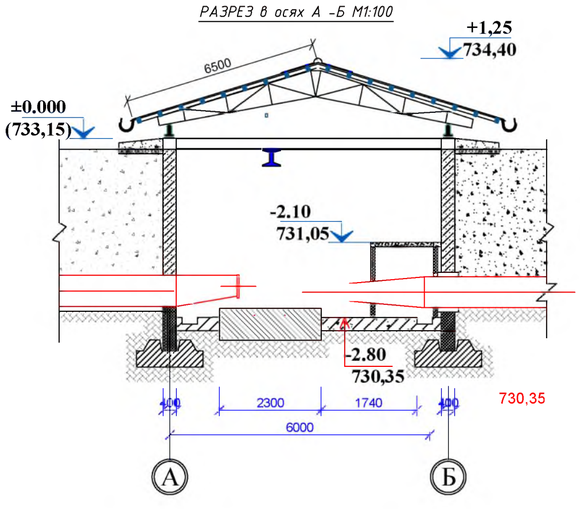

Спецификация

№ п/п	Обозначение	Наименование	Кол-во	Масса ед.кг	Примечание
		Существующий здание НС			
		Прогон ПР-1			
ПР-1	ГОСТ8639-82	Профиль 80х60х3 L=37200мм	16	229,15	3666,4кг
		Перекрытия			
		Волнистый листовой сталь t=0.05мм			483,60м²

Примечание

1. Данный лист рассматривать совместно с листом- 3,4,5 и ТХ.СО

Изм.	Кол.уч.	Лист	№ док.	Подп.	Дата	АС
						"Баркарорсозии пойгоххои обкашии Лохур-0,Лохур-1,Лохур-2 ва Лохур-3 дар нохияи Рудаки"
Разработ.		Файдуллоев О.				Насосной станции Лохур-2. Архитектурно-строительная часть.
ГИП		Шомили У.				Стадия: РП; Лист: 6; Листов: 6
Нач. отдел		Шомили У.				Схема расположения деревянных элементов кровли. Спецификация
Норм. контр.		Хайбаров С.				ГУП "Проектный Институт "Точикгипроводхоз" Душанбе - 2026

Согласовано

Инв. подл | Подпись и дата | Взамен инв.

Таб. 1

Ведомость основных комплектов рабочих чертежей		
Обозначение	**Наименование**	**Примечание**
1	2	3
ПЗ	Пояснительная записка	Книга-1
ТГИ	Инженерно-топогеодезический изысканий	Книга-2
НРР.ЮЖ	Напорно-регулирующий резервуар W=250м³	Альбом-1
ТХ и ТК	Площадка насосной станции I-го подъема. Технологическая часть и технологическая коммуникации	Альбом-2
АС	Площадка насосной станции I-го подъема. **Архитектурно-строительная часть**	Альбом-3
АС	**Насосной станции Суфи-Ориф. Дежурное помещение** **Архитектурно-строительная часть**	Альбом-4
АС	**Насосной станции Суфи-Ориф. Уборная на 1-го очко** **Архитектурно-строительная часть**	Альбом-5
ЭО	Электротехническая часть	Альбом-6
СМ	Сметная документация	Книга-3

Таб. 2

Ведомость рабочих чертежей основного комплекта **ТХ**		
Лист	**Наименование**	**Примечание**
1	2	3
1	Общие данные	
2	План здание трансформаторное помещение. Ведомость объёмов работ	
3	Фасад по А-Б и Б-А.	
4	План кровли.Спецификация	
5	Схема расположения деревянных элементов кровли.Спецификация	
6	Разрез 1-1;2-2. Узел "В" Спецификация	
7	Окна из металло-пластиковых профилей О-1,2,3 и 4. Спецификация.	
8	Вороты ВМ-1 и ВМ-2. Спецификация.	

Таб.3

Ведомость ссылочных и прилагаемых документов		
Обозначение	Наименование	Примечание
	Ссылочные документы	
ГОСТ 10704-91	Трубы металлические	
ГОСТ 9466-75	Электроды для дуговой сварки сталей и наплавки	
	классификация и общие технические условия	
ГОСТ 19903-74	Лист стальная	
30ч906бр	Задвижки с электроприводом	
ГОСТ 8509-93	Уголки стальные горячекатаные равнопрочные	
	Прилагаемые документы	
ТХ.СО-1	Спецификация основного оборудования насосной станции	2-листов

Настоящий проект выполнен в соответствии с
дествующими нормами и правилами,
в том числе по взрыво - пожарной безопасности.

Гл. инженер проекта Шомили У.

						АС
						"Баркарорсозии пойгоххои обкашии Лохур-0,Лохур-1,Лохур-2 ва Лохур-3 дар нохияи Рудаки"
Изм.	Кол.уч.	Лист	**№ док.**	Поди.	Дата	
Разработ.		**Фрайдунпоев О.**				Насосной станции Лохур-2. Архитектурно-строительная часть.
ГИП		Шомили У.				
Нач. отдел		Шомили У.				
Норм. контр.		Хайбаров С.				Общие данные.

Стадия	Лист	Листов
РП	1	8

ГУП "Проектный Институт "Точикгипроводхоз" Душанбе - 2026

Согласовано


Взамен инв.

Подпись и дата

Инв. подл

План здание трансформаторное помещение

М1:100

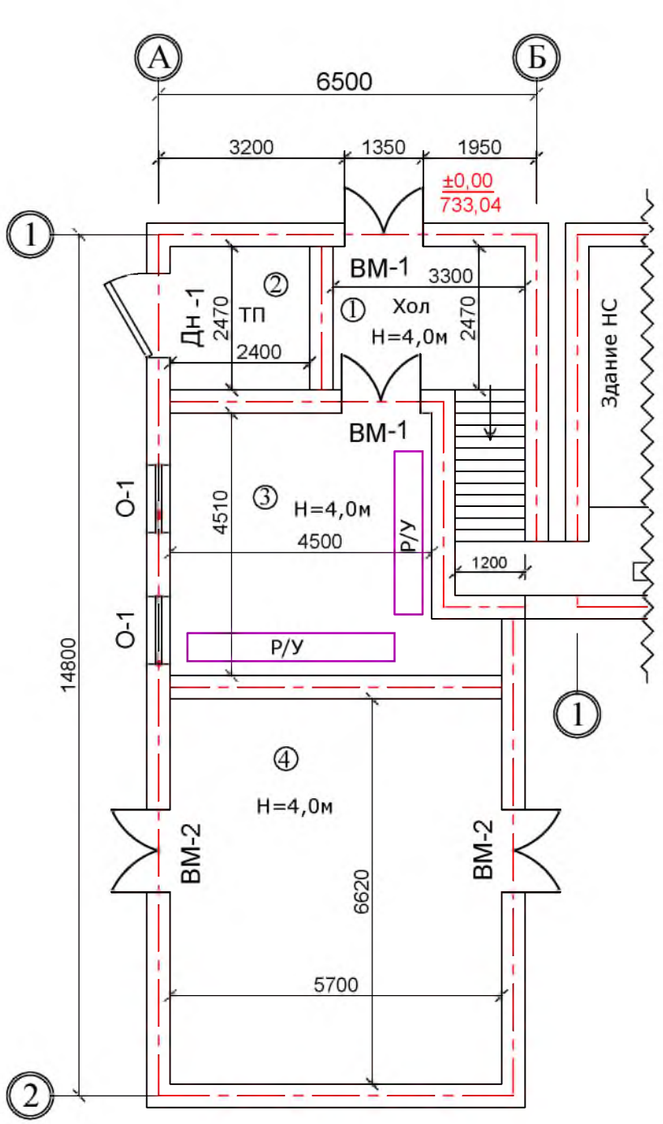

Ведомость объёмов работ				
№ п /п	Наименование	Ед. изм	Кол-во	Примечание
1	Демонтаж существующие деревянные оконные блоки раз:1200х1900мм (n=2,0шт)	м²	4,56	
2	Демонтаж существующие деревянные дверные блоки раз:1350х2350мм (n=2,0шт)	м²	6,345	
3	Демонтаж существующие деревянные дверные блоки раз:1420х2350мм (n=2,0шт)	м²	6,674	
4	Демонтаж существующие деревянные дверные блоки раз:1450х2100мм (n=1,0шт)	м²	3,045	
5	Очистка внутренных стены	м²	235,14	
6	Шпатлёвка, грунтовка и водоэмульционая краска внутренних стены и балки	м²	235,14	
7	Очистка потолка в ручную	м²	72,11	
8	Шпатлёвка, грунтовка и водоэмульционая окраска потолка за два раза	м²	72,11	
9	Очистка старый существующий штукатурка наружных стены	м²	238,16	
10	Устройства декоративной фасадной штукатурки наружных стены (дождик) - AMY TERAZIT Код: 223и 230	м²	238,16	
11	Устройство отмостка вокруг здания раз:100см t=10см из бетона В12,5	м³	4.50	
12	Окраска существующая лестница за два раза	м²	5,0	
13	Установка серанит на цокольный част наружных стен высотой h=60см	м²	30,0	
	Устройство пола			
14	Устройство пола из бетона В15 t=10см	м³	7,21	

Экспликация здании и сооружении

№ п/п	Наименование	Ед. измер.	Кол-во	Примечание
1	**Хол** раз:2,47х3,3х4,0м	шт	1,0	Существующий подлежит восстановление
2	**Помещение ТП** раз:2,4х2,47х4,0м	пм	1,0	Существующий подлежит восстановление
3	**Помещение Р/У** раз:4,5х4,51х4,0м	шт	1,0	Существующий подлежит восстановление
4	**Помещение складное** раз:5,7х6,62х4,0м	шт	1,0	Существующий подлежит восстановление

Примечание

1. Данный лист рассматривать совместно с листом- 3,4,5 и ТХ.СО

Согласовано

Взамен инв.

Подпись и дата


Инв. подл

						АС
						"Баркарорсозии пойгоххои обкашии Лохур-0,Лохур-1,Лохур-2 ва Лохур-3 дар нохияи Рудаки"
Изм.	Кол.уч.	Лист	№ док.	Подп.	Дата	
Разработ.		Фрайдунпосев О.				Насосной станции Лохур-2. Архитектурно-строительная часть.
ГИП		Шомили У.				
Нач. отдел		Шомили У.				
Норм. контр.		Хайбаров С.				План здание трансформаторное помещение. Ведомость объёмов работ


Стадия	Лист	Листов
РП	2	8

ГУП "Проектный Институт "Точикгипроводхоз" Душанбе - 2026


ФАСАД 1-3

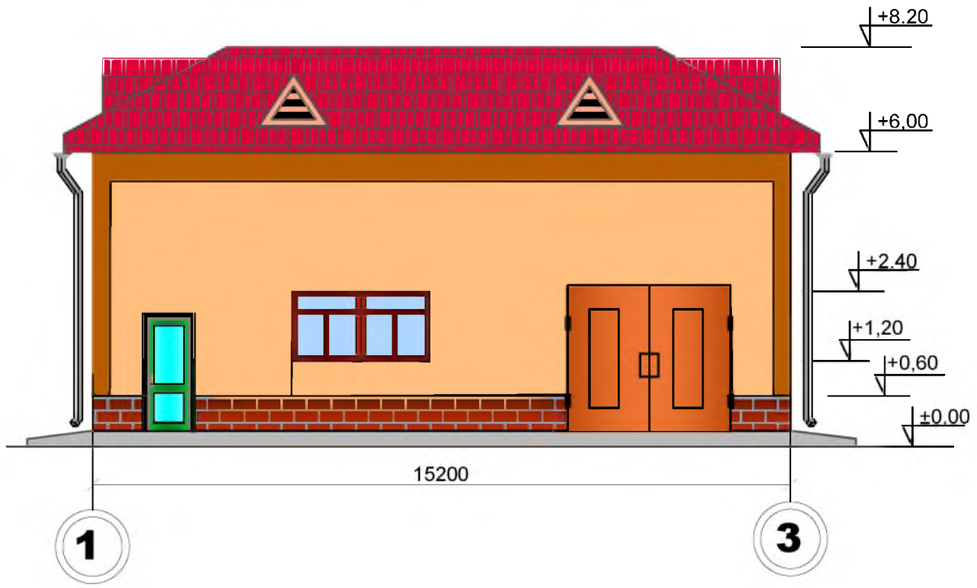

ФАСАД А-Б

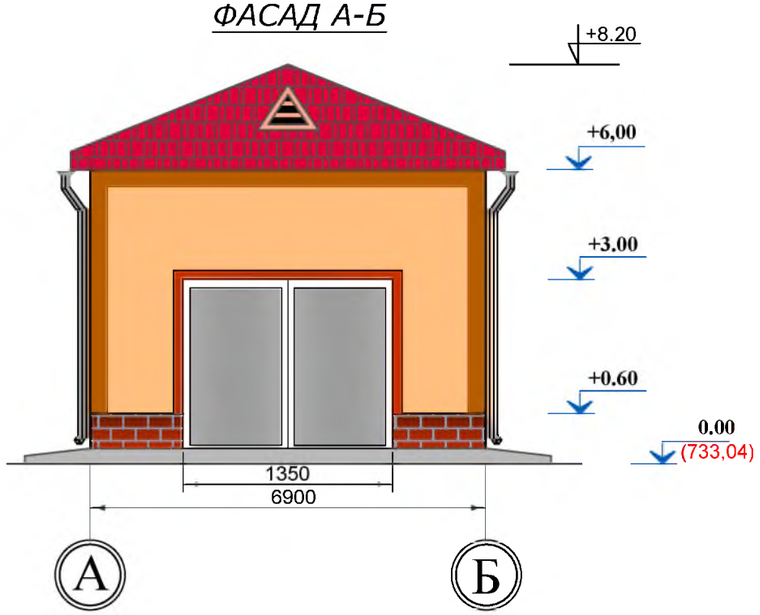

ФАСАД Б-А

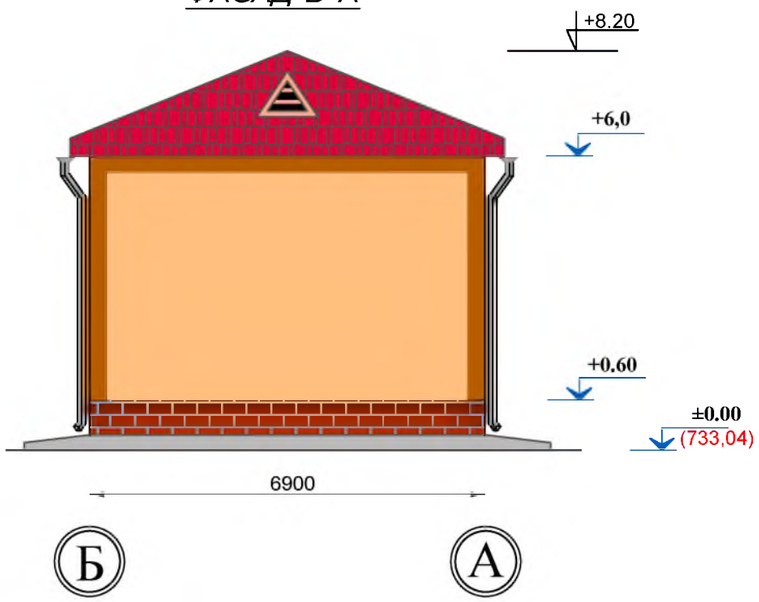

Согласовано


Взамен инв.

Подпись и дата

Инв. подл

						АС	
						"Баркарорсозии пойгоххои обкашии Лохур-0,Лохур-1,Лохур-2 ва Лохур-3 дар нохияи Рудаки"	
Изм.	Кол.уч.	Лист	№ док.	Подп.	Дата		
Разработ.		Фрайдуншоев О.				Насосной станции Лохур-2. Архитектурно-строительная часть.	Стадия: РП; Лист: 3; Листов: 8
ГИП		Шомили У.					
Нач. отдел		Шомили У.				Фасад по А-Б и Б-А.	ГУП "Проектный Институт "Точикгипроводхоз" Душанбе - 2026
Норм. контр.		Хайбаров С.					


План кровли
(на отметке +6,00)

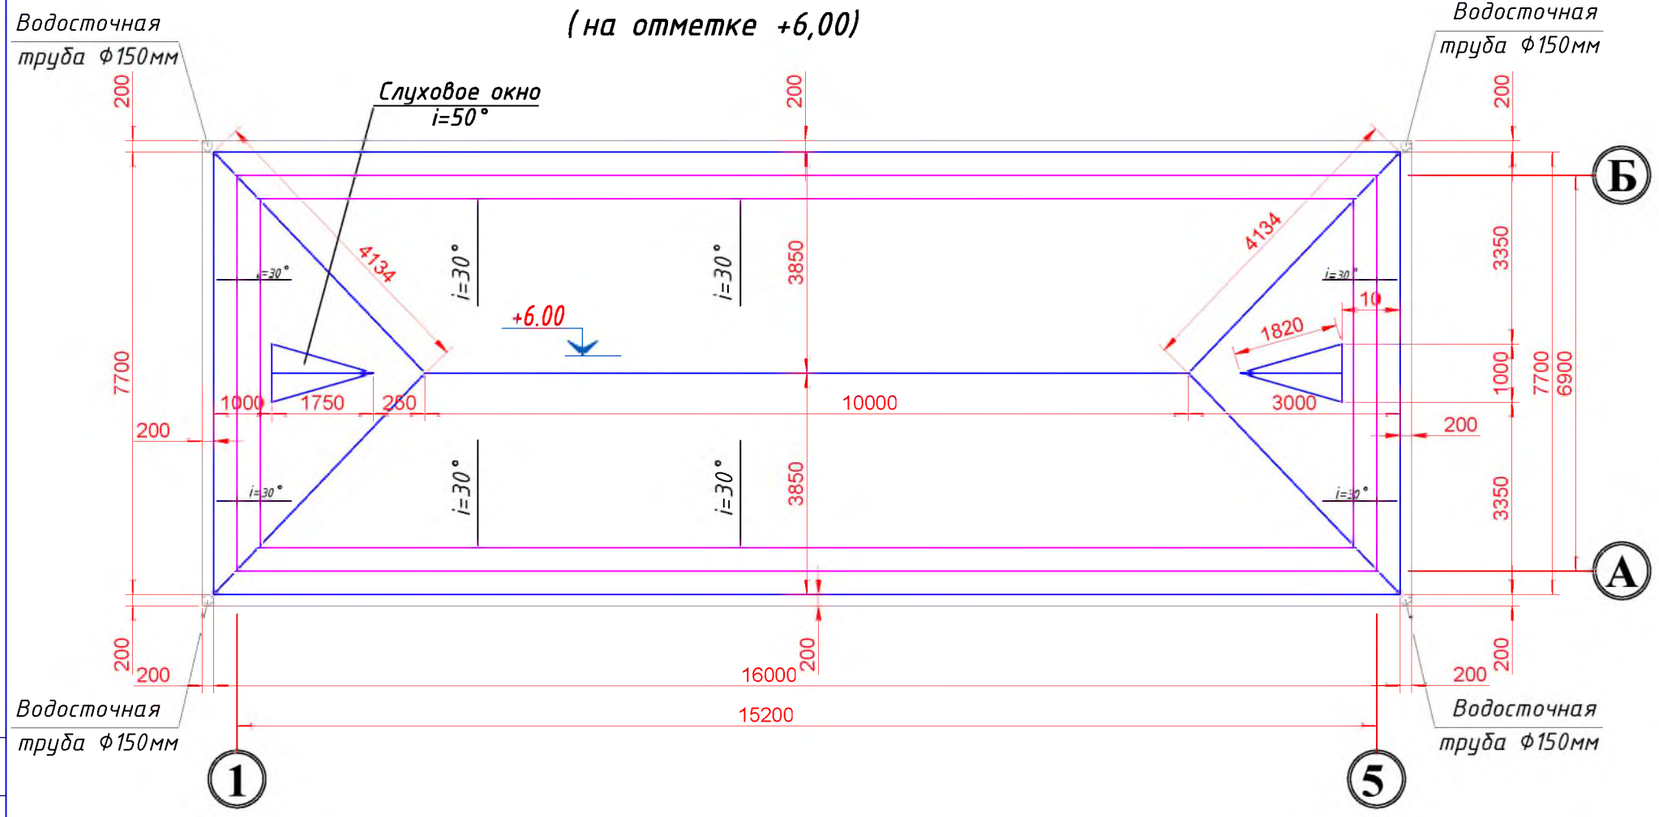


Спецификация водосточная элементов

	Наименование	Ед изм	Кол-во	Примечание
1	Желоб	пм	40,0	
2	**Водосточный труба Ø150** L=4800мм	шт	4,0	
3	Отвод 45° Ø150	шт	12,0	
4	Воронка Ø180-150	шт	4,0	
5	Коньковая деталь (фартук)	пм	23,0	


Узлы водосточных труб

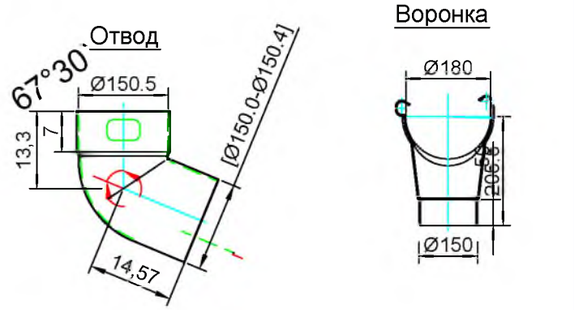


Верхнее колено 45°

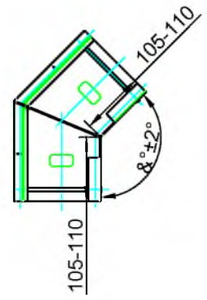

Труба

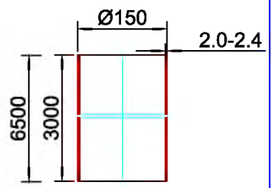

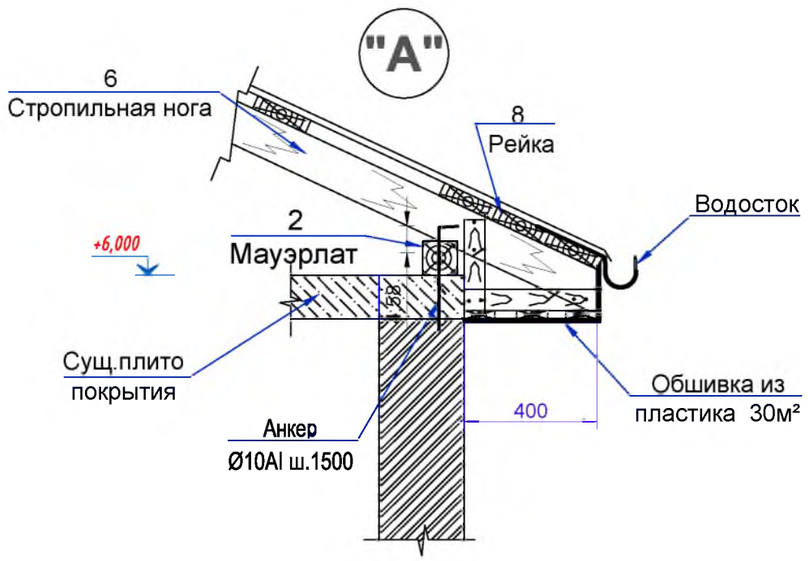

Примечание:

1. *Мауэрлат укладывается на слой толя и заанкеруются в перекрытию.*
2. *Кровля выполняется из металлочерепицы .*
3. *Все деревянные элементы антисептируется и покрываются специальном составом для повышения огнестойкости.*
4. *Спецификация элементов смотри на листе АС- 4; АС- 5;*
5. *Разрез 1-1, 2-2, 3-3, 4-4 смотри на листе АС-4; АС- 5; АС- 6;*
6. *Все узлы кровли выполнять по серии 2.160-6с в.1.*
7. *Все деревянные элементы антисептируются и покрываются специальным составом для повышения огнестойкости .*
8. *Деревянные элементы, соприкасающиеся с кирпичной кладкой обернуть толем .*
9. *Узлы кровли выполнены согласно по серии 2.160-6с "Узлы и детали кровля".*
10. *Кровля выполняется из металлочерепицы толщ. 0.05 мм.*
11. *Данный лист см. совместно с листом -2,3,5 И 6АС .*

Согласовано

Взамен инв.


Подпись и дата

Инв. подл


Изм.	Кол.уч.	Лист	№ док.	Подп.	Дата	АС		
						"Баркарорсозии пойгоххои обкашии Лохур-0,Лохур-1,Лохур-2 ва Лохур-3 дар нохияи Рудаки"		
Разработ.		Фрайдунпсев О.				Насосной станции Лохур-2. Архитектурно-строительная часть.	Стадия	Лист	Листов
ГИП		Шомили У.					РП	4	8
Нач. отдел		Шомили У.				План кровли.Спецификация	ГУП "Проектный Институт "Точикгипроводхоз" Душанбе - 2026		
Норм. контр.		Хайбаров С.							


Схема расположения деревянных элементов кровли

(на отметке +8,200)

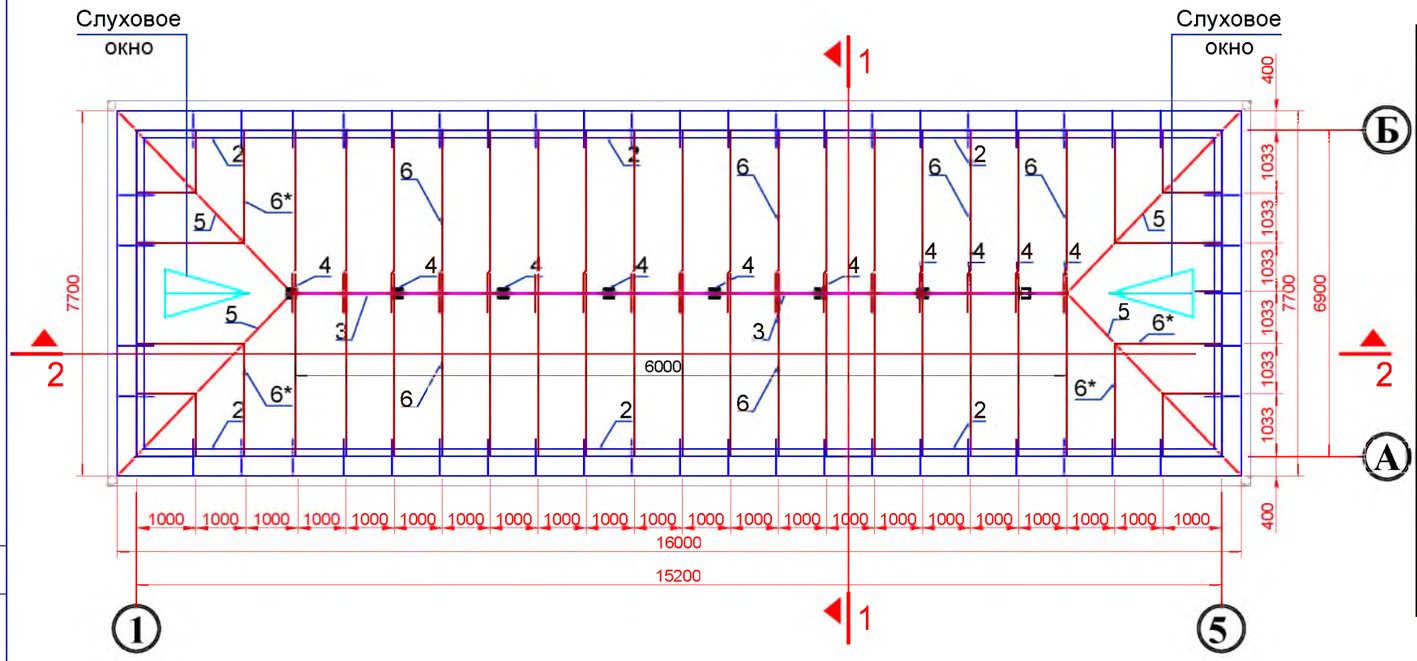

Разрез 1-1

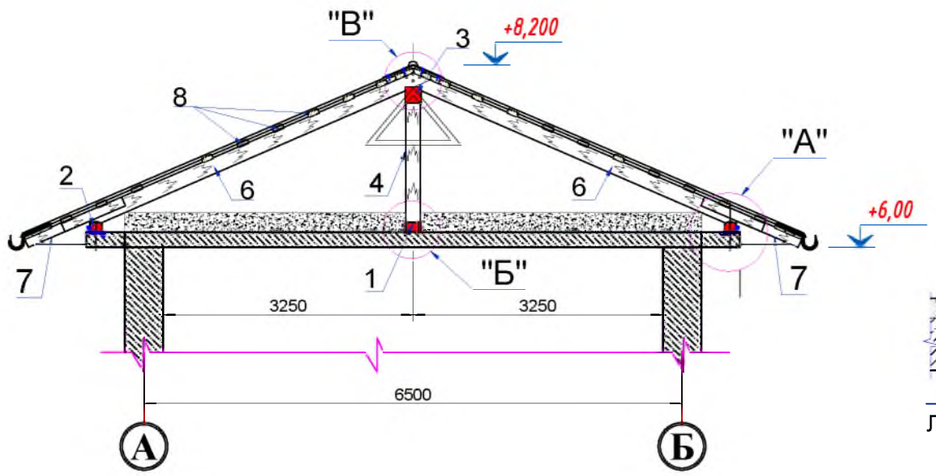


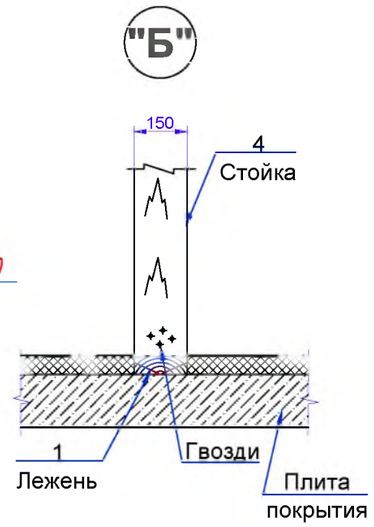

Спецификация на один элемент

Поз.	Обозначение	Сечение a, мм	Сечение b, мм	Сечение L, м, см	Колич. шт	Объем. м³.	Примечание
1	Лежень	100	150	6,0	1	0.090	
2	Мауэрлат	80	100	36,40	1	0.291	
3	Прогон	150	150	6,0	1	0.135	
4	Стойка	150	150	2,20	4	0.198	
5	Диагональная нога	50	200	4,60	4	0.184	
6	Стропильная нога	50	150	3,80	18	0.513	
6*	Стропильная нога	50	150	1,90	14	0.200	Lср=1,90м
7	Кобылка	40	120	0,8	36	0.138	
8	Рейка шаг:400мм	50	100	227,0	1	1.135	
9	Профилированный настил t=0.05мм					140м²	
10	Обшивка из пластика					16м²	
11	Металлическая хомут для крепления мвуэрлат шаг: 1м	50х5мм			40	27кг	
12	Металлическая анкеры для крепления хомут	10мм			72		

Металлический хомут для крепления мауэрлата на плата перекрытия

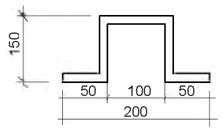

Примечание:

1. Мауэрлат укладывается на слой толя и заанкеруются в перекрытию.
2. Кровля выполняется из металлочерепицы или в олнистые стальн. листы t=0.05мм 140м².
3. Все деревянные элементы антисептируется и покрываются специальном составом для повышения огнестойкости.
4. Схема расположения элементов и спецификация элементов смотри на листе АС- 4.

						АС
						"Баркарорсозии пойгоххои обкашии Лохур-0,Лохур-1,Лохур-2 ва Лохур-3 дар нохияи Рудаки"
Изм.	Кол.уч.	Лист	№ док.	Подп.	Дата	
Разработ.		Фойдуллоев О.				Насосной станции Лохур-2. Архитектурно-строительная часть.
ГИП		Шомили У.				
Нач. отдел		Шомили У.				Схема расположения деревянных элементов кровли.Спецификация
Норм. контр.		Хайбаров С.				


Стадия	Лист	Листов
РП	5	8

ГУП "Проектный Институт "Точикгипроводхоз" Душанбе - 2026


Согласовано

Инв. подл | Подпись и дата | Взамен инв.


Разрез 2-2

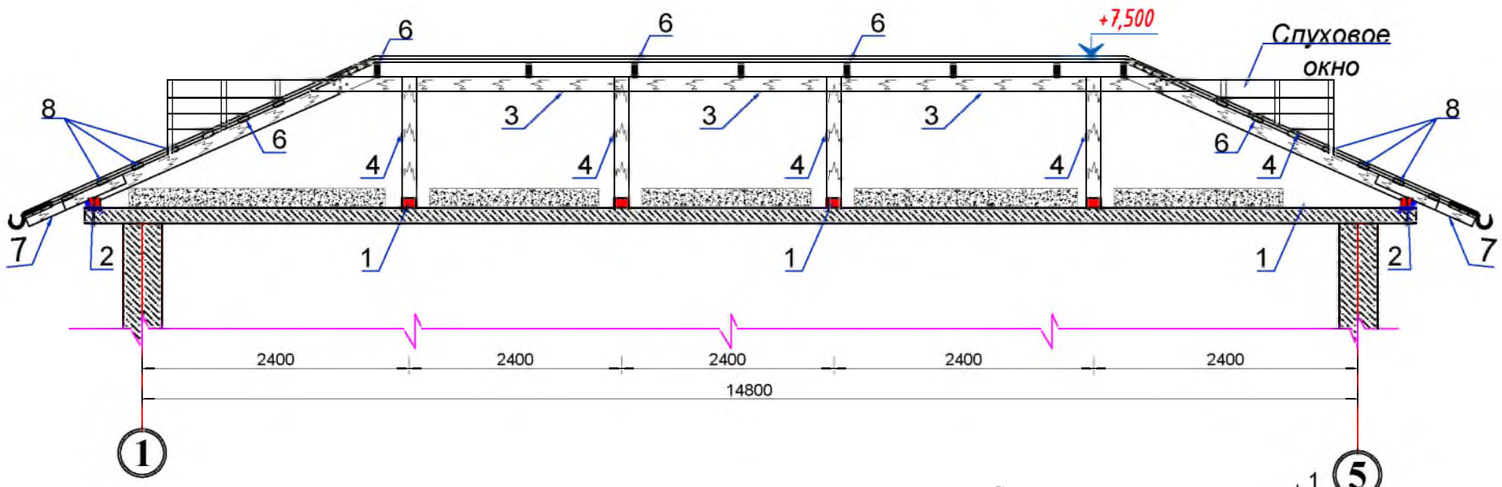


Слуховое окно

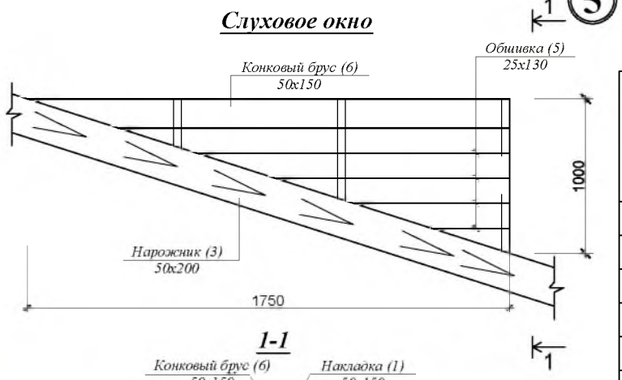

1-1

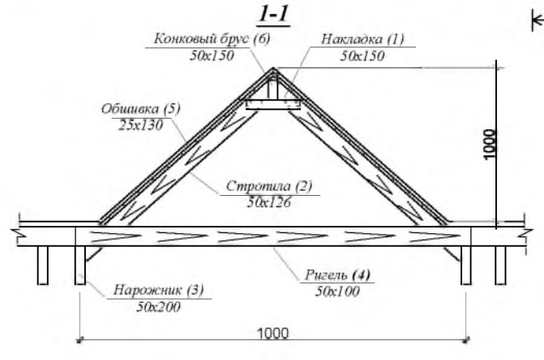

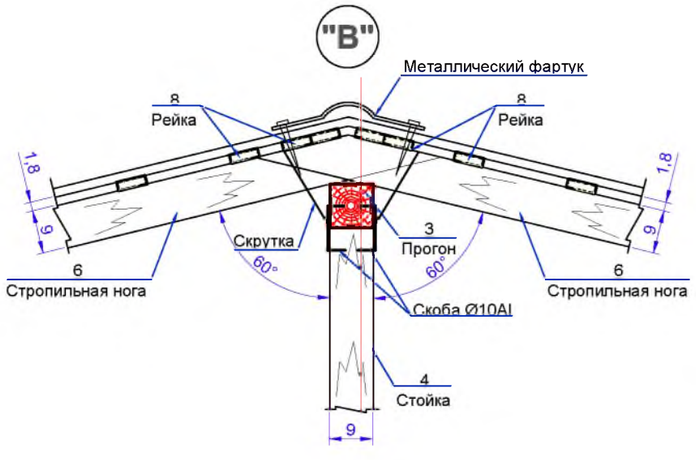

Спецификация слуховых окон

№ п/п	Наименование	Сечение мм х мм	Колич. шт.	Длина в м.		Объём м³	Примеч.
				на один	всего		
		Расход на 1 слуховое окно			2шт		
1	Накладка	50x150	1	0.30	0.30	0.002	
2	Стропила	50x126	--	--	7.0	0.044	
3	Нарожник	50x200	2	4,0	8	0,08	
4	Ригель	50x100	1	2.2	2.2	0,011	
5	Обшивка	25x130	--	--	30,6	0,10	
6	Коньковый брус	50x150	1	4,0	4,0	0,03	

Согласовано

Инв. подл | Подпись и дата | Взамен инв.

Изм.	Кол.уч.	Лист	№ док.	Подп.	Дата
Разработ.		Фрайдунпоев О.			
ГИП		Шомили У.			
Нач. отдел		Шомили У.			
Норм. контр.		Хайбаров С.			

АС

"Баркарорсозии пойгоххои обкашии Лохур-0,Лохур-1,Лохур-2 ва Лохур-3 дар нохияи Рудаки"

Насосной станции Лохур-2.
Архитектурно-строительная часть.


Стадия	Лист	Листов
РП	6	8

Разрез 1-1;2-2. Узел "В"
Спецификация


ГУП "Проектный Институт "Точикгипроводхоз"
Душанбе - 2026

Окна из металлопластиковых профилей

О-1

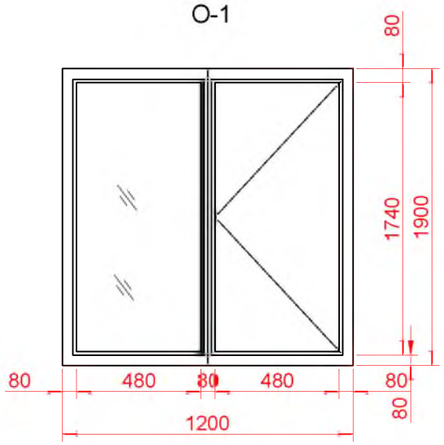


Сетка для окно. О-1

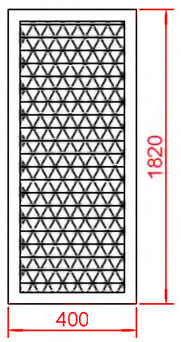

Спецификация заполнения оконных и дверных проемов

№ поз.	Наименование	Размеры проема (ммхмм)	Количество	Всего	Примечание
1	О-1	1200 x 1900	2	2	металлопластик
2	Сетки	400 x 1820	2	2	металлопластик
3	Д-1	1450 x 2100	1	1	аллюминиевое

Д - 1

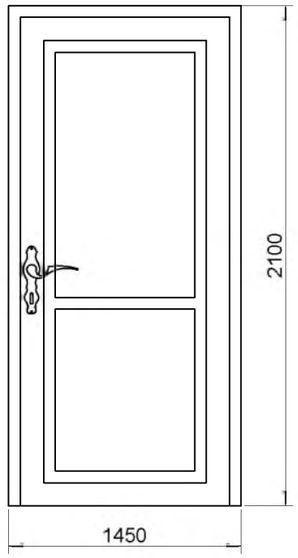

Примечание:

1. **Все окна и двери оборудуются навесами, ручками для открывания, замками в заводских условиях.**
2. **Размеры блоков окон и дверей даны по размеру проемов. Фирмам-изготовителям уточнить габариты блоков по месту, оставить монтажный зазор.**
3. **Размеры даны в мм**
4. **Данный лист рассматривать совместно с листами-2,3 и 5**

Согласовано


Взамен инв.

Подпись и дата


Инв. подл

Изм.	Кол.уч.	Лист	№ док.	Поди.	Дата	АС		
						"Баркарорсозии пойгоххои обкашии Лохур-0,Лохур-1,Лохур-2 ва Лохур-3 дар нохияи Рудаки"		
Разработ.		Фрайдунпосев О.				Насосной станции Лохур-2. Архитектурно-строительная часть.	Стадия: РП	Лист: 7 / Листов: 8
ГИП		Шомили У.						
Нач. отдел		Шомили У.				Окна из металло-пластиковых профилей О-1,2,3 и 4. Спецификация.	ГУП "Проектный Институт "Точикгипроводхоз" Душанбе - 2026	
Норм. контр.		Хайбаров С.						

Ворота ВМ-1

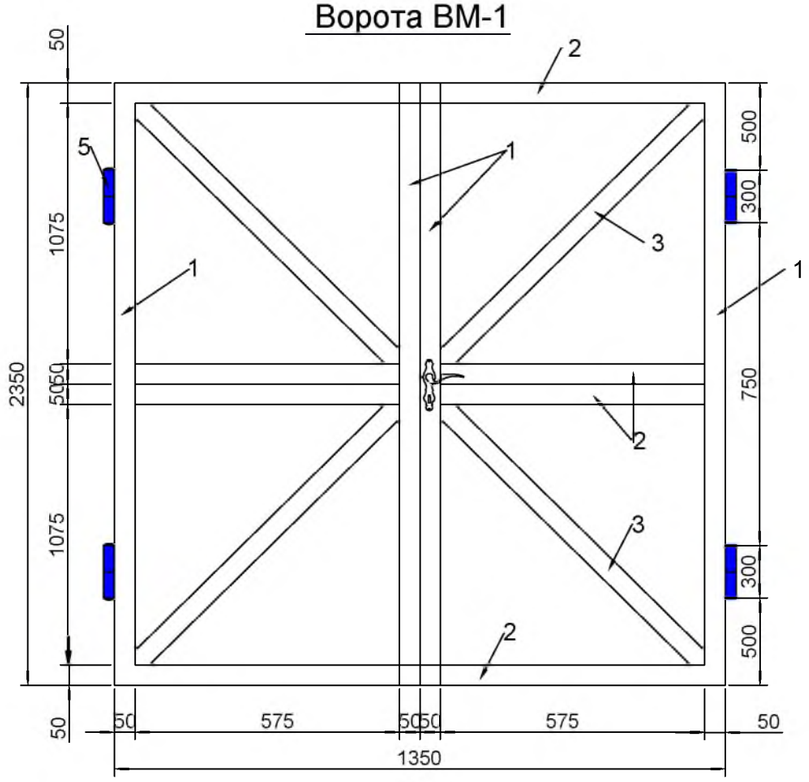

Ворота ВМ-2

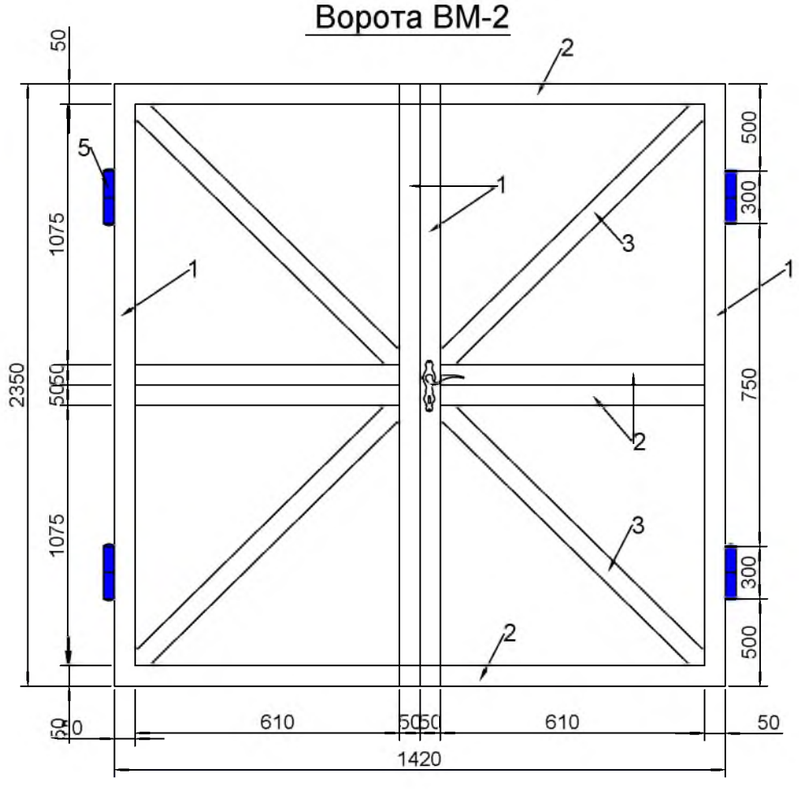

Спецификация дано на 1-го ворота

№№	Обозначение	Наименование	Кол-во	Масса ед.кг	Примечание
	Ворота ВМ-1 для Насосной станции				
1	ГОСТ 8509-72	Уголок L50x5 L=2850мм	4	10,744	42,976
2	ГОСТ 8509-72	Уголок L50x6 L=1550мм	4	5,843	23,372
3	ГОСТ 8509-72	Уголок L50x6 L=1360мм	4	5,13	20,52
4	ГОСТ 19903-74	Обшивка из листовой сталь δ=1,5мм F=3,173м²	1	37,36	
5	Серия 3.017-1 вып.6	Петля	4	1,33	5,32
6	Серия 3.017-1 вып.6	Ручка	1	1,93	
7	Серия 3.017-1 вып.6	Защелка 100 СБ	1	2,0	
	Ворота ВМ-2 для Насосной станции				
1	ГОСТ 8509-72	Уголок L50x5 L=2850мм	4	10,744	42,976
2	ГОСТ 8509-72	Уголок L50x5 L=1620мм	4	6,11	24,44
3	ГОСТ 8509-72	Уголок L50x6 L=1600мм	4	6,032	24,128
4	ГОСТ 19903-74	Обшивка из листовой сталь δ=1,5мм F=3,340м²	1	31,435	
5	Серия 3.017-1 вып.6	Петля	4	1,33	5,32
6	Серия 3.017-1 вып.6	Ручка	1	1,93	
7	Серия 3.017-1 вып.6	Защелка 100 СБ	1	2,0	

Примечание:

2.Все окна и двери оборудуются навесами, ручками для открывания, замками в заводских условиях.

3. Размеры блоков окон и дверей даны по размеру проемов. Фирмам-изготовителям уточнить габариты блоков по месту, оставить монтажный зазор.

4. Данный лист рассматривать совместно с лист-2,3,4,6,7,8 и 9

5. Спецификация дано на 1-го ворота всего по ВМ-1 и ВМ-2 -4шт

Согласовано

Взамен инв.

Подпись и дата

Инв. подл

						АС
						"Баркарорсозии пойгоххои обкашии Лохур-0,Лохур-1,Лохур-2 ва Лохур-3 дар нохияи Рудаки"
Изм.	Кол.уч.	Лист	№ док.	Поди.	Дата	
Разработ.		Фрайдунпосев О.				Насосной станции Лохур-2. Архитектурно-строительная часть.
ГИП		Шомили У.				
Нач. отдел		Шомили У.				
Норм. контр.		Хайбаров С.				Вороты ВМ-1 и ВМ-2. Спецификация.

Стадия	Лист	Листов
РП	8	8

ГУП "Проектный Институт "Точикгипроводхоз" Душанбе - 2026