АГЕНТСТВО ПО МЕЛИОРАЦИИ И ИРРИГАЦИИ
ПРИ ПРАВИТЕЛЬСТВЕ РЕСПУБЛИКИ ТАДЖИКИСТАН

ГУП "ПРОЕКТНЫЙ ИНСТИТУТ
"ТАДЖИКГИПРОВОДХОЗ"

РАБОЧИЙ ПРОЕКТ

"Баркарорсозии пойгоххои обкашии Лохур-0,Лохур-1,Лохур-2 ва Лохур-3 дар нохияи Рудаки"

АЛЬБОМ-1

Насосной станции Лохур-3.
Технологическая часть (ТХ)

ДУШАНБЕ-2026

АГЕНТСТВО ПО МЕЛИОРАЦИИ И ИРРИГАЦИИ
ПРИ ПРАВИТЕЛЬСТВЕ РЕСПУБЛИКИ ТАДЖИКИСТАН

ГУП "ПРОЕКТНЫЙ ИНСТИТУТ
"ТАДЖИКГИПРОВОДХОЗ"

РАБОЧИЙ ПРОЕКТ

"Баркарорсозии пойгоххои обкашии Лохур-0,Лохур-1,Лохур-2 ва Лохур-3 дар нохияи Рудаки"

АЛЬБОМ-1

Насосной станции Лохур-3.
Технологическая часть (ТХ)

ГЛ. ИНЖЕНЕР ИНСТИТУТА: ХАЙБАРОВ С.

ГЛ. ИНЖЕНЕР ПРОЕКТА: ШОМИЛИ У.

ДУШАНБЕ-2026

Таб. 1

Ведомость основных комплектов рабочих чертежей		
Обозначение	**Наименование**	**Примечание**
1	2	3
.ПЗ	Пояснительная записка	Книга-1
ТГИ	Инженерно-топогеодезический изысканий	Книга-2
ИГИ	Инженерно-геологический и гидрогеологичекий изысканий	Книга-3
ТХ	**Насосной станции Лохур-3.** Технологическая часть	Альбом-1
ГР	**Насосной станции Лохур-3.** Гидротехническое решение	Альбом-2
АС	**Насосной станции Лохур-3. Архитектурно-строительная часть**	Альбом-3
АС	**Насосной станции Лохур-3. Дежурное помещение Архитектурно-строительная часть**	Альбом-4
АС	**Насосной станции Лохур-3. Уборная на 1-го очко Архитектурно-строительная часть**	Альбом-5
ЭО	Электротехническая часть	Альбом-6
СМ	Сметная документация	Книга-4

Таб. 2

Ведомость рабочих чертежей основного комплекта **ТХ**		
Лист	**Наименование**	**Примечание**
1	2	3
1	Общие данные	
2	План площадка насосной станции М1:500. Экспликация и ведомость объёмов работ.	
3	План размещение гидромеханического оборудование насосной станции М1:100.	
4	Разрез в осях 1 -2. М1:100. Ведомость объёмов демонтажных работ	
5	Характеристика насоса типа KQSN800-M17-625	
6	Монтажный чертеж насоса KQSN800-M17-625	
7	Характеристика насоса типа KQSN700-M9J-869	
8	Монтажный чертеж насоса KQSN700-M9J-869	
9	Фундамент под агрегат.Ведомость объёмов работ	
10	План насосной станции. План дренажная система. М1:100	
11	Установочный чертёж дренажного-насоса. Спецификация	
12	Спецификация оборудования и материалов	

Настоящий проект выполнен в соответствии с
дествующими нормами и правилами,
в том числе по взрыво - пожарной безопасности.

Гл. инженер проекта Шомили У.

Таб.3

Ведомость ссылочных и прилагаемых документов		
Обозначение	Наименование	Примечание
	Ссылочные документы	
ГОСТ 10704-91	Трубы металлические	
ГОСТ 9466-75	Электроды для дуговой сварки сталей и наплавки	
	классификация и общие технические условия	
ГОСТ 19903-74	Лист стальная	
30ч906бр	Задвижки с электроприводом	
ГОСТ 8509-93	Уголки стальные горячекатаные равнопрочные	
	Прилагаемые документы	
ТХ.СО-1	Спецификация основного оборудования насосной станции	2-листов

Согласовано

Взамен инв.

Подпись и дата


Инв. подл

						ТХ
						"Баркарорсозии пойгоххои обкашии Лохур-0,Лохур-1,Лохур-2 ва Лохур-3 дар нохияи Рудаки"
Изм.	Кол.уч.	Лист	№ док.	Подп.	Дата	
Разработ.		Фрайдунпоев О.				Насосной станции Лохур-3. Технологическая часть (ТХ).
ГИП		Шомили У.				
Нач. отдел		Шомили У.				
Норм. контр.		Хайбаров С.				Общие данные.

Стадия	Лист	Листов
РП	1	12

ГУП "Проектный Институт "Точикгипроводхоз" Душанбе - 2026

План площадка насосной станции Лохур-3 II-го подъема М1:500

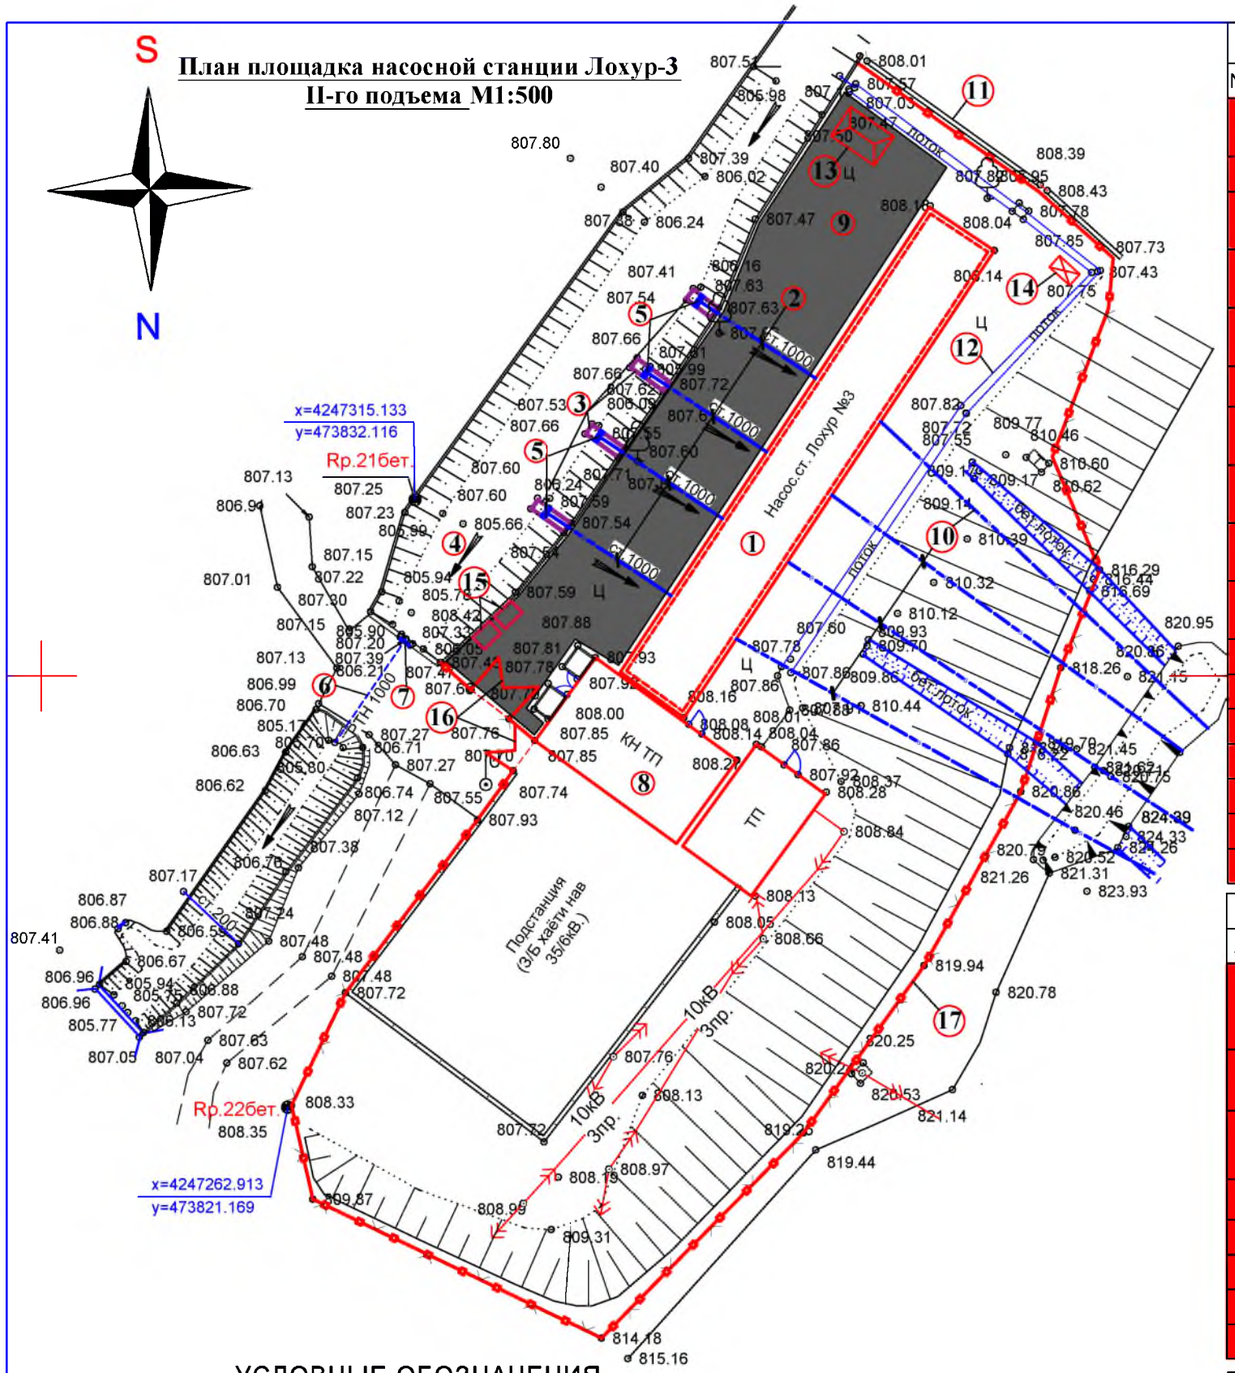

УСЛОВНЫЕ ОБОЗНАЧЕНИЯ

- Напорный и всасывающий трубопровод
- Сбросной труба
- Сетчатое ограждение
- А - Внутри площадочная подъездная асфальтная дорога

Экспликация зданий и сооружений

№ п/п	Наименование	Ед. измер.	Кол-во	Примечание
1	Здание насосной станции раз:6,0х47,0м	шт	1,0	Существующий подлежит восстановление
2	Всасывающий трубопровод Ø=1000мм, (4-нитки)	пм	56,0	Существующий сохраняется
3	Служебная площадка раз:1,0х3,50м	шт	4,0	Существующий подлежит восстановление
4	Аванкамера раз: 7,0х57,0м	шт	1,0	Существующий подлежит восстановление
5	Установка шит затвор ГС 1,0х1,0м	шт	4,0	Существующий подлежит восстановление
6	Сбросной труба РТН Ø=1000мм	пм	11,0	Существующий сохраняется
7	Сбросной затвор ГС 1,0х2,10м	шт	1,0	Существующий подлежит восстановление
8	Здание трансформаторная подстанция раз: 6,70х15,0м	шт	1,0	Существующий подлежит восстановление
9	Внутри площадочная подъездная асфальтная дорога Вср=11,0м	пм	61,0	Существующий подлежит восстановление
10	Напорный водовод D=1000мм (от здание НС до точ. подключение до напорный бассейн 4-нитки)	пм	416,0	Существующий сохраняется
11	Бетонная стенка t=40см	пм	28,0	Существующий сохраняется
12	Бетонный лоток ЛР-100	пм	70,0	Существующий сохраняется
13	Дежурное помещение раз: 3,5 х 4,0м	шт	1,0	Проектируемый
14	Уборная на 1-о очко раз:1,30х2.35х3.0м	шт	1,0	Проектируемый
15	Мусорный контейнер	шт	2,0	Проектируемый
16	Металлическая ворота В=4,0м,Н=2,0м	шт	2,0	Проектируемый
17	Ограждение территории	пм	210,0	Проектируемый

Ведомость объёмов работ

№ п/п	Наименование	Ед. изм	кол-во	Примечание
1	Разборка и восстановление внутри-площадочный асфальтобетонная покрытия t=10,0см (Вср=11м) с учетом площадка НС	м²	671,0	Lоб=61,0м
2	Устройства основания автодорога из гравийно песчаной смеси t=10см - щебня t=5см	м² м²	671,0	
3	Асфалтобетонная покрытия крупнозернистый t=6,0см мелкозернистый t=4,0см	м² м²	671,0	
4	Установка сетчатое ограждение территории В=2,0м, Н=2,0м	пм/ шт	210/ 105	см. лист.
5	Приобретение и установка металлические ворота раз :4,0х2,0м	шт	2	см. лист.
6	Установка мусорного контейнера раз:3х2м	шт	2	Рыночное
7	Устройство здание дежурное помещение раз:3,0х4,5м	шт	1	см.лист-
8	Устройство здание уборное раз:1,3х1,8м	шт	1	см.лист-

ТХ

"Баркарорсозии пойгоххои обкашии Лохур-0,Лохур-1,Лохур-2 ва Лохур-3 дар нохияи Рудаки"


Изм.	Кол.уч.	Лист	№ док.	Подп.	Дата
Разработ.		Фрайдунпоев О.			
ГИП		Шомили У.			
Нач. отдел		Шомили У.			
Норм. контр.		Хайбаров С.			

Насосной станции Лохур-1. Технологическая часть (ТХ).

Стадия	Лист	Листов
РП	2	12

План площадка насосной станции М1:500. Экспликация и ведомость объёмов работ.

ГУП "Проектный Институт "Точикгипроводхоз" Душанбе - 2026

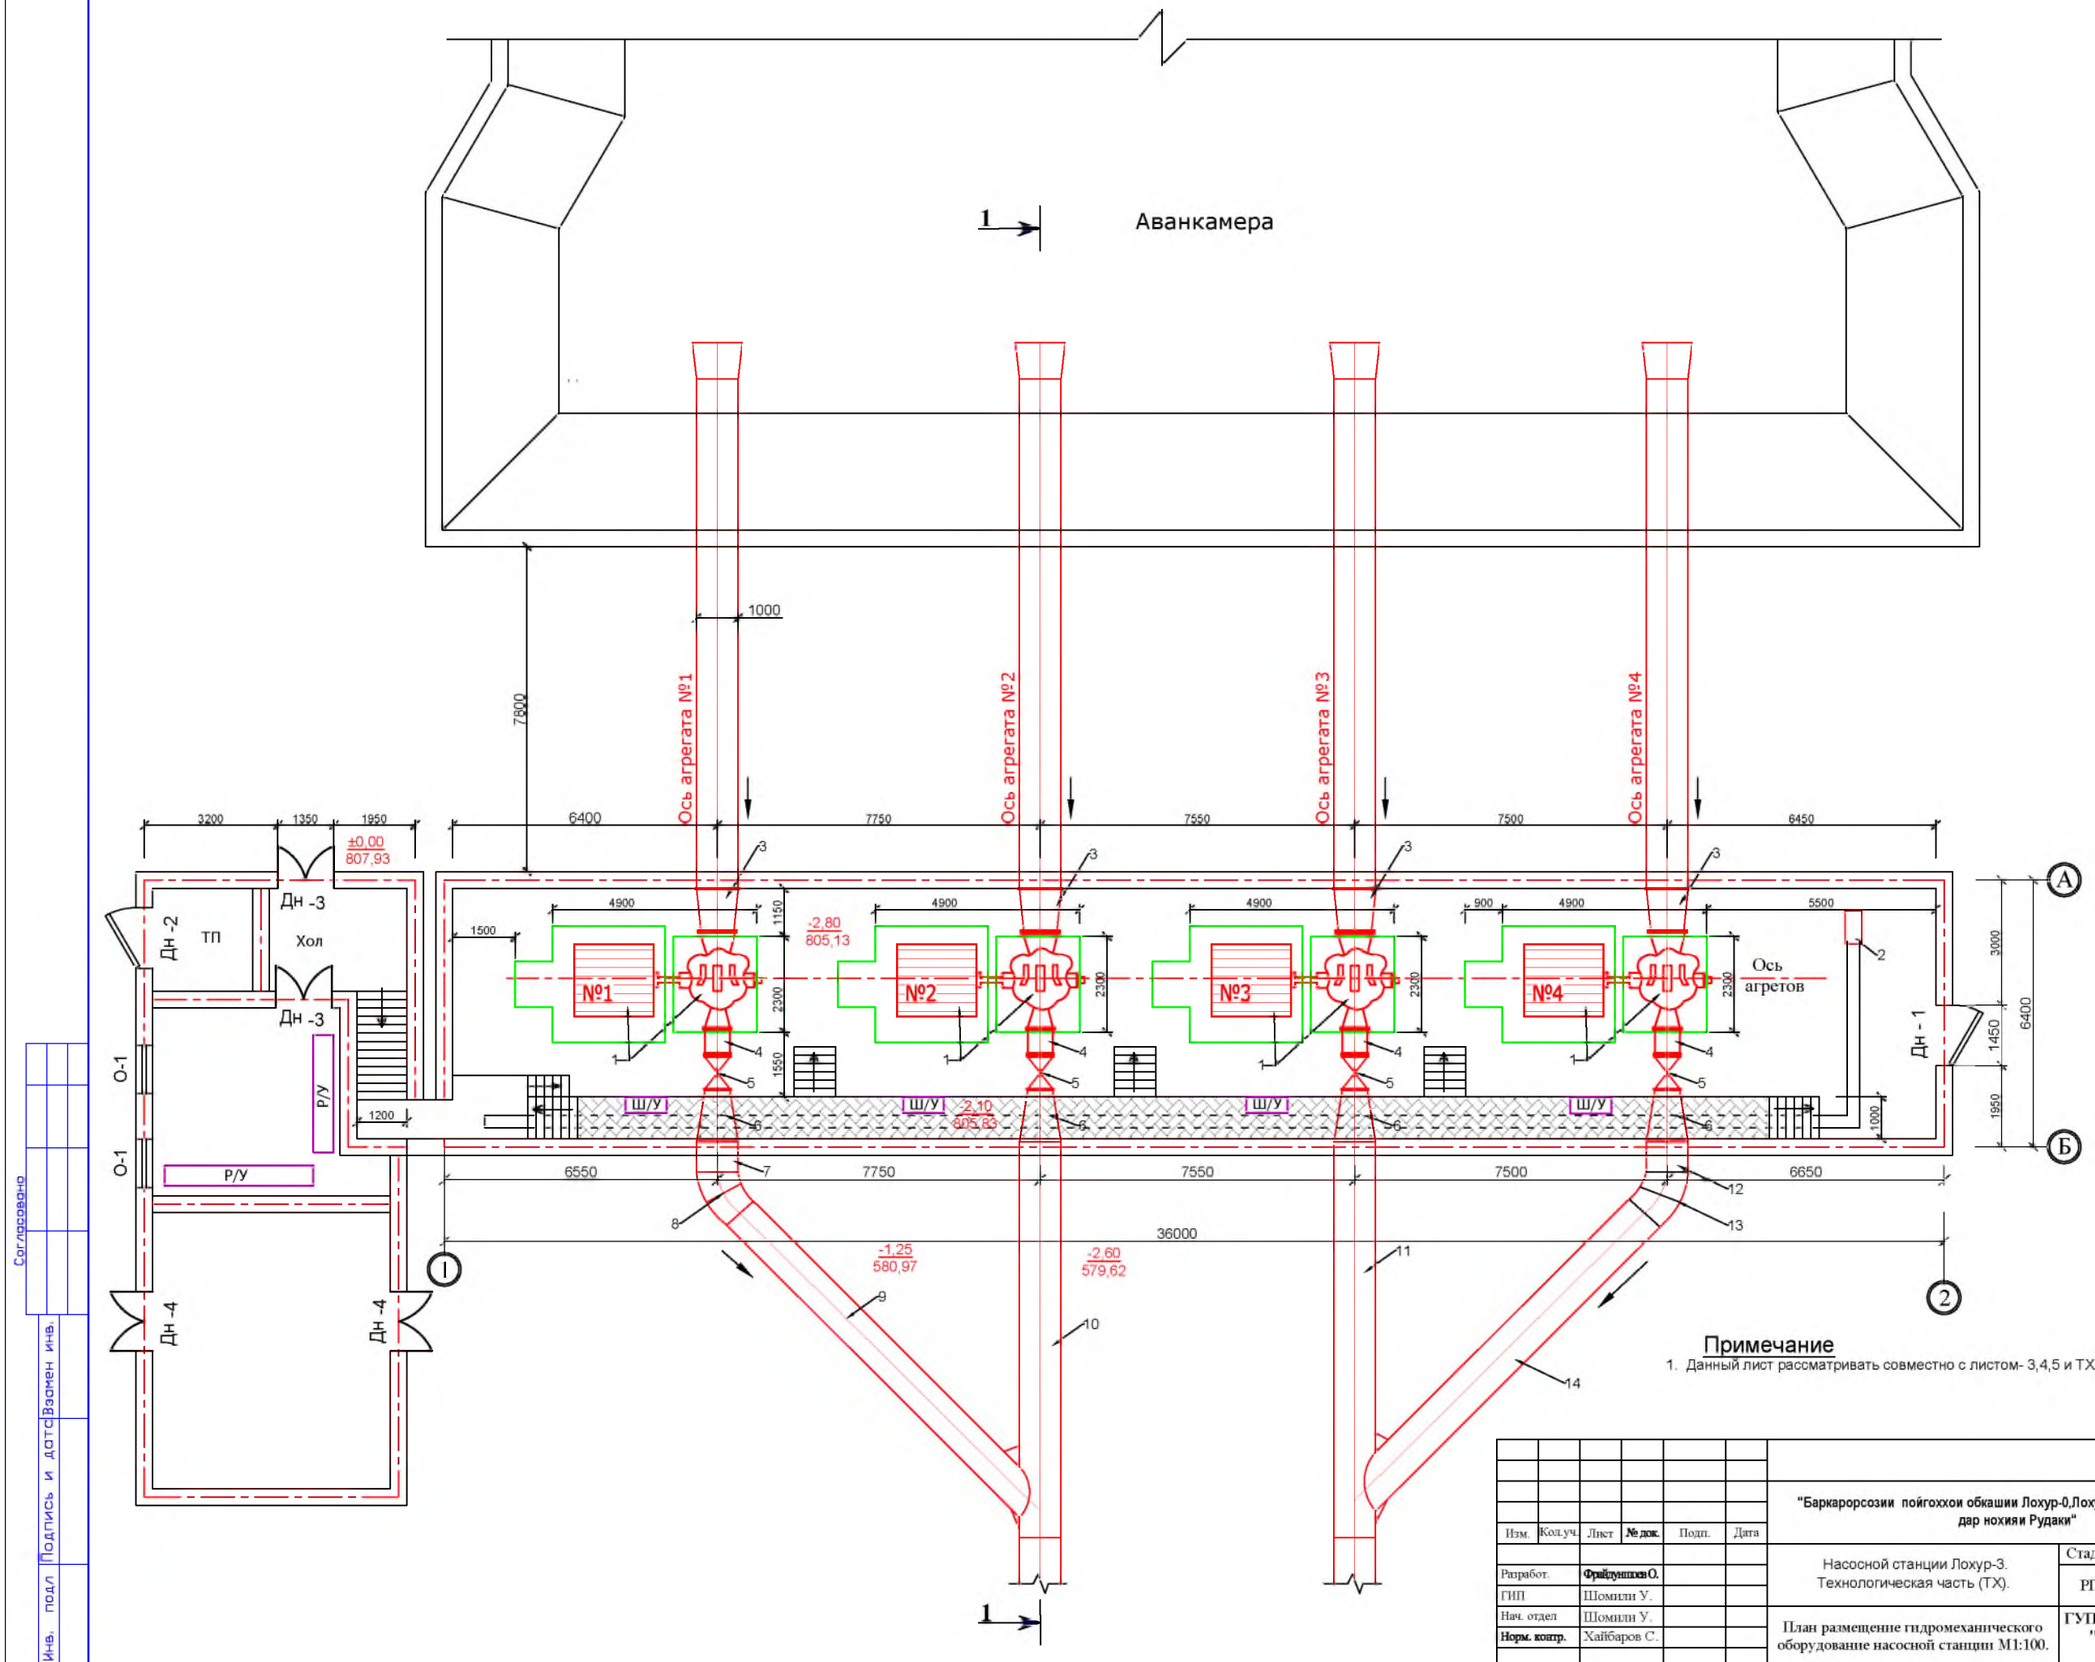


						ТХ	
						"Баркарорсозии пойгоххои обкашии Лохур-0,Лохур-1,Лохур-2 ва Лохур-3 дар нохияи Рудаки"	
Изм.	Кол.уч.	Лист	№ док.	Подп.	Дата		
Разработ.		Фрайдунзода О.				Насосной станции Лохур-3. Технологическая часть (ТХ).	Стадия: РП; Лист: 3; Листов: 12
ГИП		Шомили У.					
Нач. отдел		Шомили У.				План размещение гидромеханического оборудование насосной станции М1:100.	ГУП "Проектный Институт "Точикгипроводхоз" Душанбе - 2026
Норм. контр.		Хайбаров С.					

Согласовано


Инв. подл | Подпись и дата | Взамен инв.

РАЗРЕЗ в осях А –Б М1:100

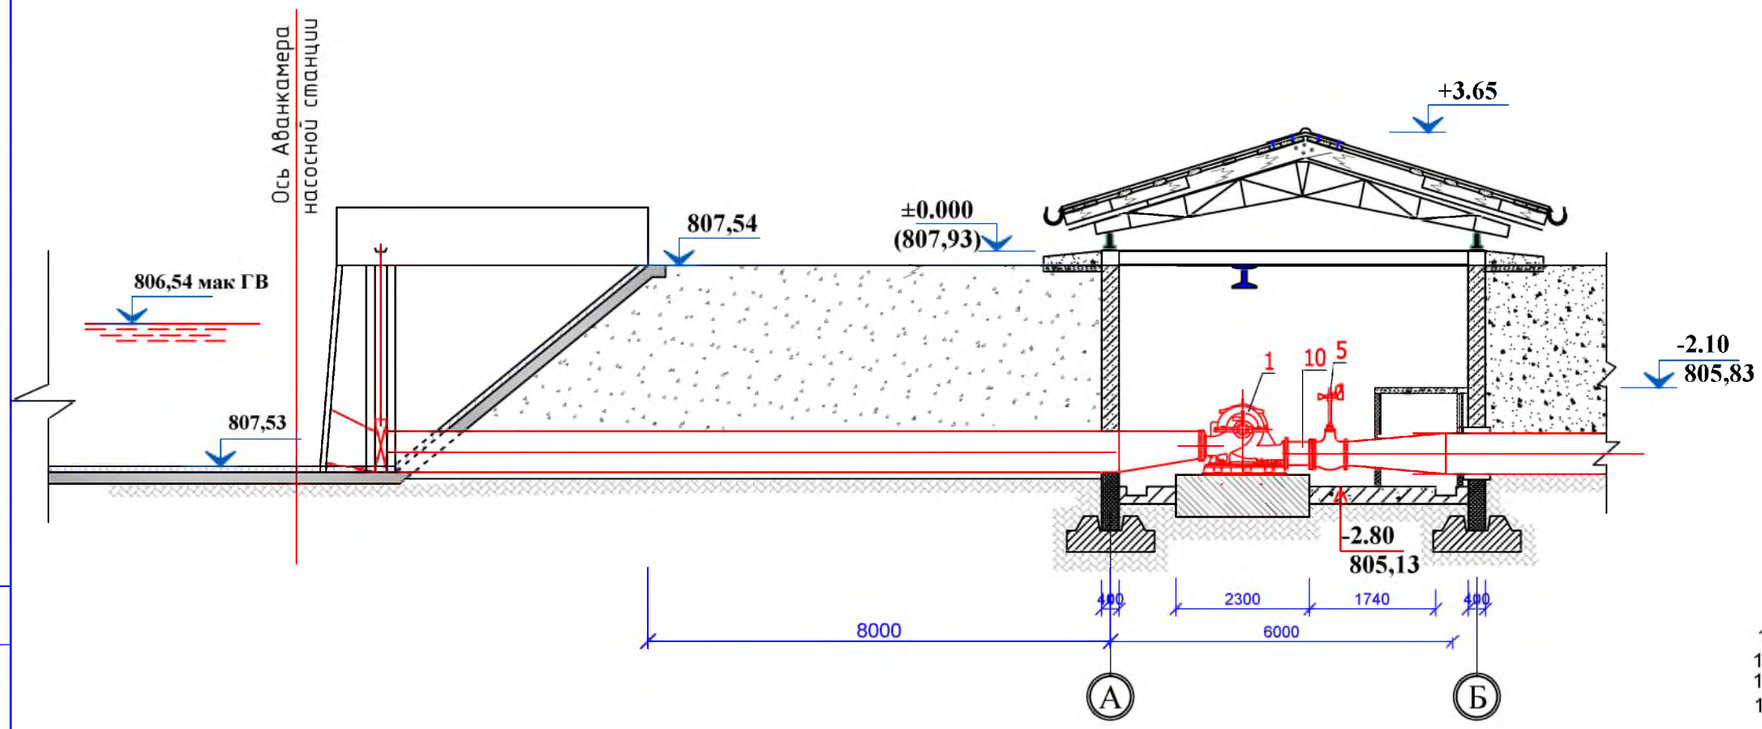

Деталировка колодец обратного клапана

М1:100

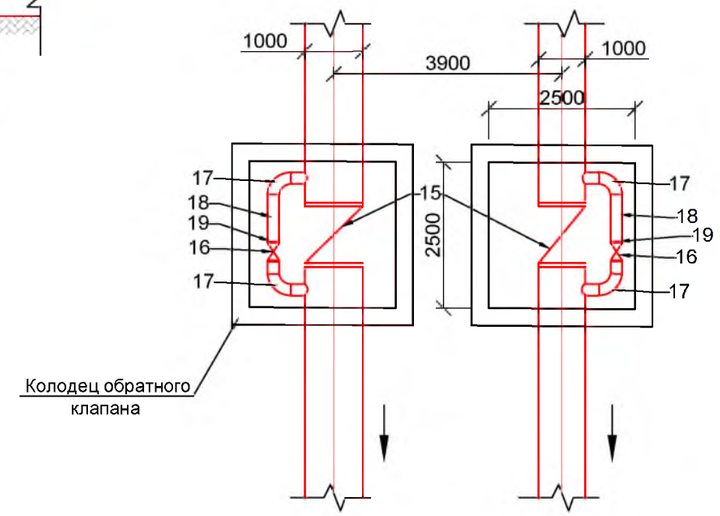

Ведомость объёмов демонтажных работ

№ П /П	Наименование	Ед. изм	Масса оборудования, кг	Примечание
1	Демонтаж насоса типа Д6300-80 (24НДс) 3-шт	кг	26298,0	Агрегат №1,2,3
2	Демонтаж электродвигатель мощность N=1000кВт 3-шт	кг	19500,0	Агрегат №1; №2 и №3
3	Демонтаж насоса типа Д4000-95 (22НДс) 1-шт	кг	4960,0	Агрегат №4
4	Демонтаж электродвигатель мощность N=1000кВт 1-шт	кг	3350,0	Агрегат №4
5	Демонтаж дренажный насос	шт	-	
6	Демонтаж сущ. переход косой Ø=800х1000мм, Ру=1,0МПа	шт	4,0	всасывающая линия
7	Демонтаж сущ. монтажная вставка Ø=600мм	шт	4,0	Напорная линия
8	Демонтаж сущ. задвижка фланцевая Ø=400мм, Ру=1,0МПа с электро-приводом	шт	4,0	Напорная линия
9	Демонтаж существующий электрические щиты	шт	4,0	
10	Демонтаж сущ. металлический напорный трубопровод Øу=1000мм, (4-нитка от здание до точка соединение)	пм	42,0	
11	Разломка и разборка существующий фундамент под оборудование в ручную с вывозом на расстоянии до 1,0км	м³	37,03	

Примечание

1. Данный лист рассматривать совместно с листом- 2,3,6 и ТХ.СО
2. Нумерация позиции см.ТХ.СО.

						ТХ
						"Баркарорсозии пойгоххои обкашии Лохур-0,Лохур-1,Лохур-2 ва Лохур-3 дар нохияи Рудаки"
Изм.	Кол.уч.	Лист	№ док.	Подп.	Дата	
Разработ.		Фрайдунпоев О.				Насосной станции Лохур-3. Технологическая часть (ТХ).
ГИП		Шомили У.				
Нач. отдел		Шомили У.				
Норм. контр.		Хайбаров С.				Разрез в осях 1 -2. М1:100. Ведомость объёмов демонтажных работ


Стадия	Лист	Листов
РП	4	12

ГУП "Проектный Институт "Точикгипроводхоз" Душанбе - 2026

Согласовано

Инв. подл | Подпись и дата | Взамен инв.

Характеристика насоса типа KQSN700-M9J-869

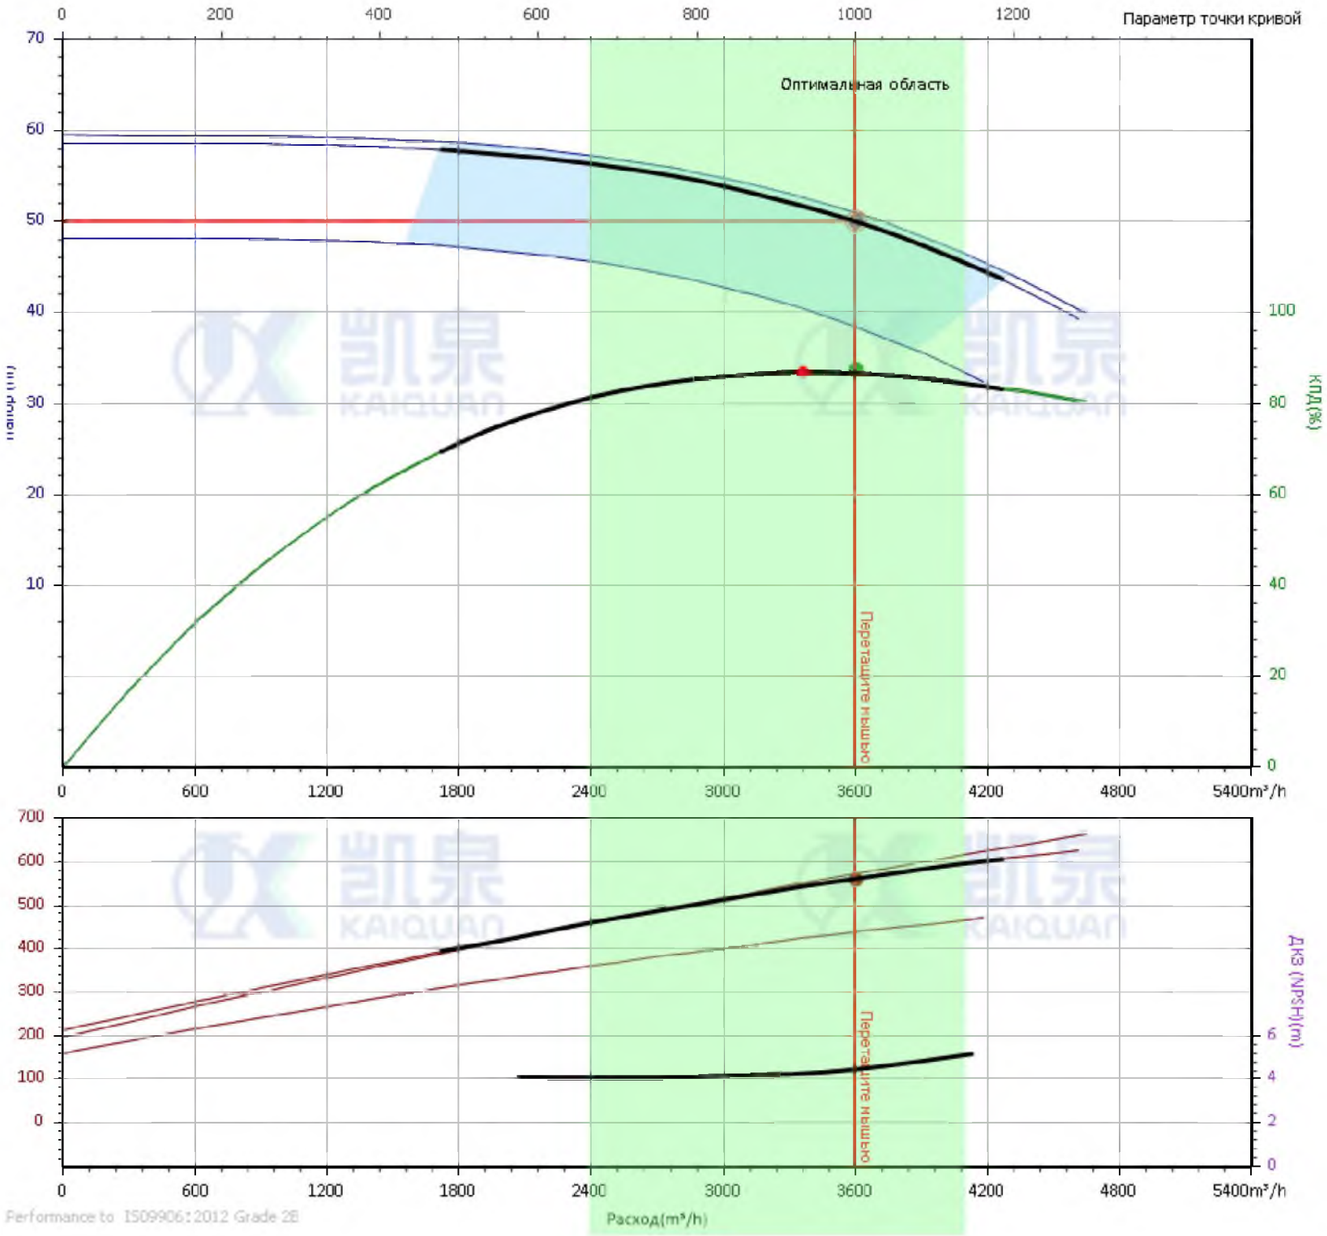

Согласовано

Взамен инв.

Подпись и дата


Инв. подл

						ТХ
						"Баркарорсозии пойгоххои обкашии Лохур-0,Лохур-1,Лохур-2 ва Лохур-3 дар нохияи Рудаки"
Изм.	Кол.уч.	Лист	№ док.	Подп.	Дата	
Разработ.		Фрайдуншоев О.				Насосной станции Лохур-3. Технологическая часть (ТХ).
ГИП		Шомили У.				
Нач. отдел		Шомили У.				
Норм. контр.		Хайбаров С.				Характеристика насоса типа KQSN700-M9J-869


Стадия	Лист	Листов
РП	5	12

ГУП "Проектный Институт "Точикгипроводхоз" Душанбе - 2026


Монтажный чертёж агрегата KQSN700-M9J-869

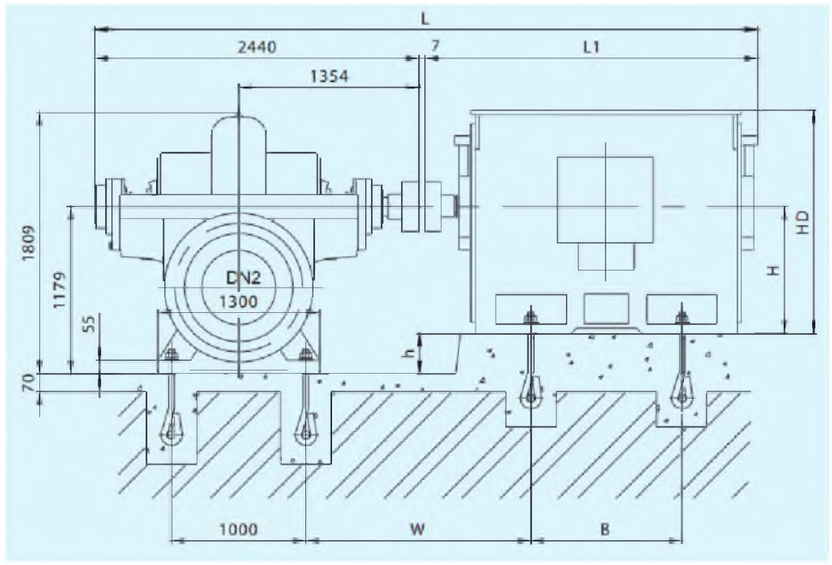

Вид с боку

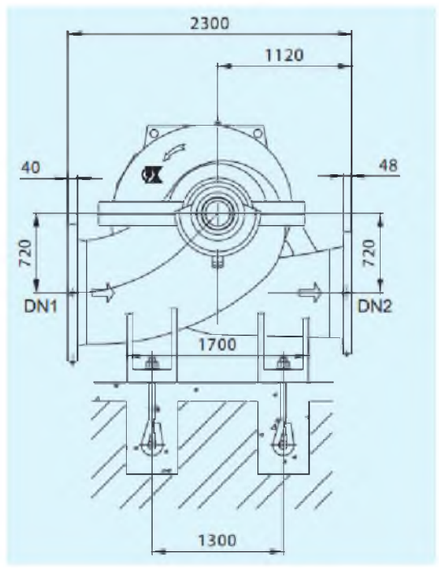


Рама агрегата типа KQSN700-M9J-869

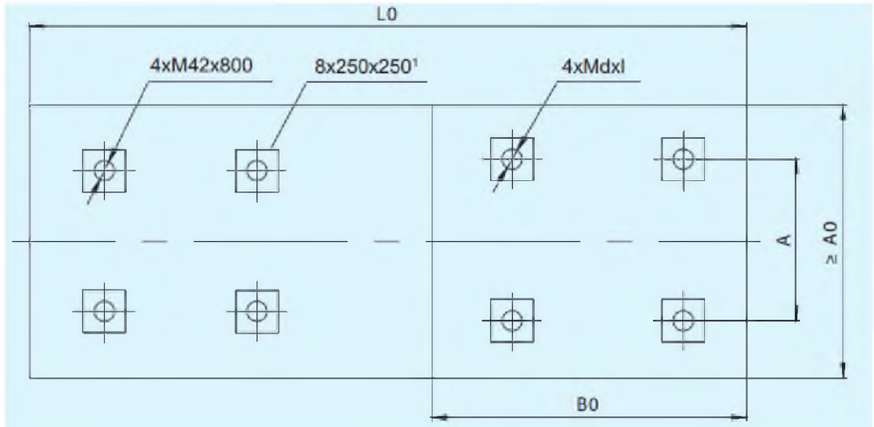


Типоразмер насоса	Диаметр рабочего колеса, мм	Подача (Q)		Напор (H), м	Частота вращения, об/мин	Мощность, кВт		Эффек-тивность (η), %	NPSHr, м	Масса, кг
		м³/ч	л/с			на валу насоса	электро-двигателя (P)			
KQSN700-M9J	869	2067	574	59	740	405,1	630	81,5	4,3	5405
		3444	957	52		557,0		87,5		
		4133	1148	46		628,9		83,0		

Типоразмер насоса	Электродвигатель				Габаритные размеры, мм												Масса, кг
	Модель	Напряж., В	Степень защиты	Мощность, кВт	L	L1	L0	A0	B0	W	A	B	h	H	HD	dxl	Эл. двиг.
KQSN700-M9J	Y500-8	6k	IP23	500–710	4989	2550	5000	1800	2500	1586	900	1250	580	500	1655	36x600	4500

Размеры фланцевого присоединения стороны всасывания DN1

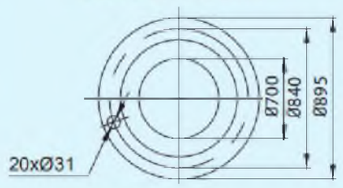

Размеры фланцевого присоединения стороны нагнетания DN2

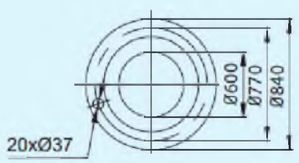


Взамен инв.

Подпись и дата

Инв. подл

						ТХ
						"Баркарорсозии пойгоххои обкашии Лохур-0,Лохур-1,Лохур-2 ва Лохур-3 дар нохияи Рудаки"
Изм.	Кол.уч.	Лист	№ док.	Подп.	Дата	
Разработ.		Фрайдунпсев О.				Насосной станции Лохур-3. Технологическая часть (ТХ).
ГИП		Шомили У.				Стадия: РП; Лист: 6; Листов: 12
Нач. отдел		Шомили У.				
Норм. контр.		Хайбаров С.				Монтажный чертеж насоса KQSN700-M9J-869
						ГУП "Проектный Институт "Точикгипроводхоз" Душанбе - 2026

Характеристика насоса типа KQSN350-M9-415

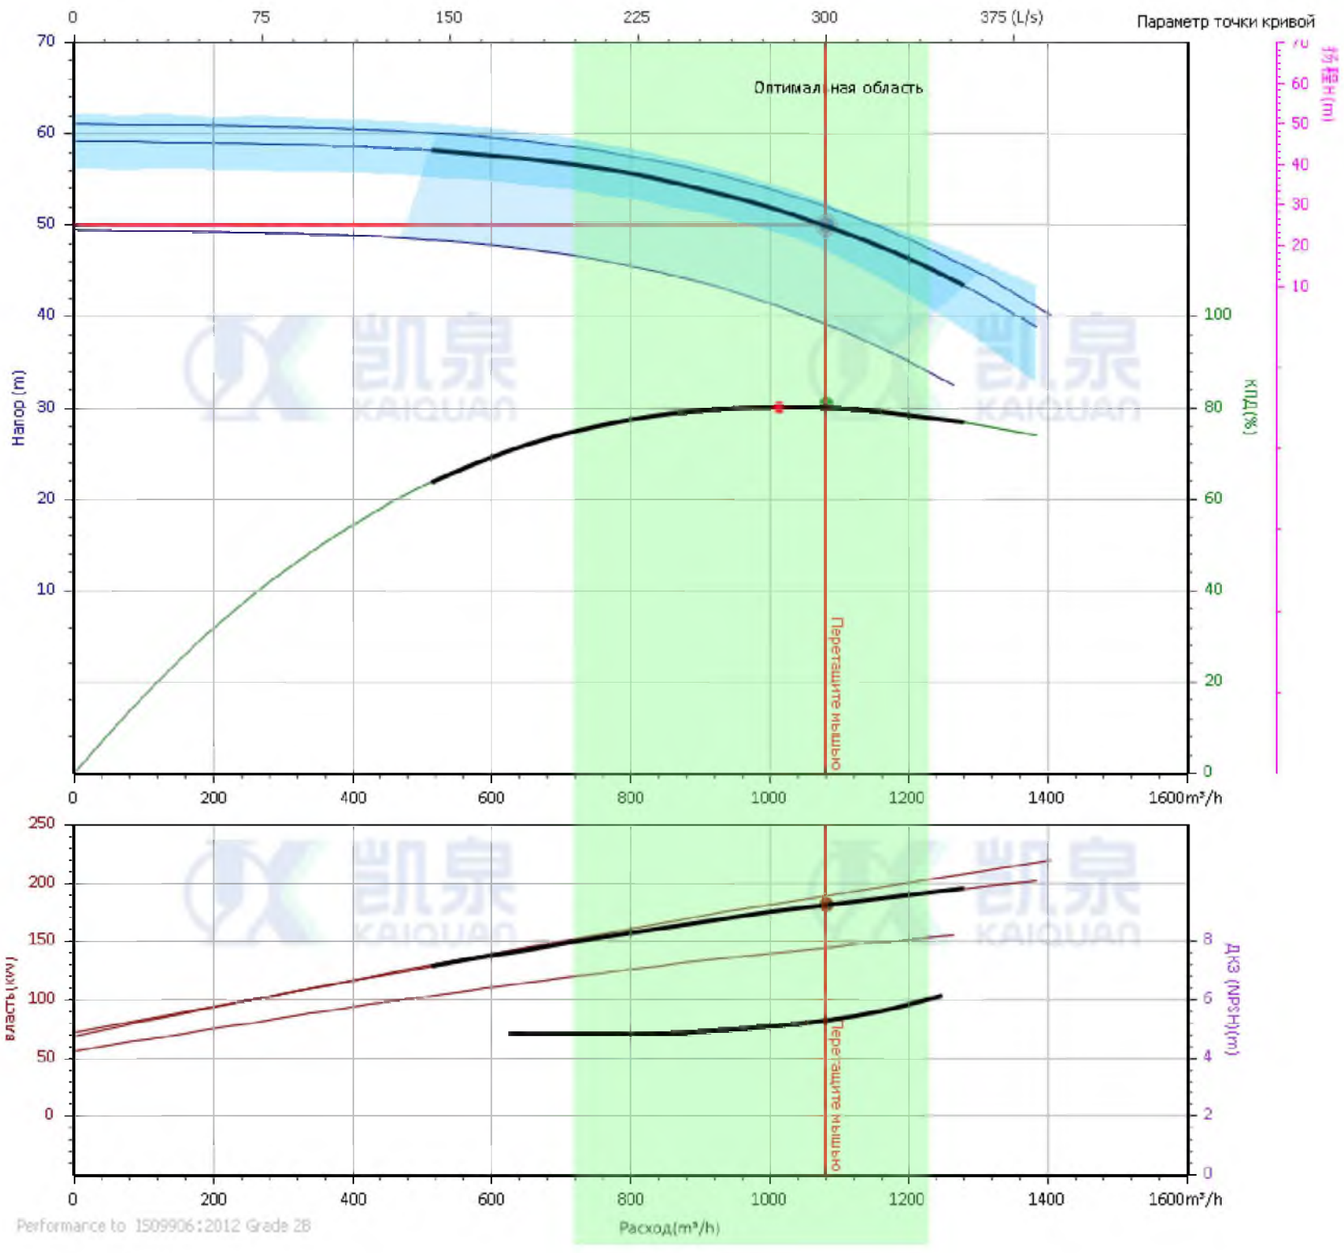

Согласовано

Взамен инв.

Подпись и дата


Инв. подл

						ТХ
						"Баркарорсозии пойгоххои обкашии Лохур-0,Лохур-1,Лохур-2 ва Лохур-3 дар нохияи Рудаки"
Изм.	Кол.уч.	Лист	№ док.	Подп.	Дата	
Разработ.		Фрайдунпосв О.				Насосной станции Лохур-3. Технологическая часть (ТХ).
ГИП		Шомили У.				
Нач. отдел		Шомили У.				
Норм. контр.		Хайбаров С.				Характеристика насоса типа KQSN350-M9-415


Стадия	Лист	Листов
РП	7	12

ГУП "Проектный Институт "Точикгипроводхоз" Душанбе - 2026

Монтажный чертёж агрегата KQSN350- M9-415

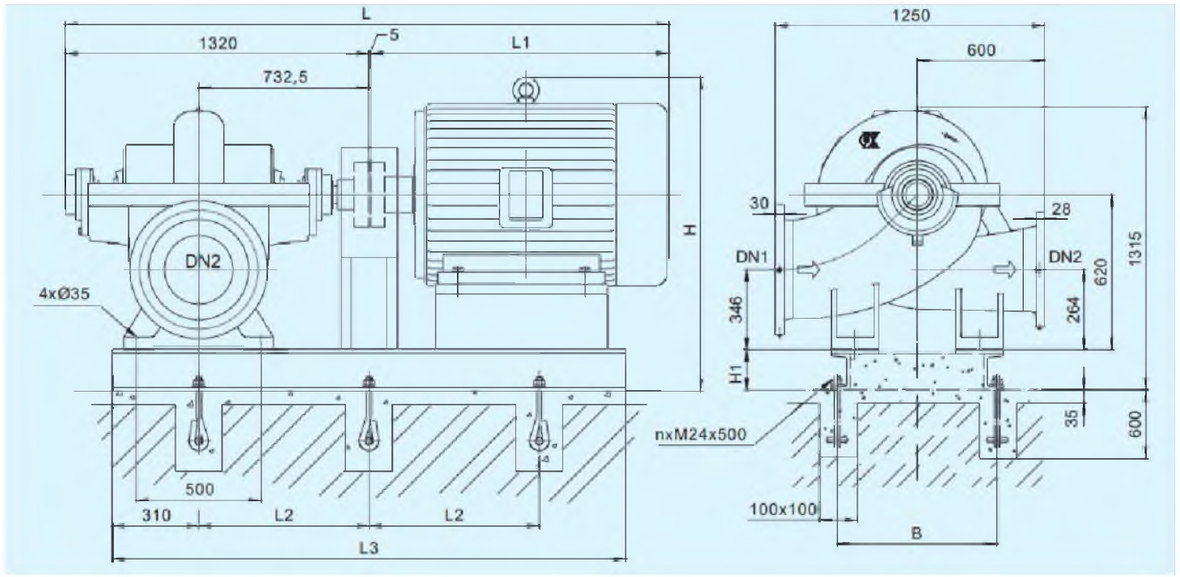

Рама агрегата типа KQSN350-M9-415

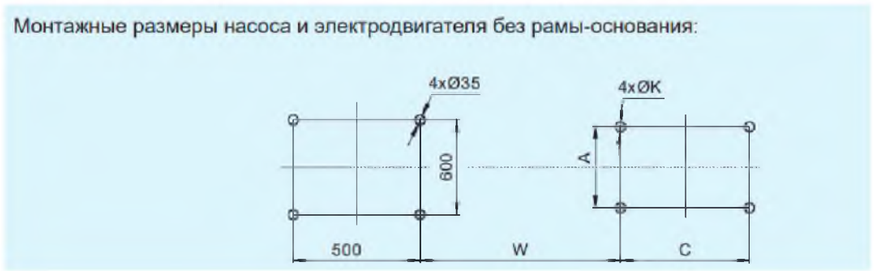

Типоразмер насоса	Диаметр рабочего колеса, мм	Подача (Q)		Напор (H), м	Частота вращения, об/мин	Мощность, кВт		Эффек-тивность (η), %	NPSHr, м	Масса, кг
		м³/ч	л/с			на валу насоса	электро-двигателя (P)			
KQSN350-M9	415	624	173,3	57	1480	147,8	220	66	5,1	1200
		1040	288,8	53		185,9		81		
		1247	346,5	46		202,9		77		

Типоразмер насоса	Электродвигатель				Габаритные размеры, мм										Масса, кг		n
	Модель	Напряж., В	Степень защиты	Мощность, кВт	L	L1	L2	L3	B	H	H1	W	A	C	K	Эл. двиг.	Рама-осн.	
KQSN350-M9	Y355-4	6000	IP23/ IP44	280–200	3215	1890	700	2750	740	1640	205	1013	630	900	28	1800	550	8

Взамен инв.

Подпись и дата


Инв. подл

						ТХ
						"Баркарорсозии пойгоххои обкашии Лохур-0,Лохур-1,Лохур-2 ва Лохур-3 дар нохияи Рудаки"
Изм.	Кол.уч.	Лист	№ док.	Подп.	Дата	
Разработ.		Фрайдуншоев О.				Насосной станции Лохур-3. Технологическая часть (ТХ).
ГИП		Шомили У.				
Нач. отдел		Шомили У.				
Норм. контр.		Хайбаров С.				Монтажный чертеж насоса KQSN350-M9-415


Стадия	Лист	Листов
РП	8	12

ГУП "Проектный Институт "Точикгипроводхоз" Душанбе - 2026

План фундамента (б/м)

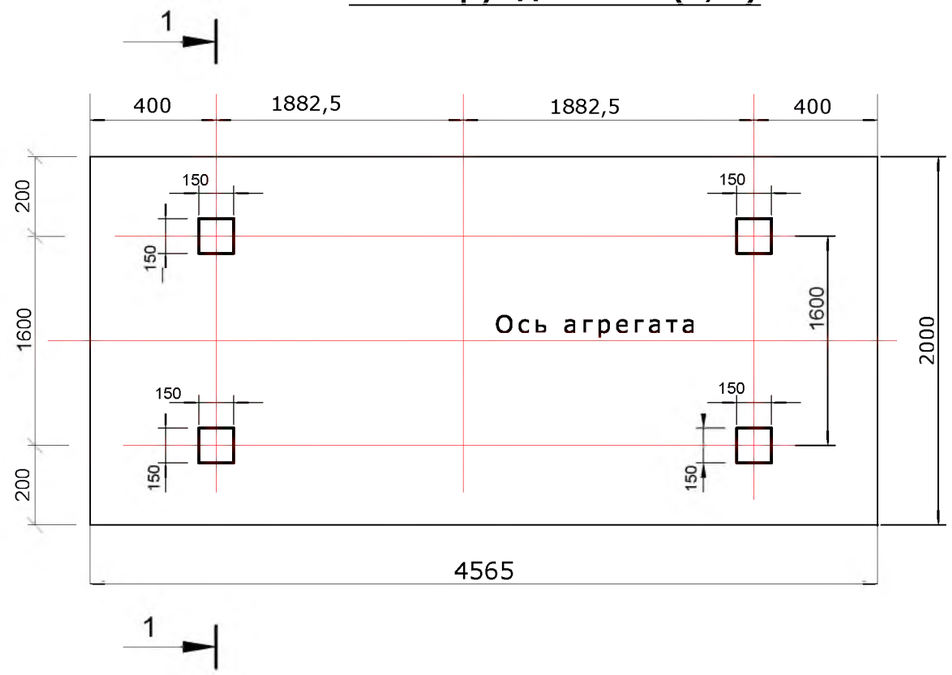

Разрез 1-1 (б/м)

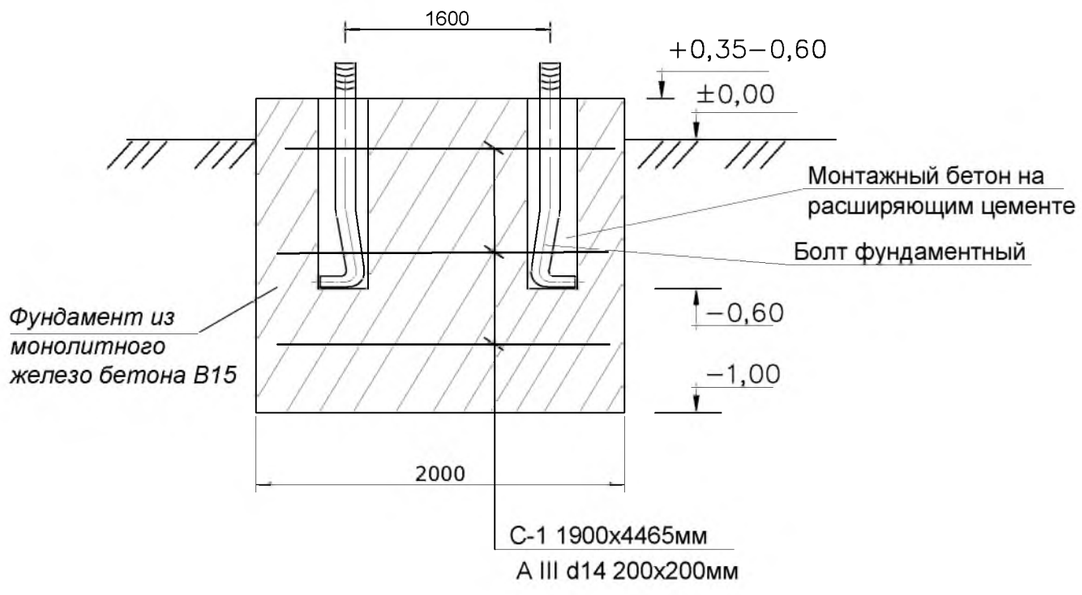

Ведомость объёмов работ дано на 1-го фундамента

N п/п	Наименование работ.	Ед изм	Кол-во	Примечание
1	Монолитный бетон В15 - F150 -W 6	м³	13,24	На 1 фундамент
2	Монтажный бетон на расширяющемся цементе	м³	0,10	На 1 фундамент
3	Болт фундаментный М30х600. ГОСТ 24379.1-80 шт.6	кг	27,30	На 1 фундамент
4	Гайка Ø30 ГОСТ 5927-80* шт. 4	кг	1,34	На 1 агрегат
5	Шайба Ø30 ГОСТ 24379.1-80 шт.4	кг	1,98	На 1 агрегат
6	Сетка С-1 раз:1090х2430 ячейки 200/200 из Арм-а AIII Ø14мм ГОСТ5781-82 3-шт (1-шт=102,85кг)	кг	308,55	На 1 агрегат
7	Шайба Ø30 ГОСТ 24379.1-80 шт.4	кг	9,50	На 1 агрегат

Всего - 4 шт

Примечание

1. Данный лист рассматривать совместно с листом ТХ-3,4,5
2. В сметы учитывать демонтаж, разломка и разборки существующие фундаментные агрегаты раз:2,30х4,9х1,0м -11,27м3х4шт=45,0м3
3. Местоположение отверстий под анкерные болты уточняются по полученному оборудованию
4. Анкерные болты необходимо прикрепить с арматурной сетки фундамента

Взамен инв.

Подпись и дата


Инв. подл

						ТХ
						"Баркарорсозии пойгоххои обкашии Лохур-0,Лохур-1,Лохур-2 ва Лохур-3 дар нохияи Рудаки"
Изм.	Кол.уч.	Лист	№ док.	Подп.	Дата	
Разработ.		Фрайдунпоев О.				Насосной станции Лохур-3. Технологическая часть (ТХ).
ГИП		Шомили У.				
Нач. отдел		Шомили У.				
Норм. контр.		Хайбаров С.				Фундамент под агрегат. Ведомость объёмов работ


Стадия	Лист	Листов
РП	9	12

ГУП "Проектный Институт "Точикгипроводхоз" Душанбе - 2026

План насосной станции
М1:100

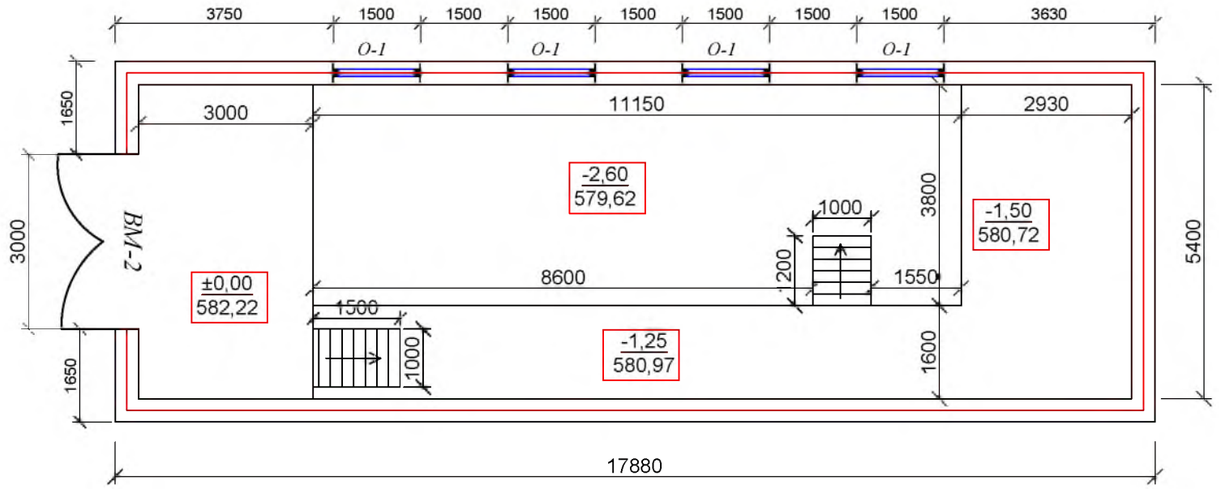

План дренажная система
М1:100

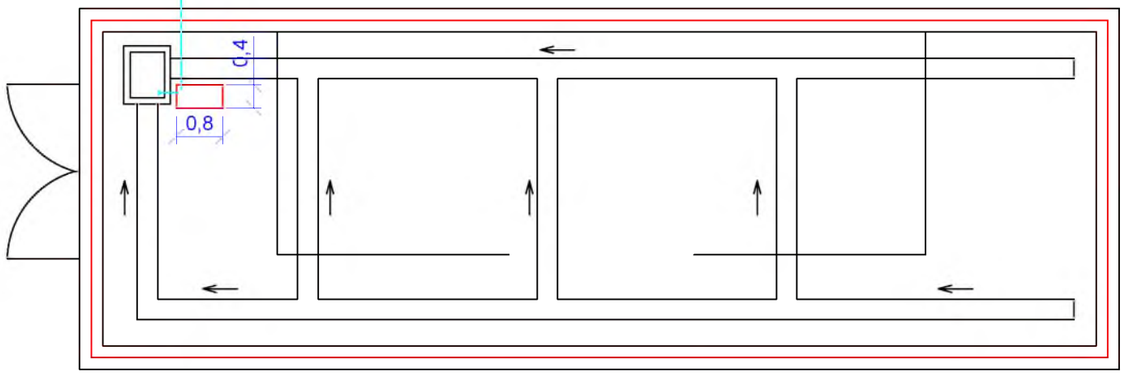

Примечание


1. Данный лист рассматривать совместно с листом- 2,3,6 и ТХ.СО

						ТХ	
						"Баркарорсозии пойгоххои обкашии Лохур-0,Лохур-1,Лохур-2 ва Лохур-3 дар нохияи Рудаки"	
Изм.	Кол.уч.	Лист	№ док.	Подп.	Дата		
						Насосной станции Лохур-3. Технологическая часть (ТХ).	Стадия: РП; Лист: 10; Листов: 12
Разработ.		Фрайдунпоев О.					
ГИП		Шомили У.					
Нач. отдел		Шомили У.				План насосной станции. План дренажная система. М1:100	**ГУП "Проектный Институт "Точикгипроводхоз" Душанбе - 2026**
Норм. контр.		Хайбаров С.					


Согласовано

Инв. подл | Подпись и дата | Взамен инв.

1-1

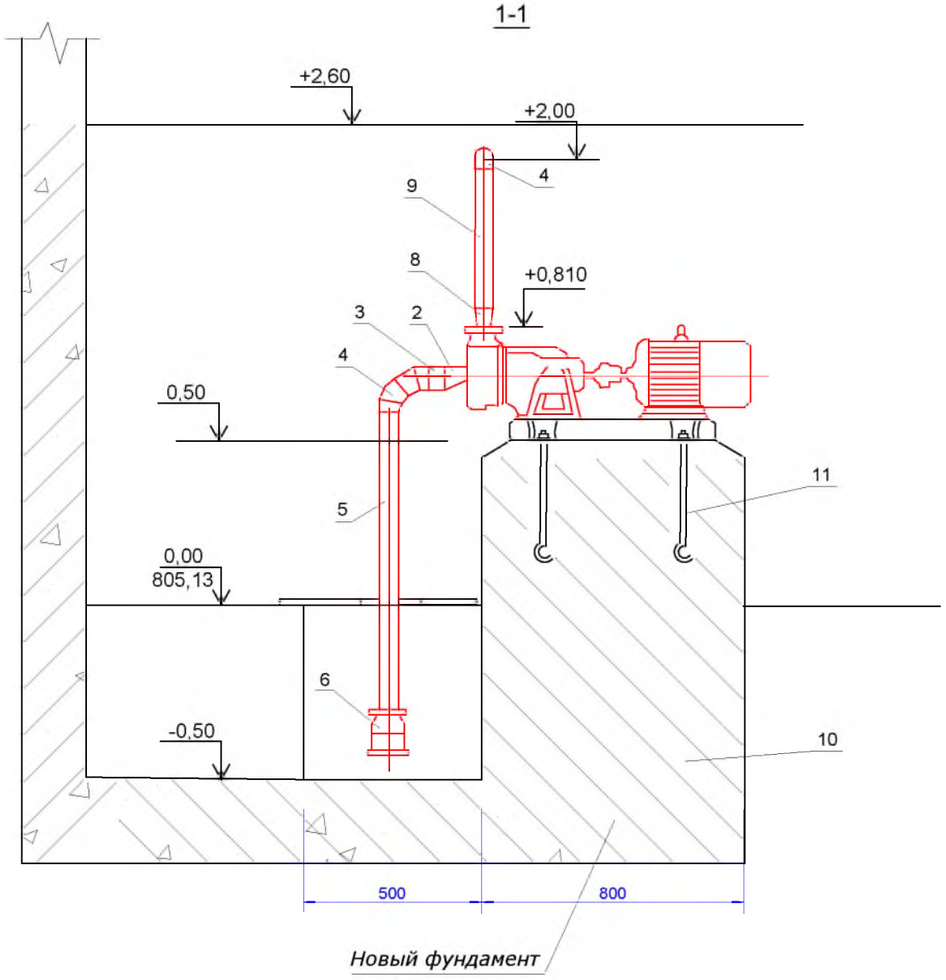

План

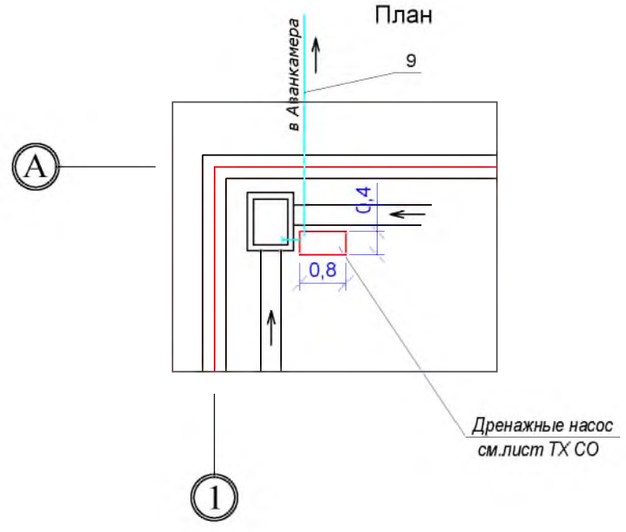

Спецификация

№№	Обозначение	Наименование	Кол-во	Масса ед.кг	Примечание
		Стандартные изделия			
1	ГОСТ 12817-80	Фланец 40-0,25МПа	1	1,04	
2		Муфты переходные 40х50мм	1	0,128	
3	ГОСТ 8957-75	Труба 50х3,0 **ГОСТ3262-75**	1		L=200,0мм
4	ГОСТ 12820-80	Отвод 90° 57х3,0	2	0,40	
5	ГОСТ 8946-75	Труба 50х3,0 **ГОСТ3262-75**	1		L=800,0мм
6		Приёмный клапан d=50мм	1		
7		Фланец 32-0,25МПа	1	1,04	
8		Муфты переходные 32х50мм	1		
9		Труба 50х3,0 **ГОСТ3262-75**	1		L=6200,0мм
10		Монолитный бетон В15	1		0,32м³
11		Анкерный болты М14	4		

Примечание:

1. Отметке ±0,00 соответствует отметка пола камеры 579,62

2. Дренажной насос с эл/двигателем включено в СО (поз 4)

						ТХ
						"Баркарорсозии пойгоххои обкашии Лохур-0,Лохур-1,Лохур-2 ва Лохур-3 дар нохияи Рудаки"
Изм.	Кол.уч.	Лист	№ док.	Подп.	Дата	
Разработ.		Фрайдунпосев О.				Насосной станции Лохур-3. Технологическая часть (ТХ).
ГИП		Шомили У.				
Нач. отдел		Шомили У.				
Норм. контр.		Хайбаров С.				Установочный чертёж дренажного-насоса. Спецификация

Стадия	Лист	Листов
РП	11	12

ГУП "Проектный Институт "Точикгипроводхоз" Душанбе - 2026

Согласовано


Взамен инв.

Подпись и дата

Инв. подл

План водопроводного колодца (2500x2500 mm)

Разрез 1 - 1

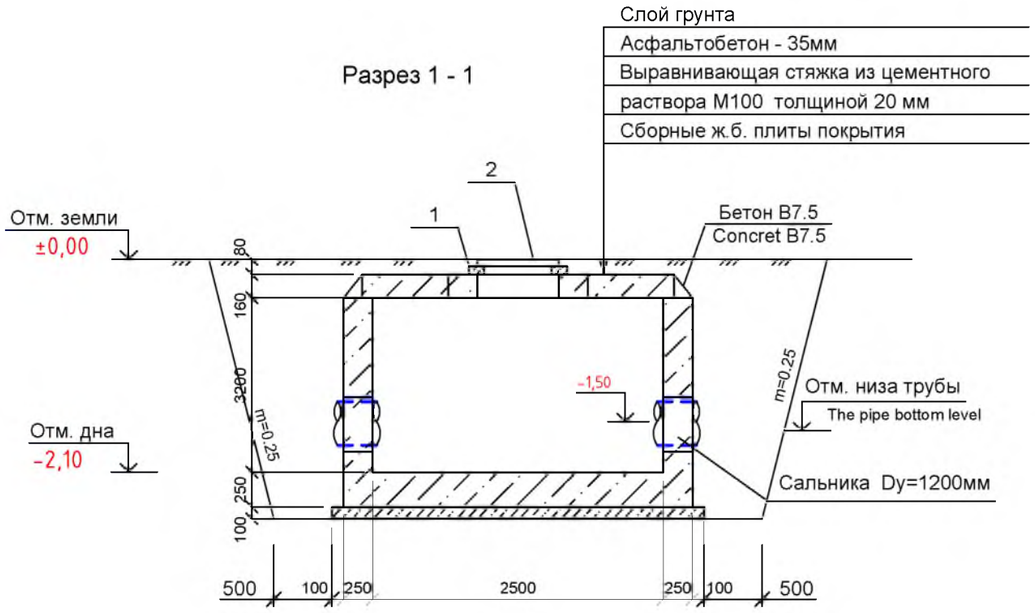

План котлована водопроводного колодца (2500x2500 mm)



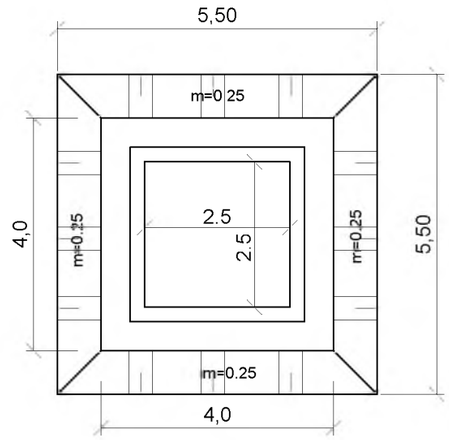


Схема расположения плит покрытия водопроводного колодца

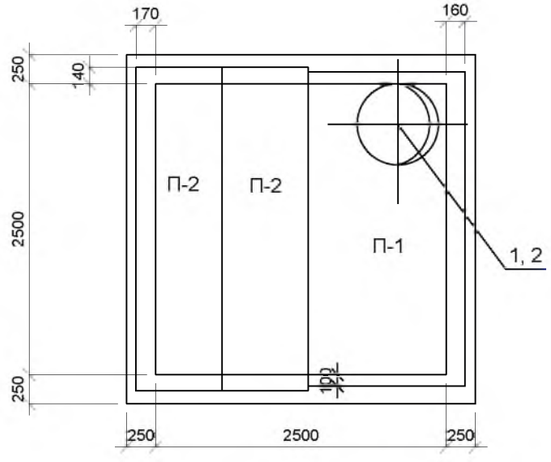

План водопроводного колодца

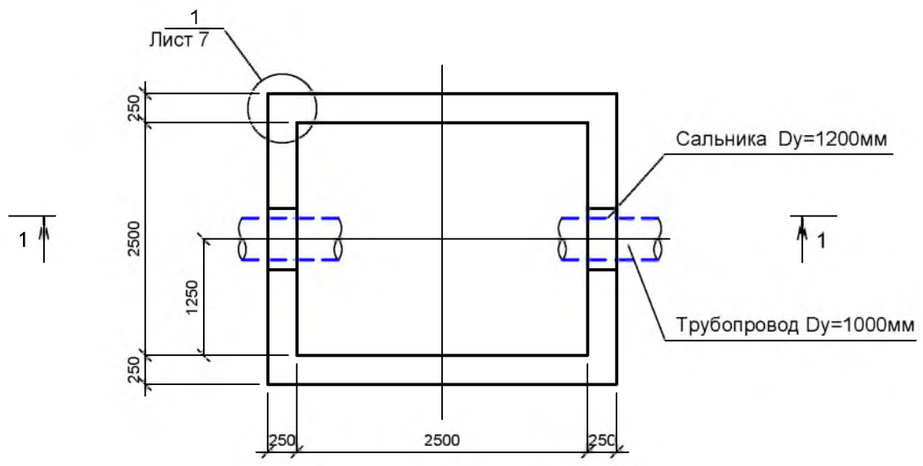

Спецификация плит покрытия

Марка	Обозначение	Наименование	Кол-во	Масса ед. кг.	Примеч.
	Сборные ж.б. конструкции Precast concrete structures				
П1	901-09-11.84, ал. V	Cover plate Плита покрытия П24-5Б	1	1450	
П2	3.006.1-2.87, вып. 2	Cover plate Плита покрытия П24д-5	2	930	
1	3.900-3, вып. 7	Support ring Кольцо опорное КЦО-1	1	50	
		Metal structures Металлические конструкции			
2	GOST 3634-99	Люк "Т" d=700 мм	1	69	

Ведомость объемов работ

№ ПП	Наименование	Ед. изм	Кол-во	Примечание
1	Разработка грунта II-кат	м³	67,0	5% Вручную
2	Обратная засыпка	м³	40,0	
3	Гидроизоляция битумом 2-раза по наружных поверхностям соприкасающийся с грунтом	м²	35,2	

*** Ведомость объемов работ и спецификация дано на 1-шт всего-4шт

*** Данный лист рассматривается совместно с листами 3 и 7.


						ТХ
						"Баркарорсозии пойгоххои обкашии Лохур-0,Лохур-1,Лохур-2 ва Лохур-3 дар нохияи Рудаки"
Изм.	Кол.уч.	Лист	№ док.	Поди.	Дата	
Разработ.		Фрайдунпоев О.				Насосной станции Лохур-2. Технологическая часть (ТХ).
ГИП		Шомили У.				
Нач. отдел		Шомили У.				Конструкция камера обратного клапана Ведомость объёмов работ. Спецификация.
Норм. контр.		Хайбаров С.				


Стадия	Лист	Листов
РП	10	12

ГУП "Проектный Институт "Точикгипроводхоз" Душанбе - 2026

Взамен инв. | Подпись и дата | Инв. подл


Water supply manhole (2500x2500 mm)

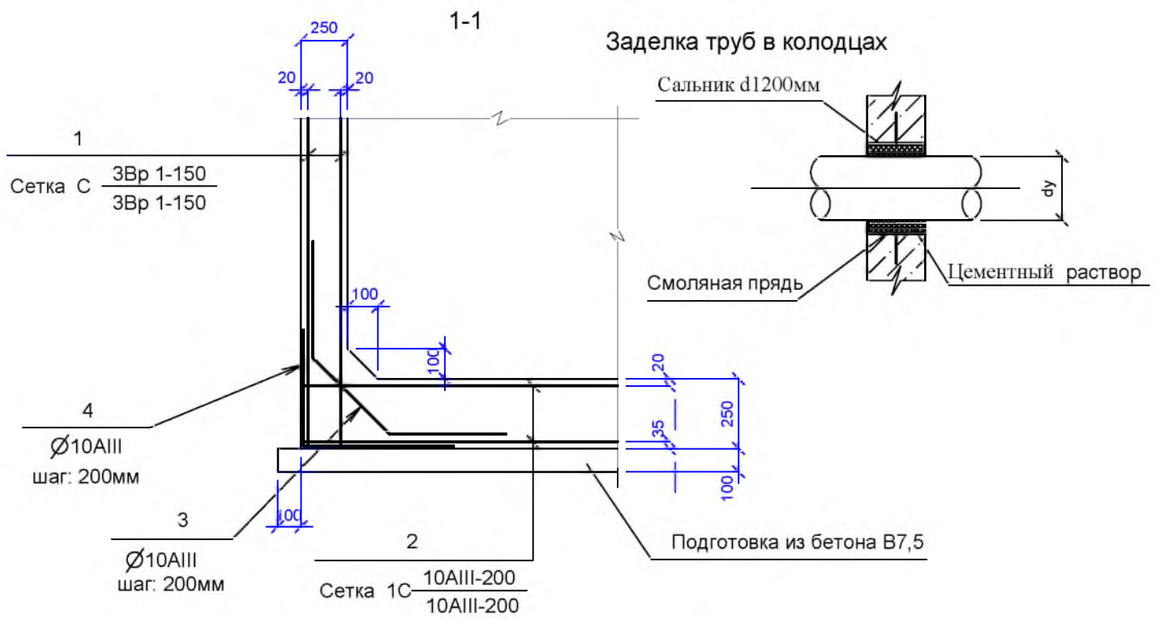

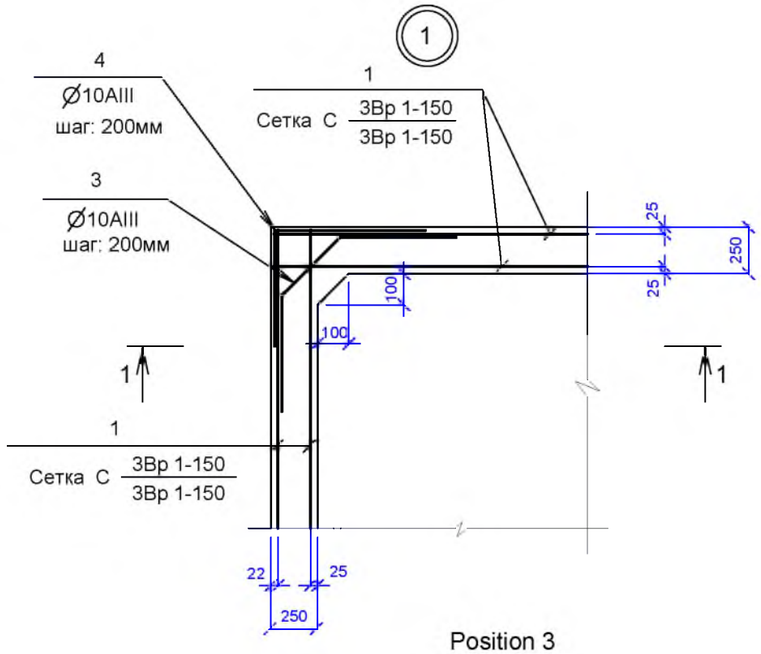


Position 3

Ø 10AIII

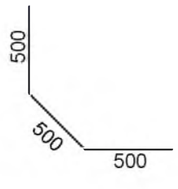

Position 4

Ø 10AIII

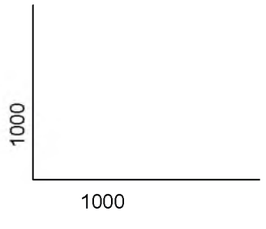

Спецификация на колодец Specification for the manhole

Поз. Position	Обозначение Designation	Наименование Name	Кол-во Number	Примеч. Remarks
		Сборочные единицы		
1	GOST 8478-81	Арм. сетка С 3Вр 1-150 / 3Вр 1-150	74,0 m2	60,0кг
2	GOST 23279-85	Арм. сетка1С 10AIII-200 / 10AIII-200	18,0 m2	111,06кг
3	GOST 5781-82*	Ø10AIII L=1500	84 pcs.	0,93 kg
4		Ø10AIII L=2000	96 pcs.	1,23 kg
5		Установка сальника d=1200мм	2,0	
		Материалы Materials		
		Concrete Бетон B15, W4, F100 (днище bottom)	2,25	m^3
		Concrete Бетон B15, W4, F100 (стенки wall)	8,80	m^3
		Concrete (preparation) Бетон B7,5, W4, F100 (подготовка)	1,02	m^3

Расход арматуры на колодец

N,N п/п	Наименование	Количество на колодец	Примеч.
1	Арматурная сталь Ø10AIII	307,8 kg	
2	,, Ø3BpI	60,0 kg	
	Итого Total	340,1 kg	

Примечание

1. Стены и днище колодца выполнить из бетона В15
2. Арматуру сеток в местах установки сальников вырезать и приварить к сальникам.
3. Узел 1 см.лист №6

ТК

Изм.	Кол.уч	Лист	№ док	Подп	Дата	Насосной станции Лохур-2. Технологическая часть (ТХ). Конструкция колодец обратного клапана	Лист 11

Согласовано

Взамен инв.

Подпись и дата

Инв. подл

Спецификация оборудования и материалов

№ № П/П	Наименование и техническая характеристика оборудования и материалов Завод-изготовитель (для импортного оборудования-страна, фирма)	Тип, марка оборудования, обозначение документа и опросного листа	Наимено - вание ед.изм.	Код	Код завода изготовителя	Цена единицы тыс.руб.	Кол-во	Масса единицы оборудования, кг	Примечание
	Оборудование								
1	Насос типа Д-горизонталные одно ступенчатые с раб.колесо Dк=862,8мм, корпус из высокопровочный чугун (ВЧ. 40-60) Q=3600м³/ч; H=50м, n=750.об/мин, (рабочий колесо насоса из нержавейший сталь) с электродвигателями мощностью N=640 кВт. напряжение U=6000В; n=750об/мин с учетом заводской рамы и транспортировкой до объекта и подготовка машин к испытанию сдачей под наладку и пуску для соединение к электросети **(агрегаты №1; №2 и №3 Левого вращение китайского производства)**	KQSN700-M9J-869 Y500-8	шт				3,0	9905,0	29715,0кг
	Насос типа Д-горизонталные одно ступенчатые с раб.колесо Dк=408,5мм, корпус из высокопровочный чугун (ВЧ. 40-60) Q=1080м³/ч; H=50м, n=1500.об/мин, (рабочий колесо насоса из нержавейший сталь) с электродвигателями мощностью N=250 кВт. напряжение U=6000В; n=1500об/мин с учетом заводской рамы и транспортировкой до объекта и подготовка машин к испытанию сдачей под наладку и пуску для соединение к электросети **(агрегаты №4 Левого вращение китайского производства)**	KQSN350-M9-415 Y355-4	шт				1,0	1750,0	1750,0кг
2	Дренажный центробежный насос типа К 20/18 Q=20м³/час, H=18м. с раб.колесо Dк=129мм, n=2900об/мин мощность эл. двигателя типа 4А80В2 N=2,2 кВт. напряжение U=220/380В; n=3000об/мин	К 20/18 (2К-9) 4А80В2	шт				1,0	68,0	68,0кг
	Всасывающая линия								
3	Переход концентрический Dy=800x1000x7мм, L=470мм	МН2883-62	шт				4,0	109,0	436,0кг
	Напорная линия								
4	Монтажная вставка Dy=600мм, L=274мм на напорной линии	AVK	шт				4,0	95,0	380,0кг
5	Задвижка стальная фланцевая Ø=600мм, L=800мм Ру=1,0МПа,с электроприводом	**30ч915бр**	шт				4,0	1320,0	5280.0кг
6	Переход концентрический Dy=600x1000x7мм, L=917мм	МН2883-62	шт				4,0	230,0	920.0кг
7	Металлическая труба Øн=1020x7мм, L=700м	ГОСТ 10704-91	шт				1,0	174,9	122,0кг
8	Отвод 45° Øн=1000x6мм, L=1240мм	МН2878-62	шт				1,0	187,0	-
9	Металлическая труба Øн=1020x7мм, L=10000мм	ГОСТ 10704-91	шт				1,0	174,9	1749,0кг
10	Металлическая труба Øн=1020x7мм, L=9500мм	ГОСТ 10704-91	шт				1,0	174,9	1661,0кг
11	Металлическая труба Øн=1020x7мм, L=9500мм	ГОСТ 10704-91	шт				1,0	174,9	1661,0кг
12	Металлическая труба Øн=1020x7мм, L=700м	ГОСТ 10704-91	шт				1,0	174,9	122,0кг
13	Отвод 45° Øн=1000x6мм, L=1240мм	МН2878-62	шт				1,0	187,0	-
14	Металлическая труба Øн=1020x7мм, L=10000мм	ГОСТ 10704-91	шт				1,0	174,9	1749,0кг
	Колодец обратного клапан								
15	Приобретение и монтаж обратный клапан фланцевый Dy=1000мм, Ру=1,6мПа	КО1000.16-4311	шт				4,0	1300,0	5200,0кг
16	Приобретение и монтаж задвижки Dy=100мм,Ру=1,0Мпа на сбросной линии	30ч6бр	шт				4,0	39,5	158,0кг
17	Отвод 90° Øу=100x6мм, L=300мм	ГОСТ 17375-83*	шт				8,0	3,80	30,4кг
18	Металлическая труба Øн=114x7мм, L=1600мм	ГОСТ 10704-91	шт				4,0	29,552	118,21кг
19	Фланец стальной приварной Dy=100мм,Ру=1,6мПа	ГОСТ 12820-80	шт				8,0	4,73	37,84кг
	Болты и Гаек М16 L=75мм	ГОСТ 12820-80	шт				64,0	0,149 /0,033	**9,536 / 2,112кг**

ПРИМЕЧАНИЕ:

1. Учесть электроды 3% от всего веса металлоконструкции.
2. Учесть масленную краску для металлоконструкции.
3. Данный лист рассматривать совместно с лист-2,3,4,5,5а,6 и 7

Изм.	Кол.уч.	Лист	№ док.	Подп.	Дата
Разработ.		Фрайдунпсев О.			
ГИП		Шомили У.			
Нач. отдел		Шомили У.			
Норм. контр.		Хайбаров С.			

ТХ

"Баркарорсозии пойгоххои обкашии Лохур-0,Лохур-1,Лохур-2 ва Лохур-3 дар нохияи Рудаки"

Насосной станции Лохур-3. Технологическая часть (ТХ).

Стадия	Лист	Листов
РП	1	1

Спецификация оборудования и материалов

ГУП "Проектный Институт "Точикгипроводхоз" Душанбе - 2026

Согласовано


Взамен инв

Подпись и дата

Инв. подл

Формат А3

Характеристика насоса типа Д KQSN700-M9J n=750 об/мин

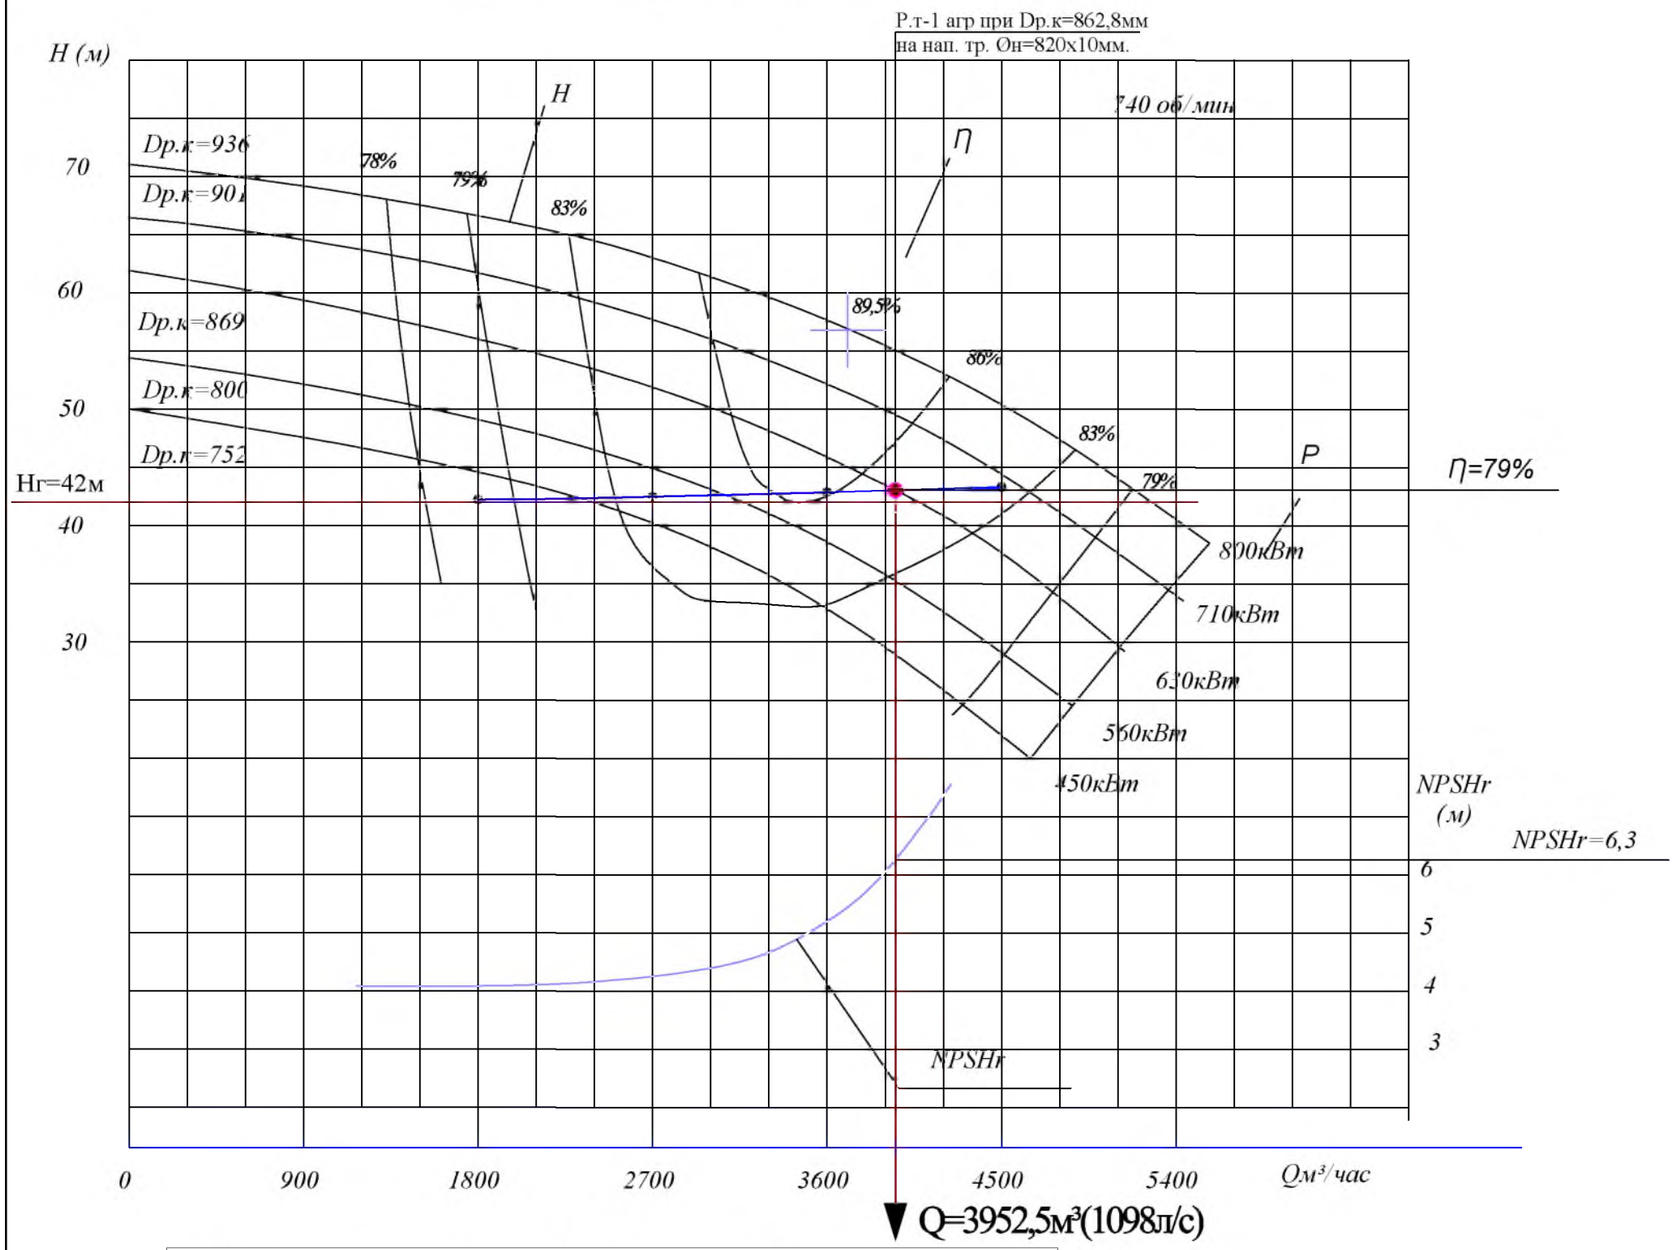


Определение манометрический напор и расчетный расход насоса типа Д KQSN700-M9J

Q л/сек	Q м³/час	Нгео. м	L, км	Dтр.в,мм	i на 1км, в м	∑i,в м	Н,ман в м при 1-го агрегат	Примечание
		При работе 1-го агрегата						
500,0	1800,0	42,0	0,124	820х10	1,46	0,22	42,22	
750,0	2700	42,0	0,124	820х10	3,18	0,47	42,47	
1000,0	3600,0	42,0	0,124	820х10	5,66	0,84	42,84	
1250,0	4500,0	42,0	0,124	820х10	8,84	1,32	43,32	

Изм.	Кол.уч.	Лист	№ док.	Подп.	Дата	ТХ		
						"Баркарорсозии пойгоххои обкашии Лохур-0,Лохур-1,Лохур-2 ва Лохур-3 дар нохияи Рудаки"		
Разработ.		Фрайдуншоев О.				Насосной станции Лохур-3. Технологическая часть (ТХ).	Стадия	Лист	Листов
ГИП		Шомили У.					РП	1	1
Нач. отдел		Шомили У.				Рабочая характеристика насоса типа KQSN700-M9J	ГУП "Проектный Институт "Точикгипроводхоз" Душанбе - 2026		
Норм. контр.		Хайбаров С.							

Характеристика насоса типа Д KQSN350-M9 n=1500 об/мин

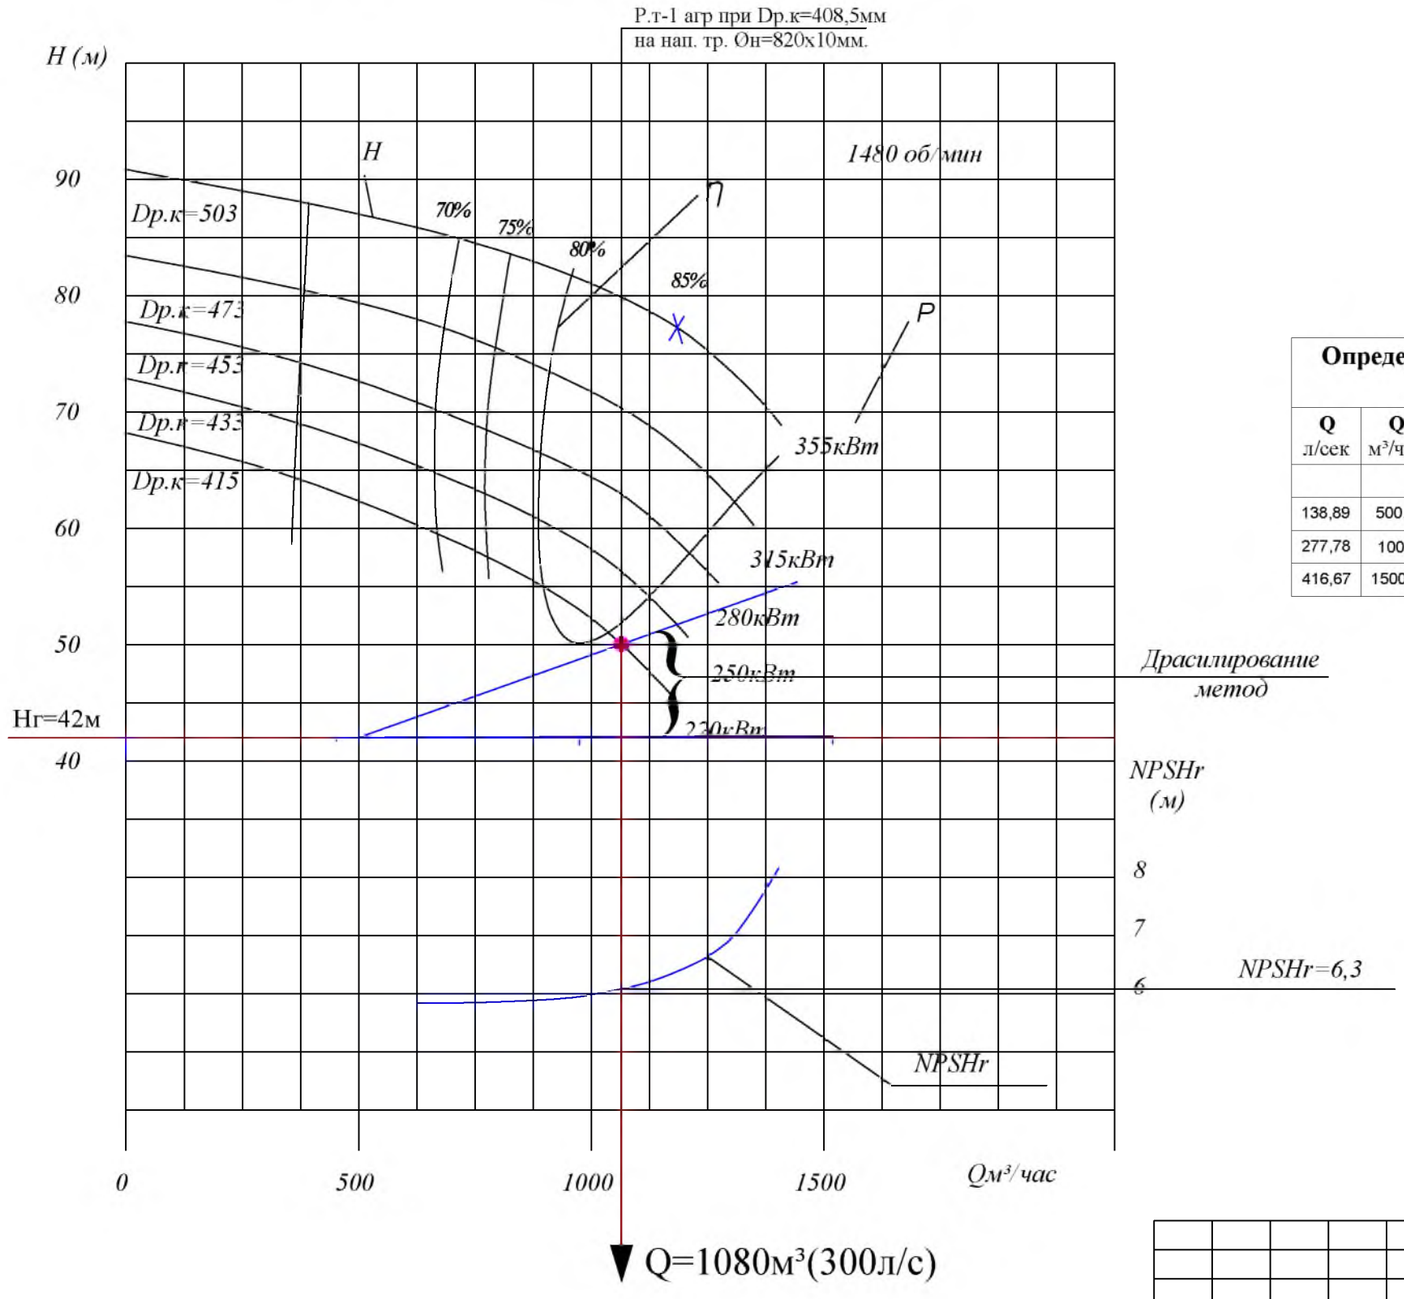

Определение манометрический напор и расчетный расход насоса типа Д KQSN350-M9

Q л/сек	Q м³/час	Нгео. м	L, км	Dтр.мм	i на 1км, в м	∑i,в м	Нман в м при 1-го агрегат	Примечание
		При работе 1-го агрегата						
138,89	500,0	42,0	0,124	820х10	0,143	0,021	42,021	
277,78	1000	42,0	0,124	820х10	0,49	0,073	42,073	
416,67	1500,0	42,0	0,124	820х10	1,04	0,15	42,15	

						ТХ
						"Баркарорсозии пойгоххои обкашии Лохур-0,Лохур-1,Лохур-2 ва Лохур-3 дар нохияи Рудаки"
Изм.	Кол.уч.	Лист	№ док.	Подп.	Дата	
Разработ.		Фрайдуншоев О.				Насосной станции Лохур-3. Технологическая часть (ТХ).
ГИП		Шомили У.				
Нач. отдел		Шомили У.				
Норм. контр.		Хайбаров С.				Рабочая характеристика насоса типа KQSN700-M9J

Стадия	Лист	Листов
РП	1	1

ГУП "Проектный Институт "Точикгипроводхоз" Душанбе - 2026